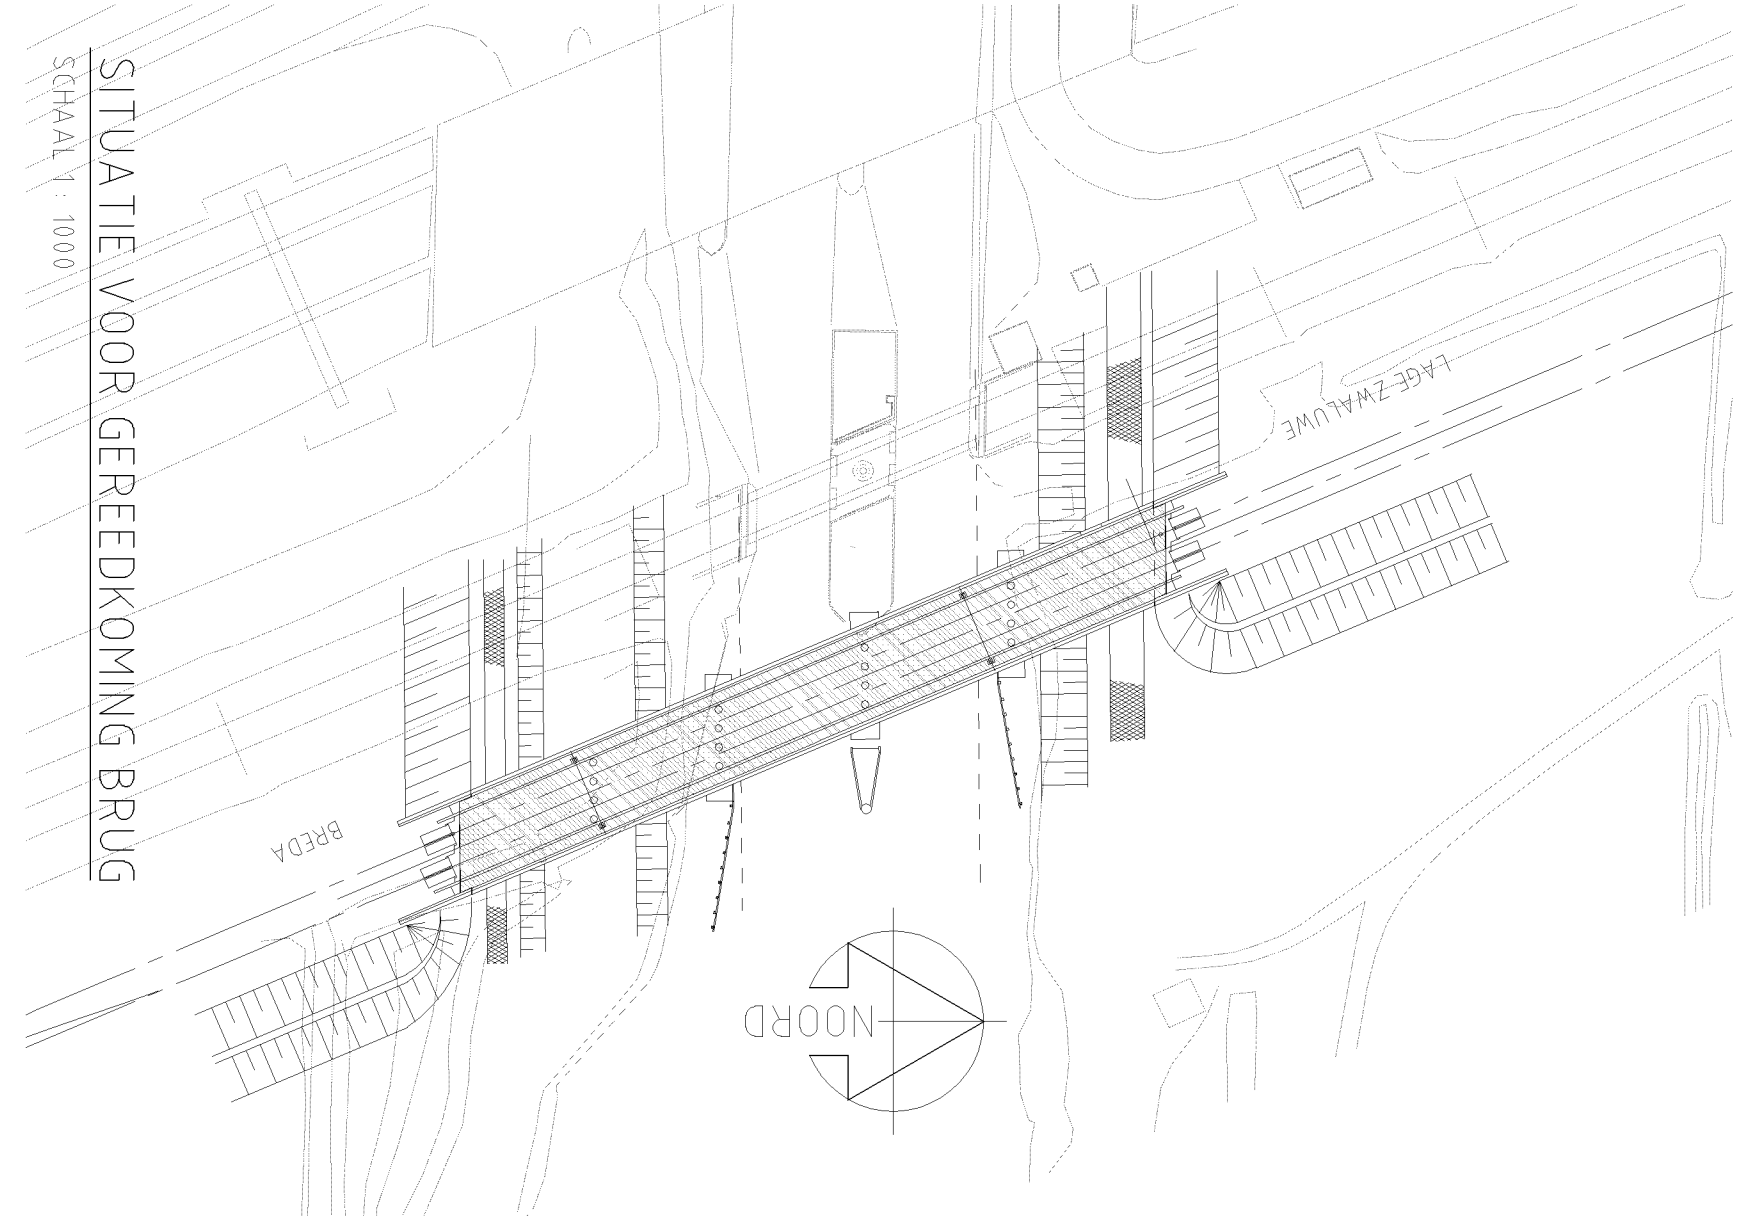


- MATERIALEN	
- MASTIK BETON	B36
- PREFABRIK BETHOALEN	B32
- WAPENING	FEB SLD
- STALEN PALEN	x65 MET. BETWOUWING B35

		146E INALING - PERSONEERIX SPORRBEIJE OER DE MOER DIVIZIJE IN DOORSCHERIN	
Per	A	1013	8.556
De	01	8.556	01
ProRail			