


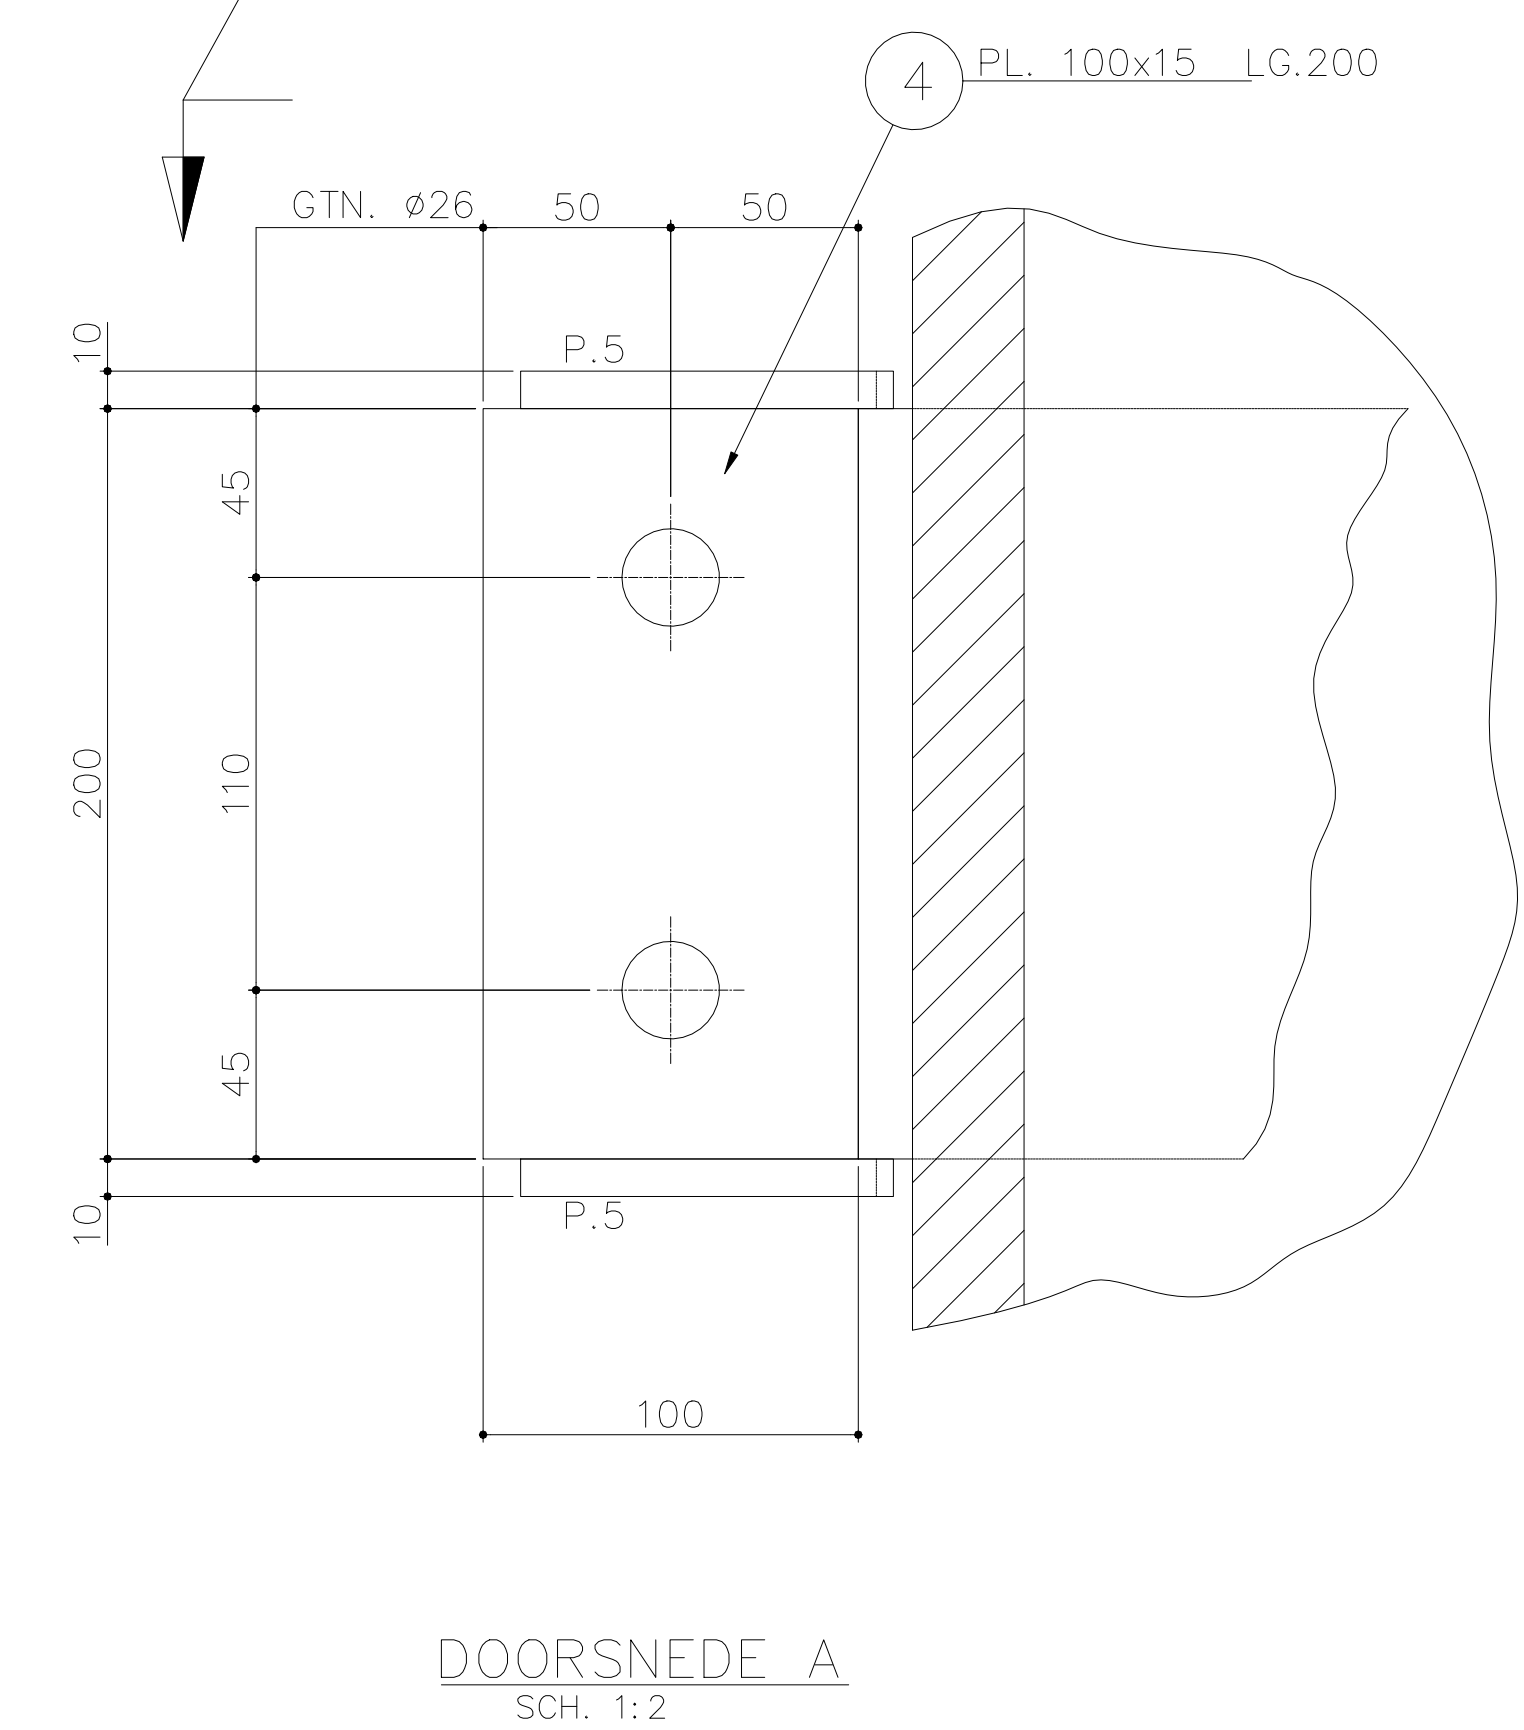
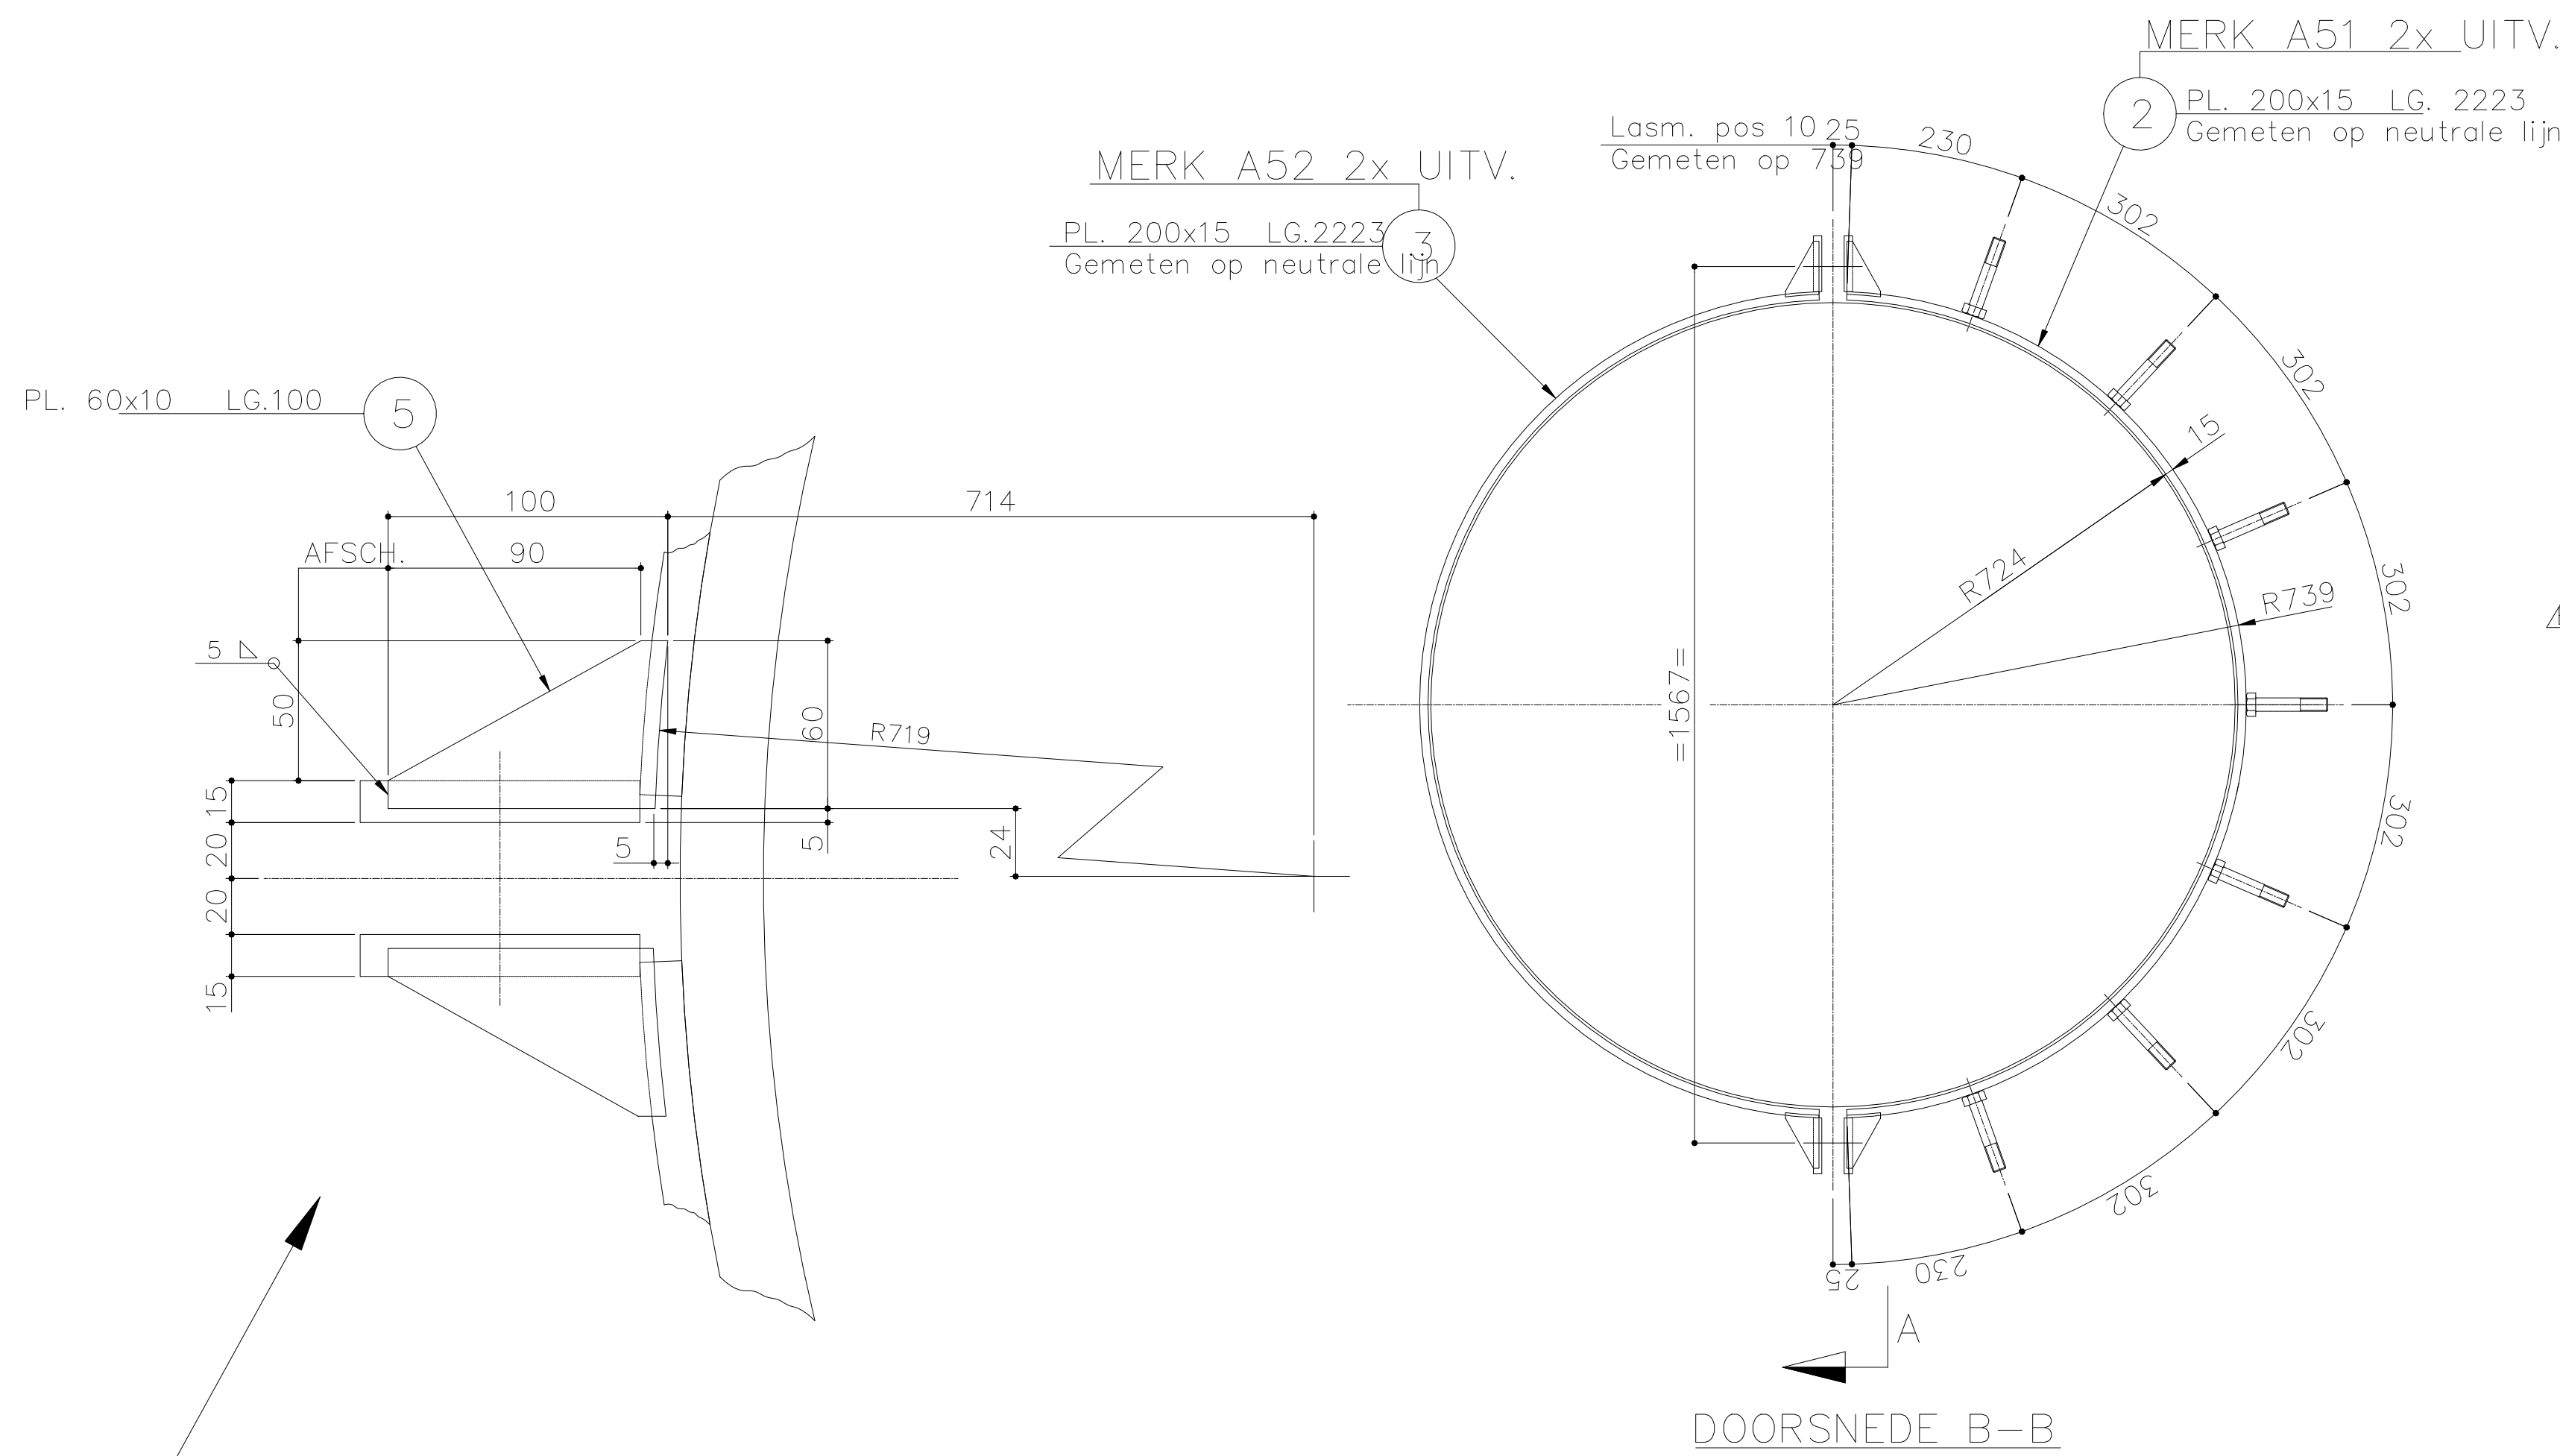


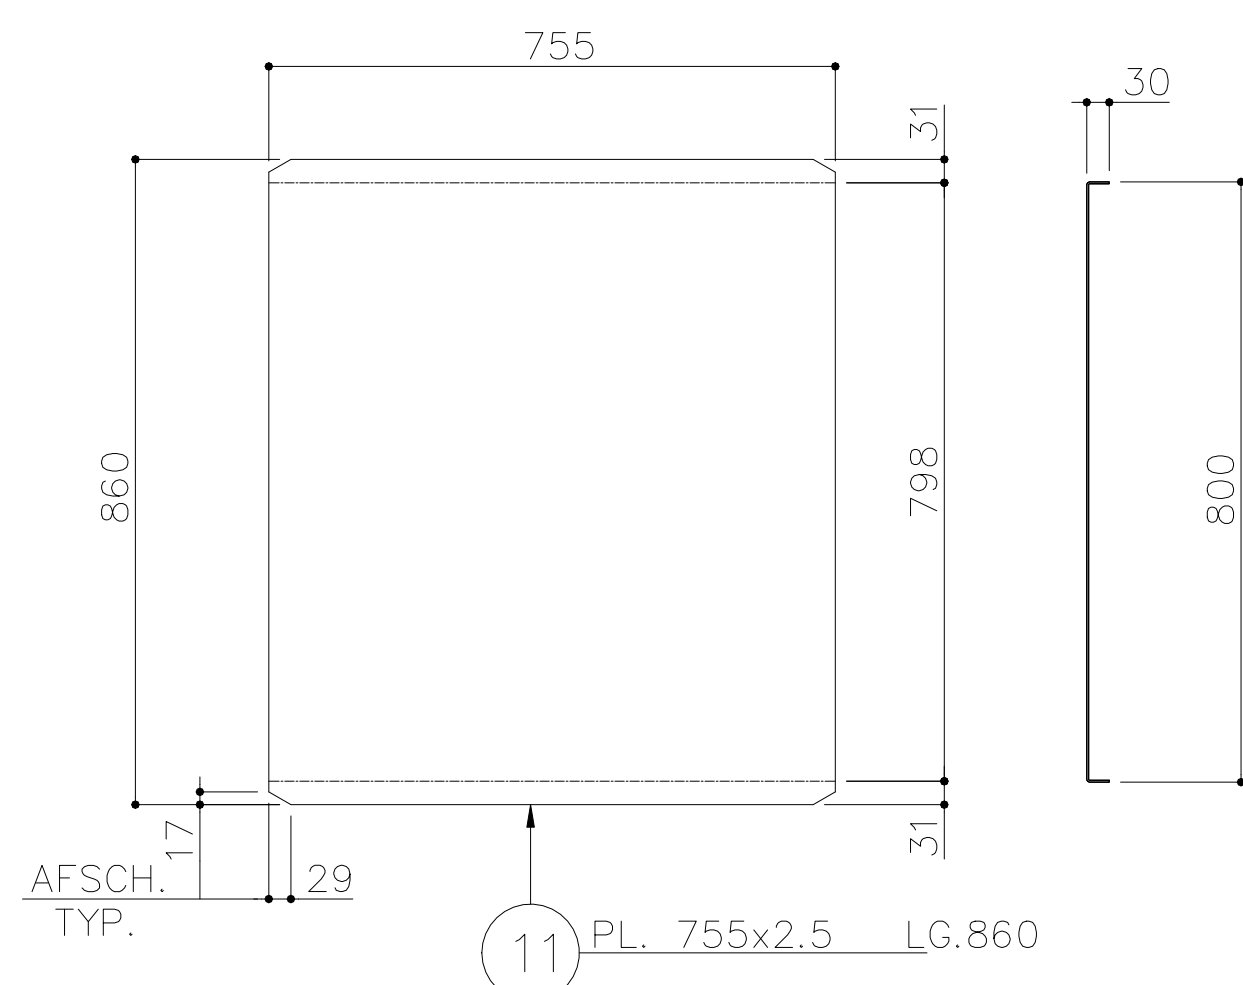

DOORSNEDE B-B

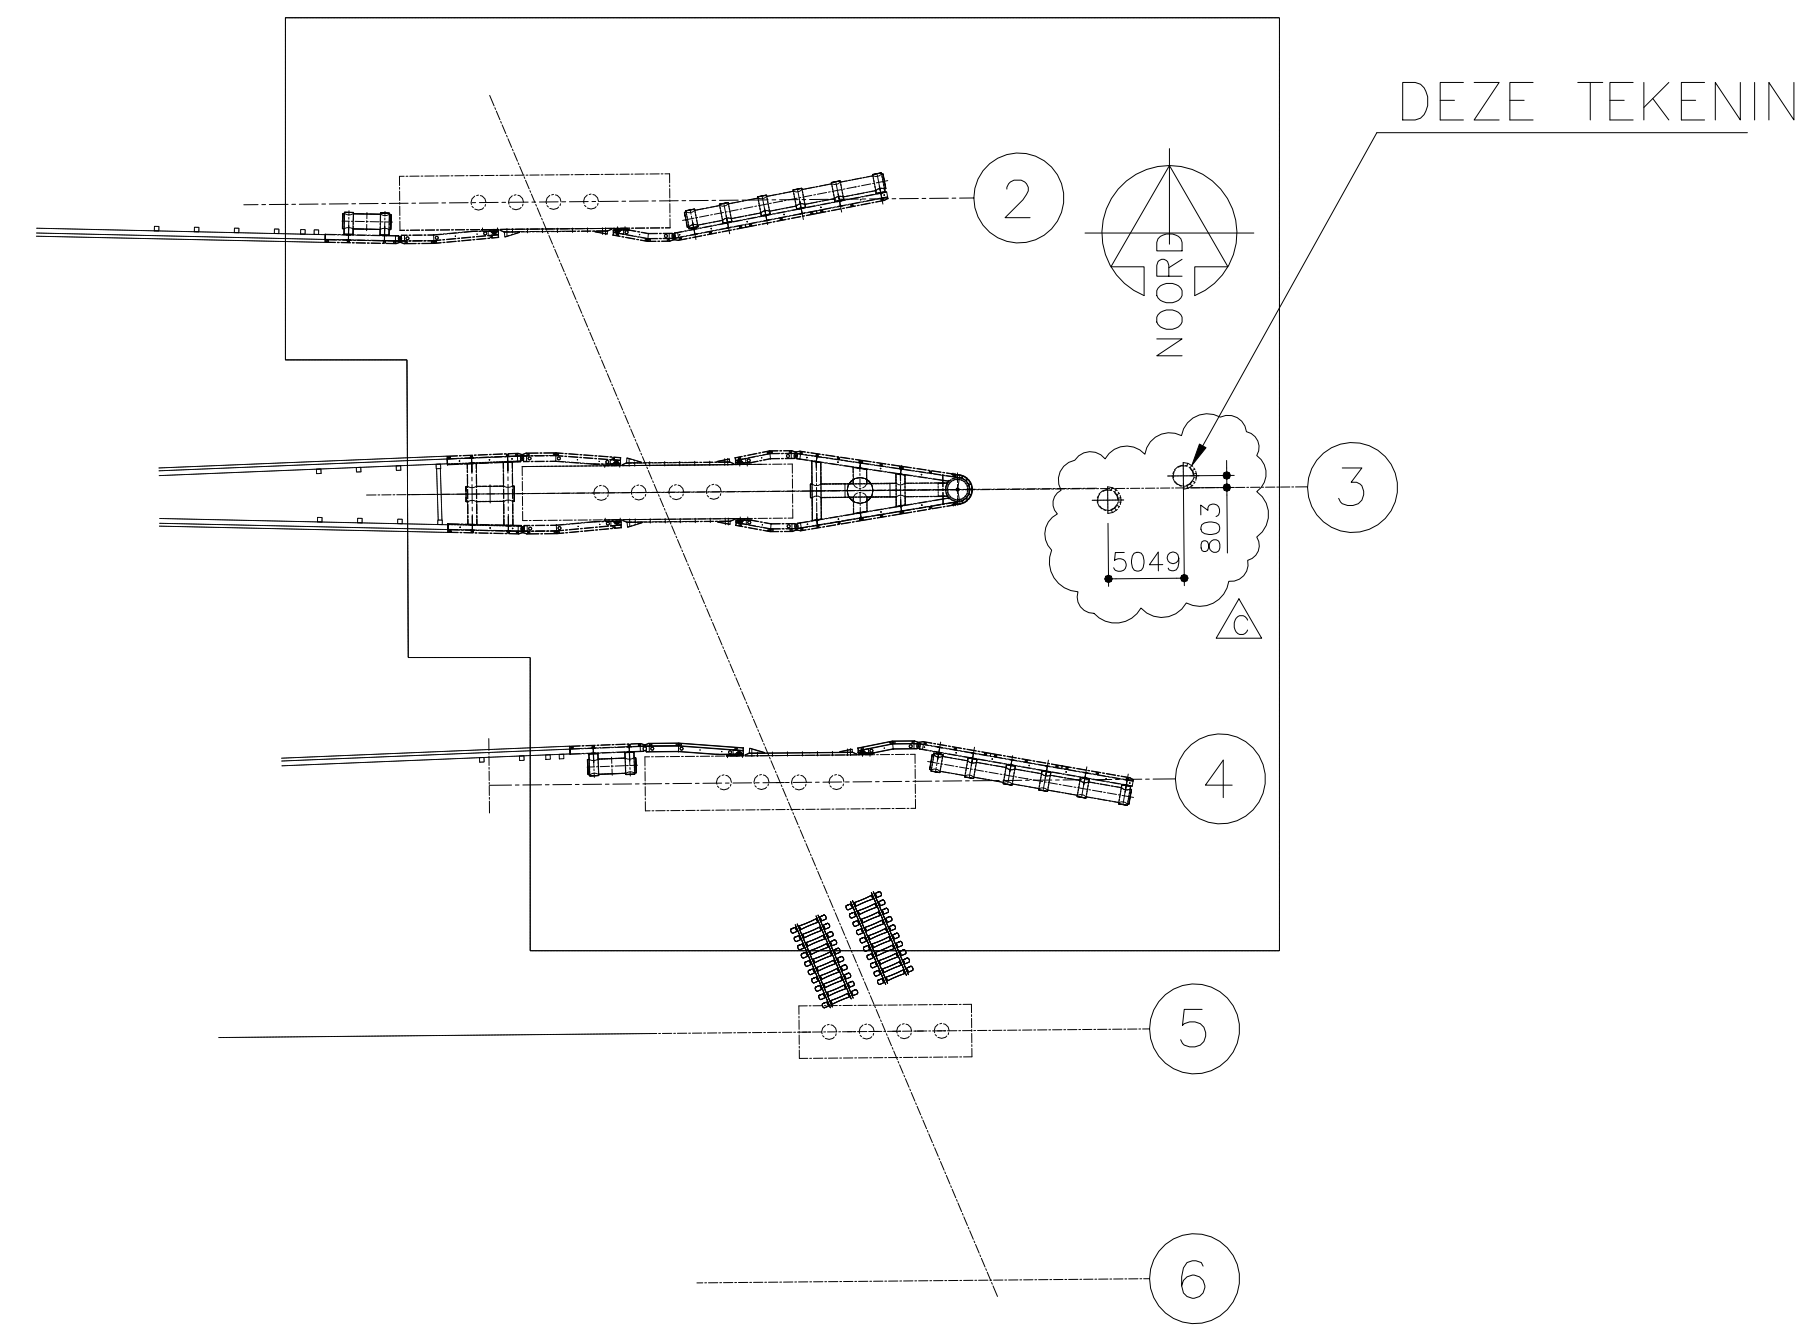

MERK A54 1x UITV.
ROND 45 LG. 890

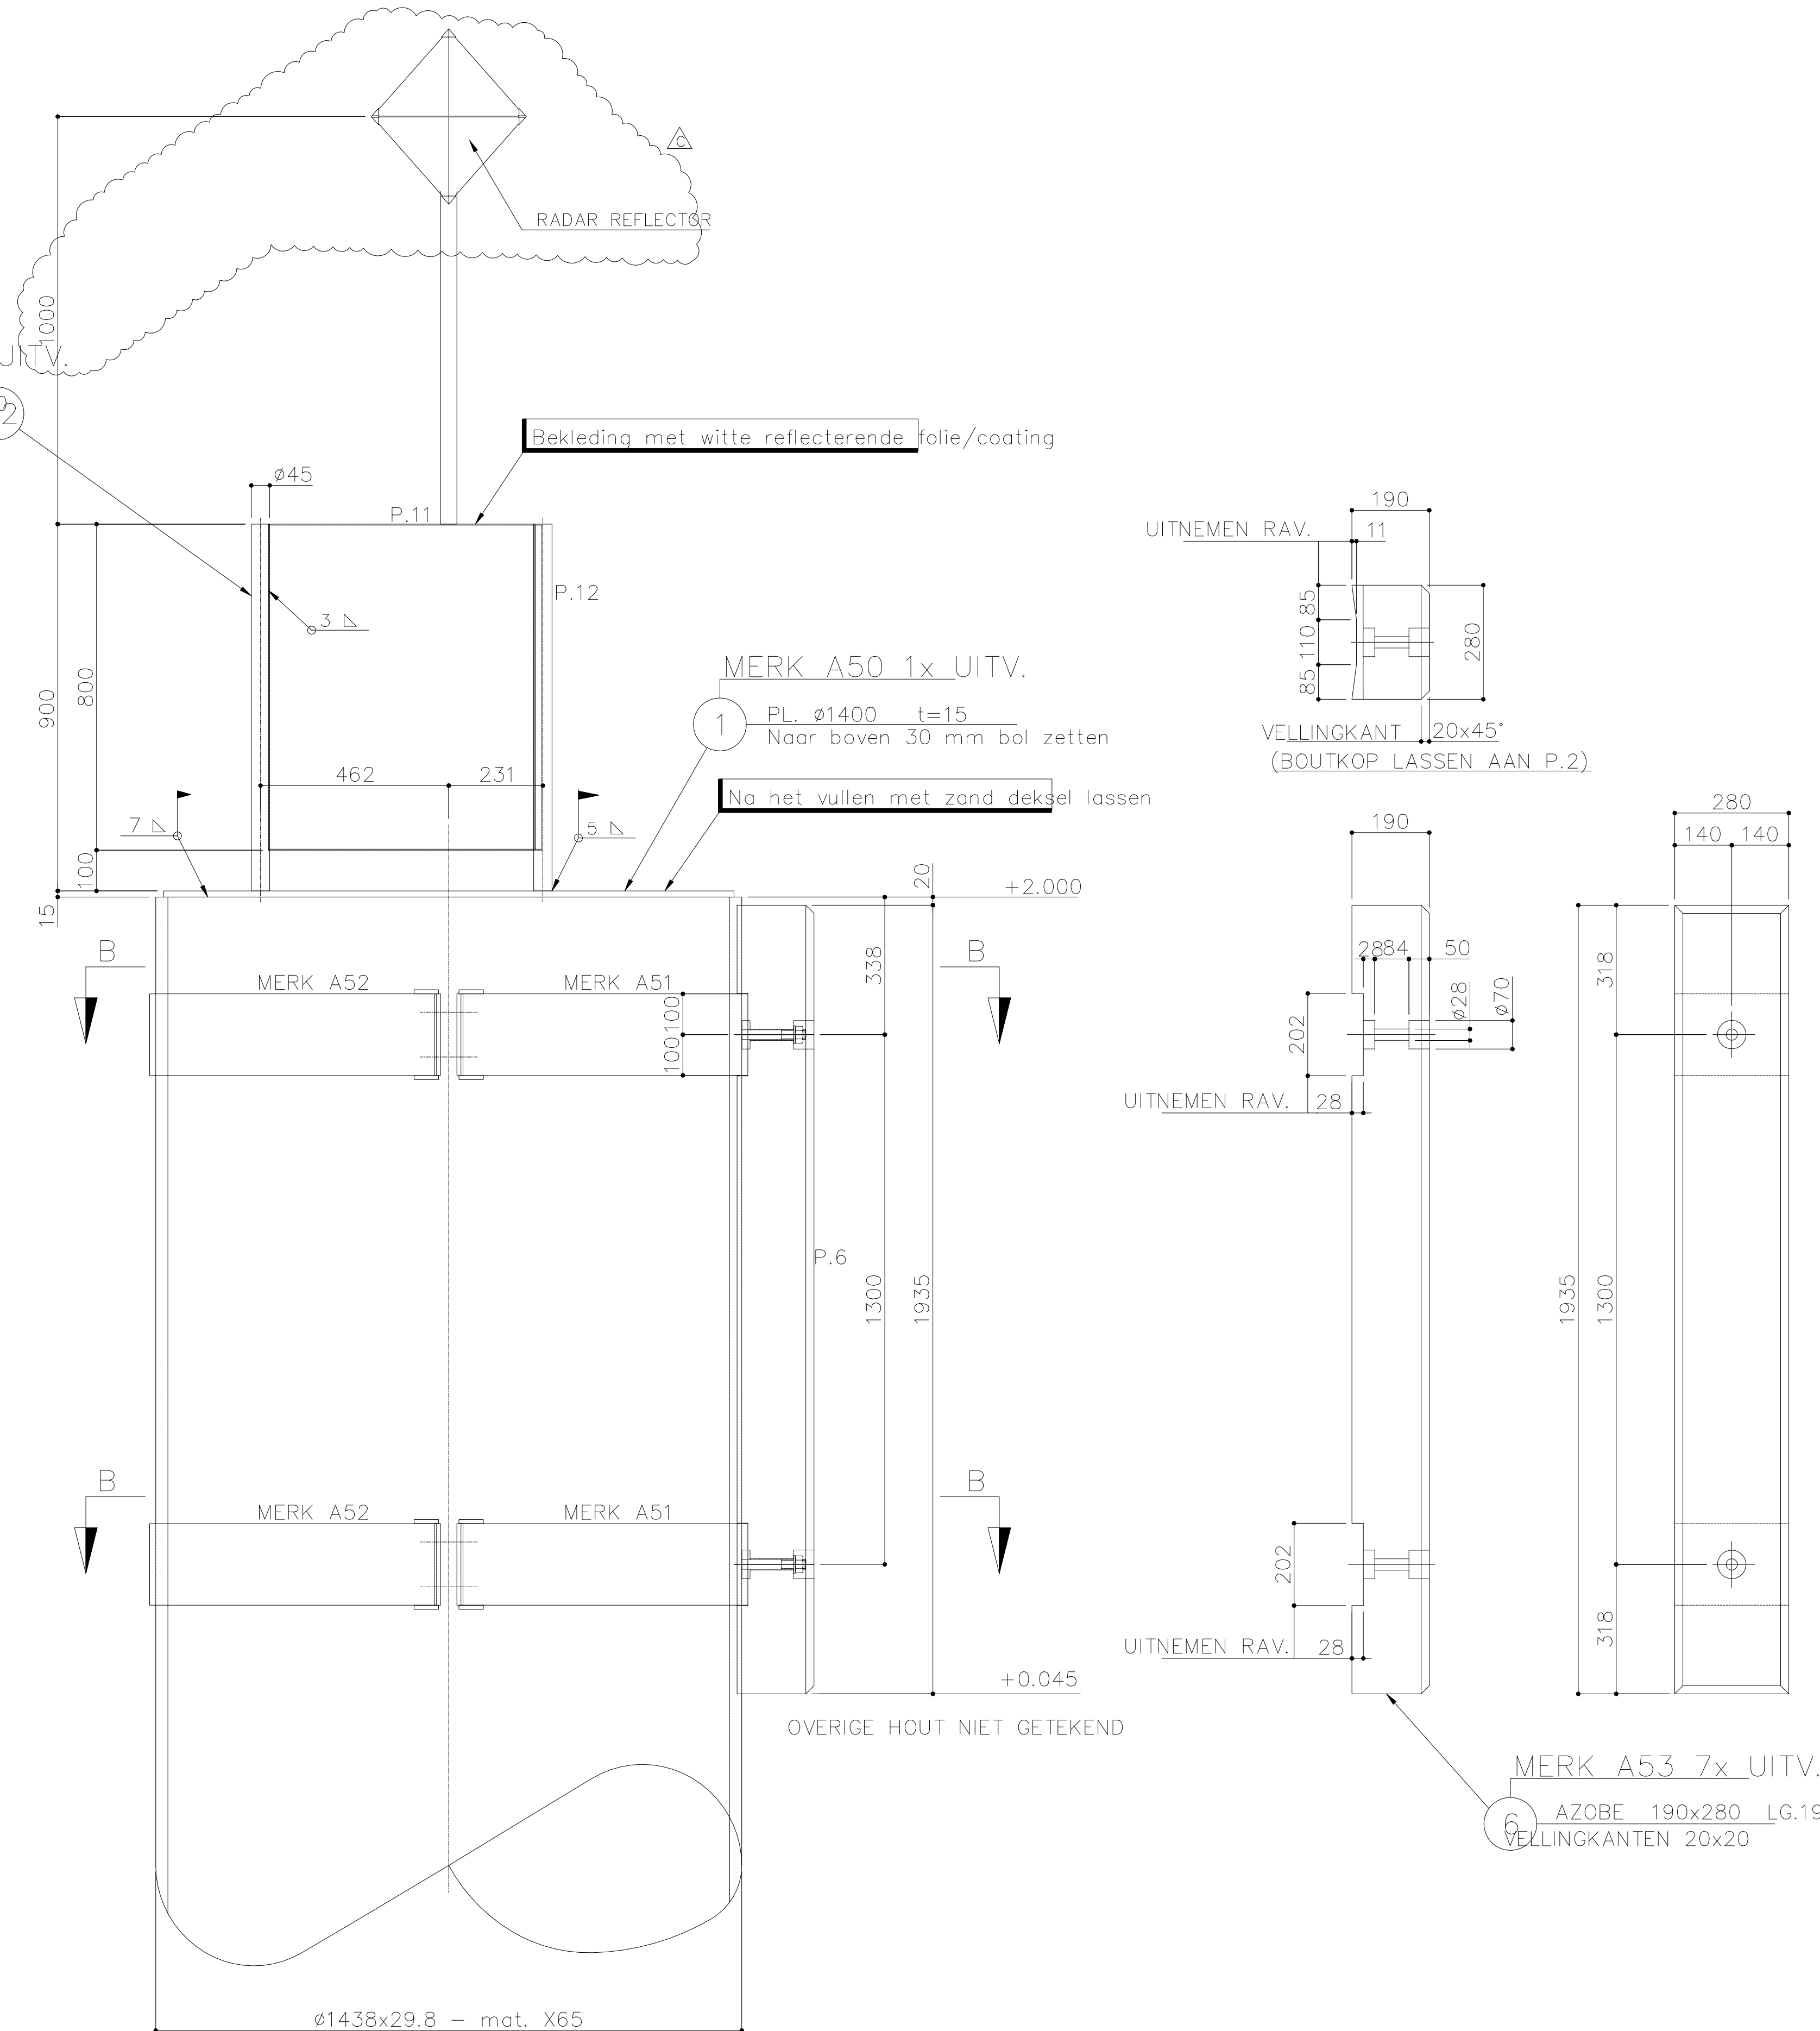

SITUATIE GELEIDEWERK OOSTZIJDE
SCHAAAL 1 : 500

- OPMERKINGEN:
- MATEN IN MILLIMETERS TENZIJ ANDERS VERMELD
 - NIVEAU'S IN METER T.O.V. NAP
 - MATERIAAL S235 TENZIJ ANDERS VERMELD
 - LASSEN 6 TENZIJ ANDERS VERMELD RONDOM
 - CONSERVERING: PALEN CONSERVEREN TOT 1 mtr ONDER BODEMNIVEAU
 - Stralen SA 2½
 - 1^{ste} laag 75 µm AMERCOAT 235
 - 2^{de} laag 150 µm AMERCOAT 235
 - 3^{de} laag 150 µm AMERLOCK 400C - RAL 7043

POS: 1 t/m 12
MERKEN: A50 t/m A54

STUKLIJST Nr. 03
BOUTENLIJST Nr. 03

C	20-03-2008	AS BUILT	P.v.T.	HvdM
B	10-01-2008	als aangegeven	H.Tu	
A	09-01-2008	aanpassing i.v.m. pool	H.Tu	
D	27-11-2007	Eerste uitgave	H.S	
Wijz.	Datum	Omschrijving	Get.	Gez.
Volker Staal en Funderingen bv				
TECHNISCH BUREAU				
Auteursrecht voorbehouden volgens de wet.				
OPDRACHTGEVER: WATERSCHAP BRABANTSE DELTA				
PROJECT: DE MARK UPGRADING REMMINGWERK				
BENAMING: WRIJFHOUT AAN WAARSCHUWINGSPAAL				
TEKENING NR.: W1045-03				
Bijz.: School: 1:2 1:10 1:500 Datum: 27-11-2007 Get.: H. Sliker Gez.: Formaat: A0				
Volker Staal en Funderingen bv Quarantaineweg 10 3088 KP Rotterdam Postbus 64548 3008 KA Rotterdam Telefoon 010-2992288 Telefax 010-2992277 Handelsreg. Rotterdam 24229578				