
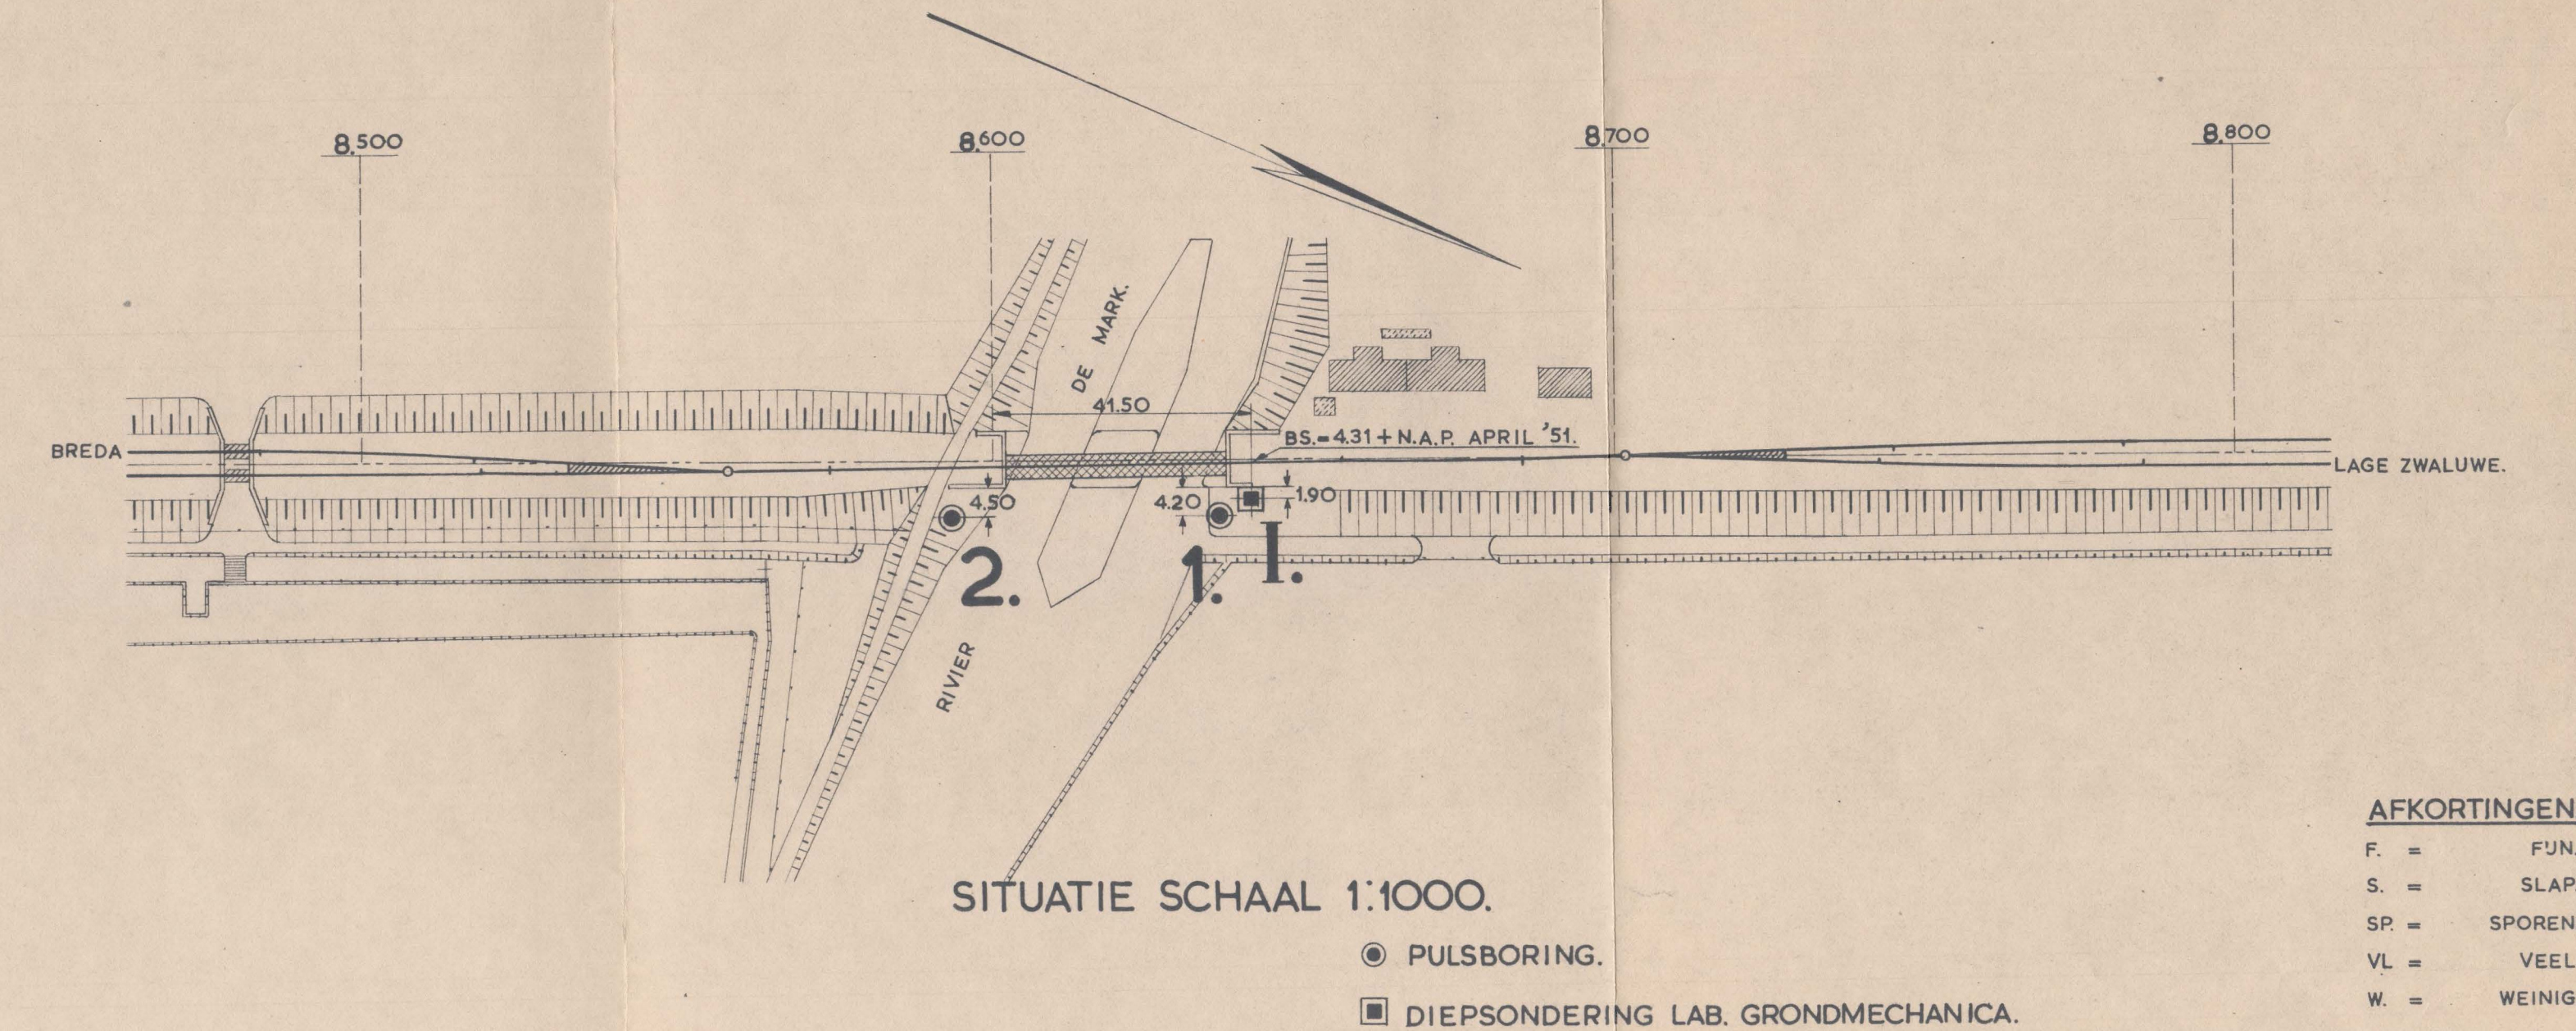


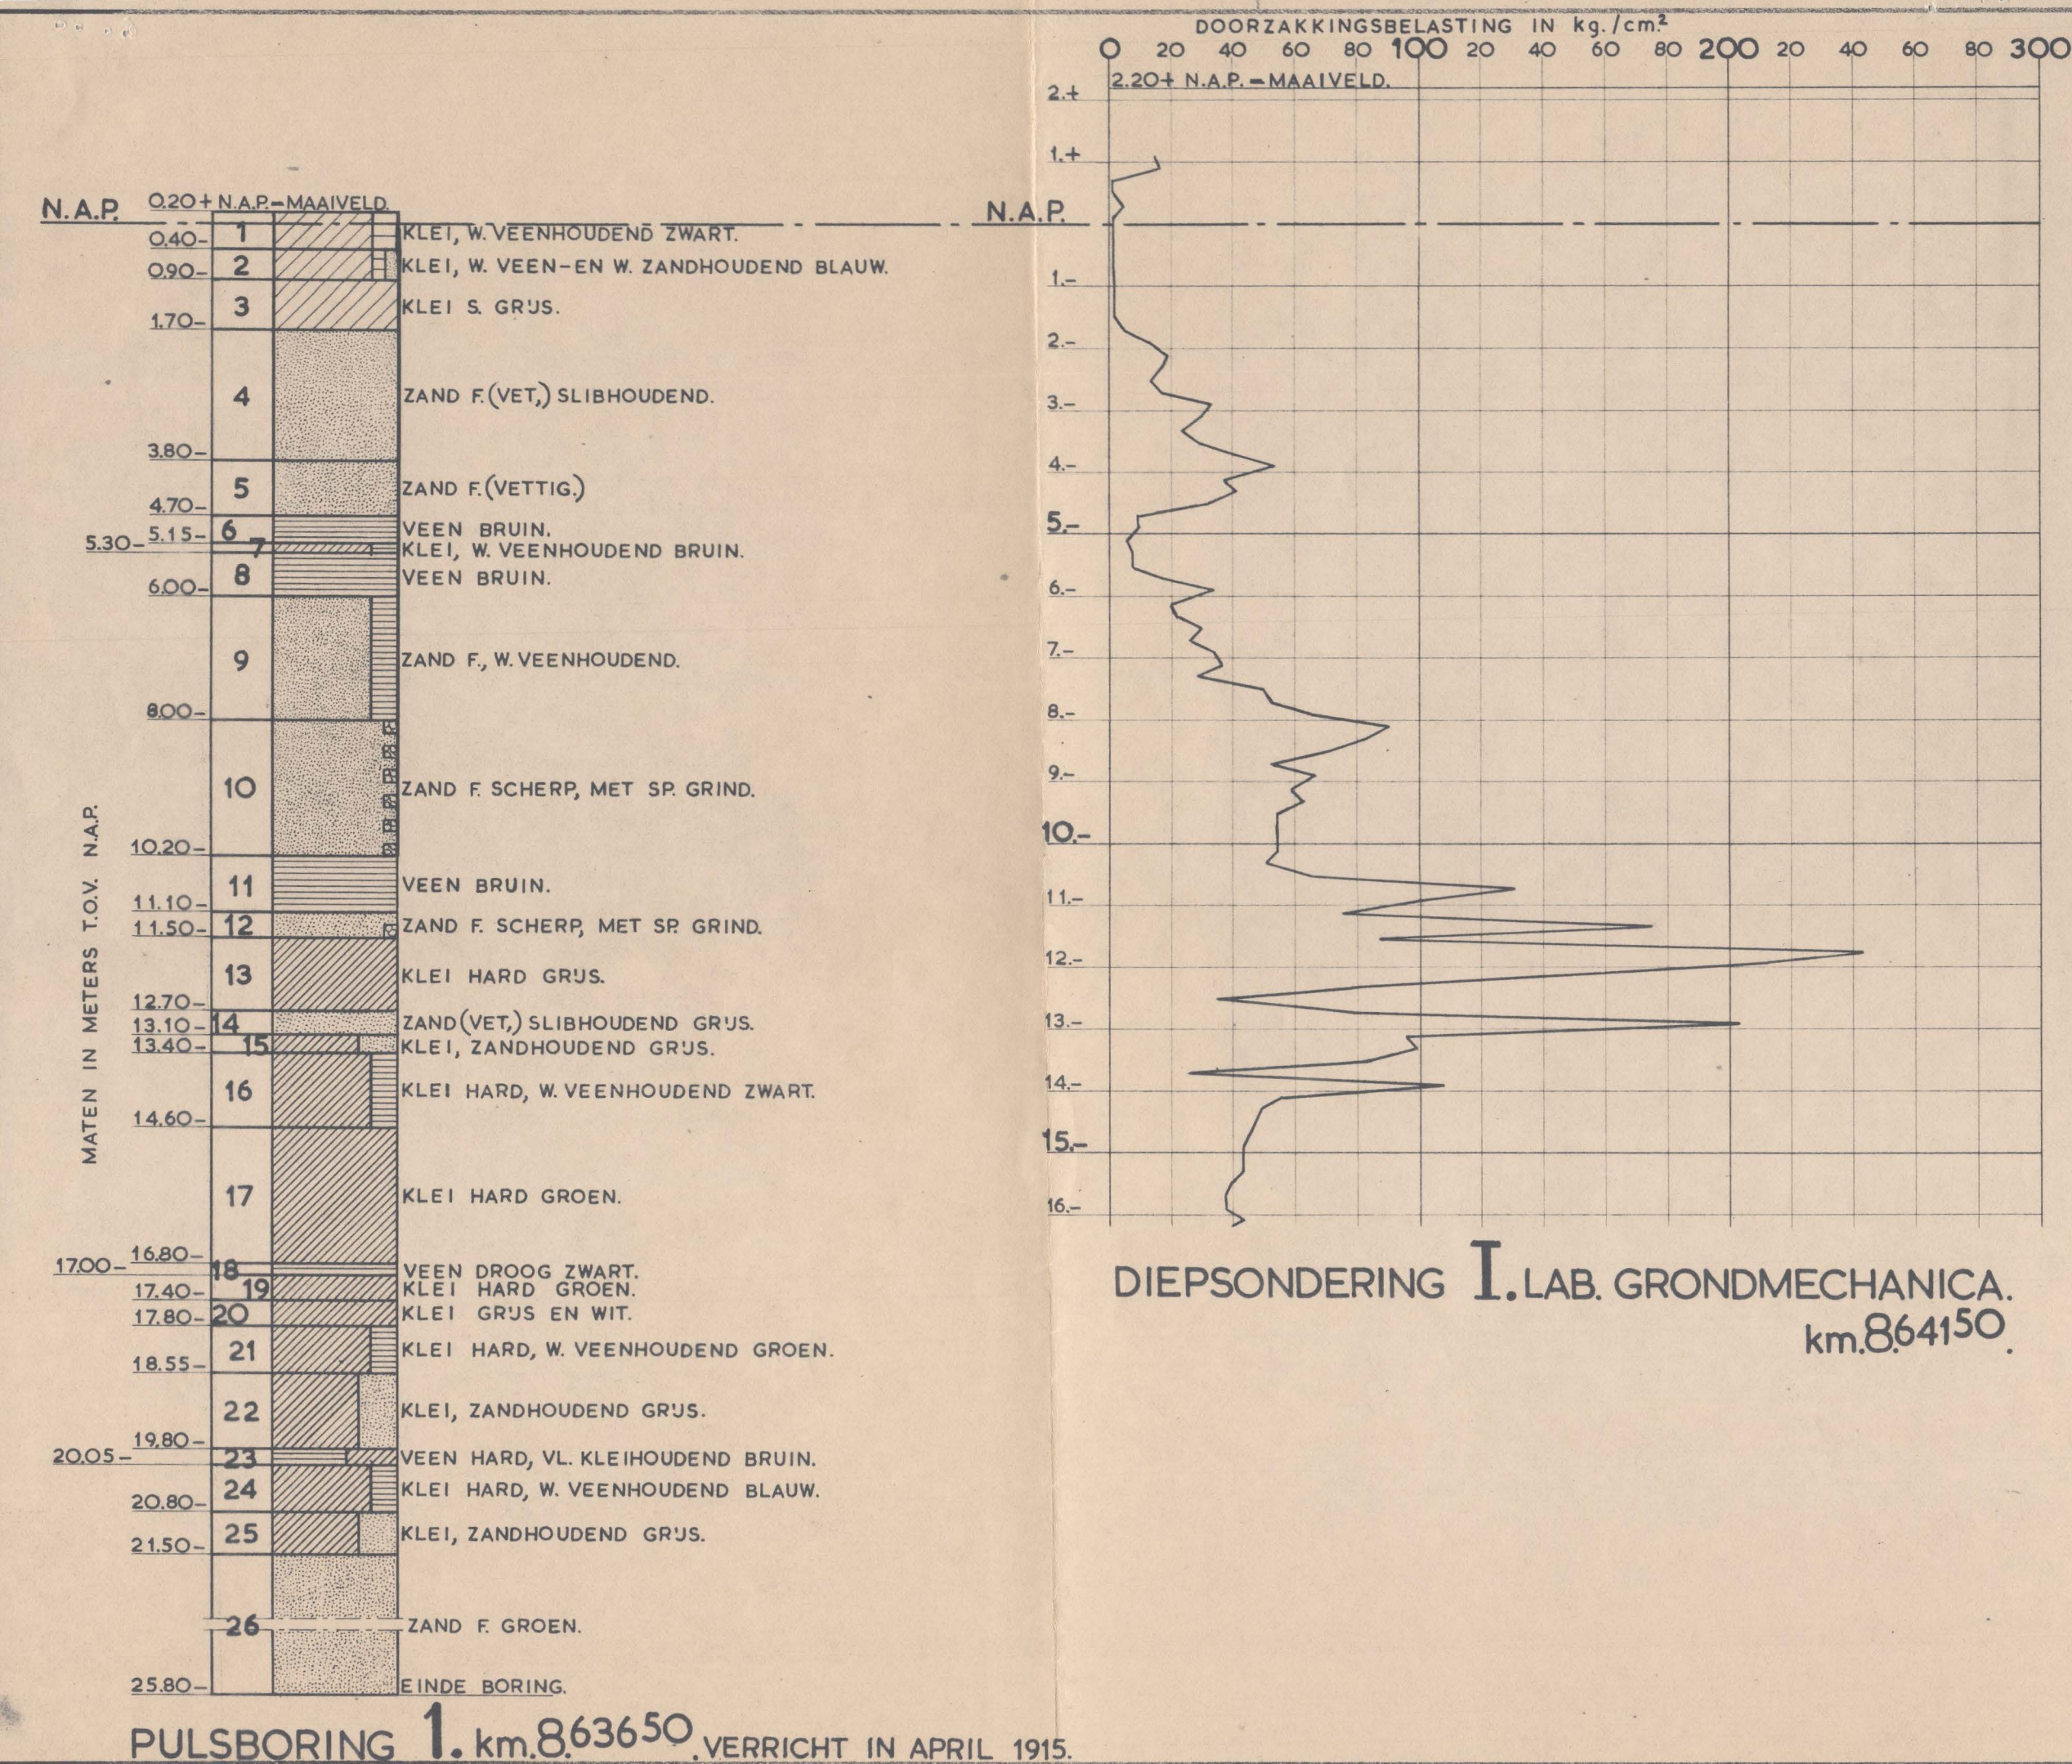

MATEN IN METERS.			
N.V. NEDERLANDSCHE SPOORWEGEN DIENST VAN WEG EN WERKEN AFD. BAANBOUW W.W. 8			
LIJN: BREDA — LAGE ZWALUWE.			ARCHIEF
KNOOPP.:			BODEMONDERZO
● No. 1 en 2. ● No. ■ No. ◆ No. ■ No. I.	TEN BEHOEVE VAN: GEWAPEND BETON REM- MINGWERK VOOR BRUG 0/d MARK. km. 8,64150 SCHAAAL: 1:100 en 1:1000 GEZ.: <i>M</i>	geb.: ges.: LAB. GROND. get.: BROUWER. gew.: gew.:	4-15. 4-51. 4-51. 2. VOLGNo. BOORSTAAT:
BEHOORT BIJ BRIEF:			LIJN-KNOOP No. 12