




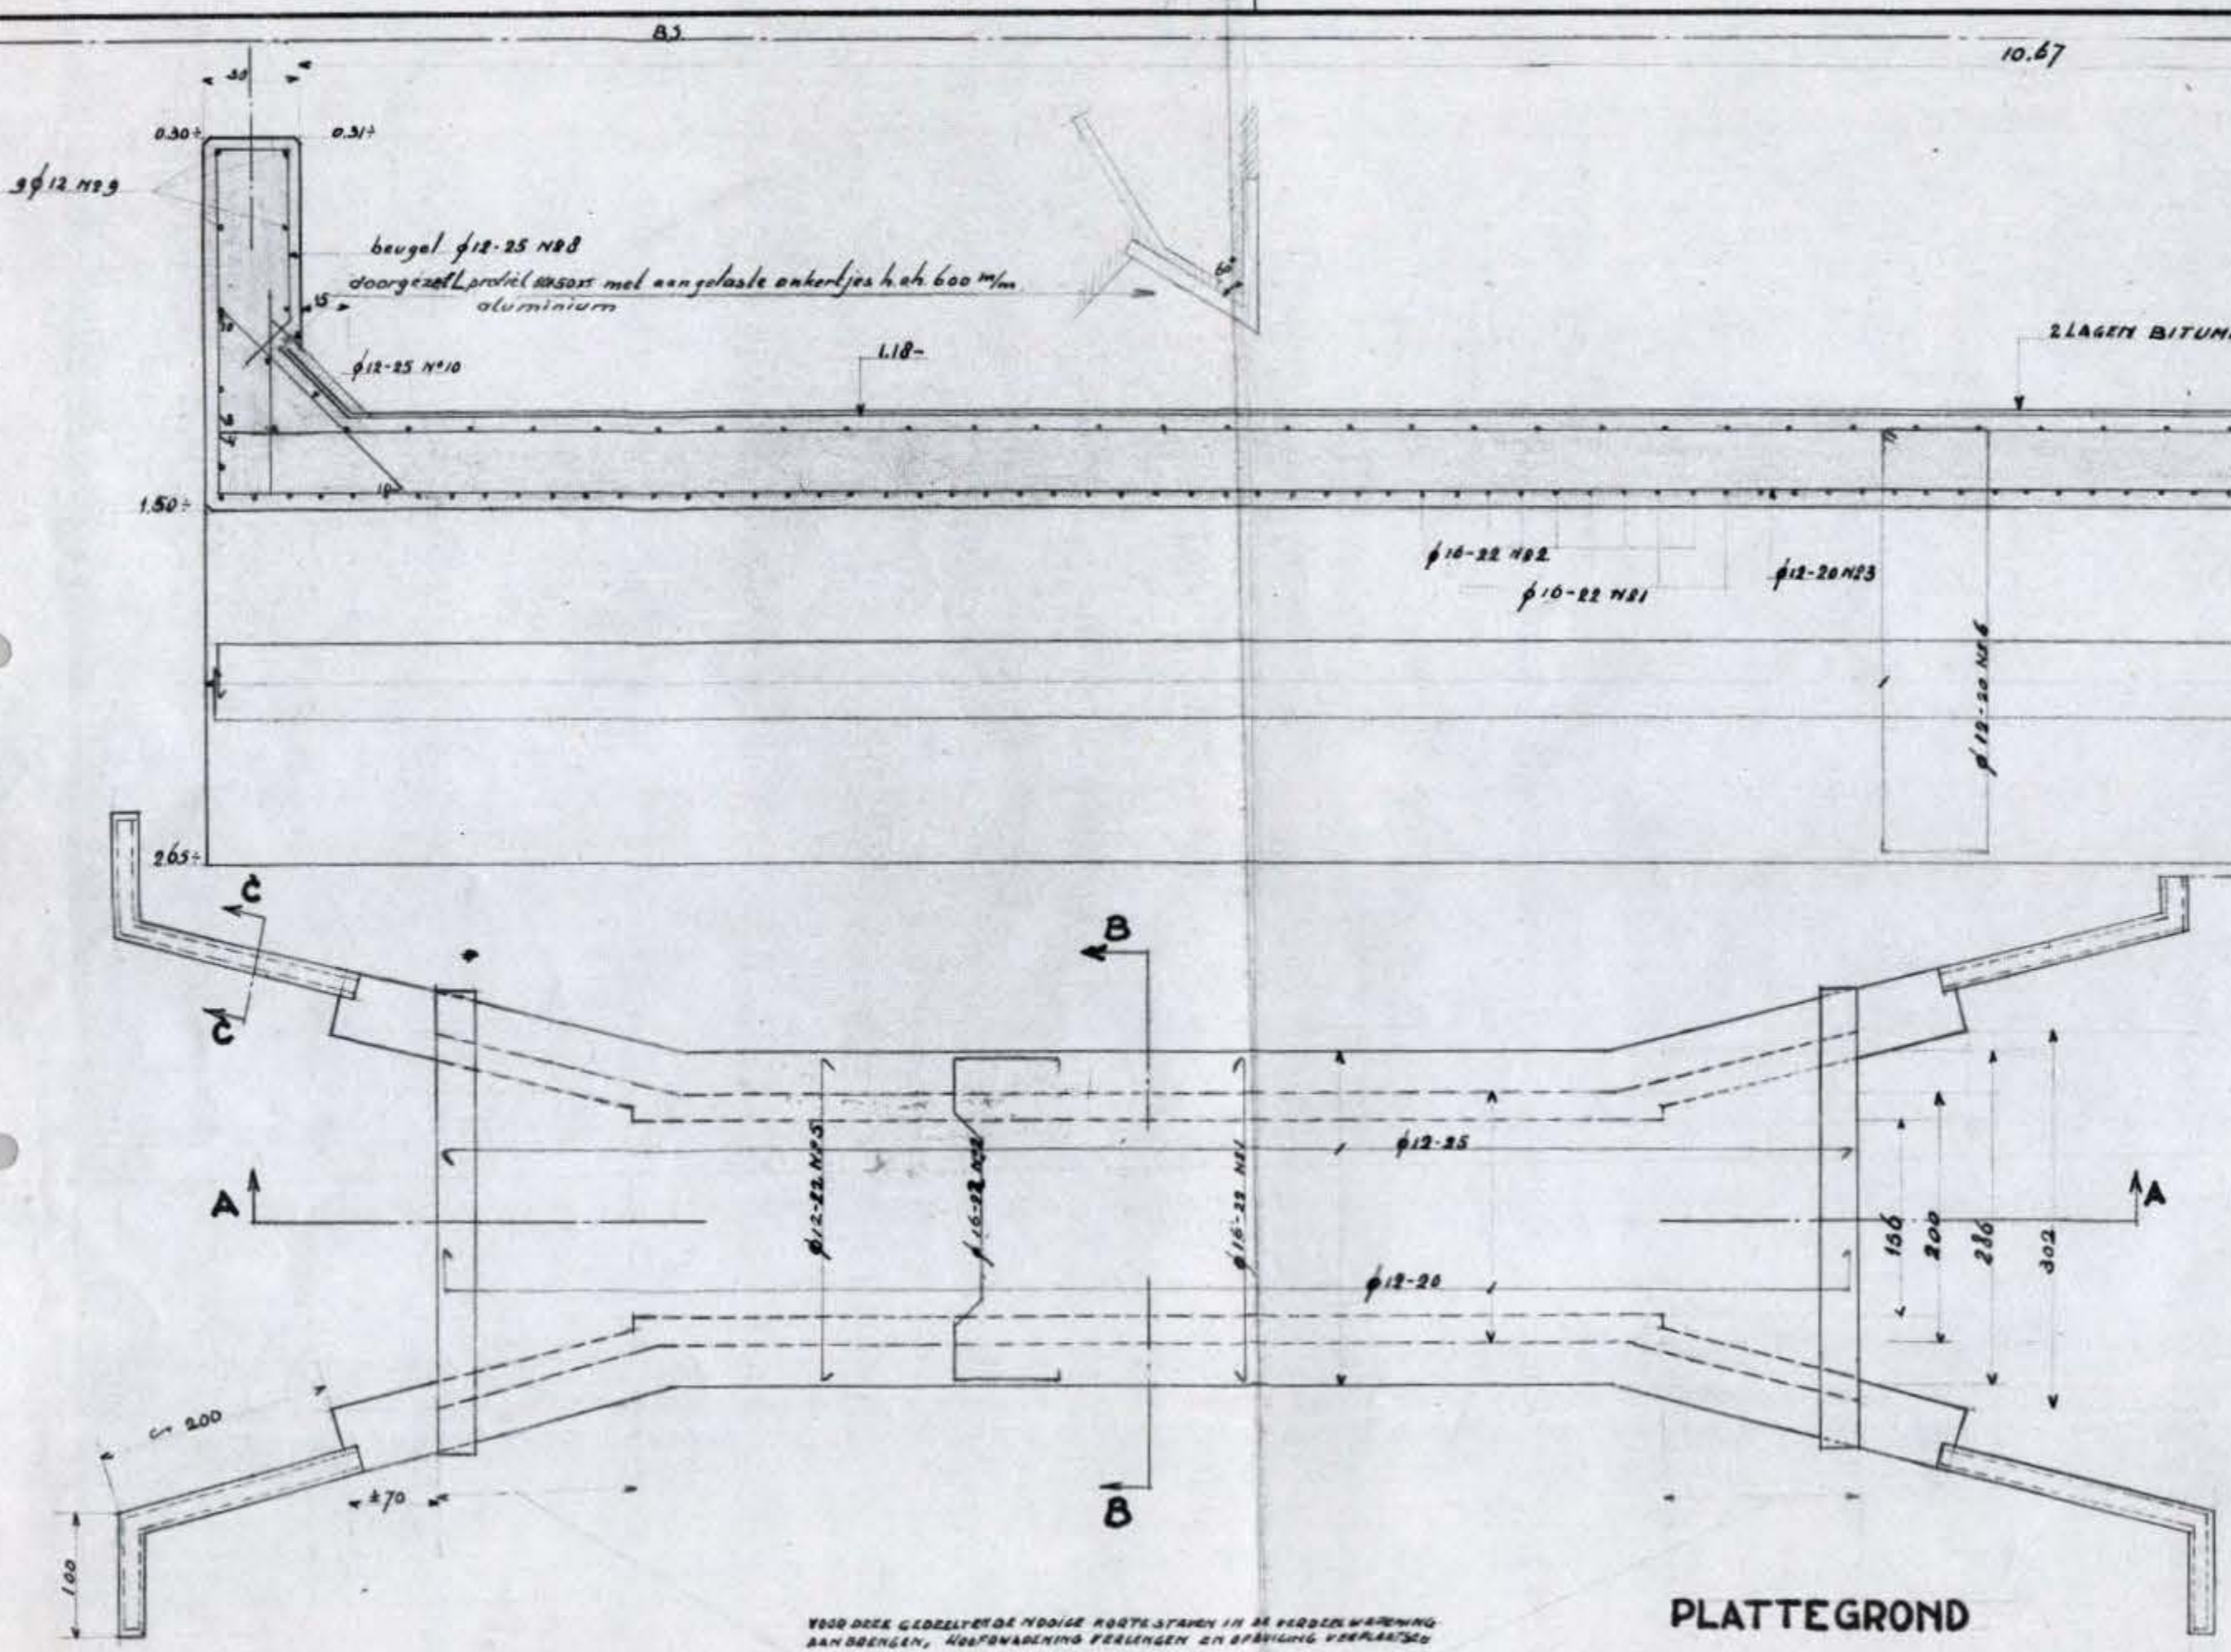


PLATTEGROND

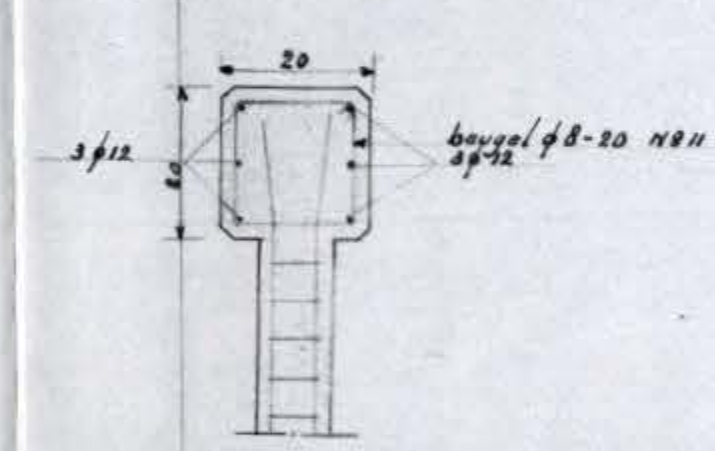


DOORSNEDE AA

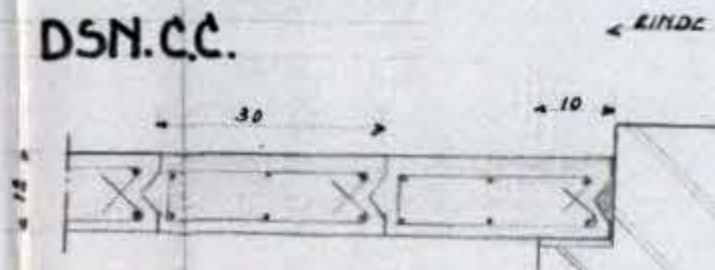

AANSLUITING DAM-WAND AAN VLEUGEL

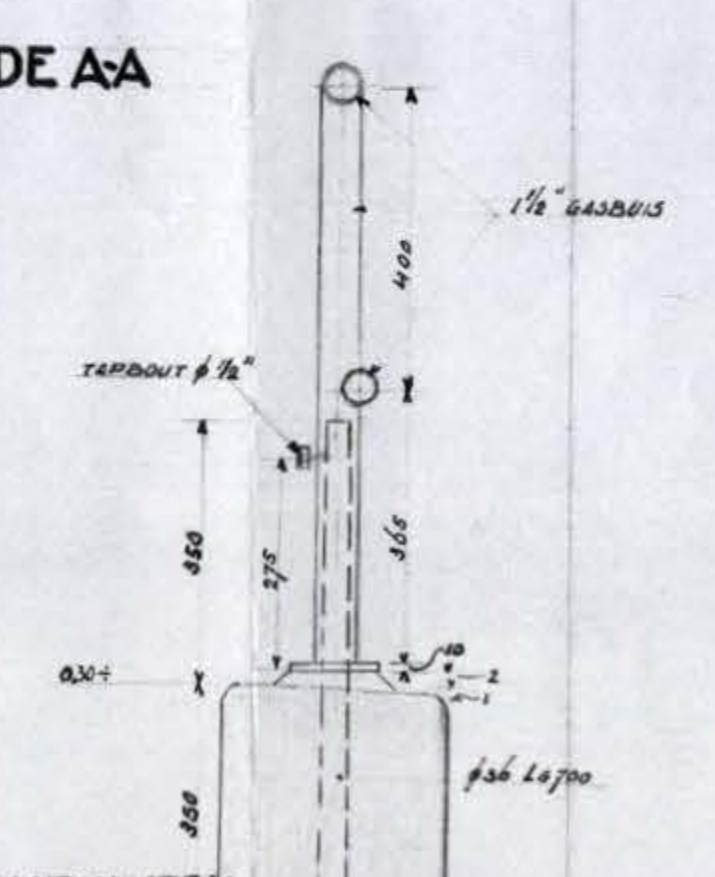

DSN.OVER HEKWERK

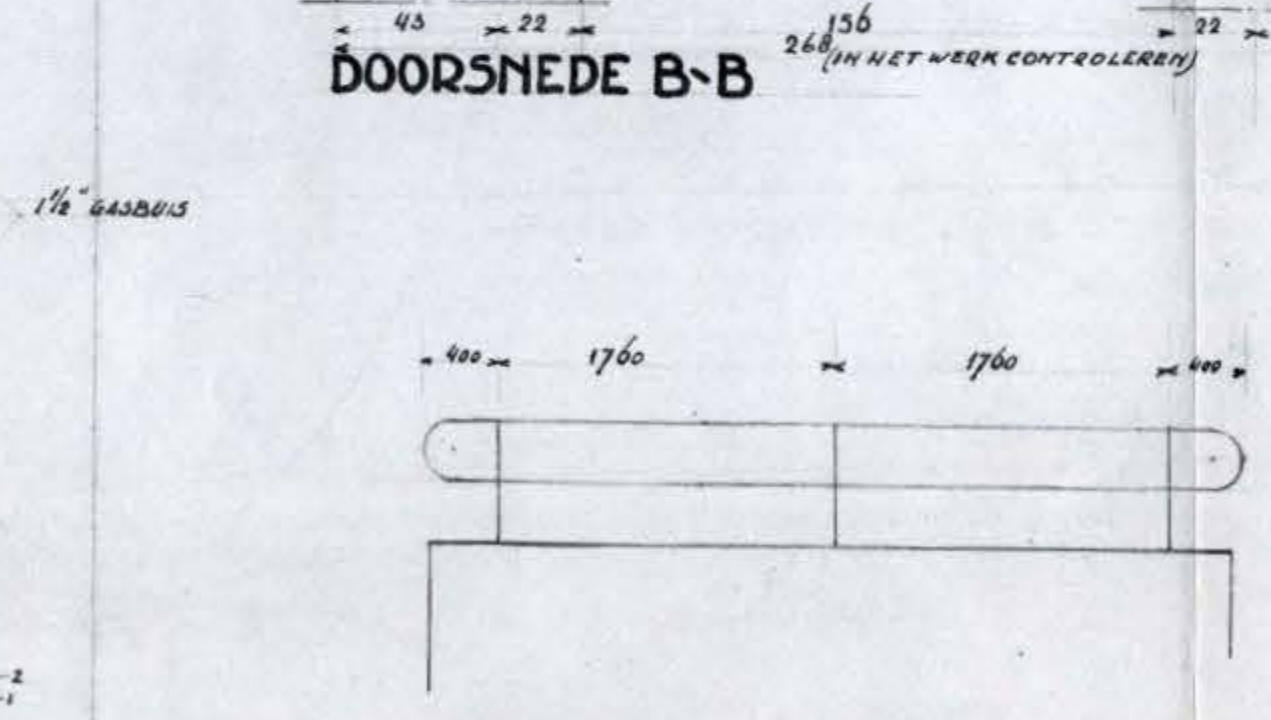

DOORSNEDE B-B

AANZICHT HEKWERK

CEMENT KLASSE 3
BETONSTAAL Q235
BETONDEKING 3.5 CM
MINIMUM KUBUSSTERKTE 170 N/mm² (BLOK 250 N/mm²)
MIN. BUIKTREKSTERKTE 170 N/mm² (BLOK 250 N/mm²)
MET BETONCONTROLS

VERKLARING:
MATEN IN CM
STAALMATEN IN MM
HOOGTEMATEN IN M LOK. B3
— NIJUM WERK
— BESTAAND WERK
— BETON D
— METSELWERK

BLUJEND ARCHIEF Ww
23.03.2018
Collo
Bijlage No. 7

Nº	VAK	OMSCHRIJVING VAN DE WIJZIGING	NAAM	DATUM	GEZ.
N.V. NEDERLANDSCHE SPOORWEGEN					
DIENST VAN DE EXPLOITATIE					
INSPECTIE BREDA					
ROOSENDAAL- BREDA			BESTEK	GET. CREMERS 16 MRT '90	
WUZIGEN DUIKER BJKm10.68			Nº	NS	
DETAILS			AFGEGEVEN V/D UITVOERING	NAAM	DATUM
SCHAAL 1A50 · 1A20 · 1A10			BLAD	EP	Nº
CODERING 416/22 / 12 232 / 2 10 232 / 11 232					