



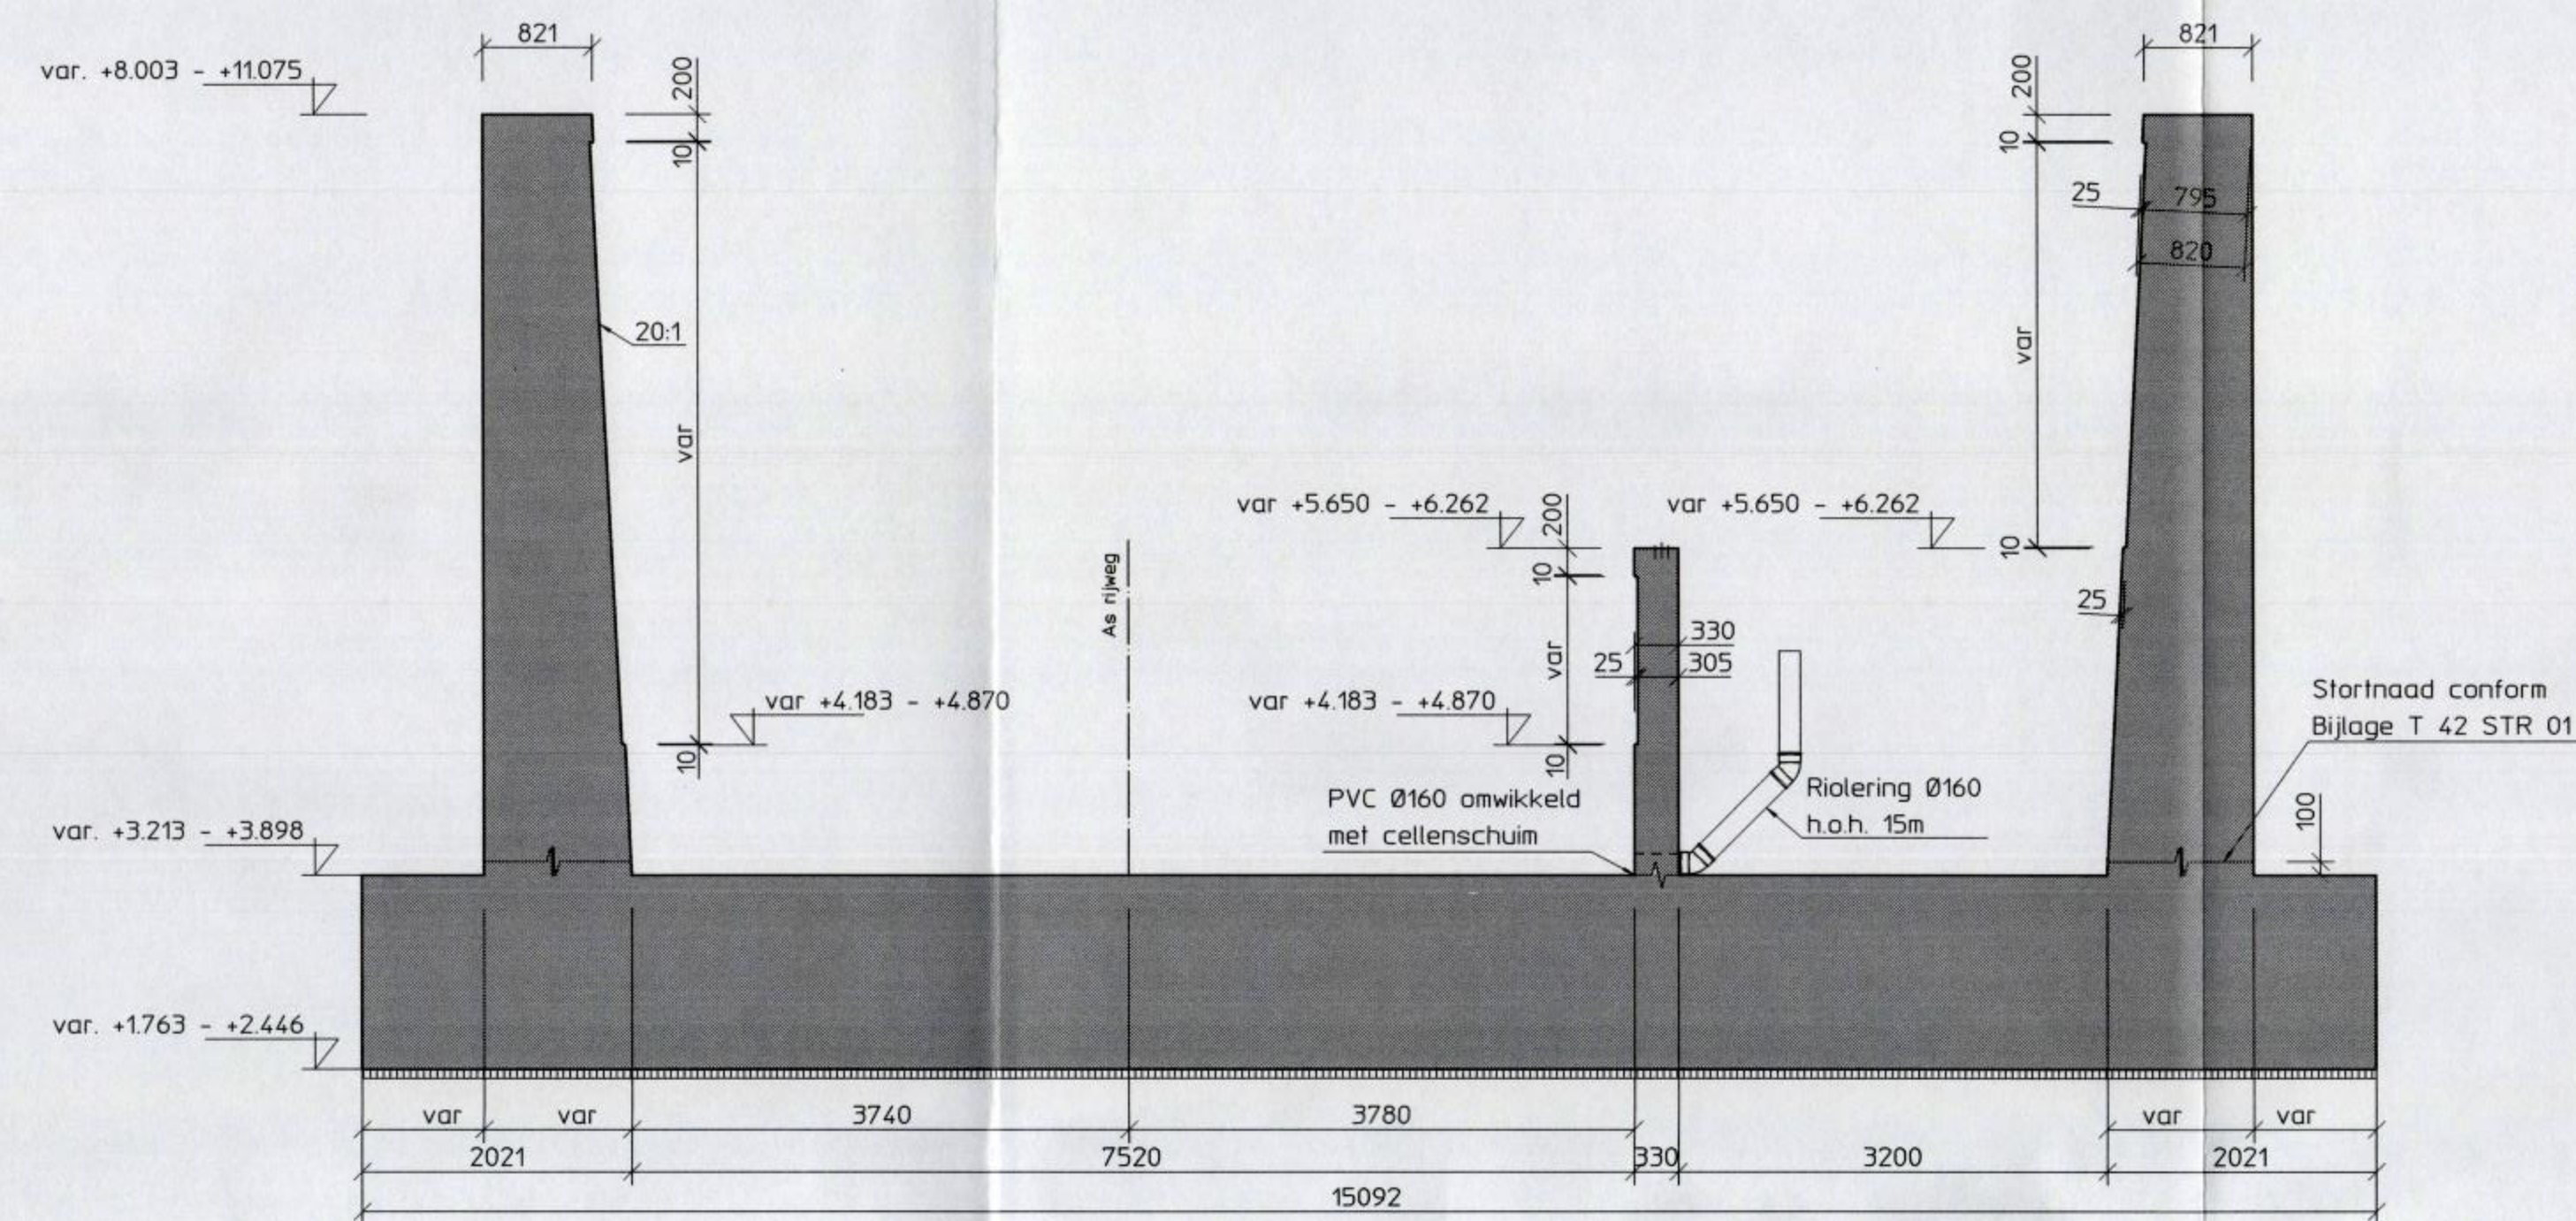


Doorsnede D

Schaal 150

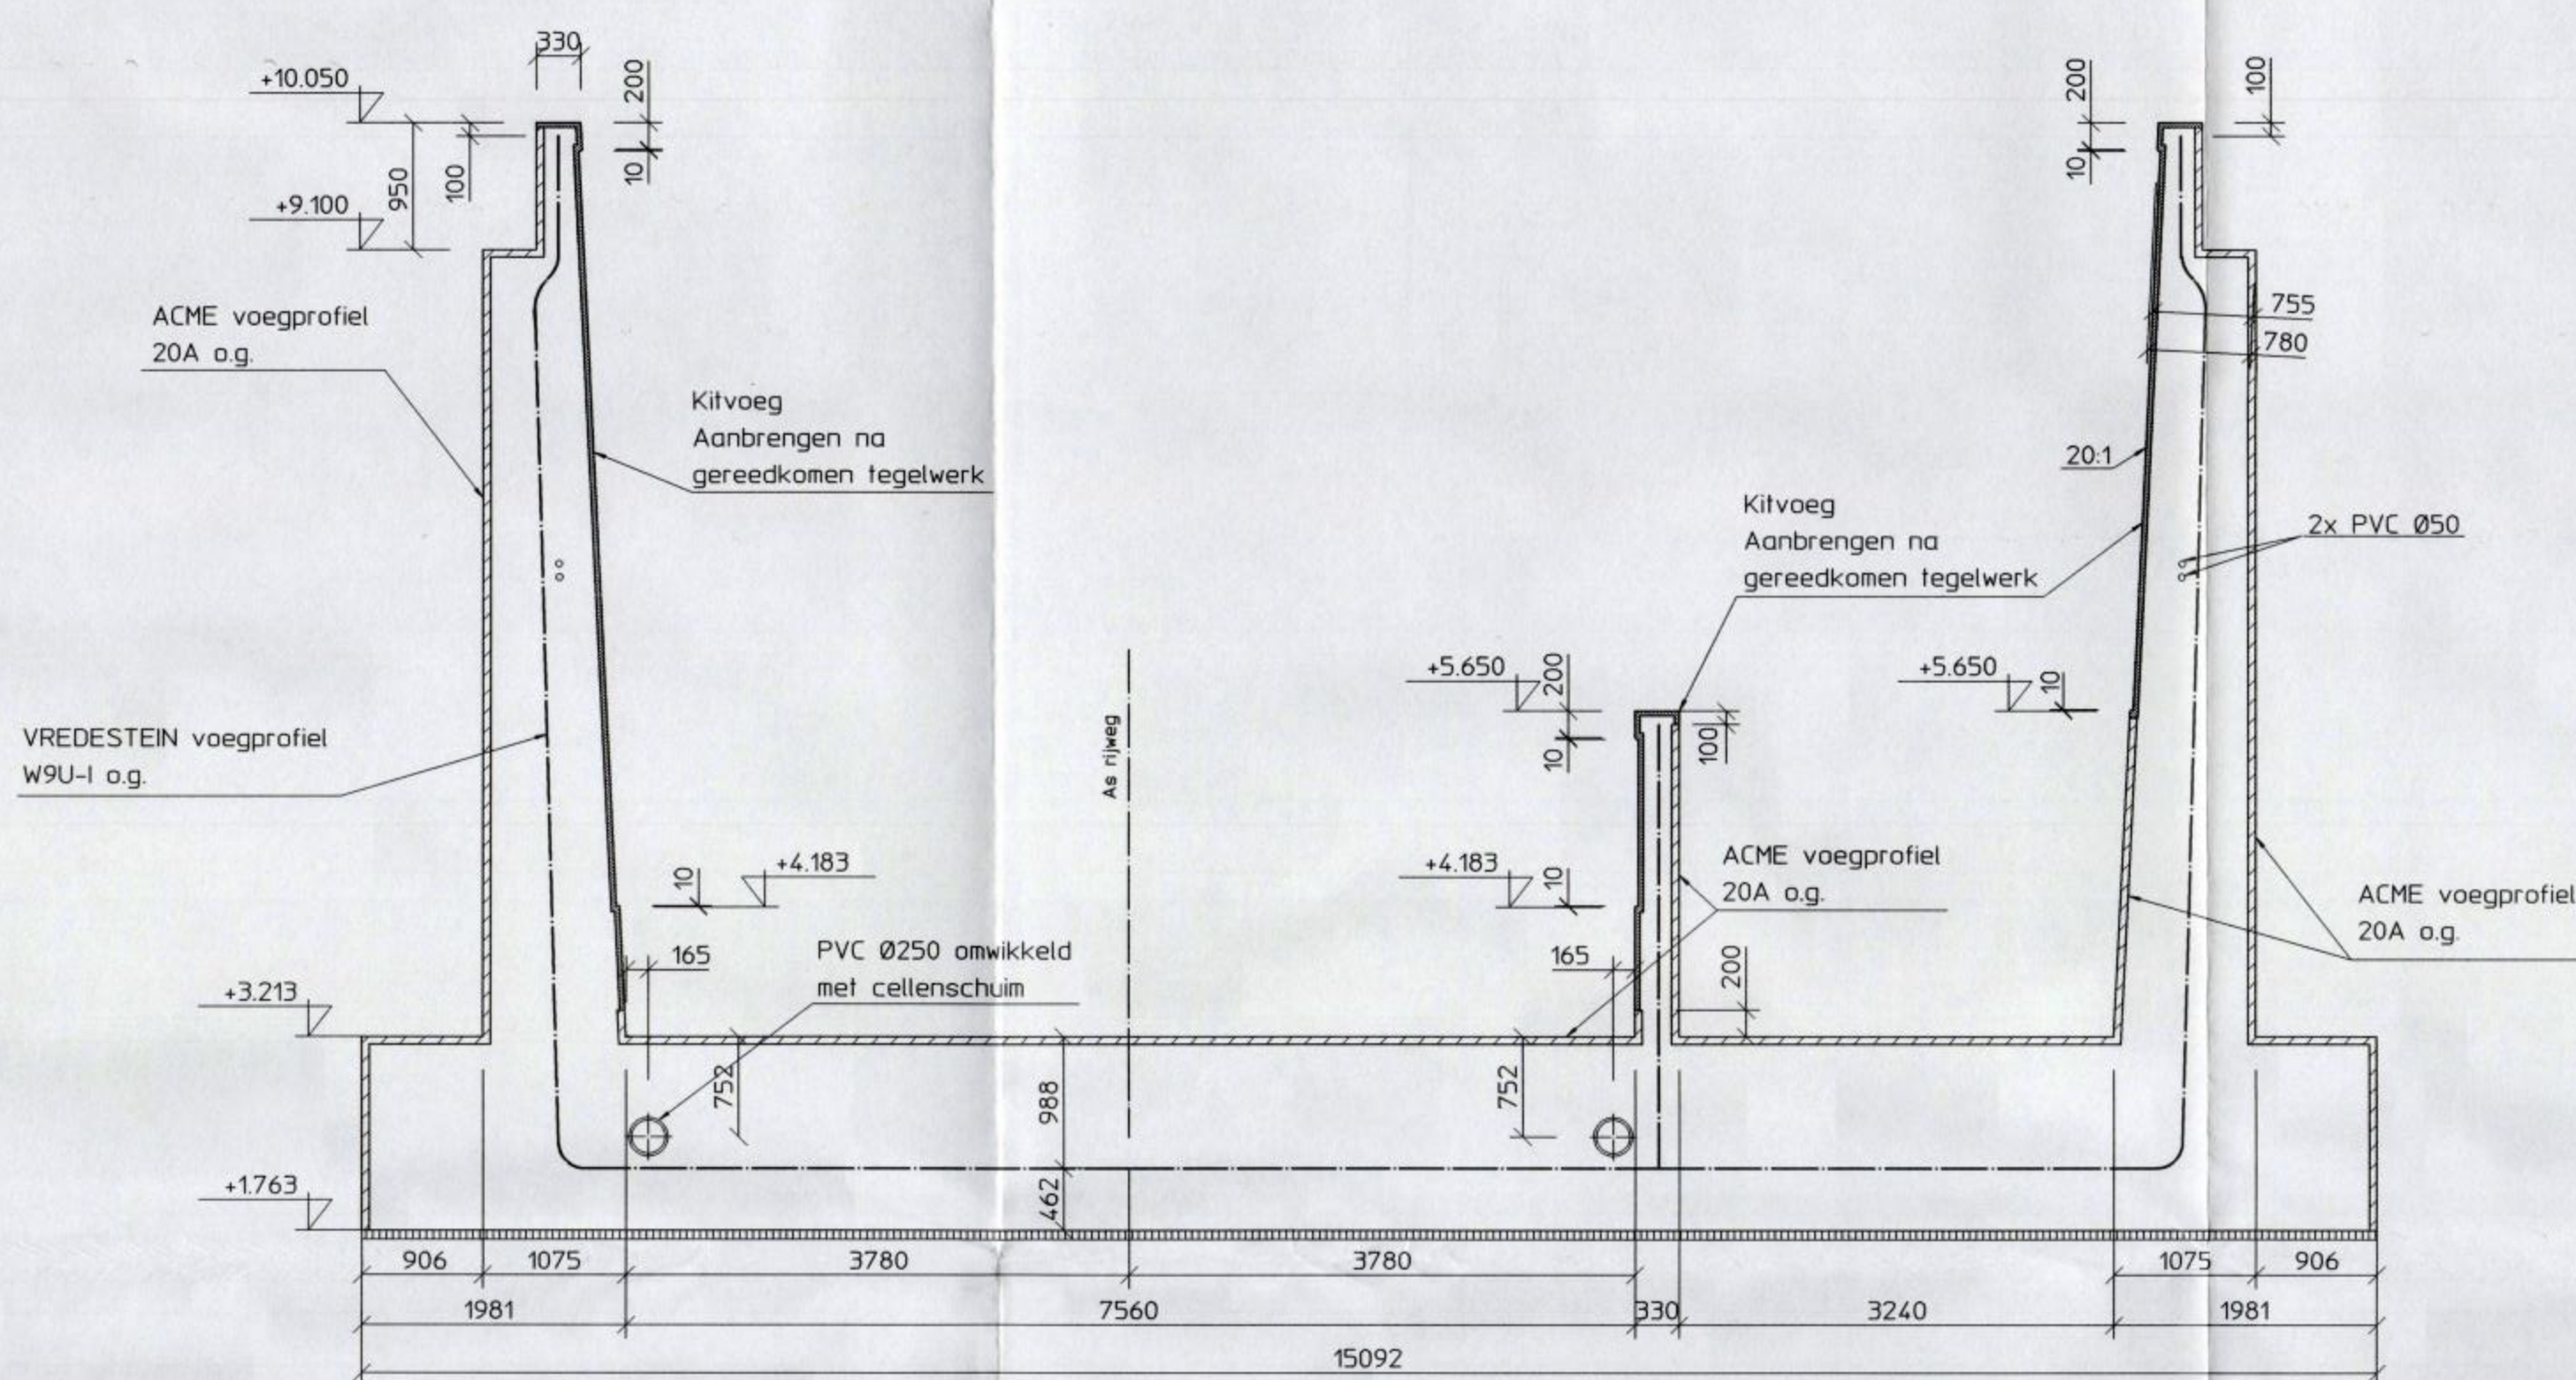


Aanzicht F

Schaal 150

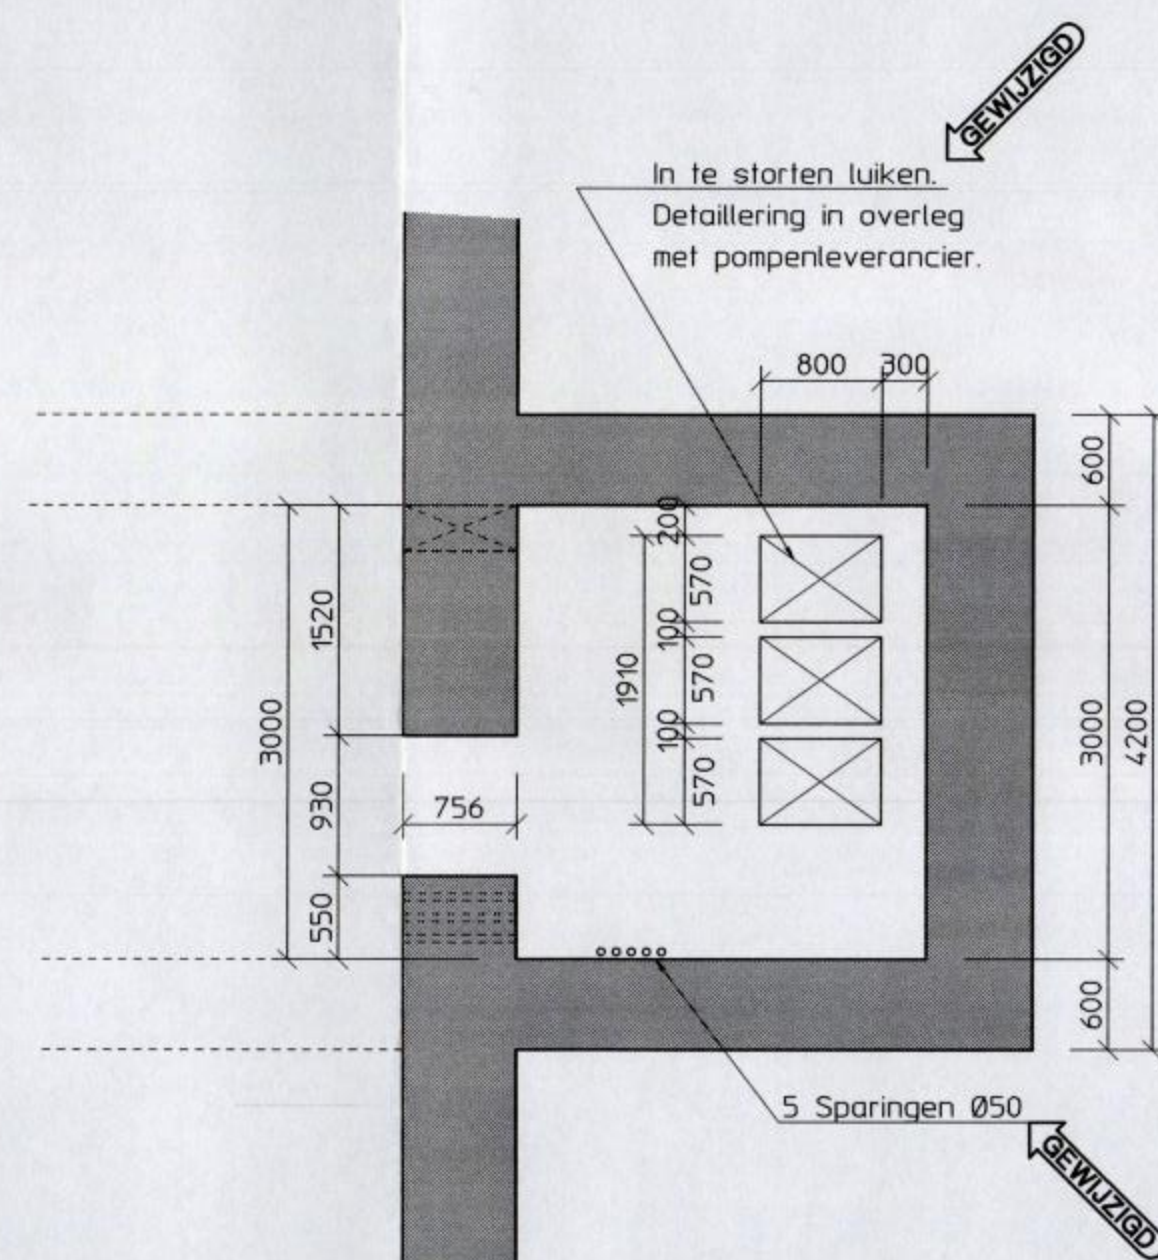


Doorsnede H

Schaal 150

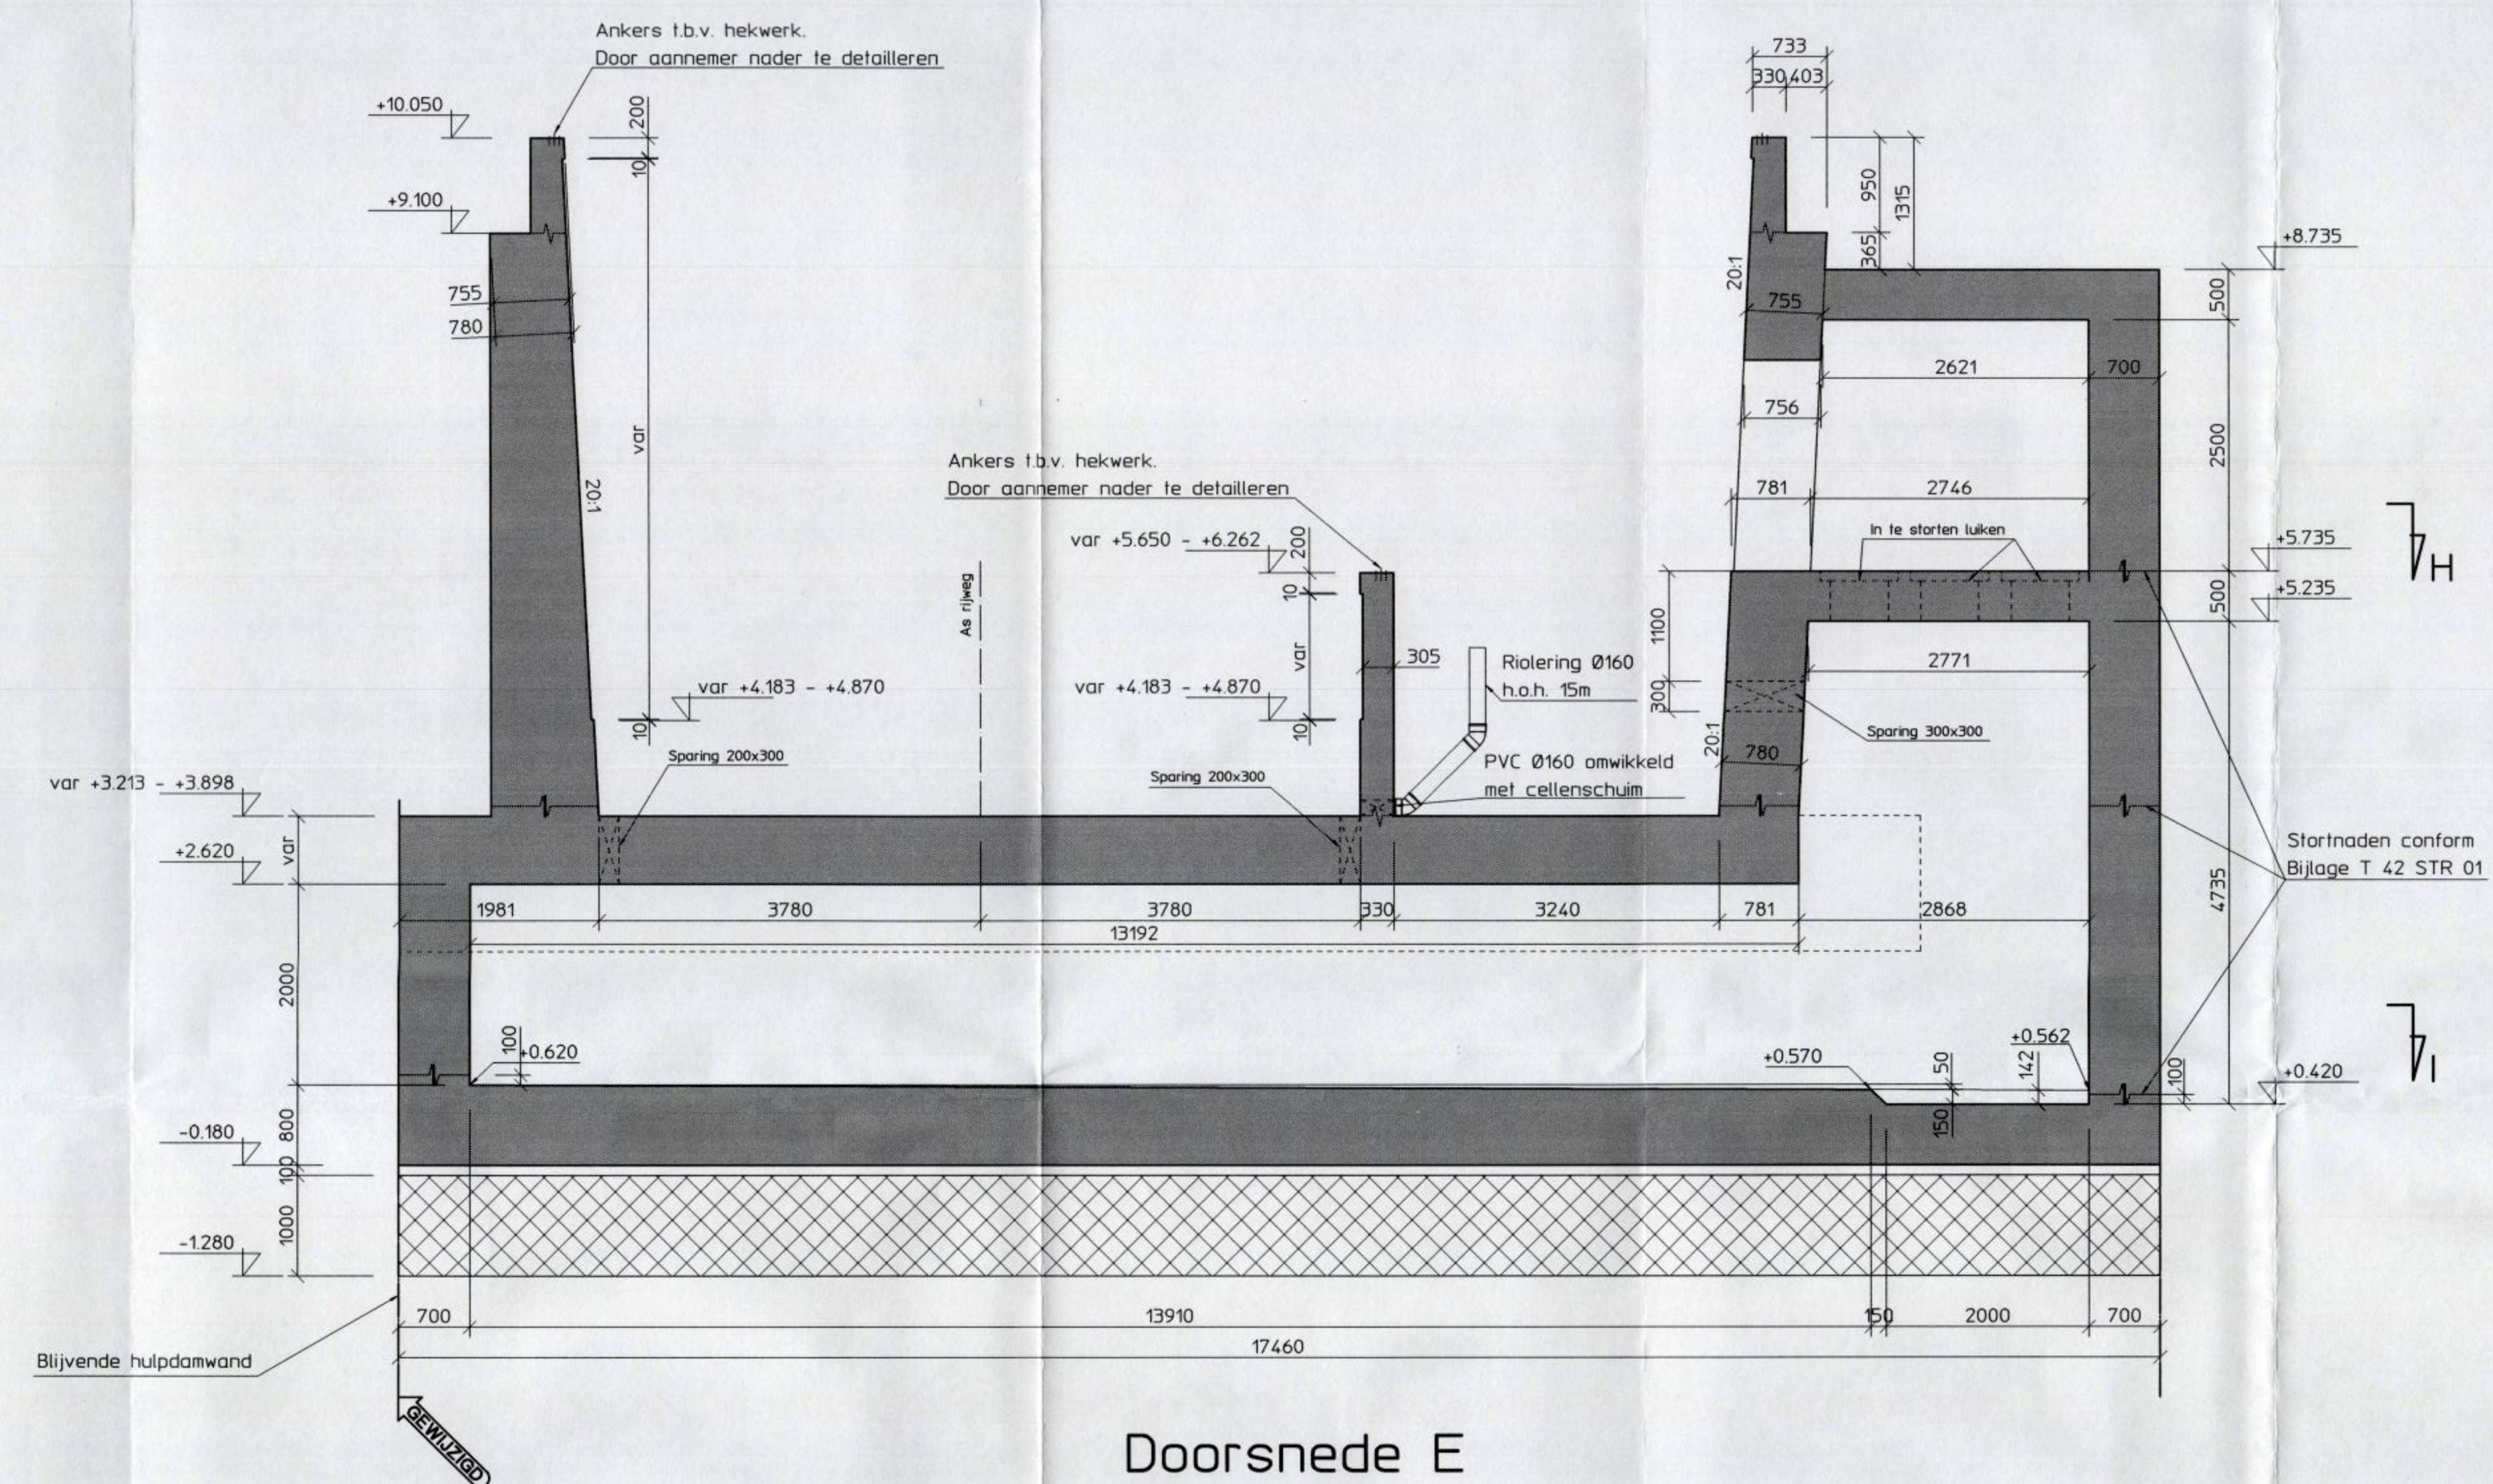


Doorsnede E

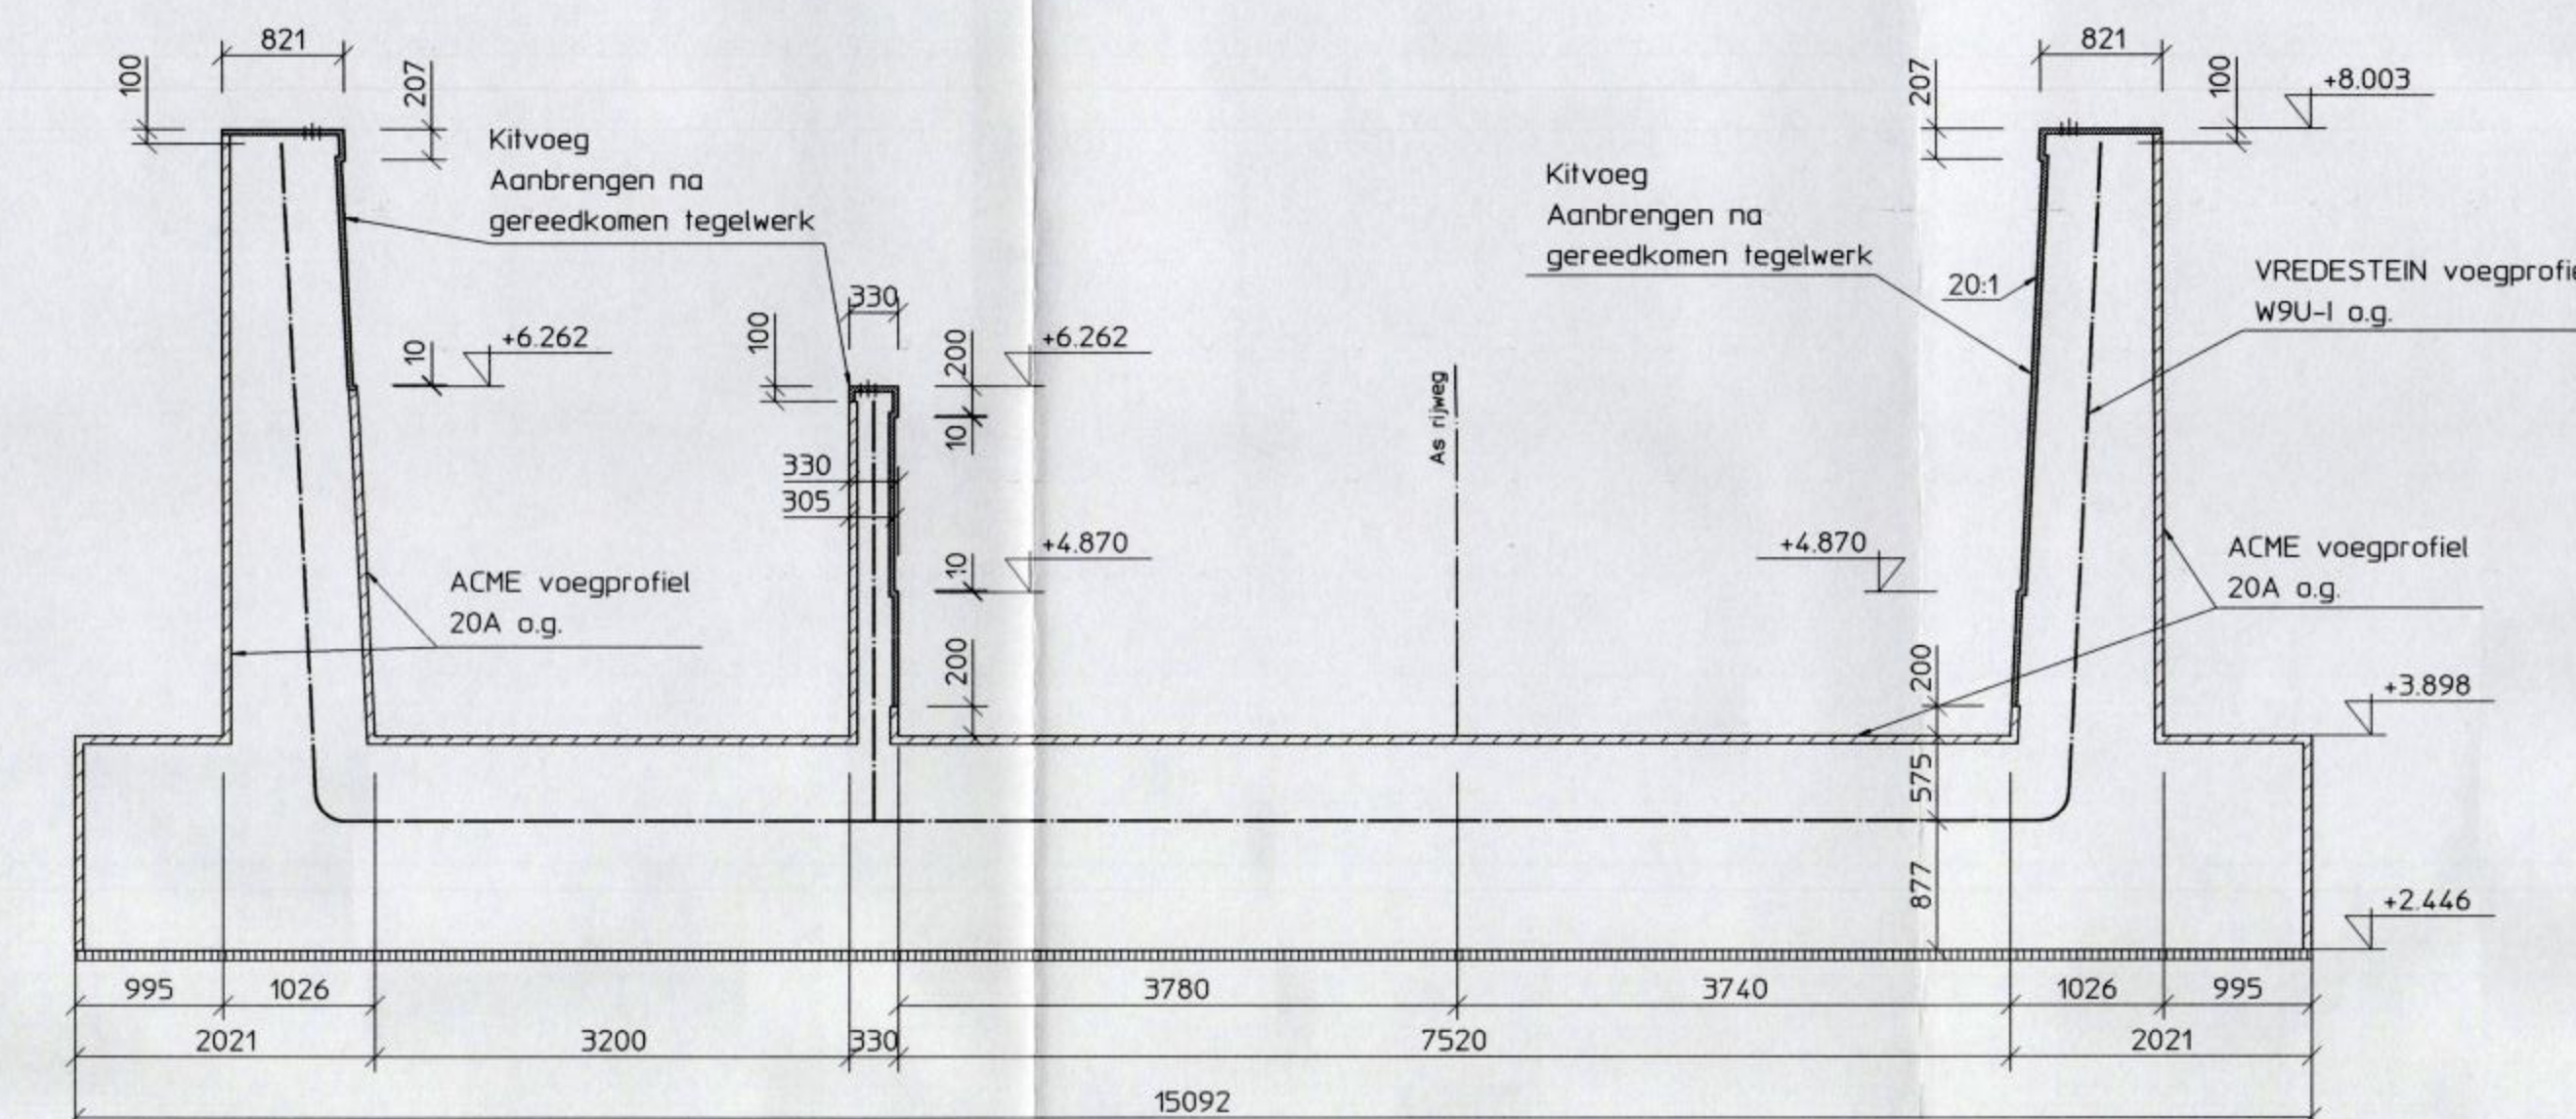

Aanzicht G

Schaal 150

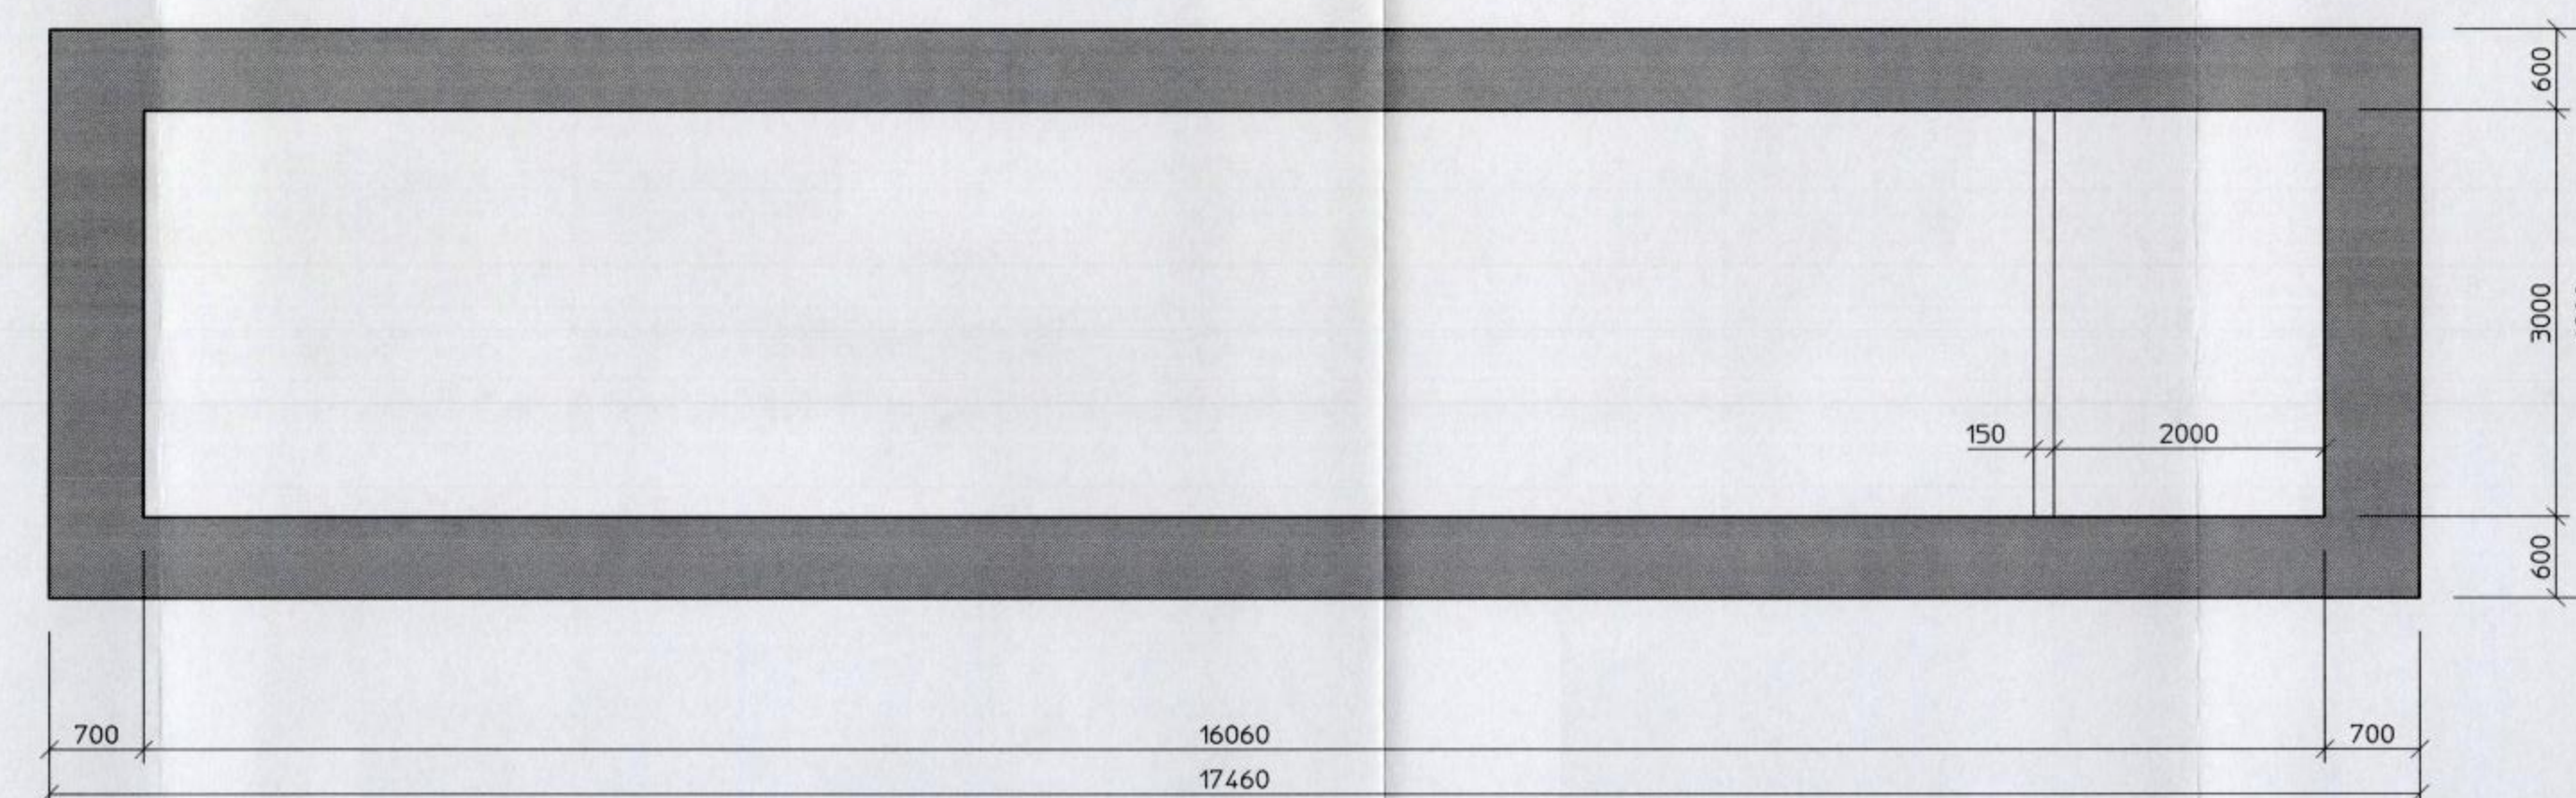

Doorsnede I

Schaal 150

- maatvoering in mm
- hoogtemaatvoering in m t.o.v. NAP.
- voor bovenaanzicht en dooraneden A, B en C zie blad 3362706 40 M
(Status: REVISIE d.d. 17-12-1999 14:37:40)

naam	par	datum	Maatvoering maat 4
getekend	H.W. Griffler	17-12-99	Blad 2
gecheckt	P. de Boeck		
projectnr	CF - Verk		
projectnr	3362706	versie	10
bestelnr	V02B09450	drin H pomp	
formaat	A0	luiken aangepast	
schaal	150	veroren datwand	
VA CT	PG 82		
H.W. Griffler	3500 GW Utrecht		
Telefoon	030 - 235 89 58		
Telefax	030 - 235 72 29		
datainfo	/na0_0wg/ct/ict23/kno011720/pa3362706/act14/1.m		

Holland Railconsult