



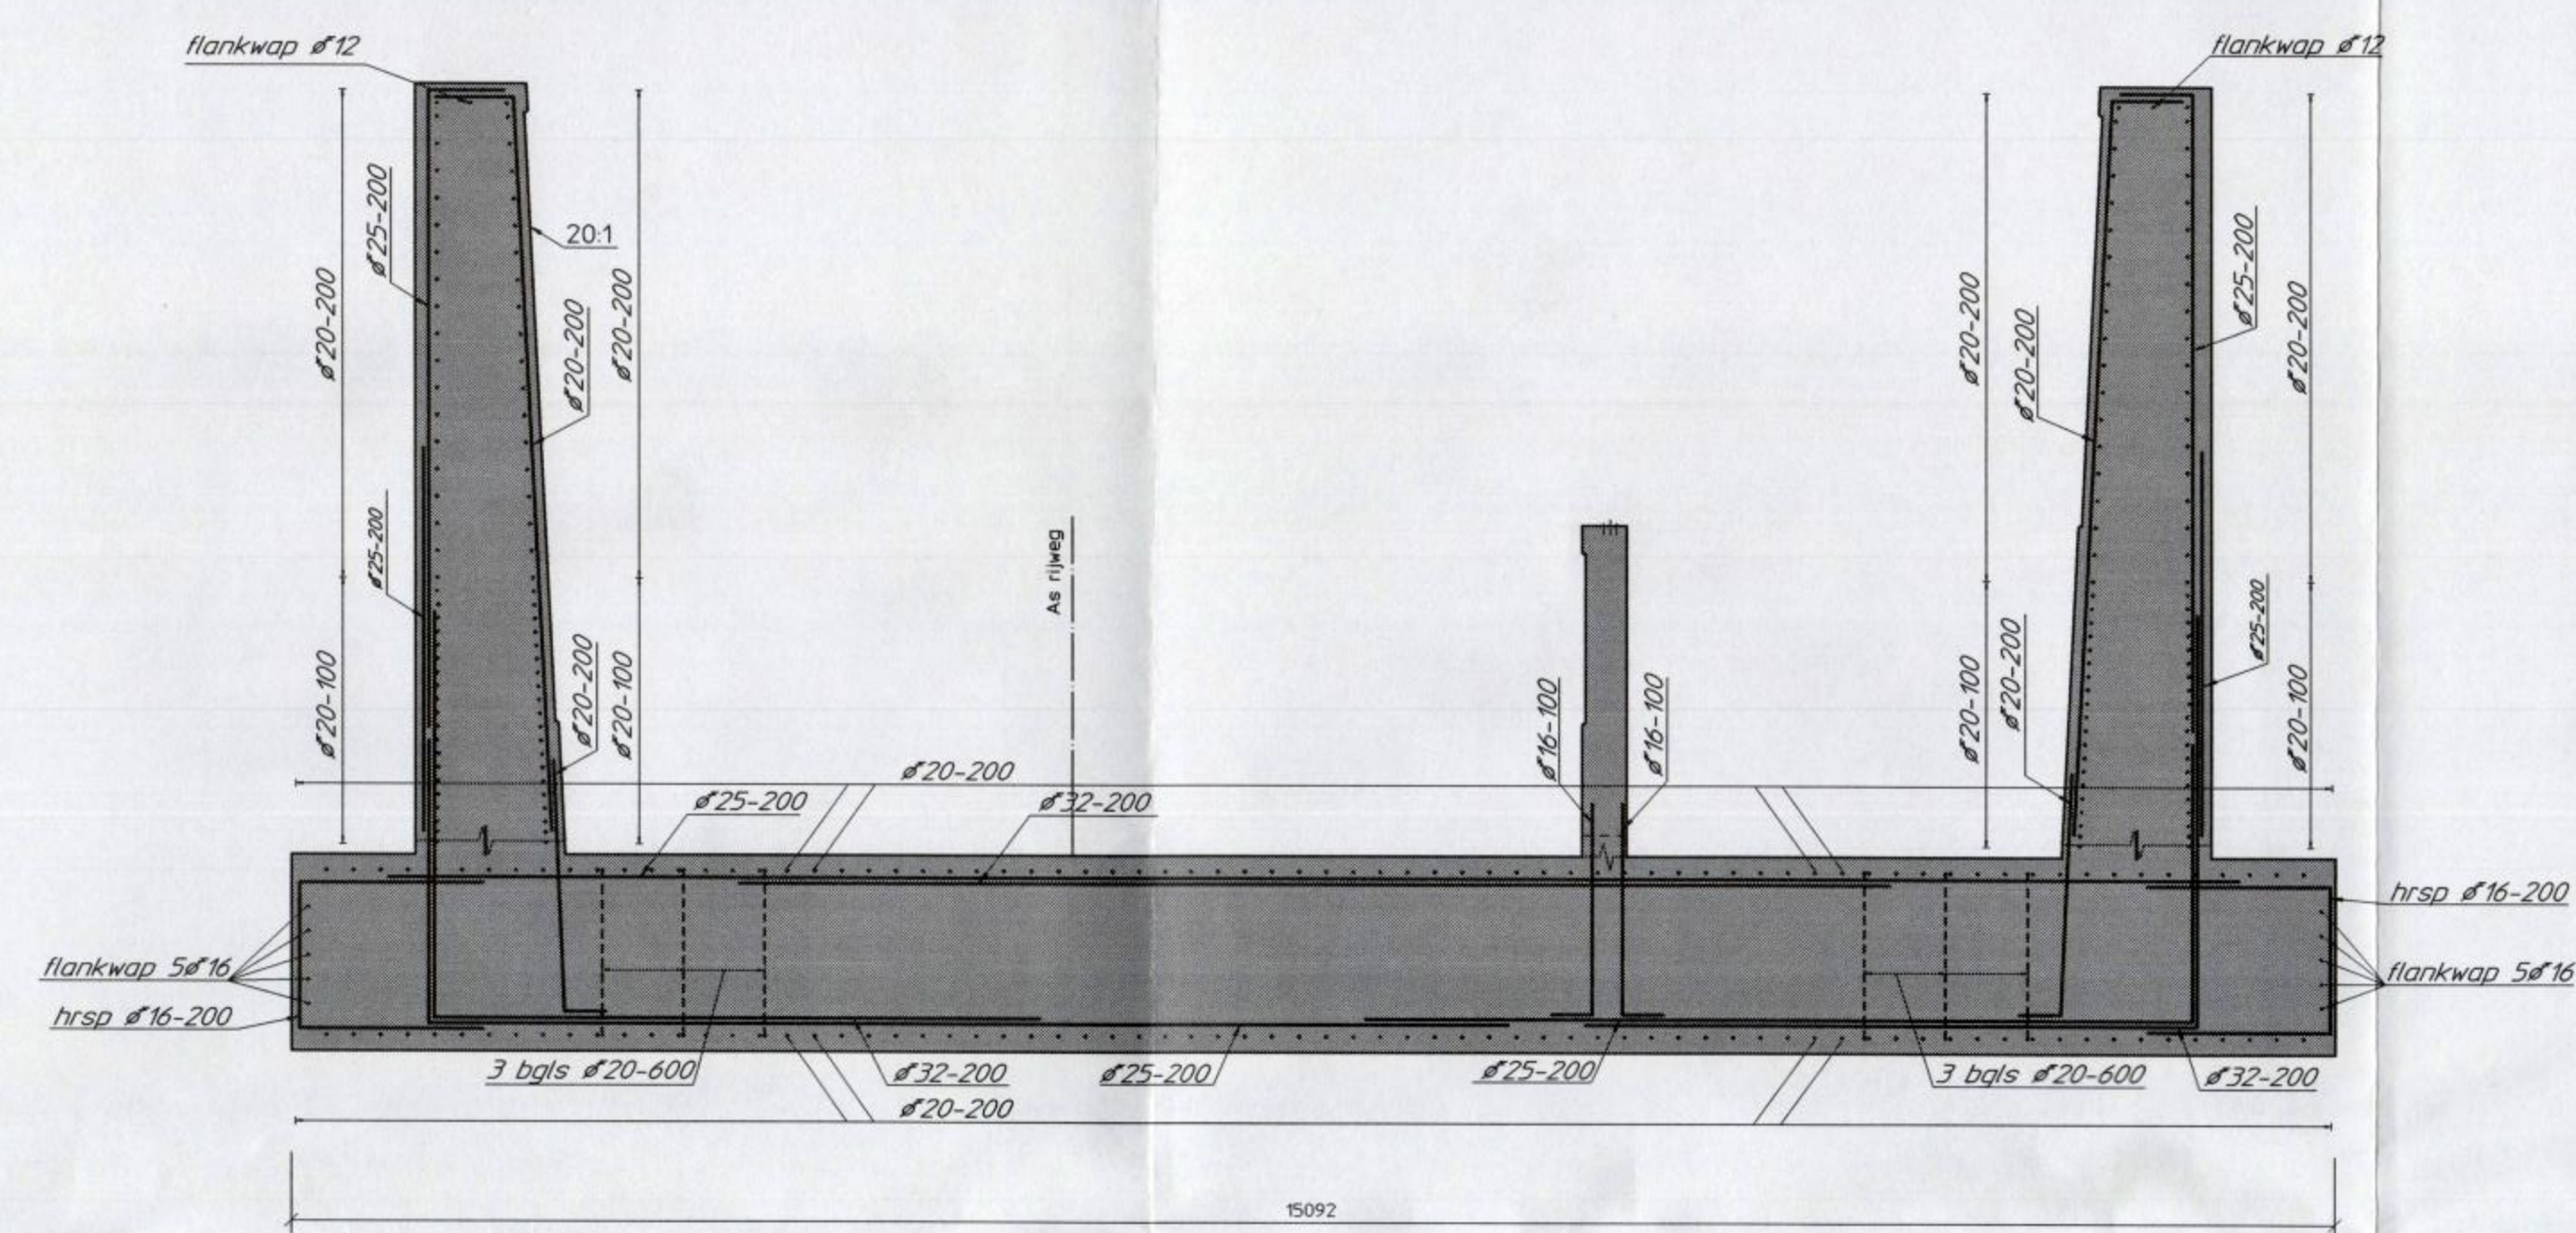


Doorsnede E-E

Schaal 150

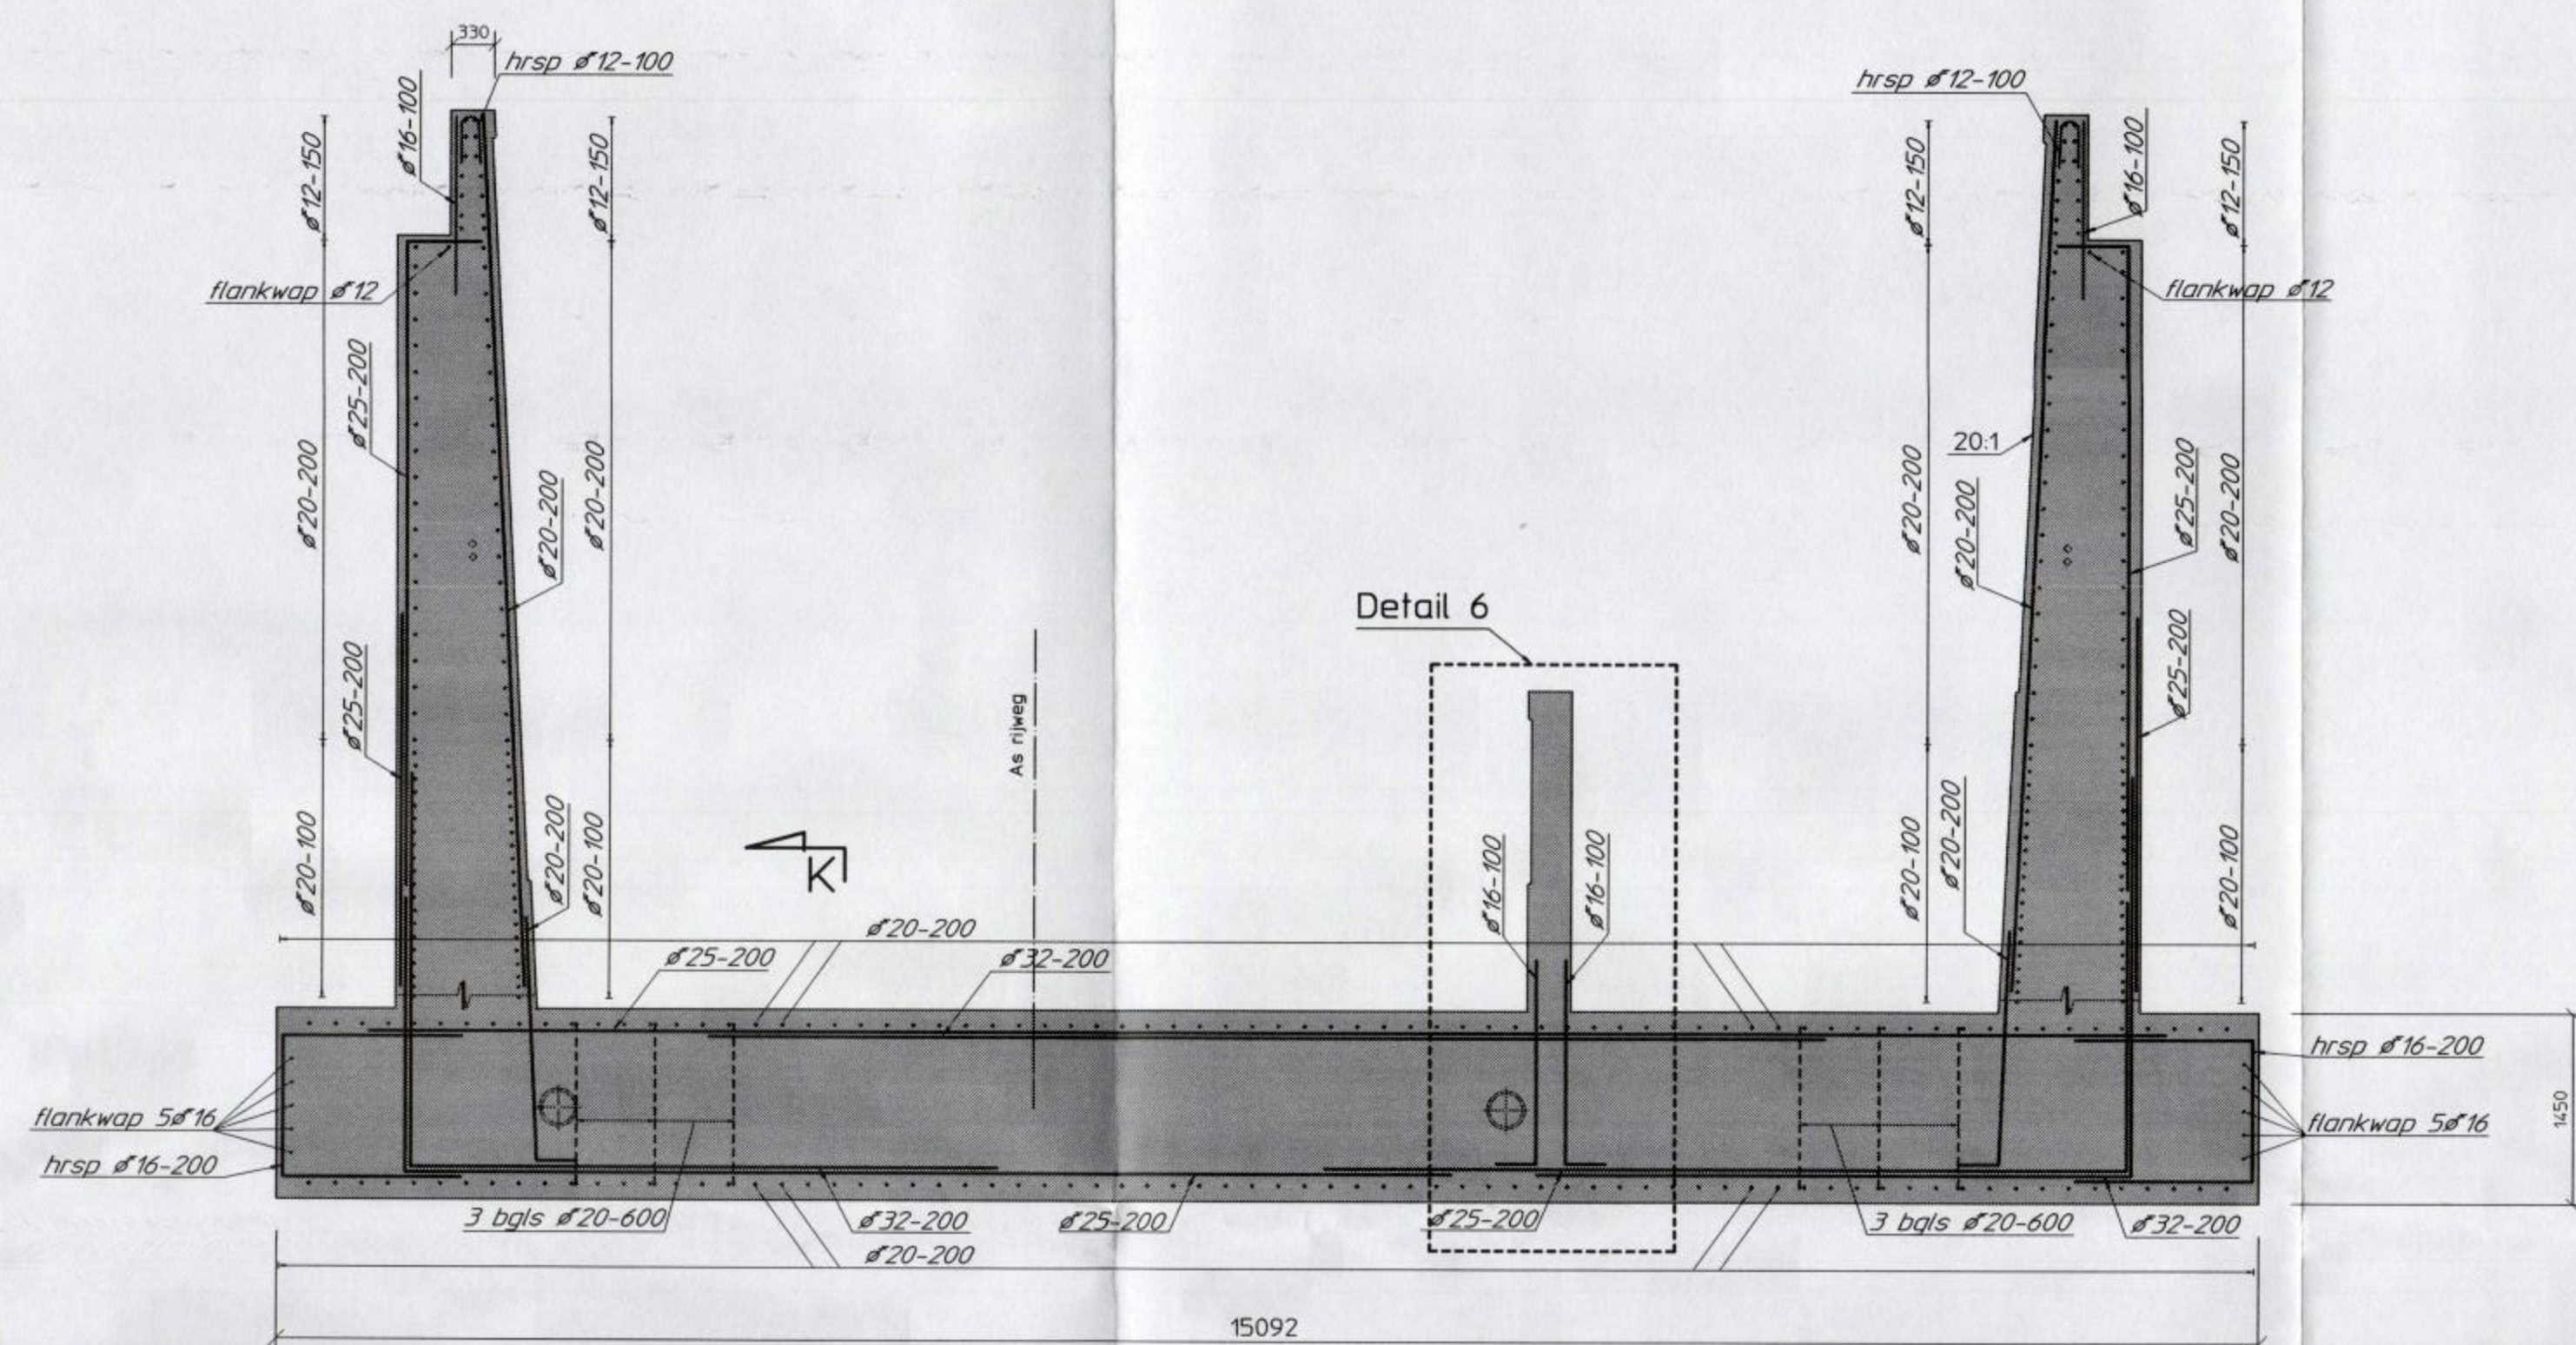

Doorsnede F-F


Schaal 150

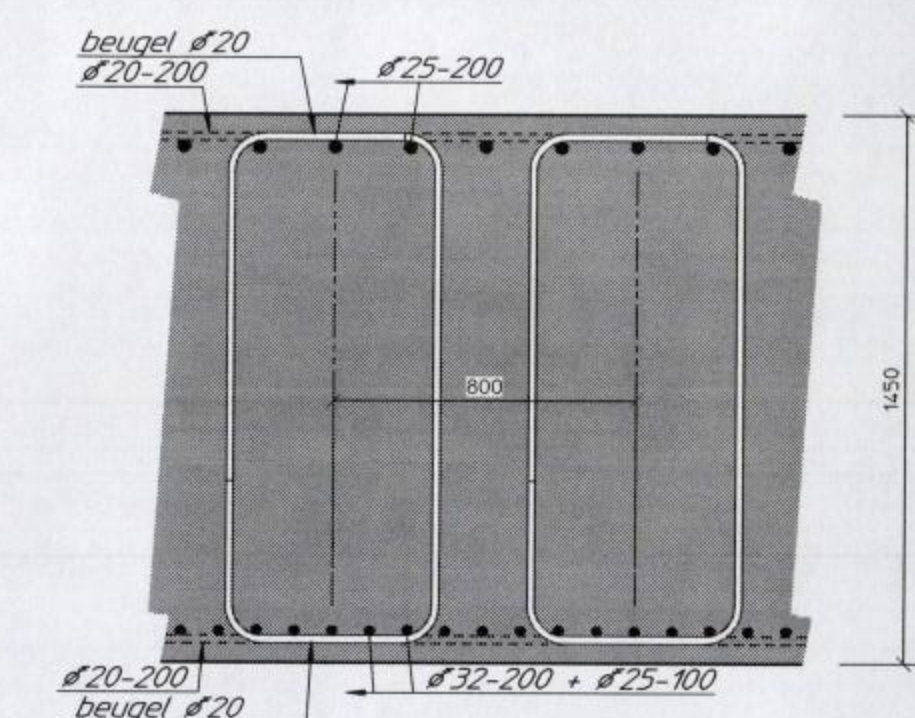

Doorsnede K-K


Schaal 120

Beugels in vloer

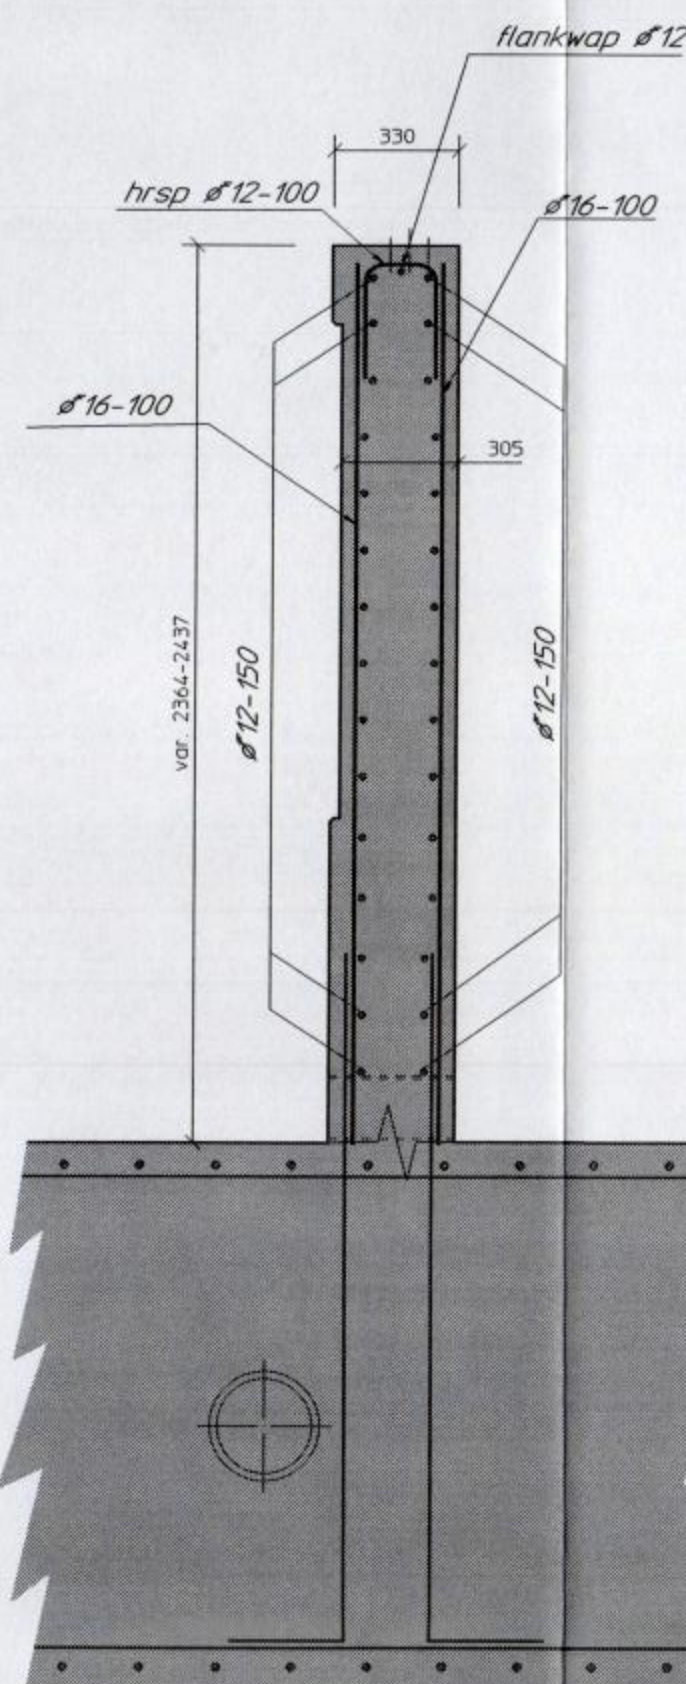


Detail 6

Schaal 120

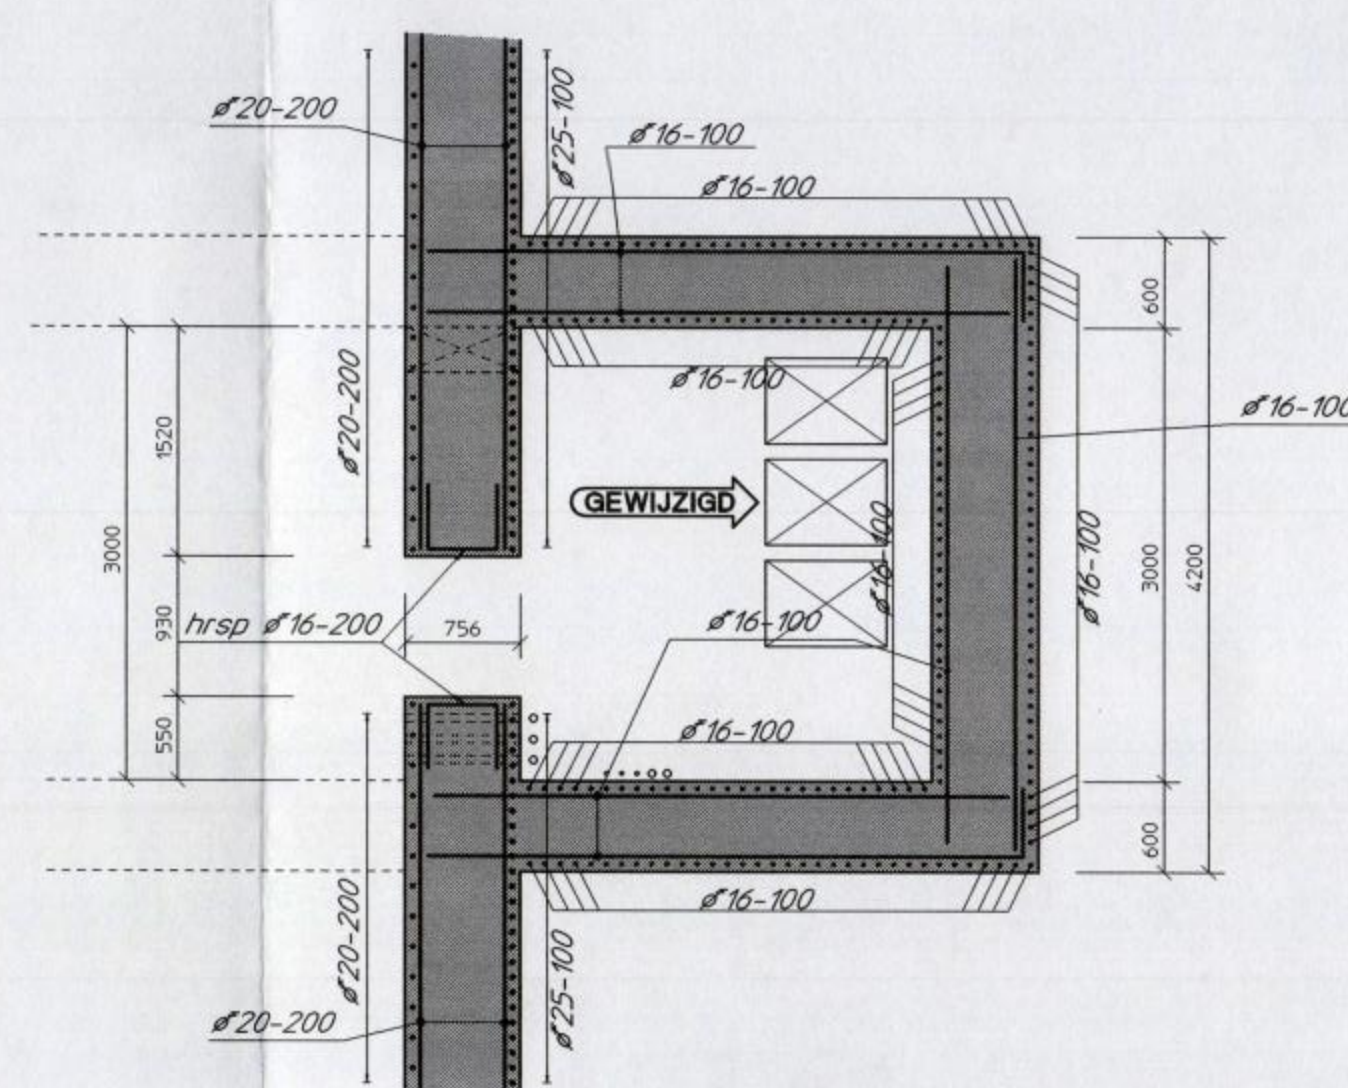


Doorsnede H-H

Schaal 150

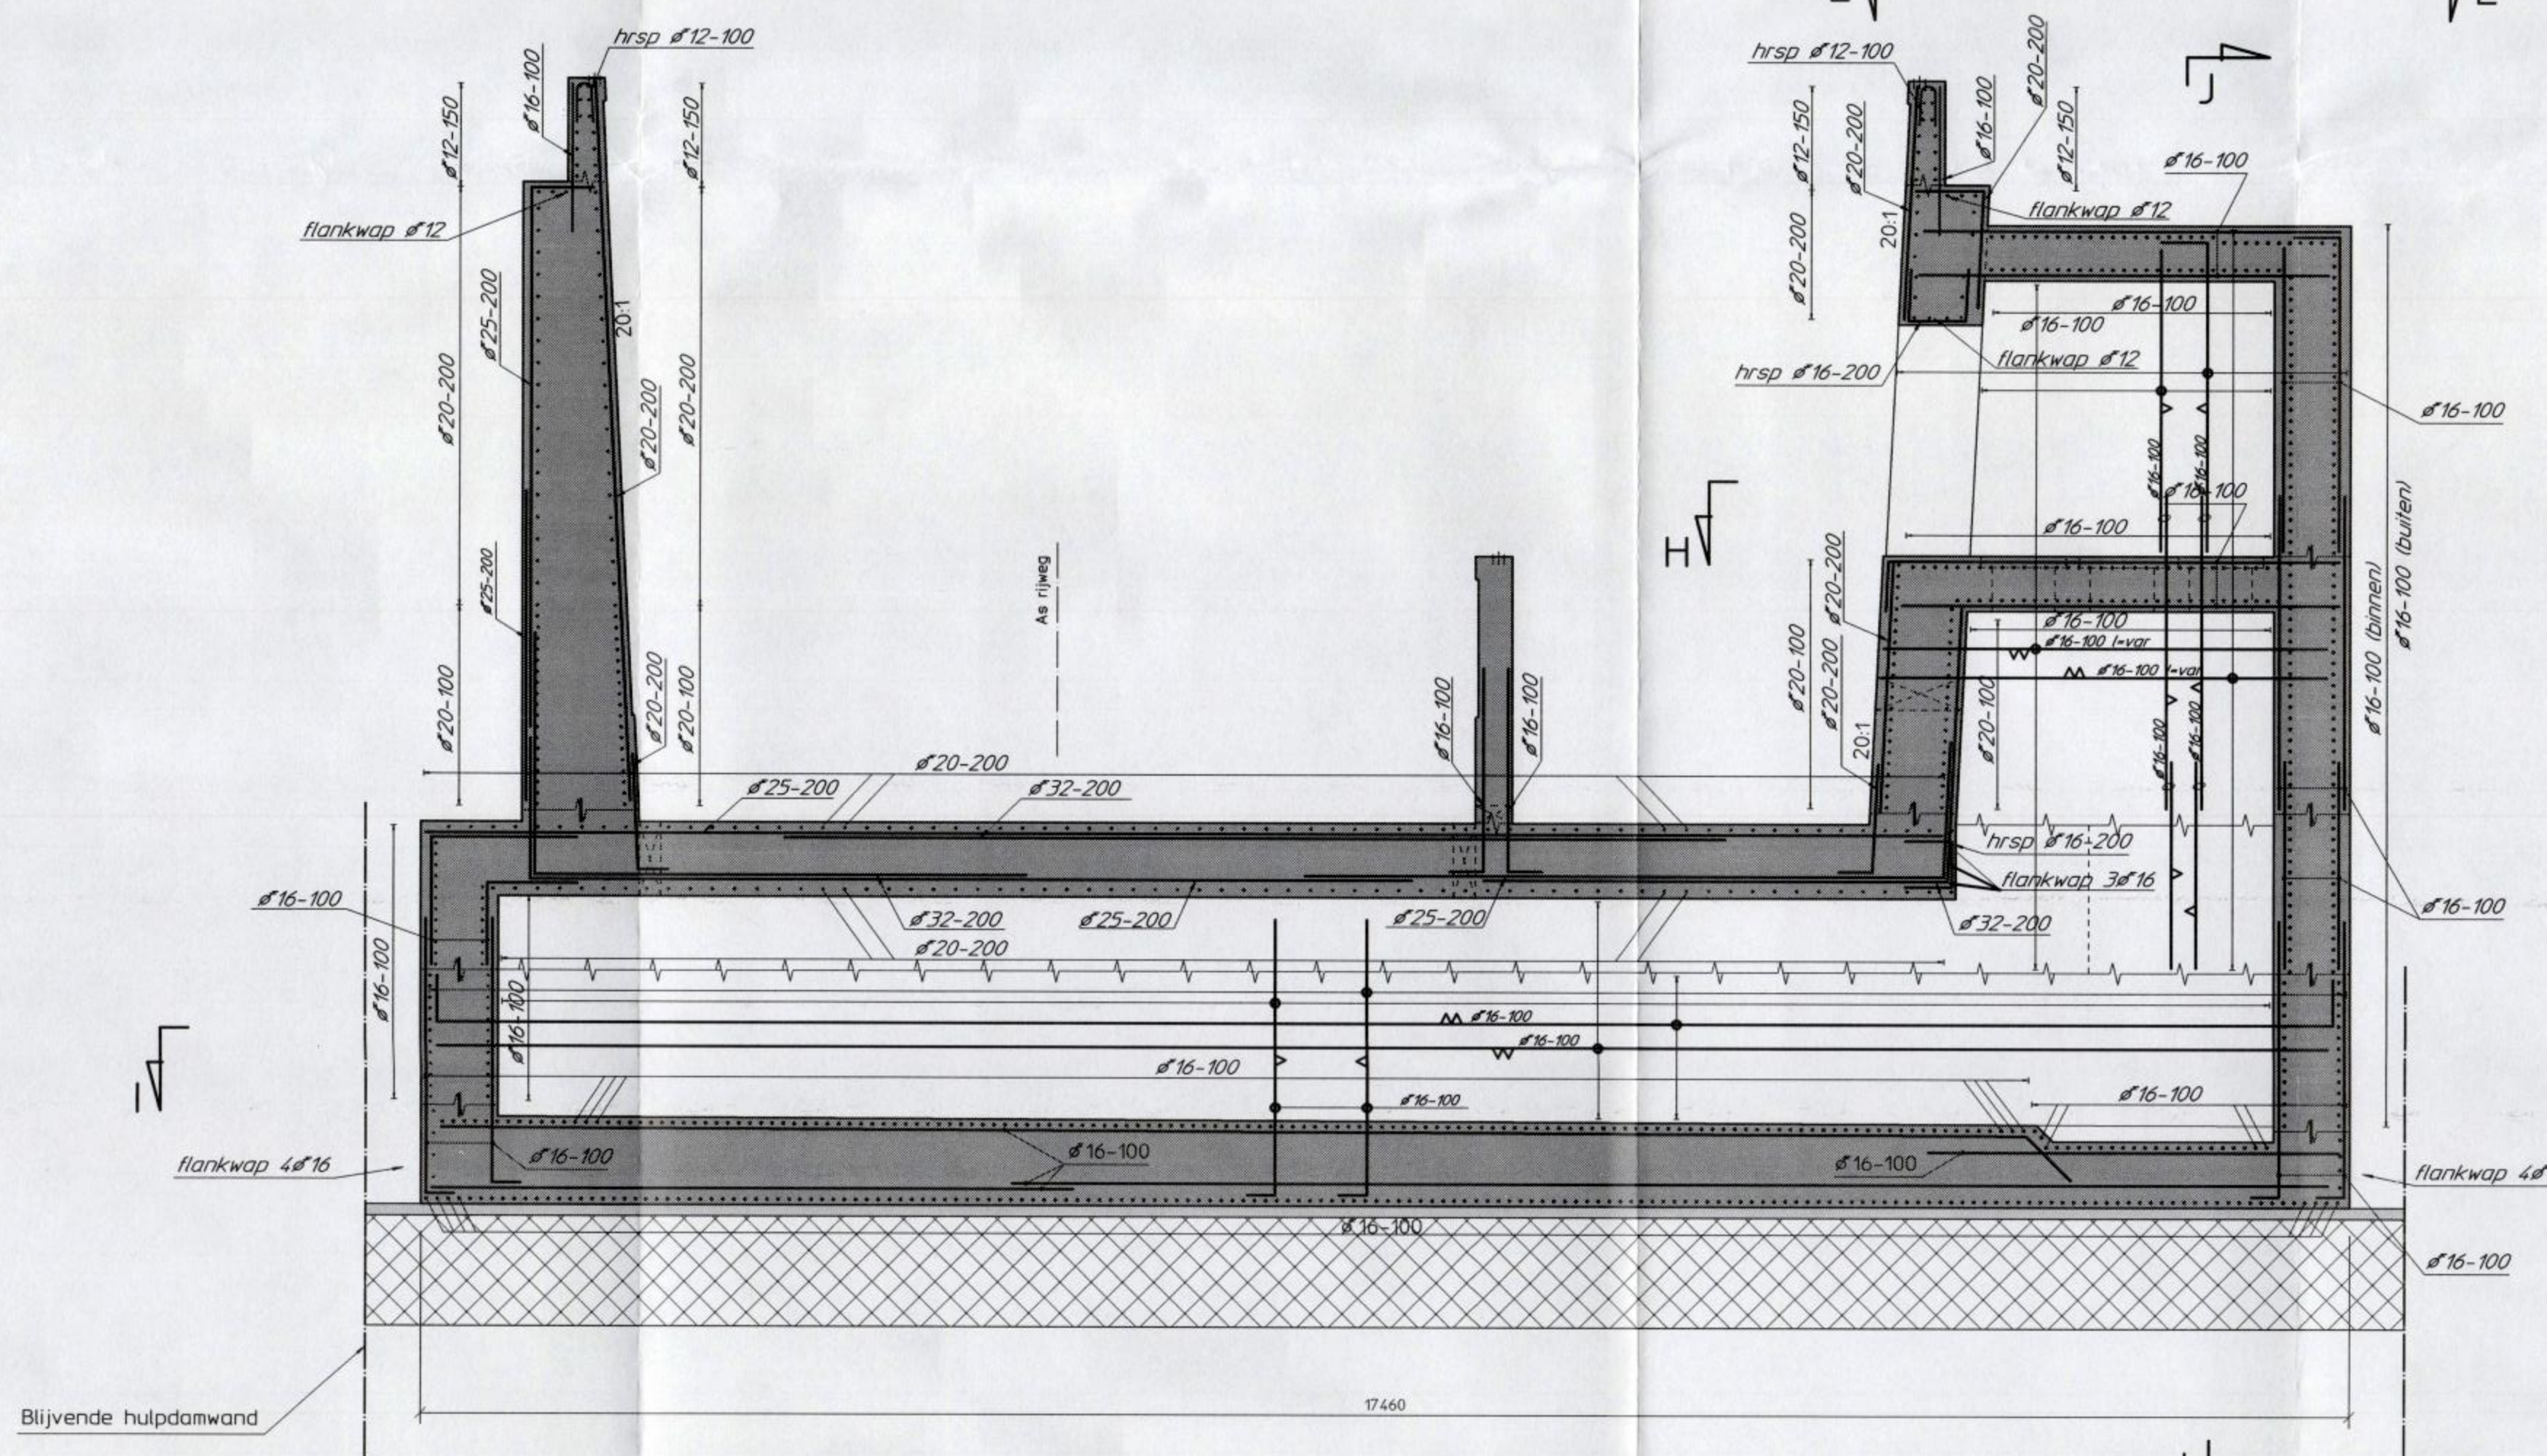

Doorsnede G-G

Schaal 150

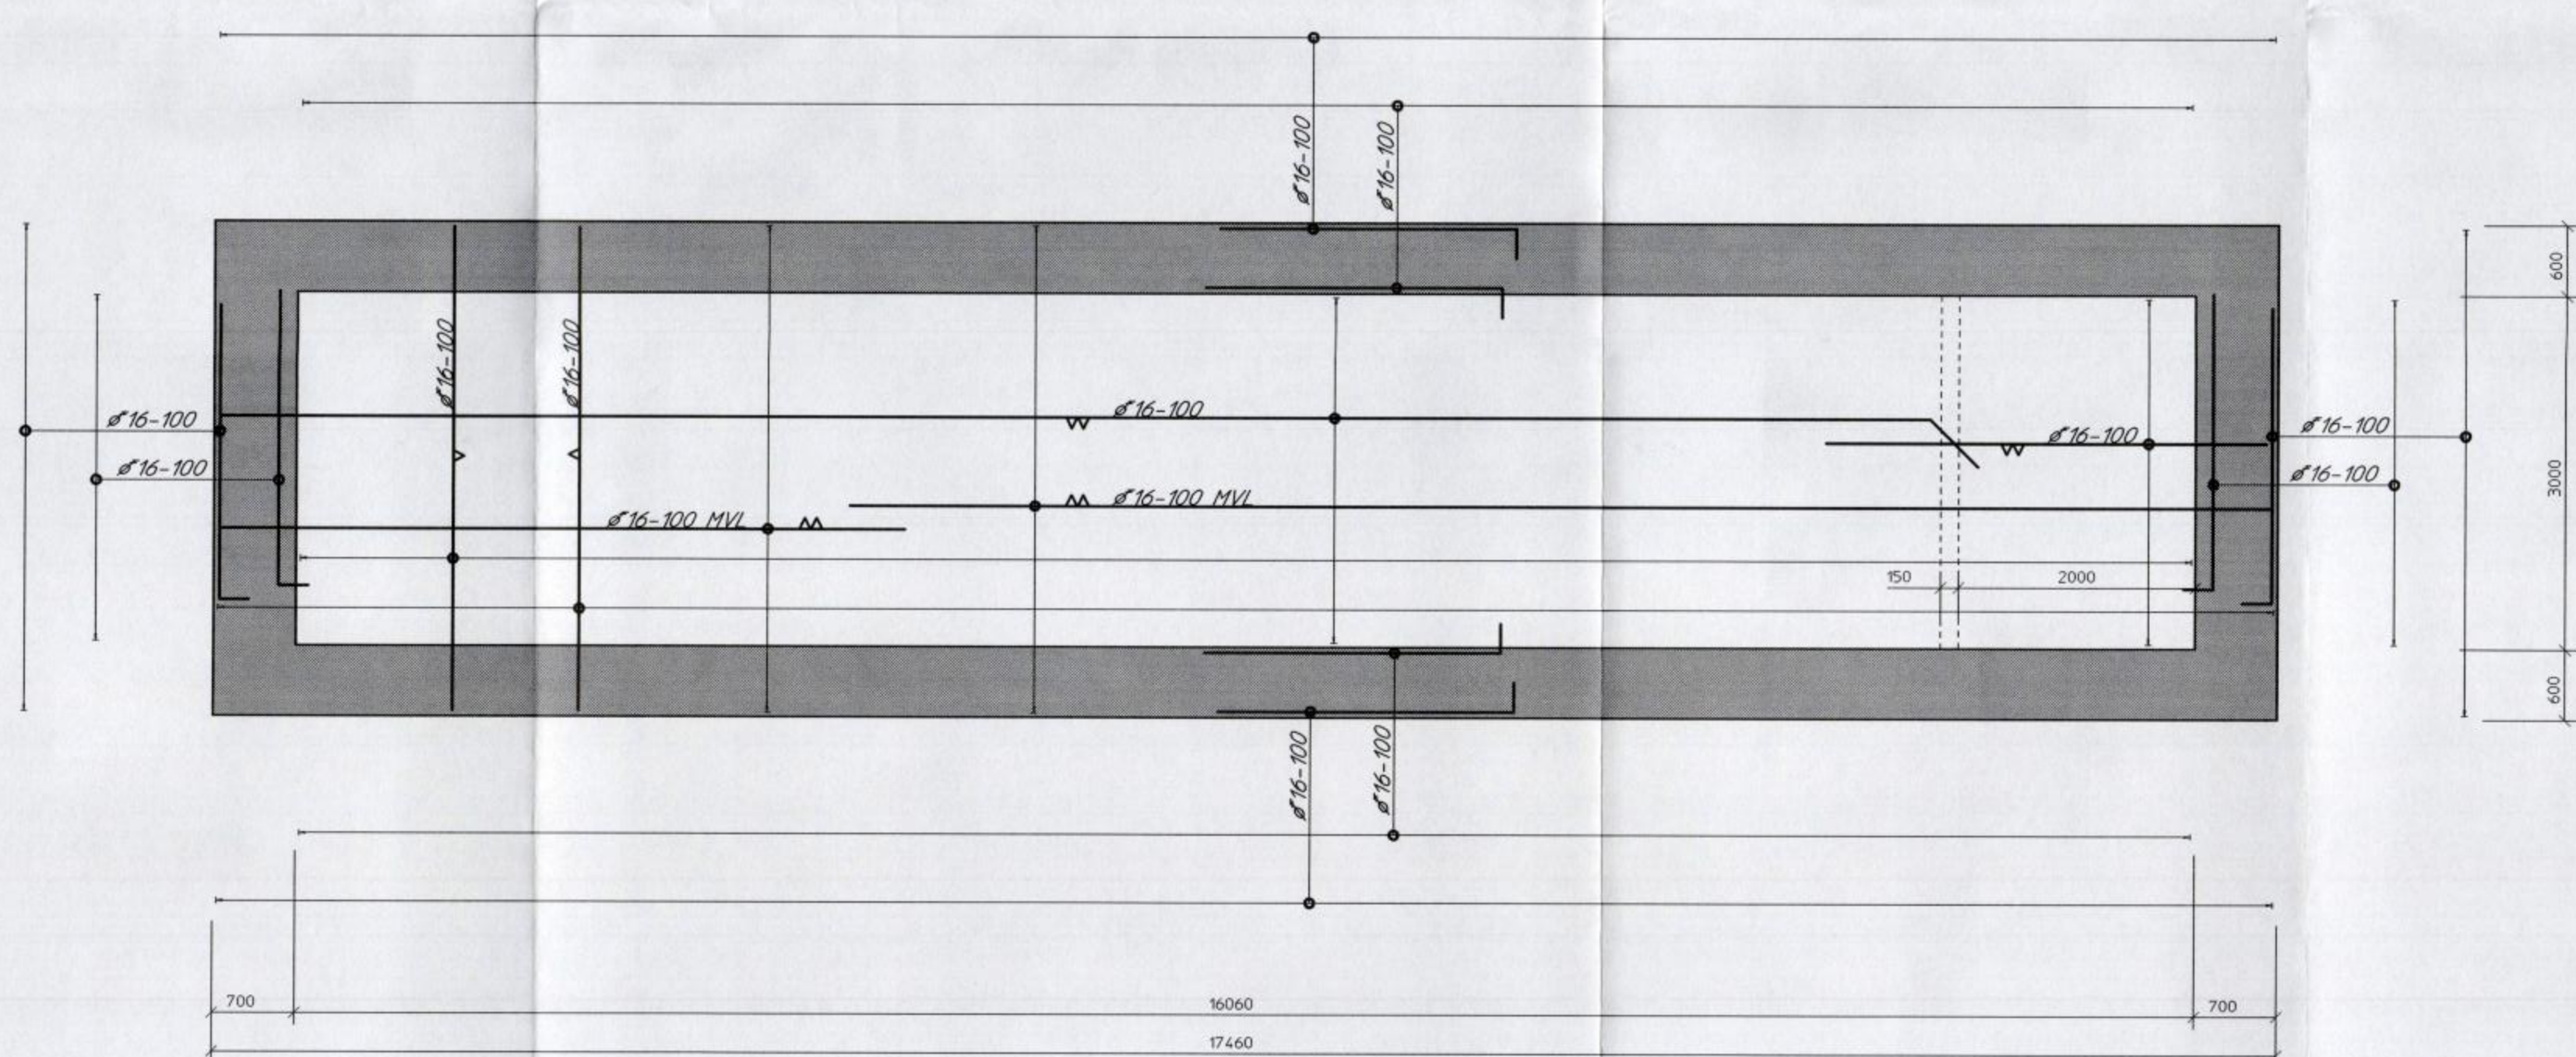


Doorsnede I-I

Schaal 150

Wapening pompkelder vloer


Aanzicht L-L

Schaal 150

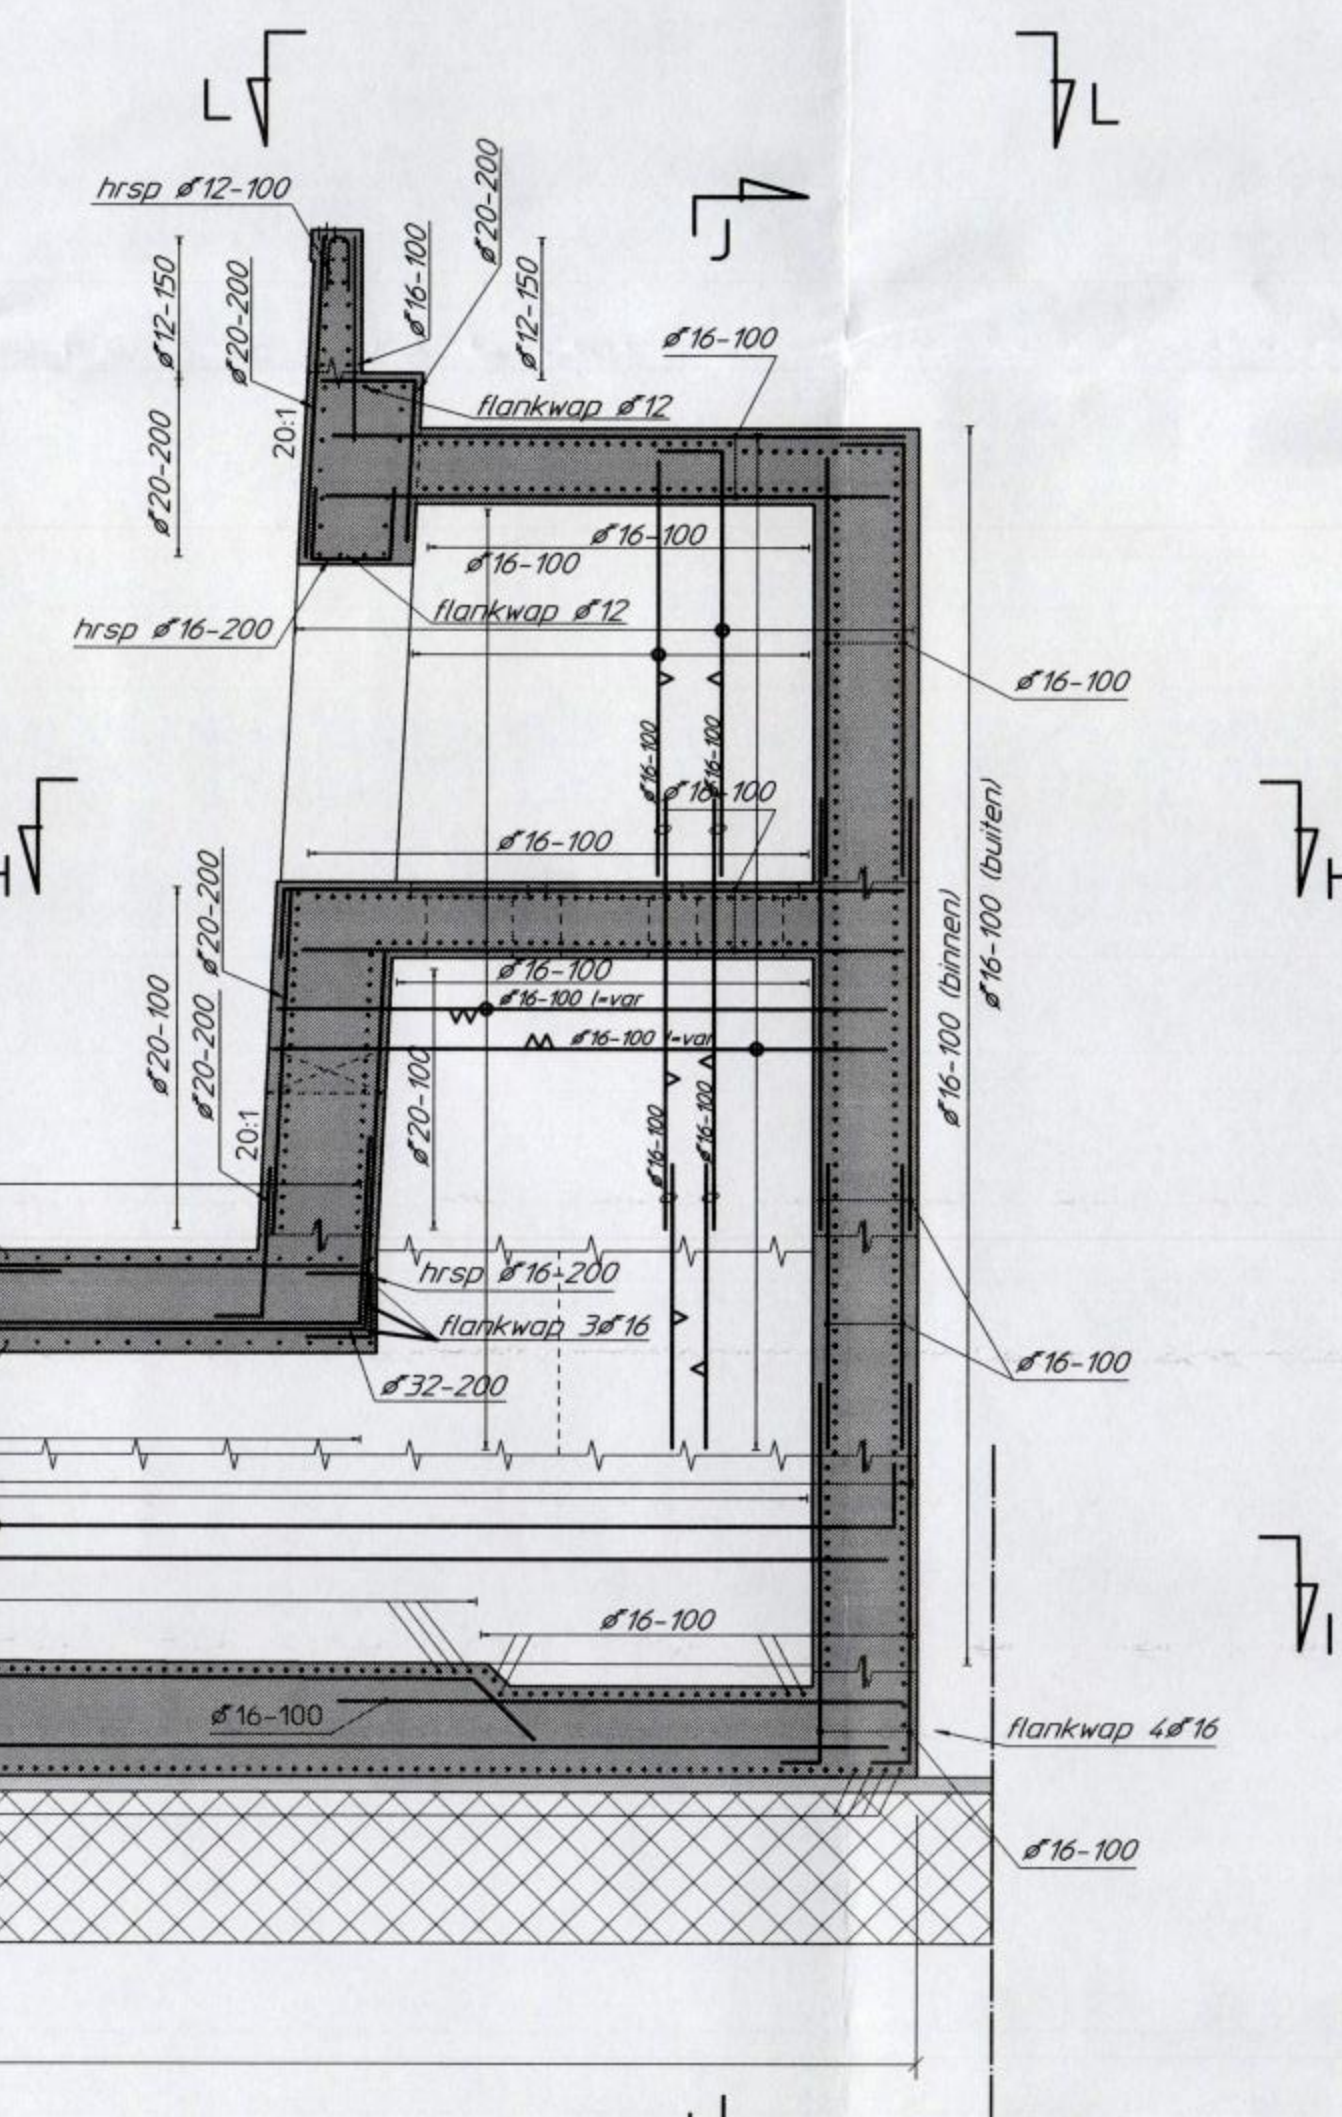

Doorsnede J-J

Schaal 150

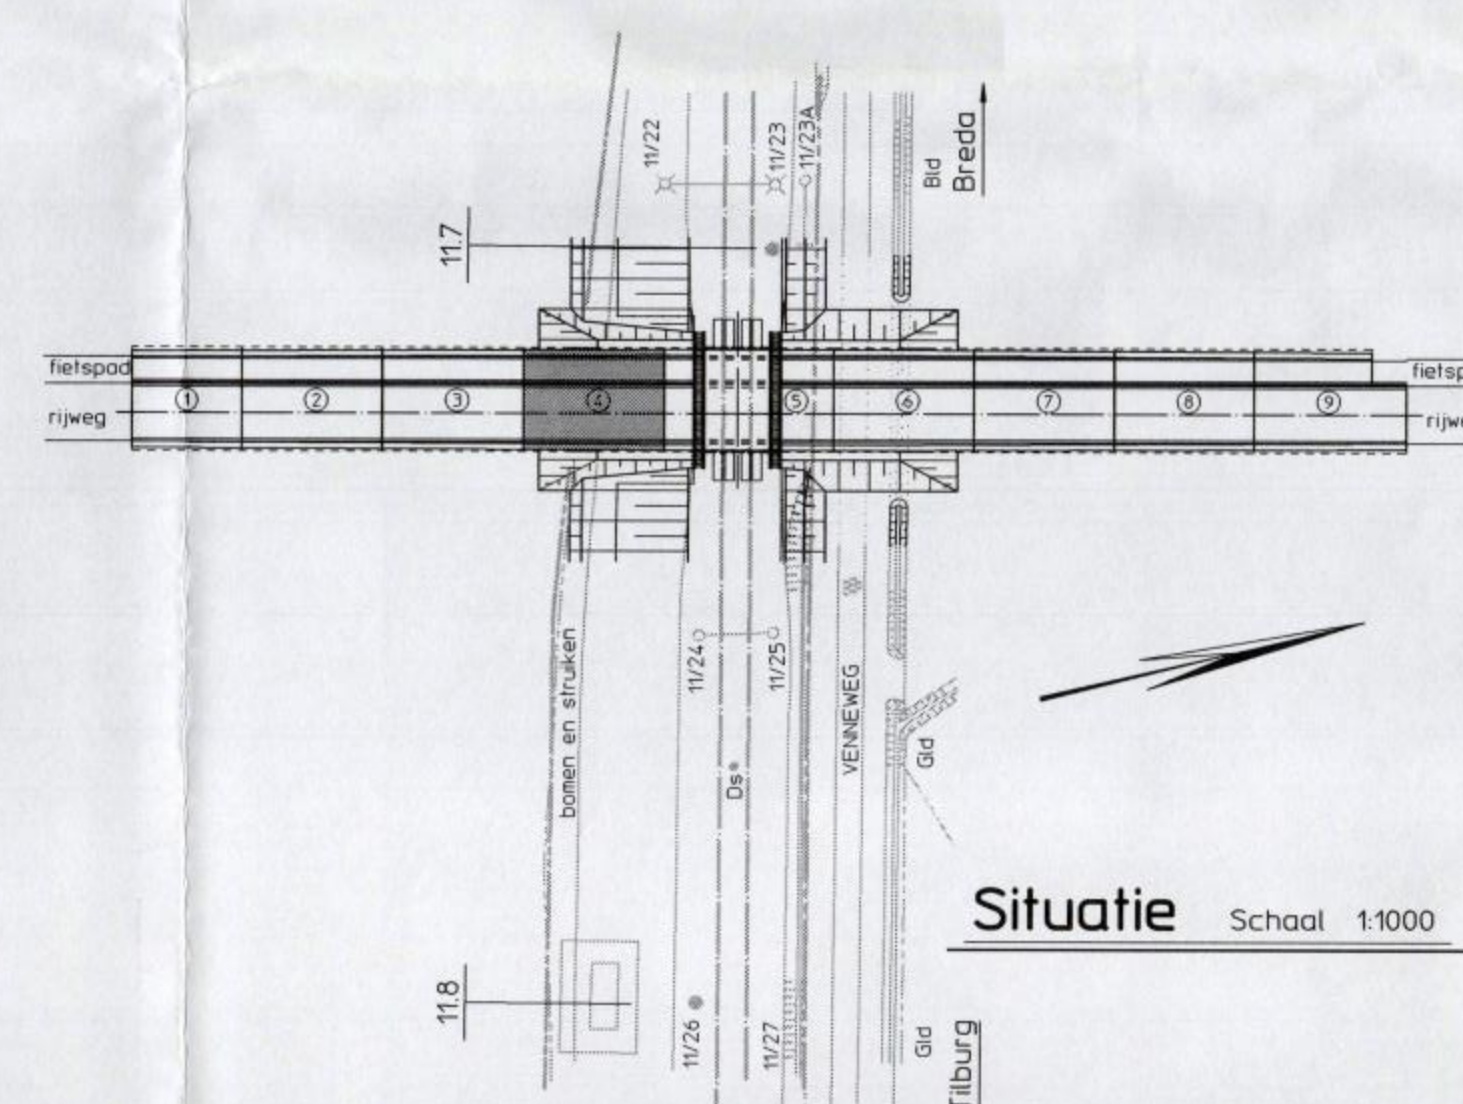

Situatie

Schaal 1:1000

Legenda

- maatvoering in mm
- hoogtemaatvoering in m t.o.v. N.A.P.
- voor overige doorsneden zie blad 3362706 40 W
- voor maatvoering zie tek. 3362706 40 M & 41 M
- MVL = met verspringende las
- var. = variabel

Status: REVISIE d.d. 17-12-1999 15:27:59

naam	par.	datum
T. Brong	17-12-99	
P. de Boer		
C.F. Vek		
projectnr.	versie	
3362706	1.0	
bestnr.	VGBR09450	
formaat	A0	
schaal	zie tek.	

Wapening maat 4
Blad 2

NS Railinfrabeheer Regio Zuid
Gilze Rijen
Onderdoorgang Europaalpen

420 123 11.720 713 3362706 41 W

VIA CT 110 82
Postbus 2850
3500 GW Utrecht
Telefoon 030 - 235 89 58
Telefax 030 - 235 72 29
plaatnr. /m10_dugc1/c1/c12/kn11720/pa3362706/ac74/L1_w_revisie boeckp c1_k 20-12-1999 10:59:57

Holland Railconsult