



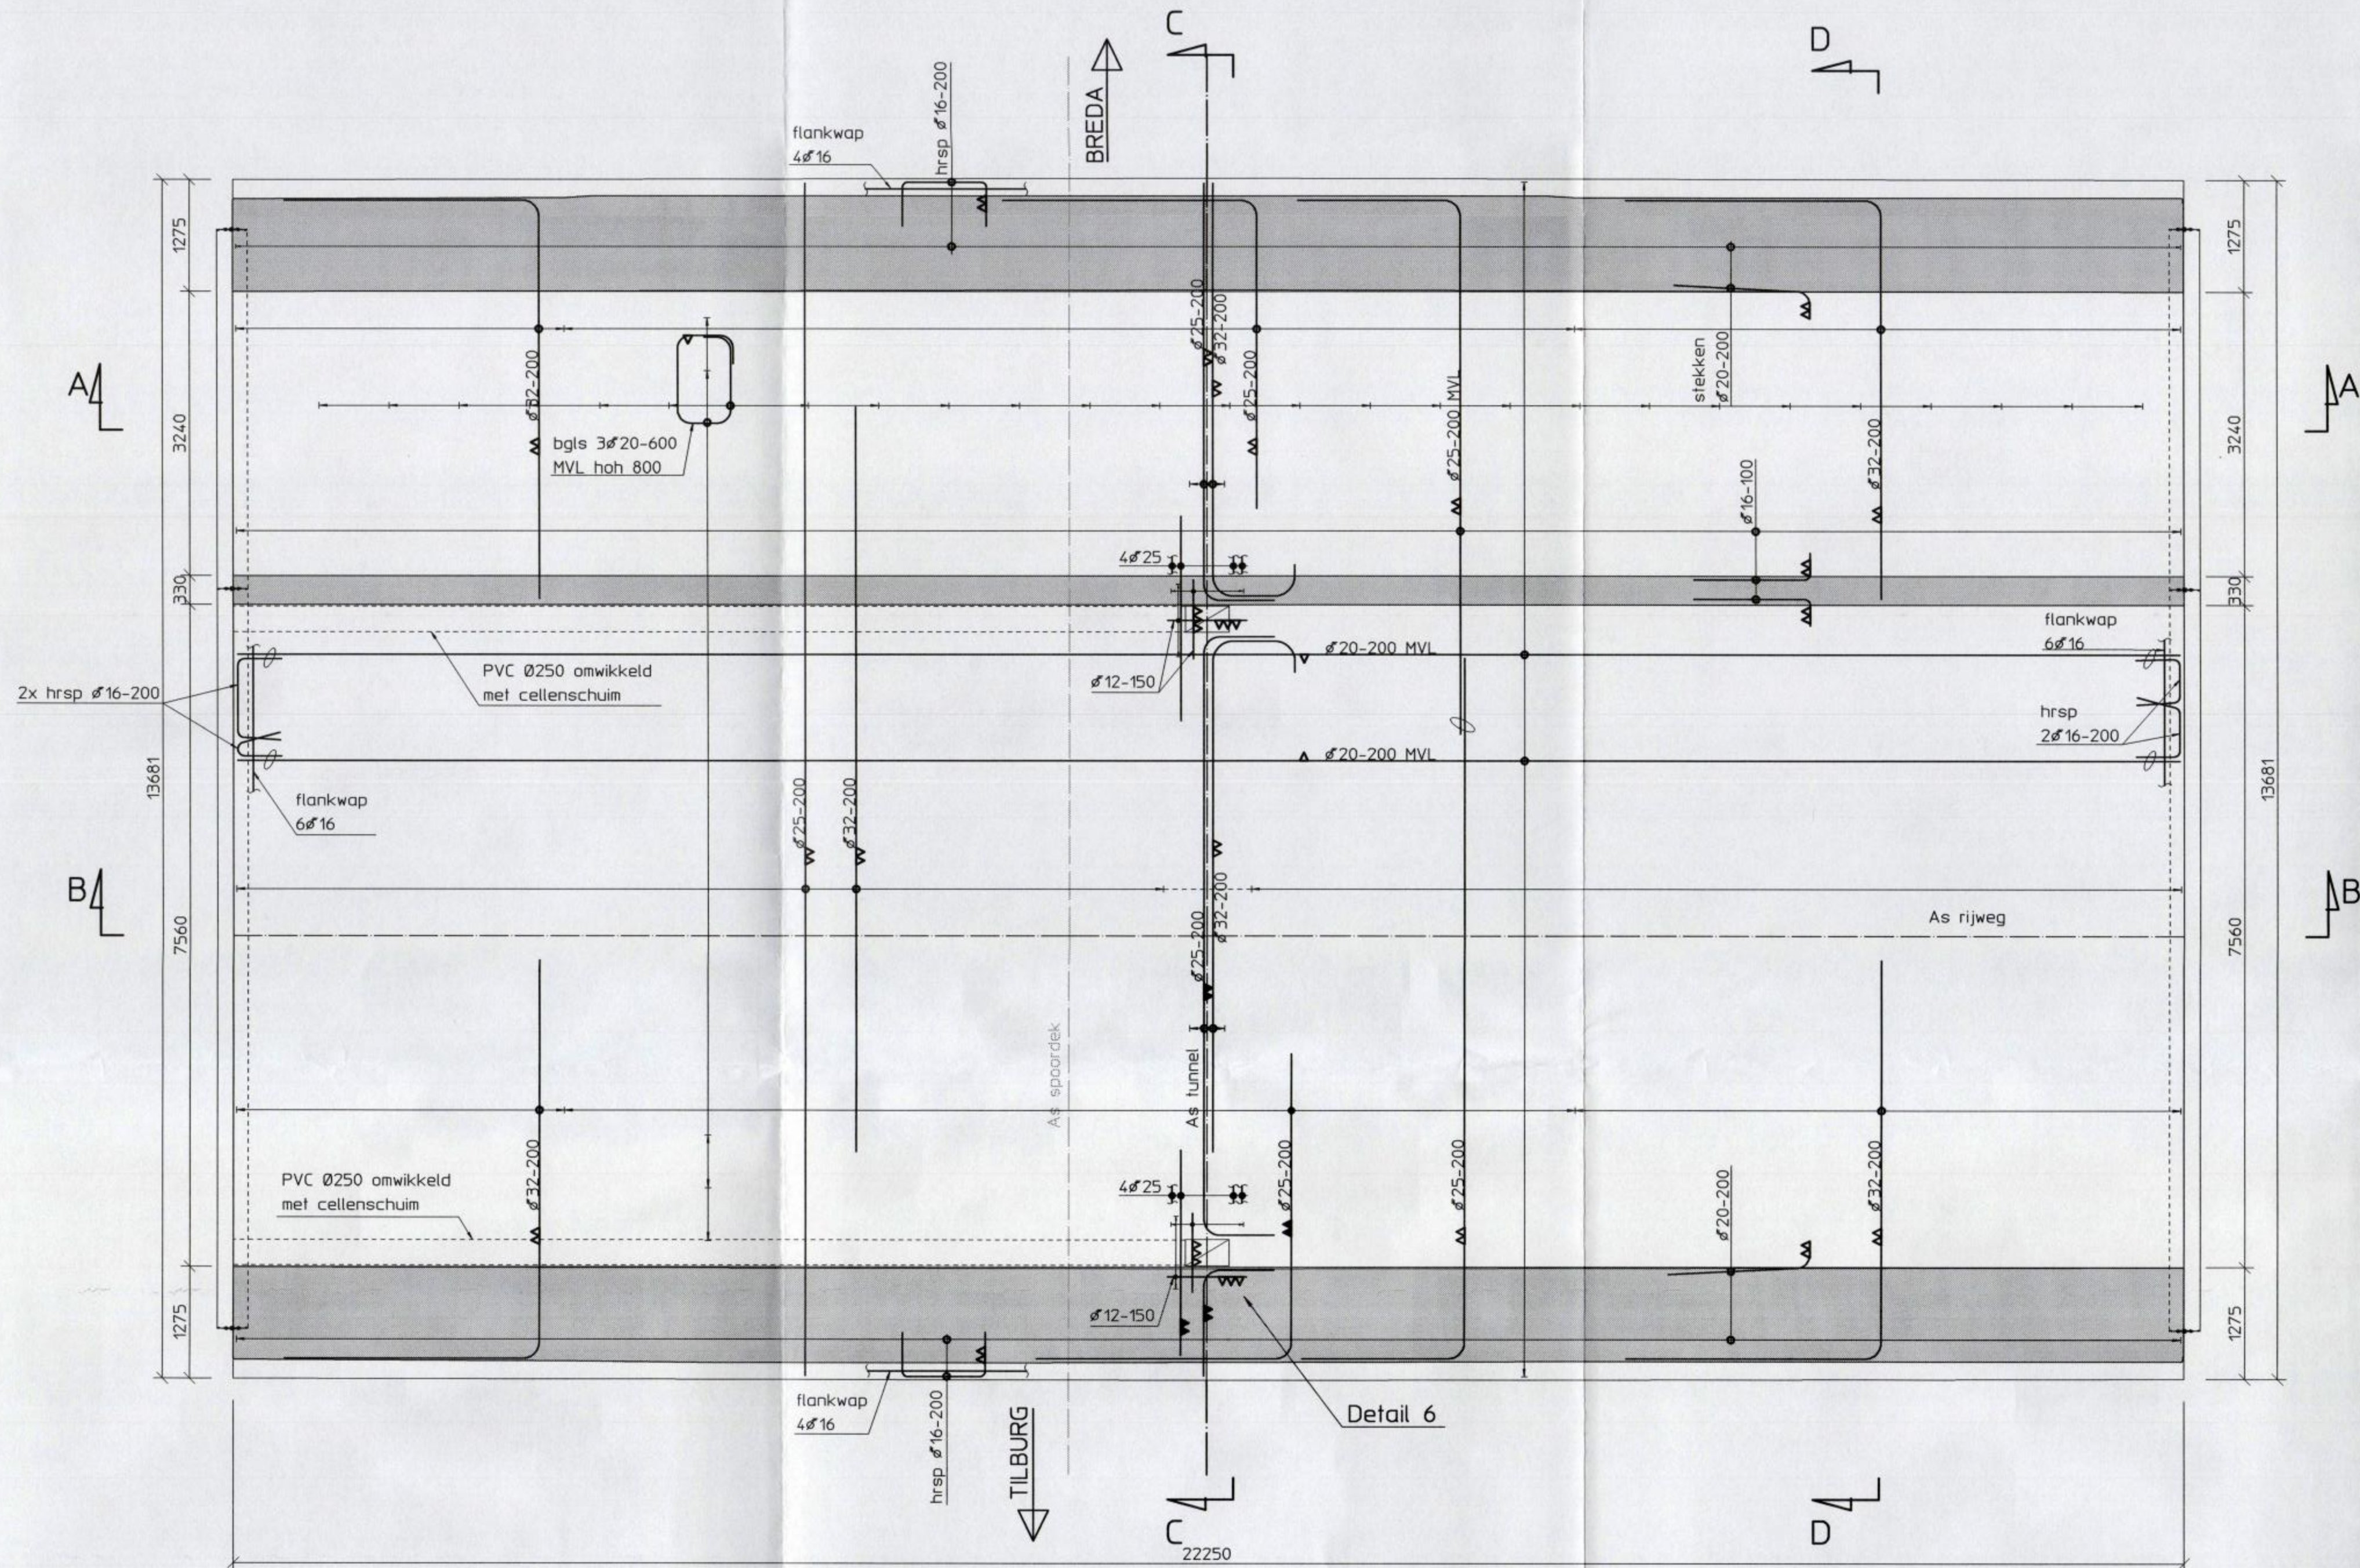


Bovenaanzicht vloer

Schaal 150

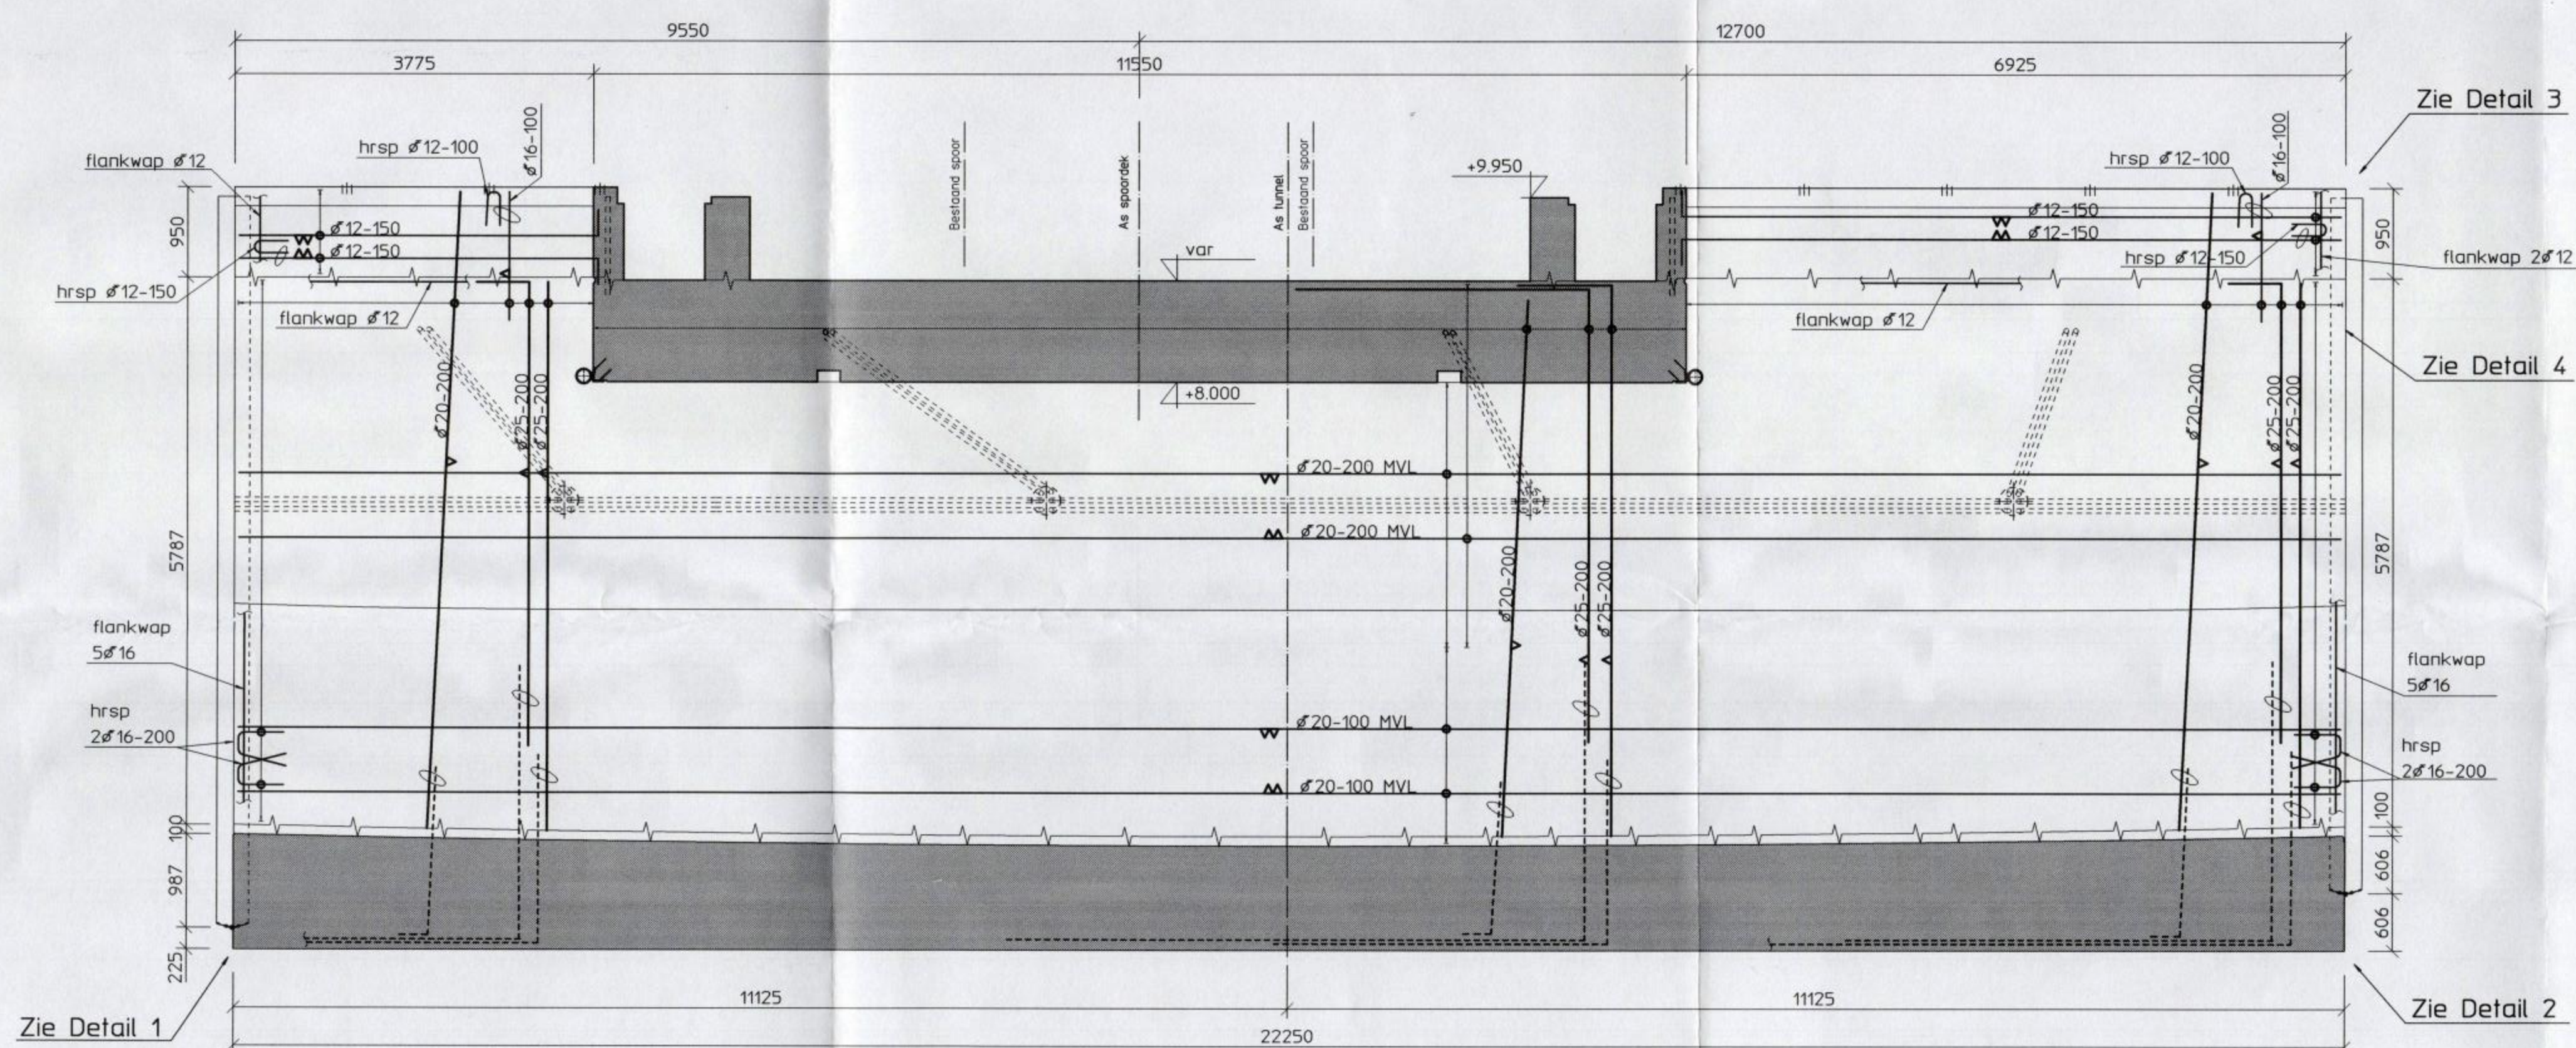


Doorsnede A

Schaal 150

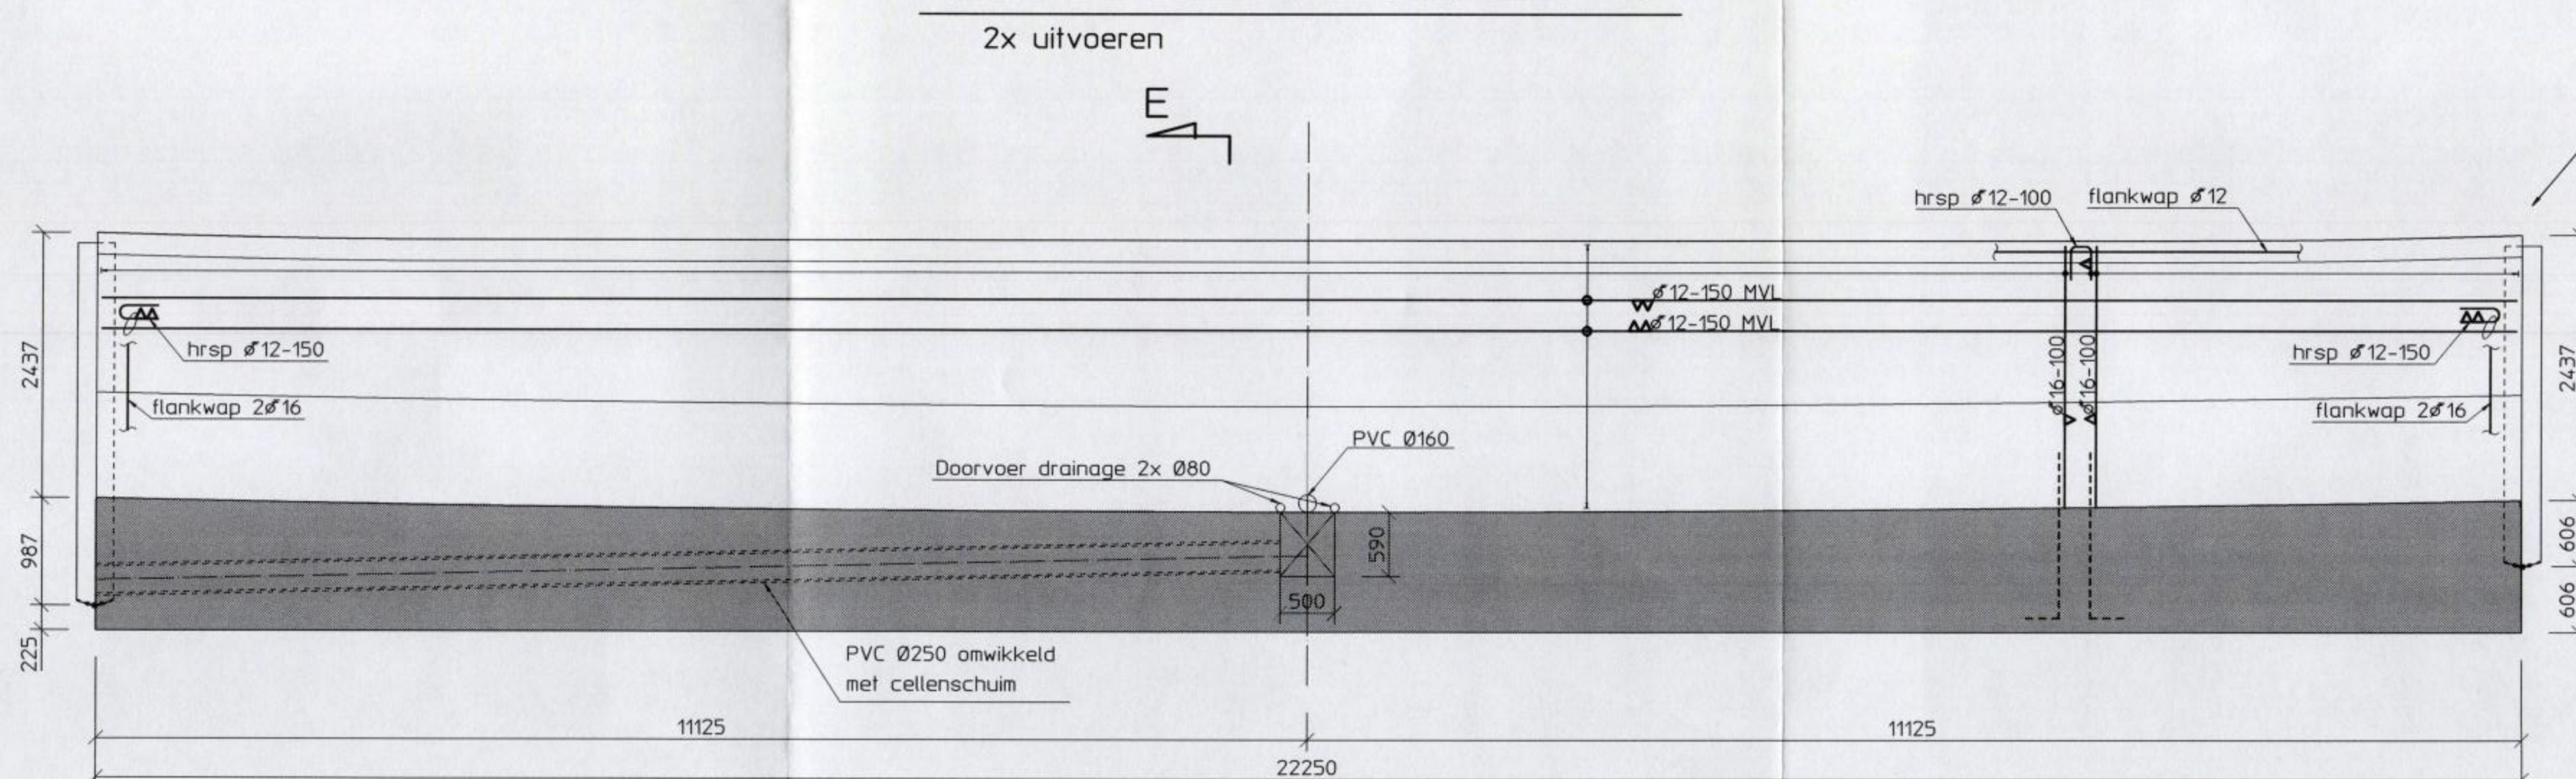


Doorsnede B

Schaal 150

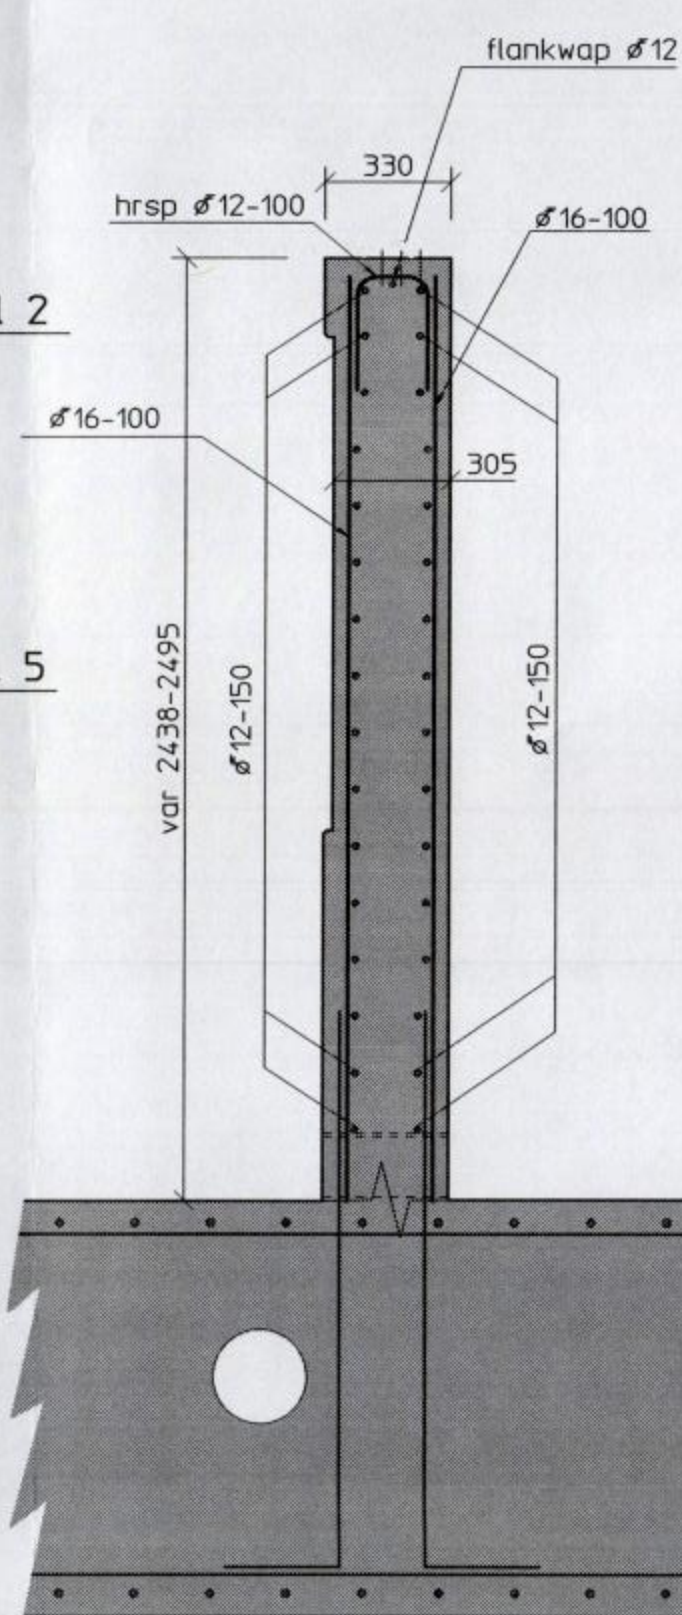


Doorsnede E

Schaal 120

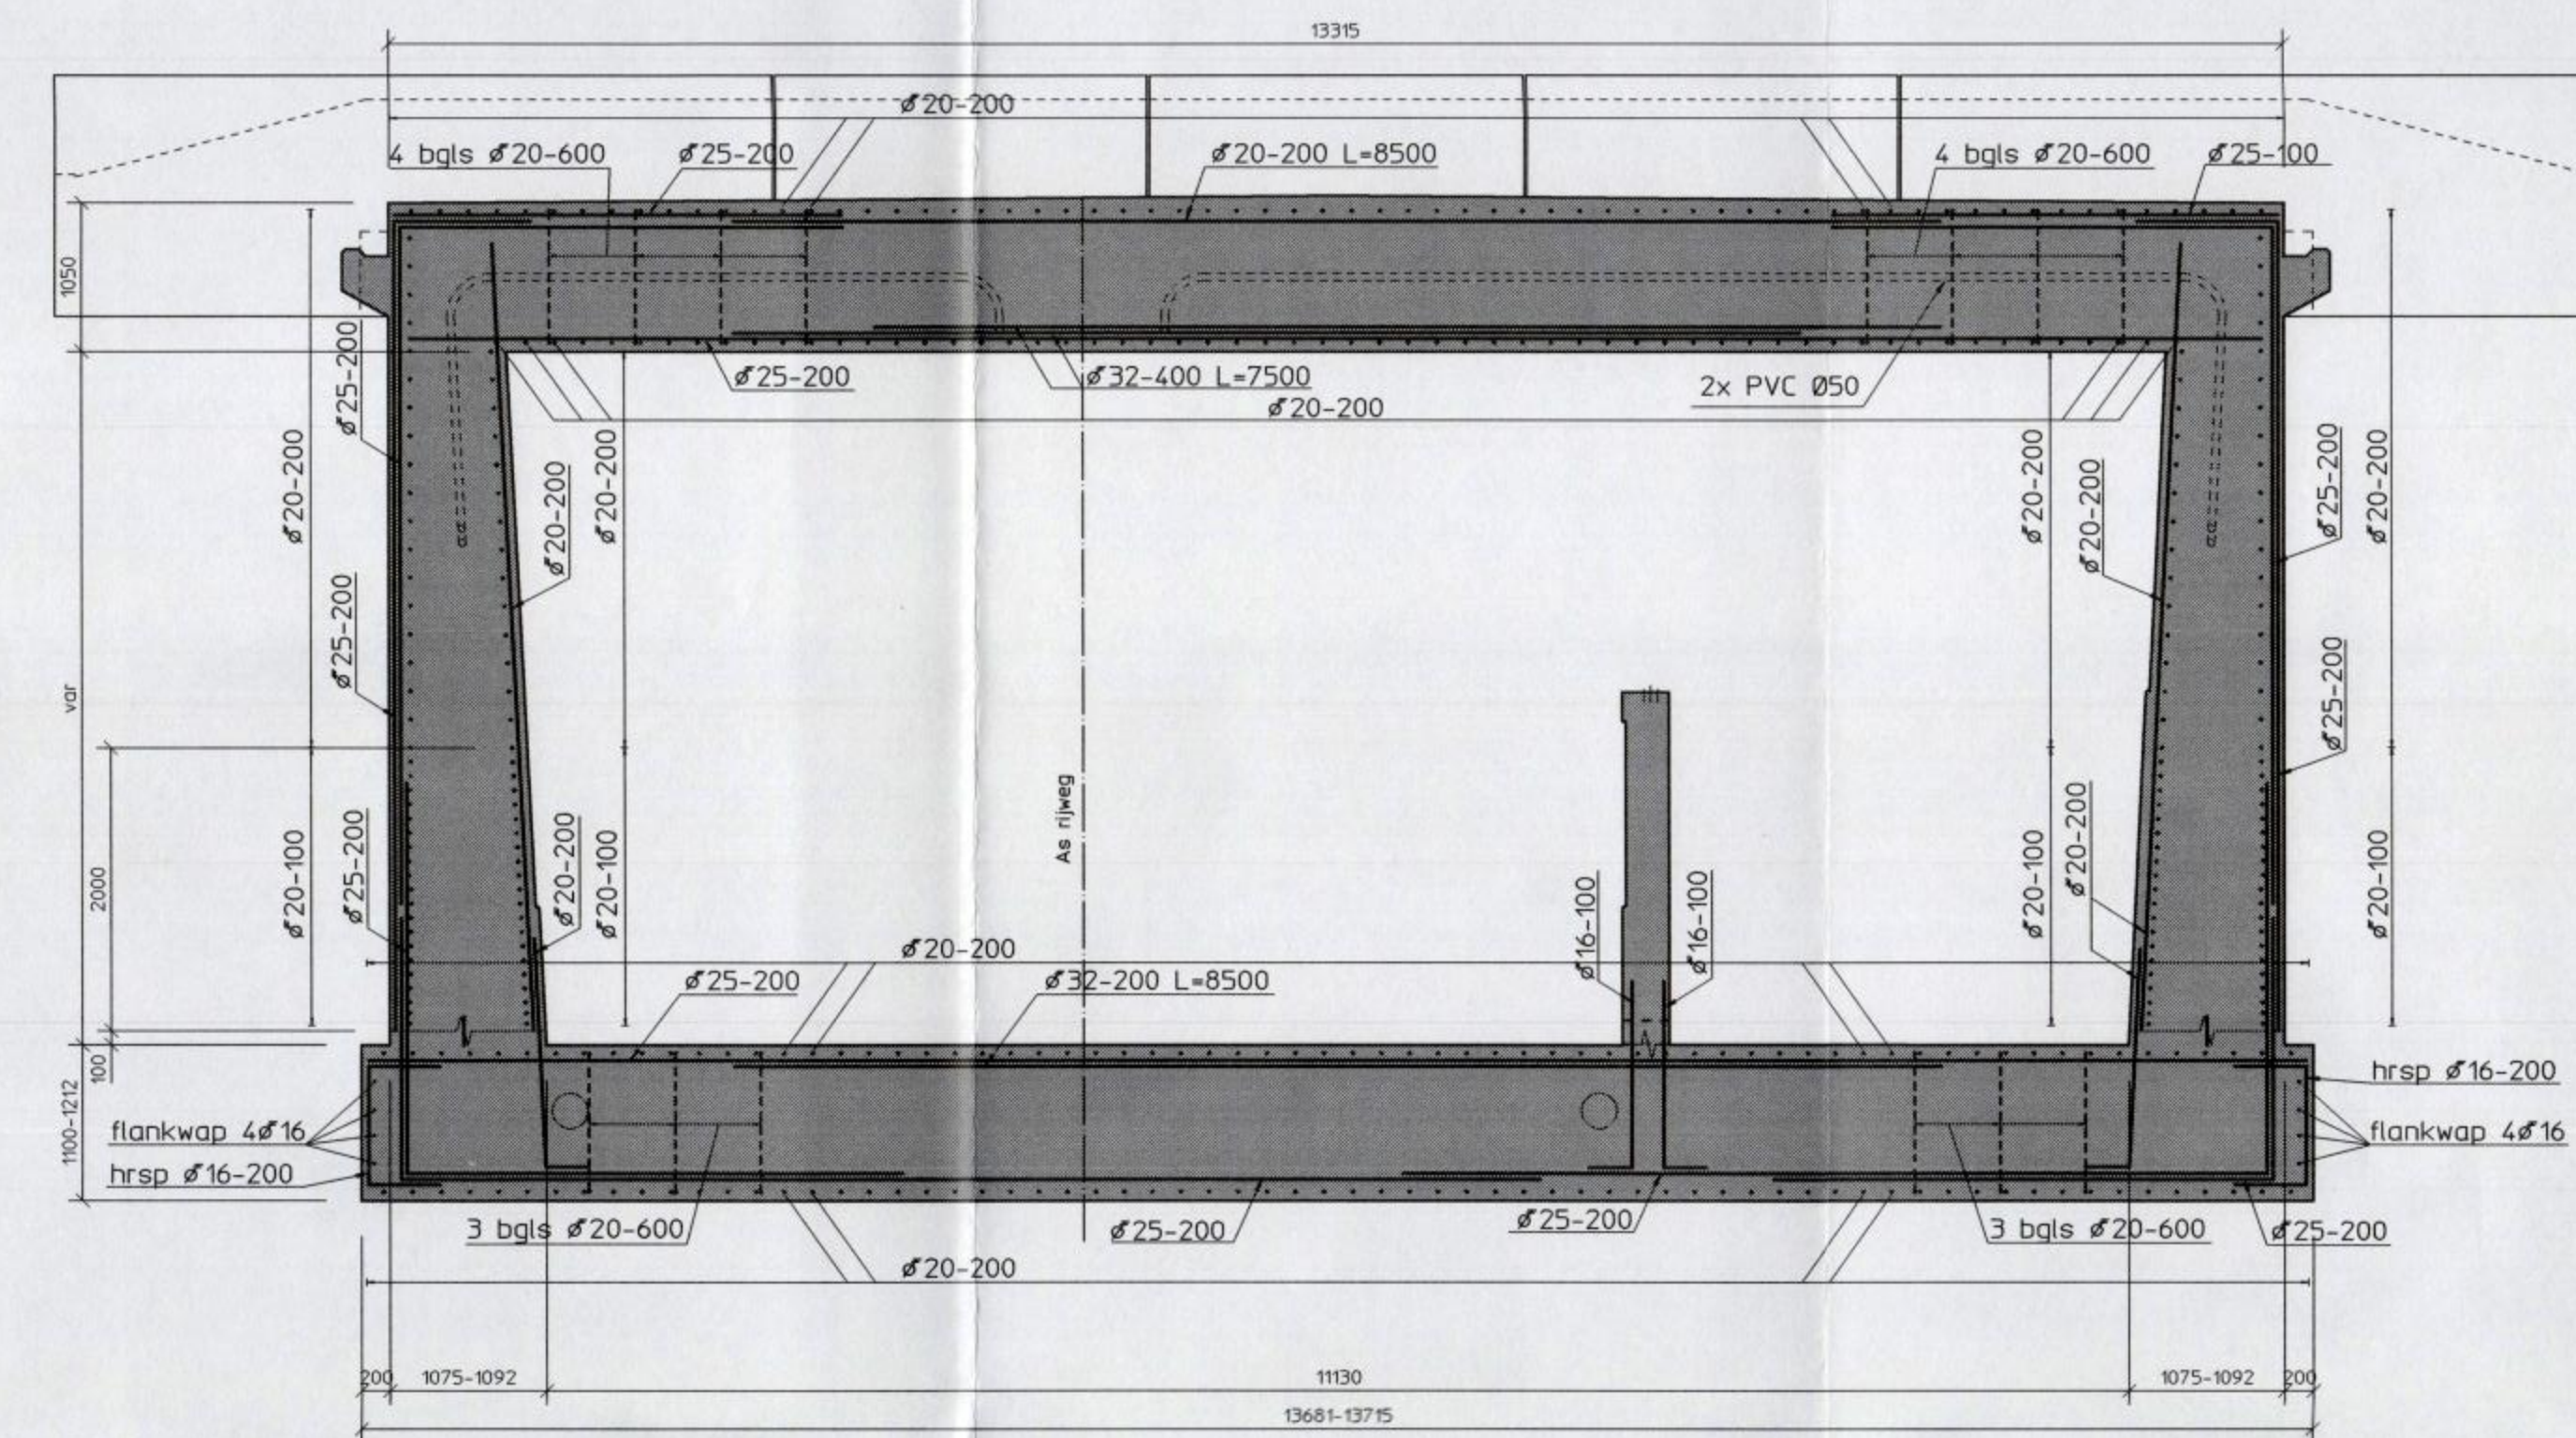


Doorsnede C

Schaal 150

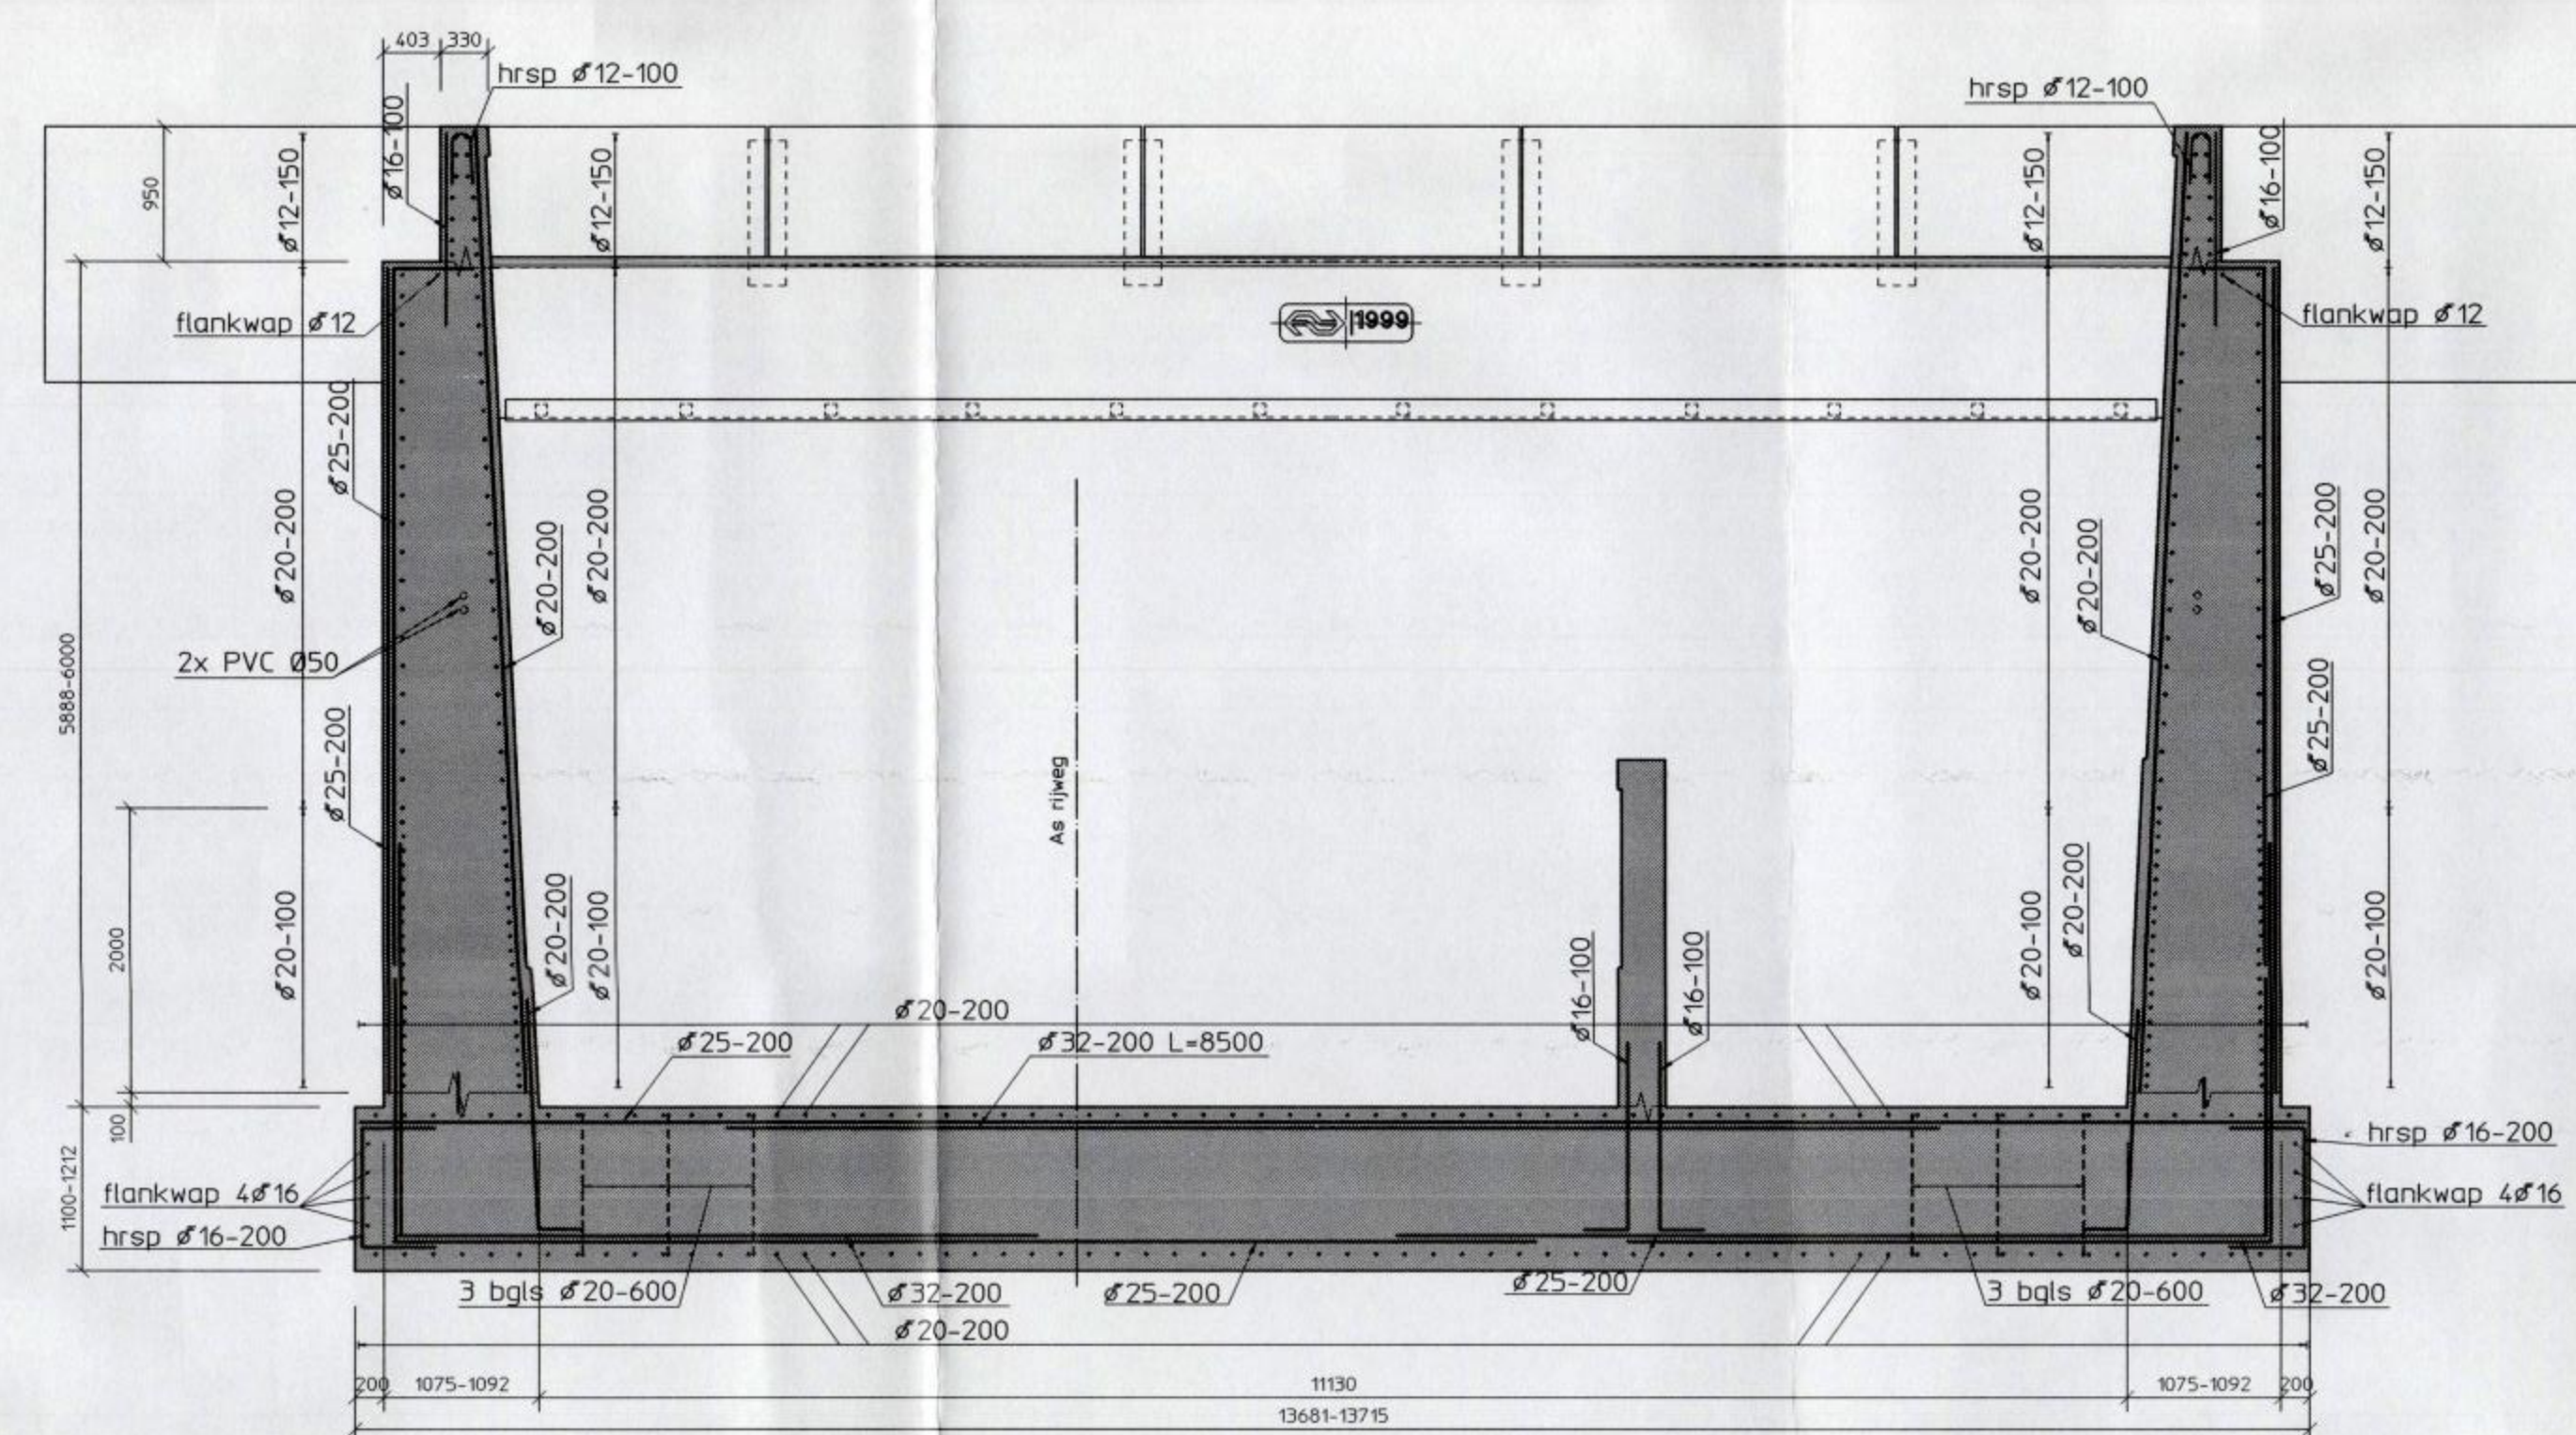


Doorsnede D

Schaal 150

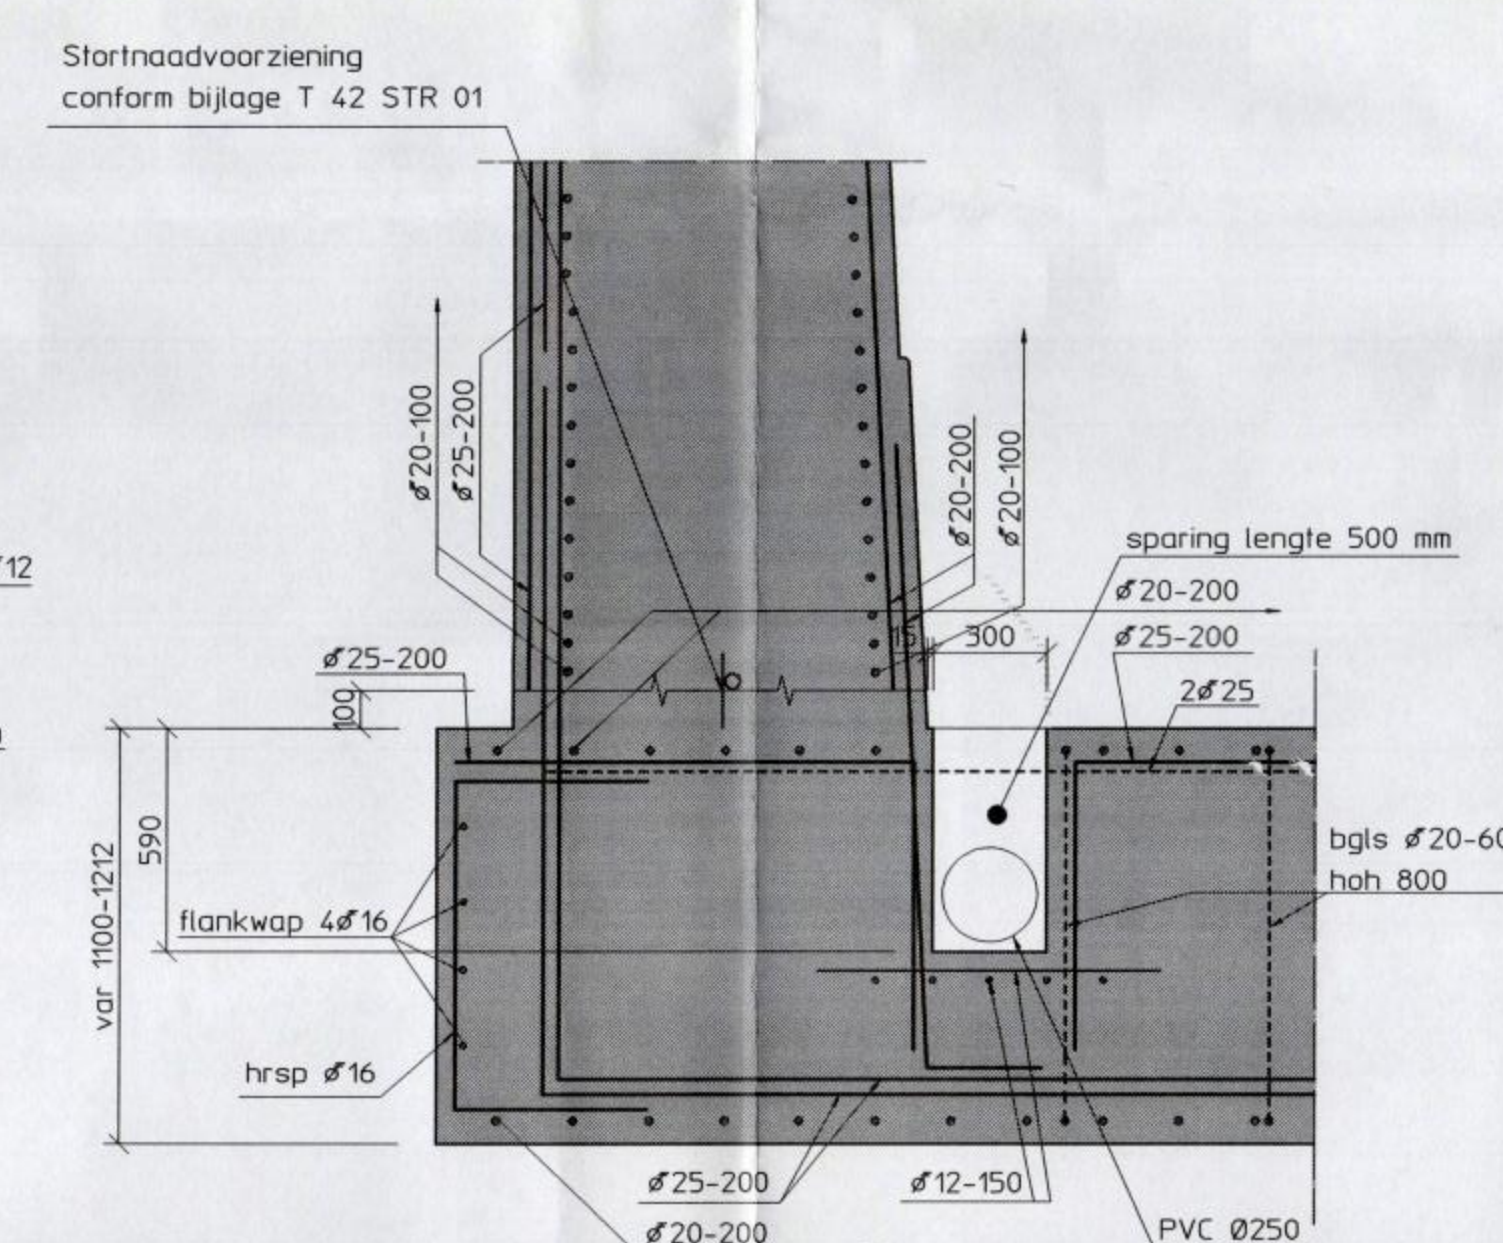


Detail 6

Schaal 120

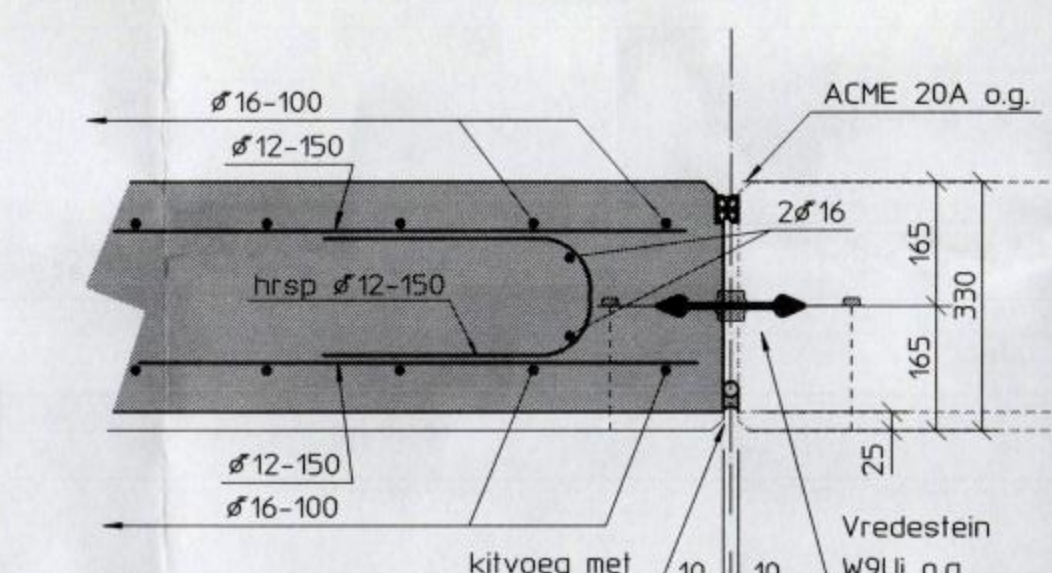

Detail 5

Schaal 110

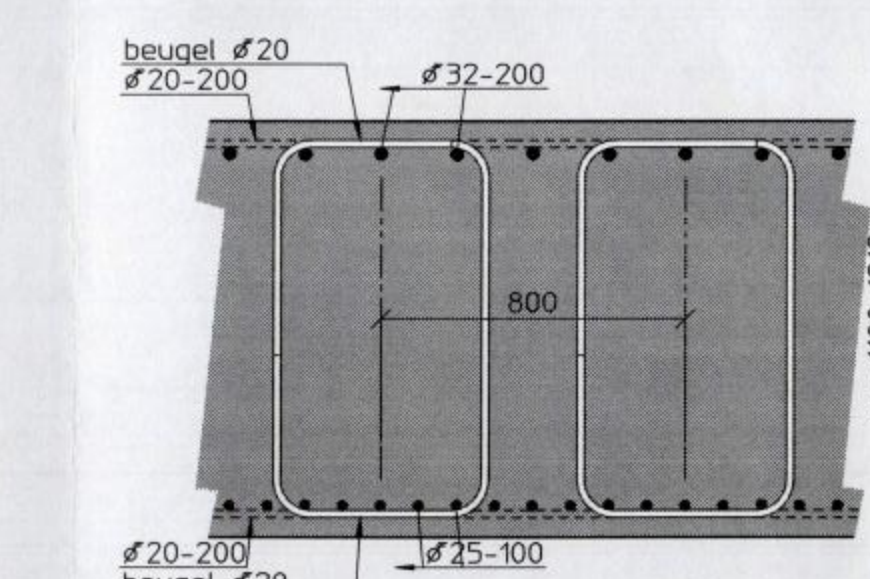

Beugels in vloer


Schaal 120

betondekkingstabel	
betonstaal :	- FeB 500 HVL en/of HK NEN 6008
beton :	- sterkteklasse B 35
	- milieuklasse 3 (vloer) / 5b (wanden-dek)
	- cement CEM III/B LH
constructieelement	
betondekking in mm	
controleerbaar	oncontroleerbaar
vloer	50
wand	50
dek	50
op- en aanstarten	35

verankeringslengten	
Ø10	*
Ø12	270
Ø14	320
Ø16	420
Ø20	570
Ø25	760
Ø28	*
Ø32	1280
Ø40	*


Detail 1

Schaal 120

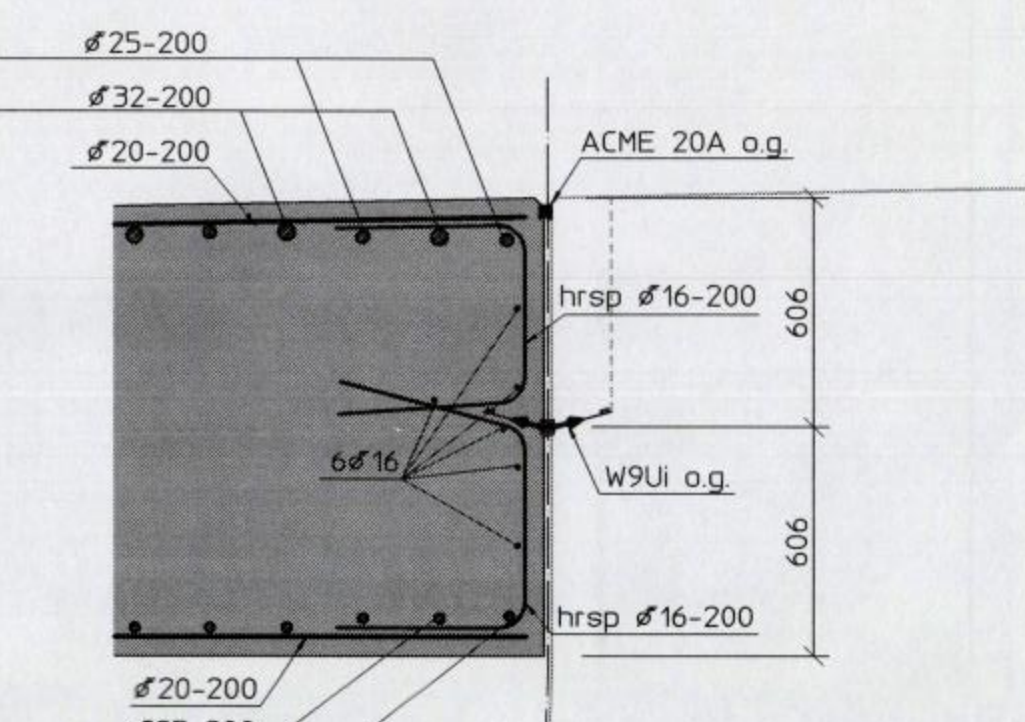


Detail 2

Schaal 120

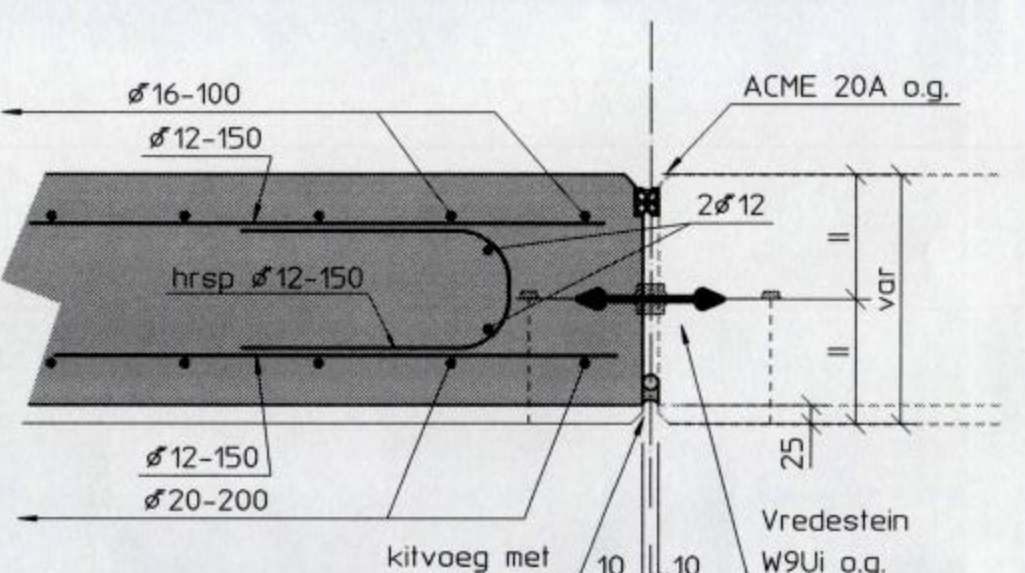


Detail 3

Schaal 110

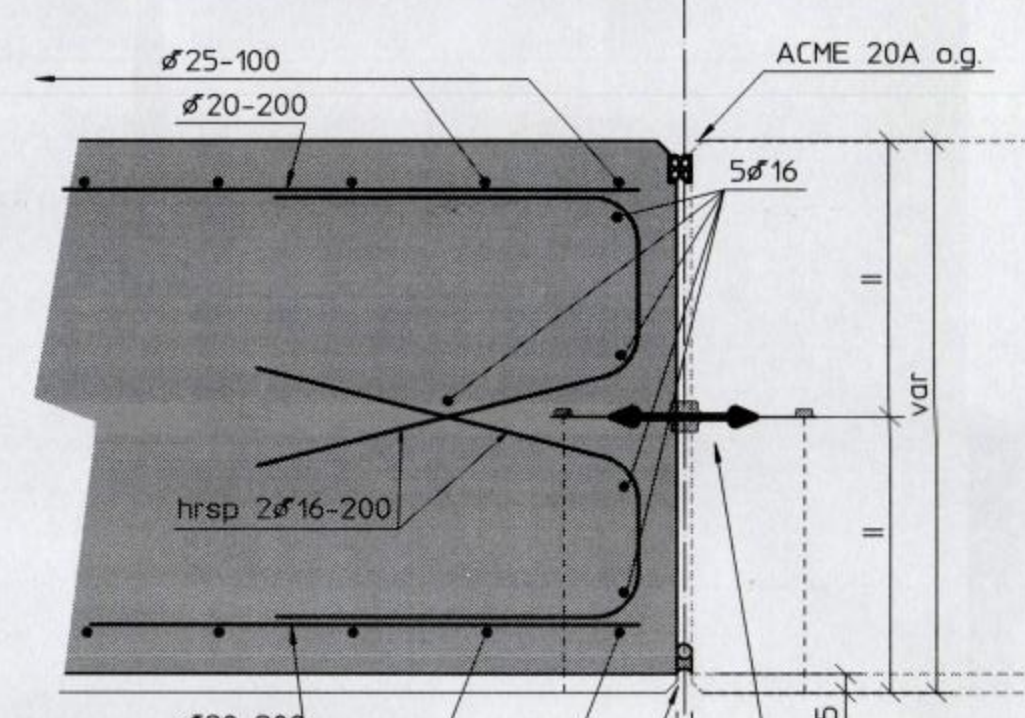

Detail 4

Schaal 110

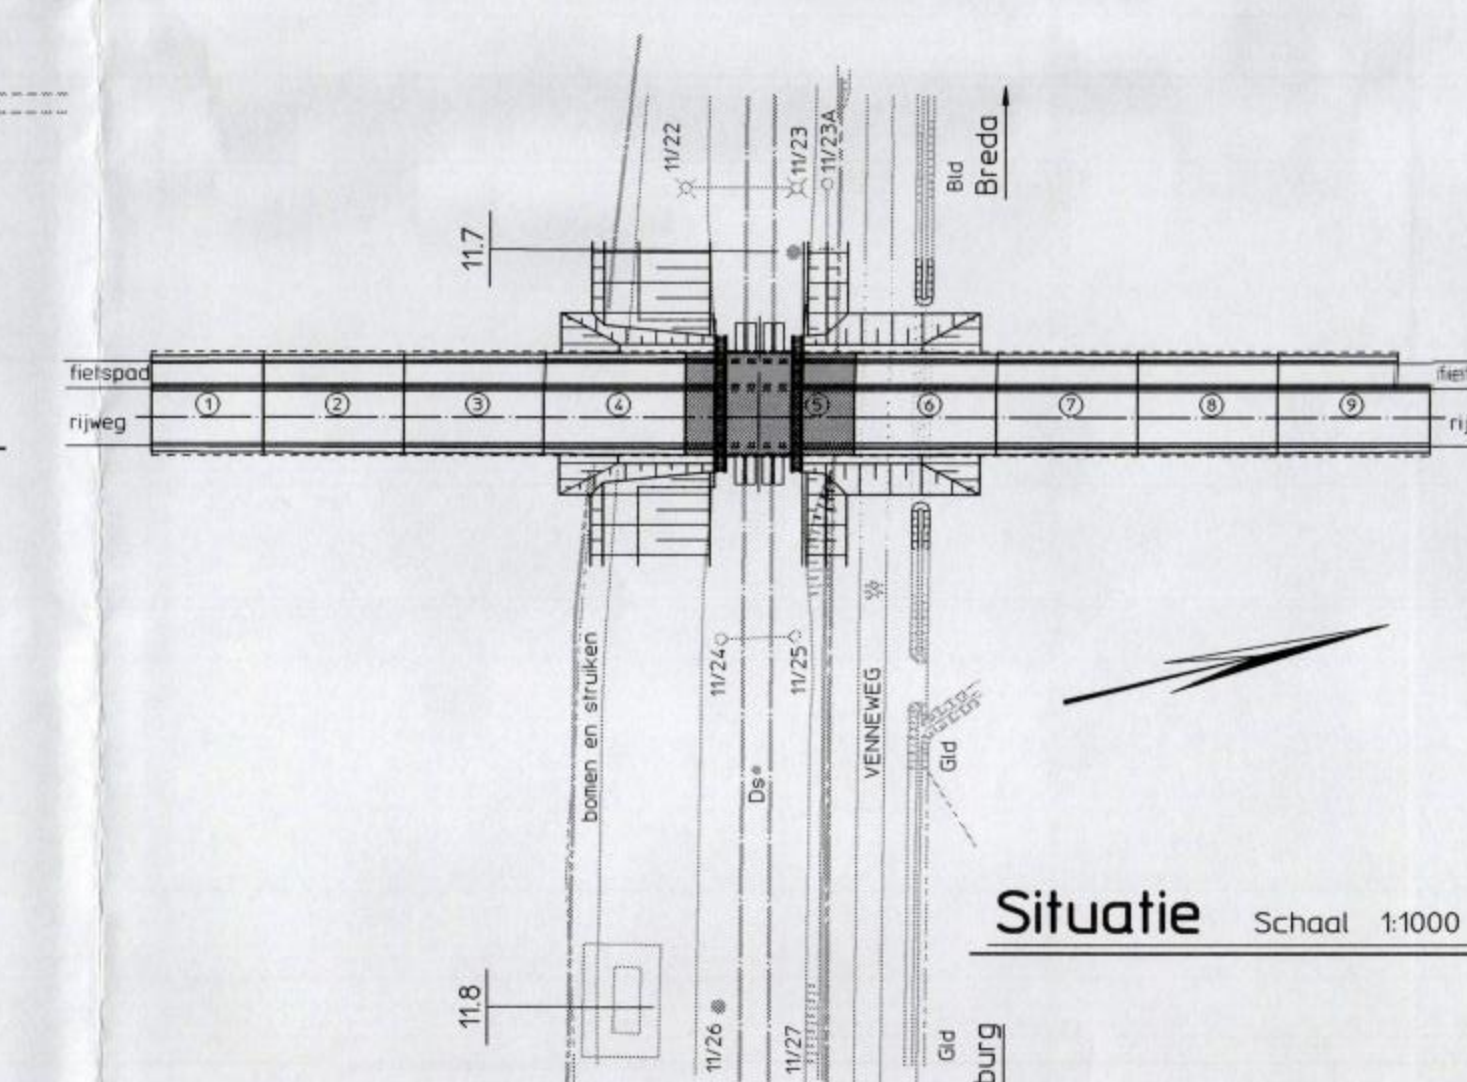

Situatie

Schaal 11000

- maatvoering in mm
- haagtemaatvoering in m tov. N.A.P.
- voor wapening dek zie tek. 3362706 51 w
- voor maatvoering zie tek. 3362706 50 m en 51 m
- MVL = met verspringende las

(Status: REVISIE d.d. 17-12-1999 14.42.08)

naam		par. datum	
gekleed	M.W. Gritter	17-12-99	Wapening Mool 5
projectleider	C.F. Vink		Blad 1
projectnr.	3362706	versie	1.0
bestelnr.	V40809450		
formaat	A0		
schaal	zie tek.		
420	123	11.720	713
3362706	50	W	
Holland Railconsult			