
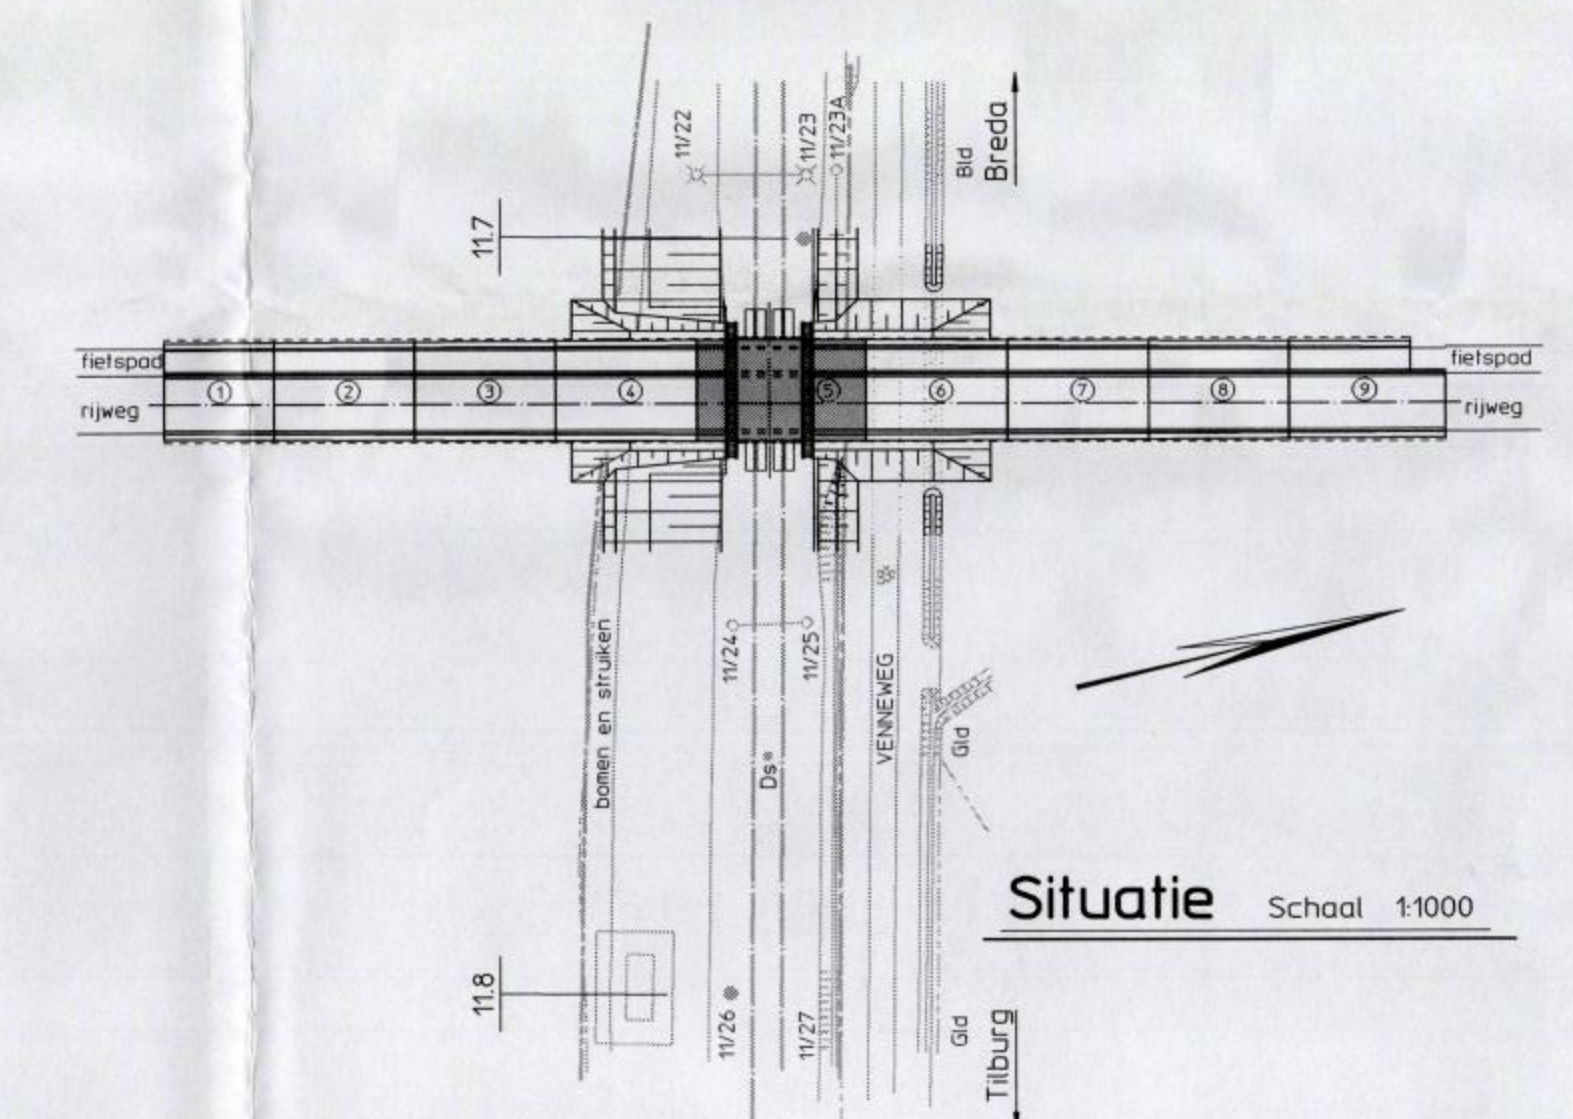
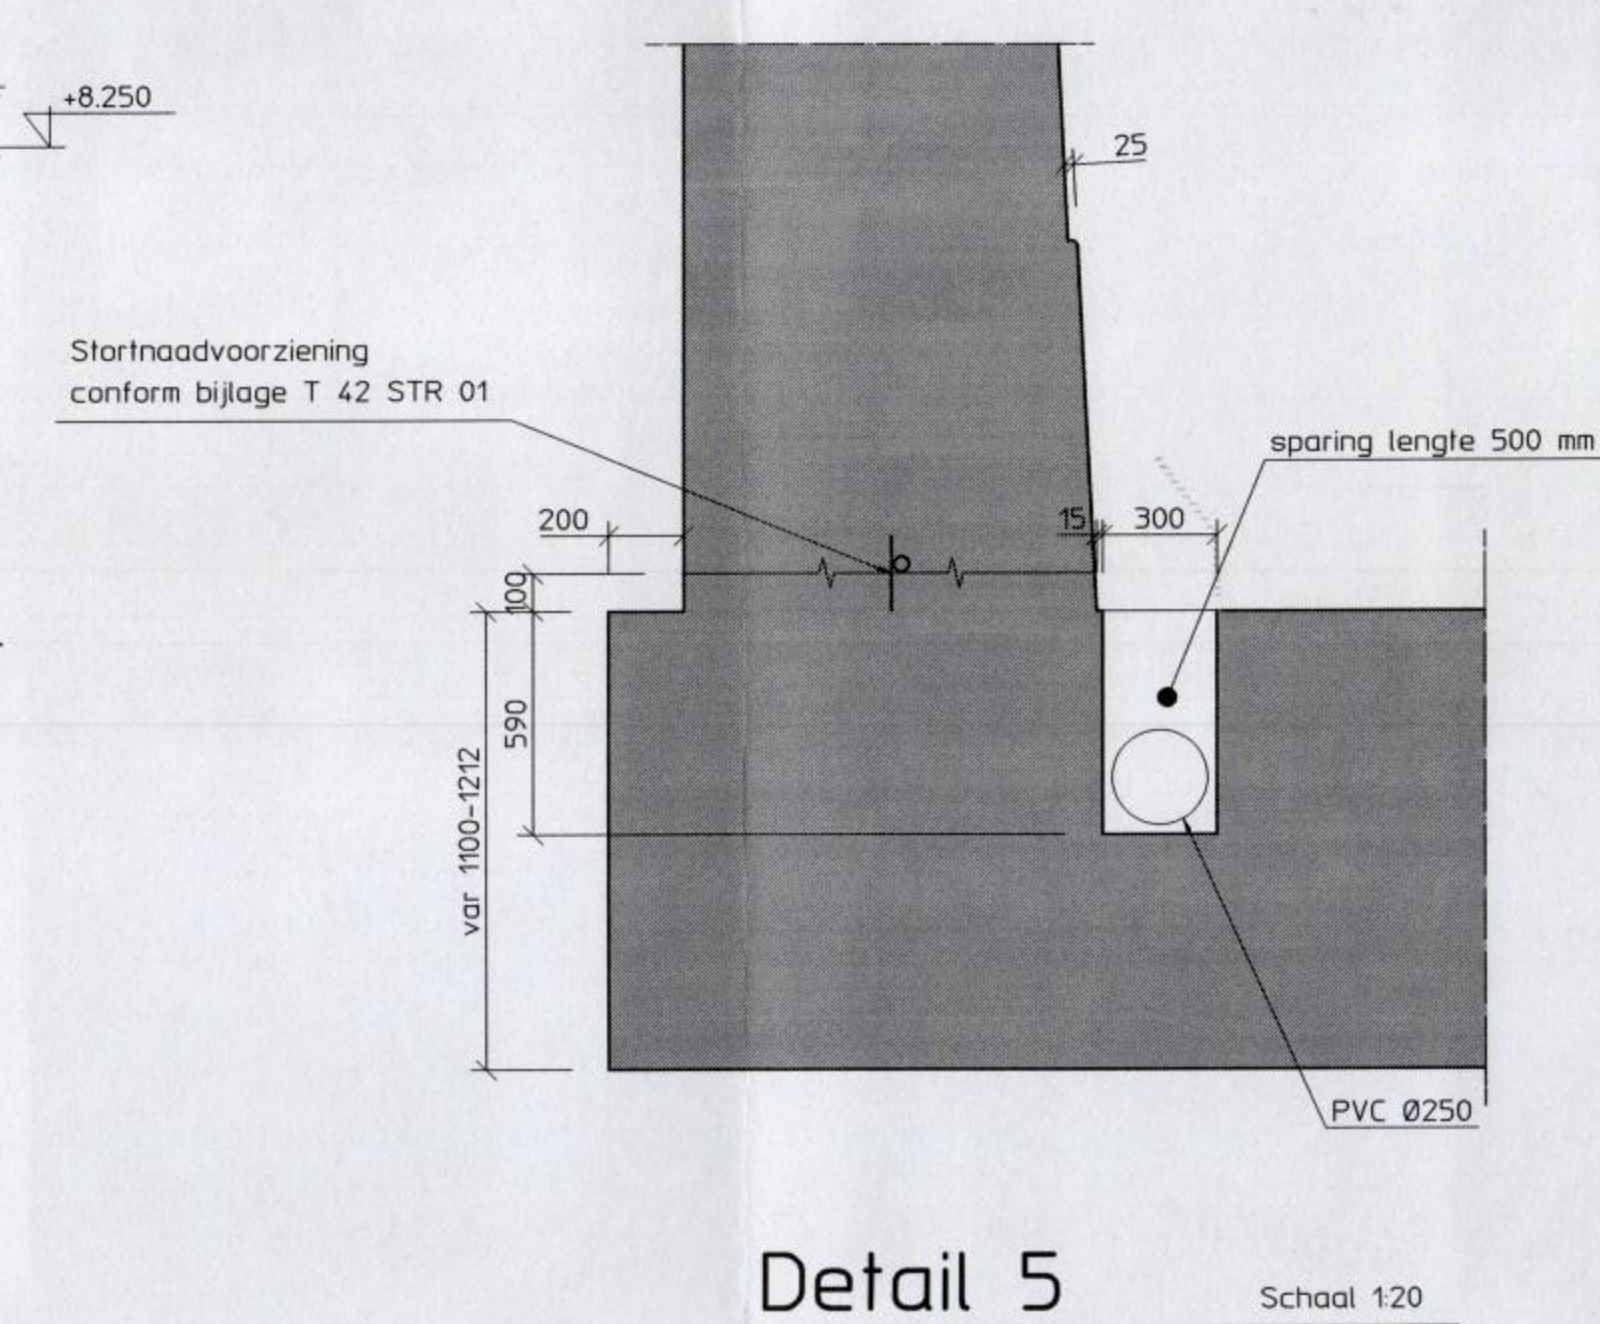
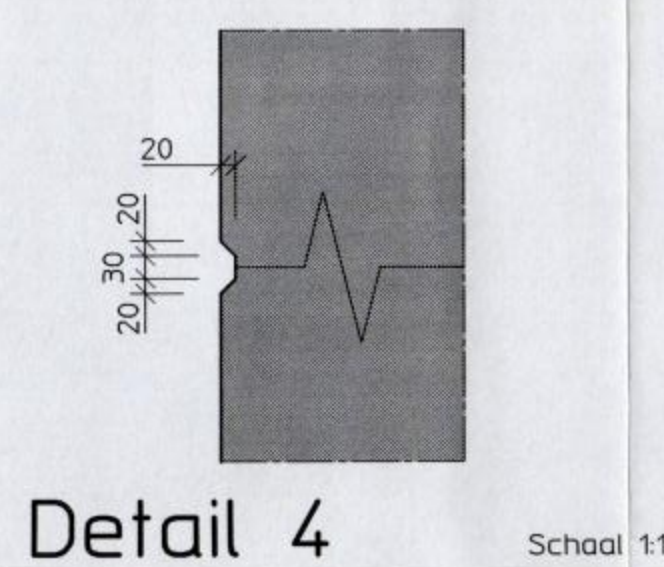
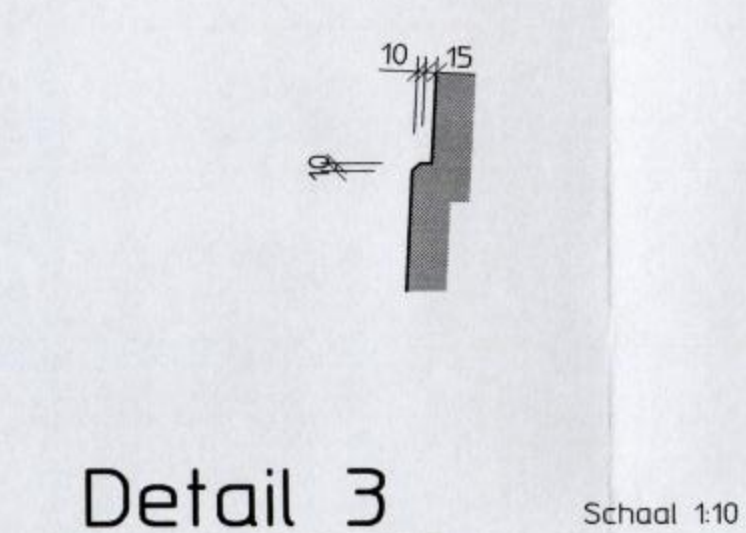
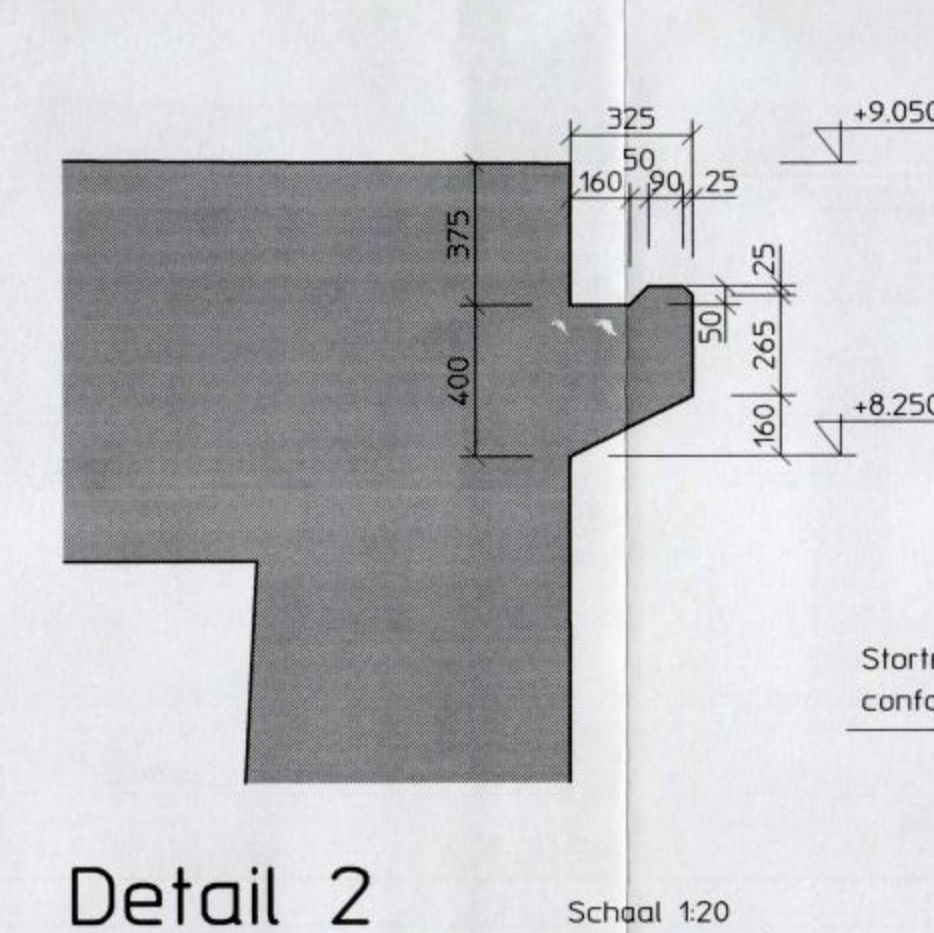
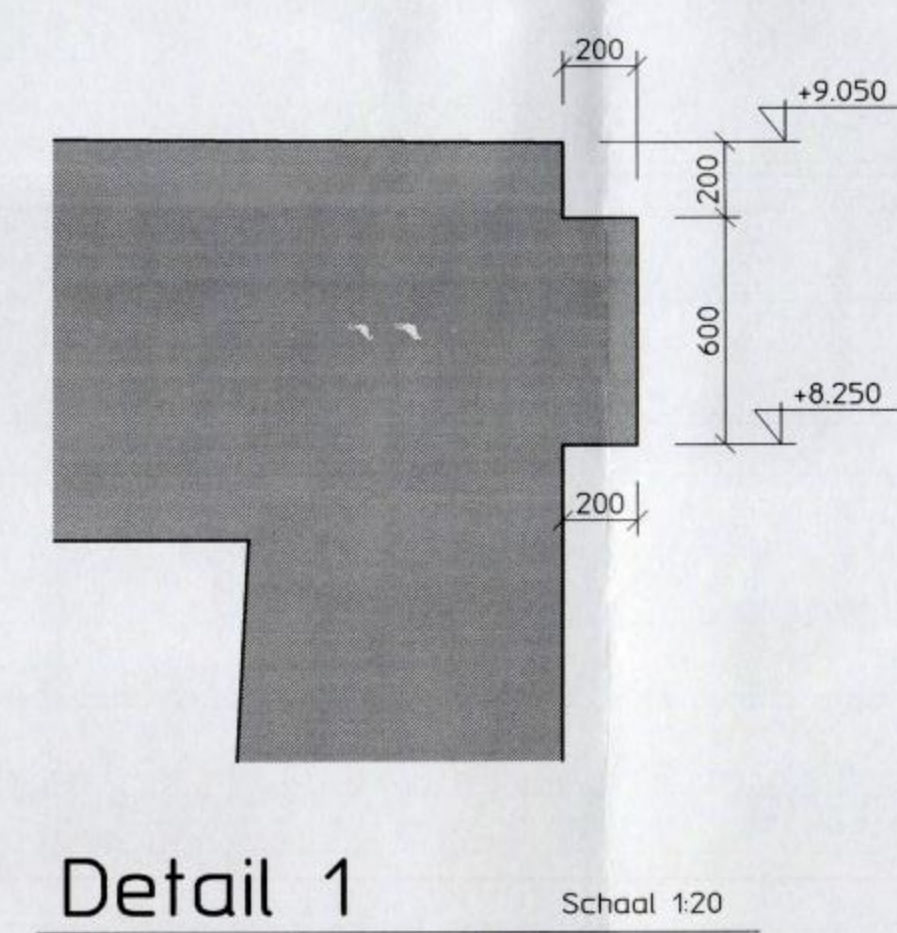
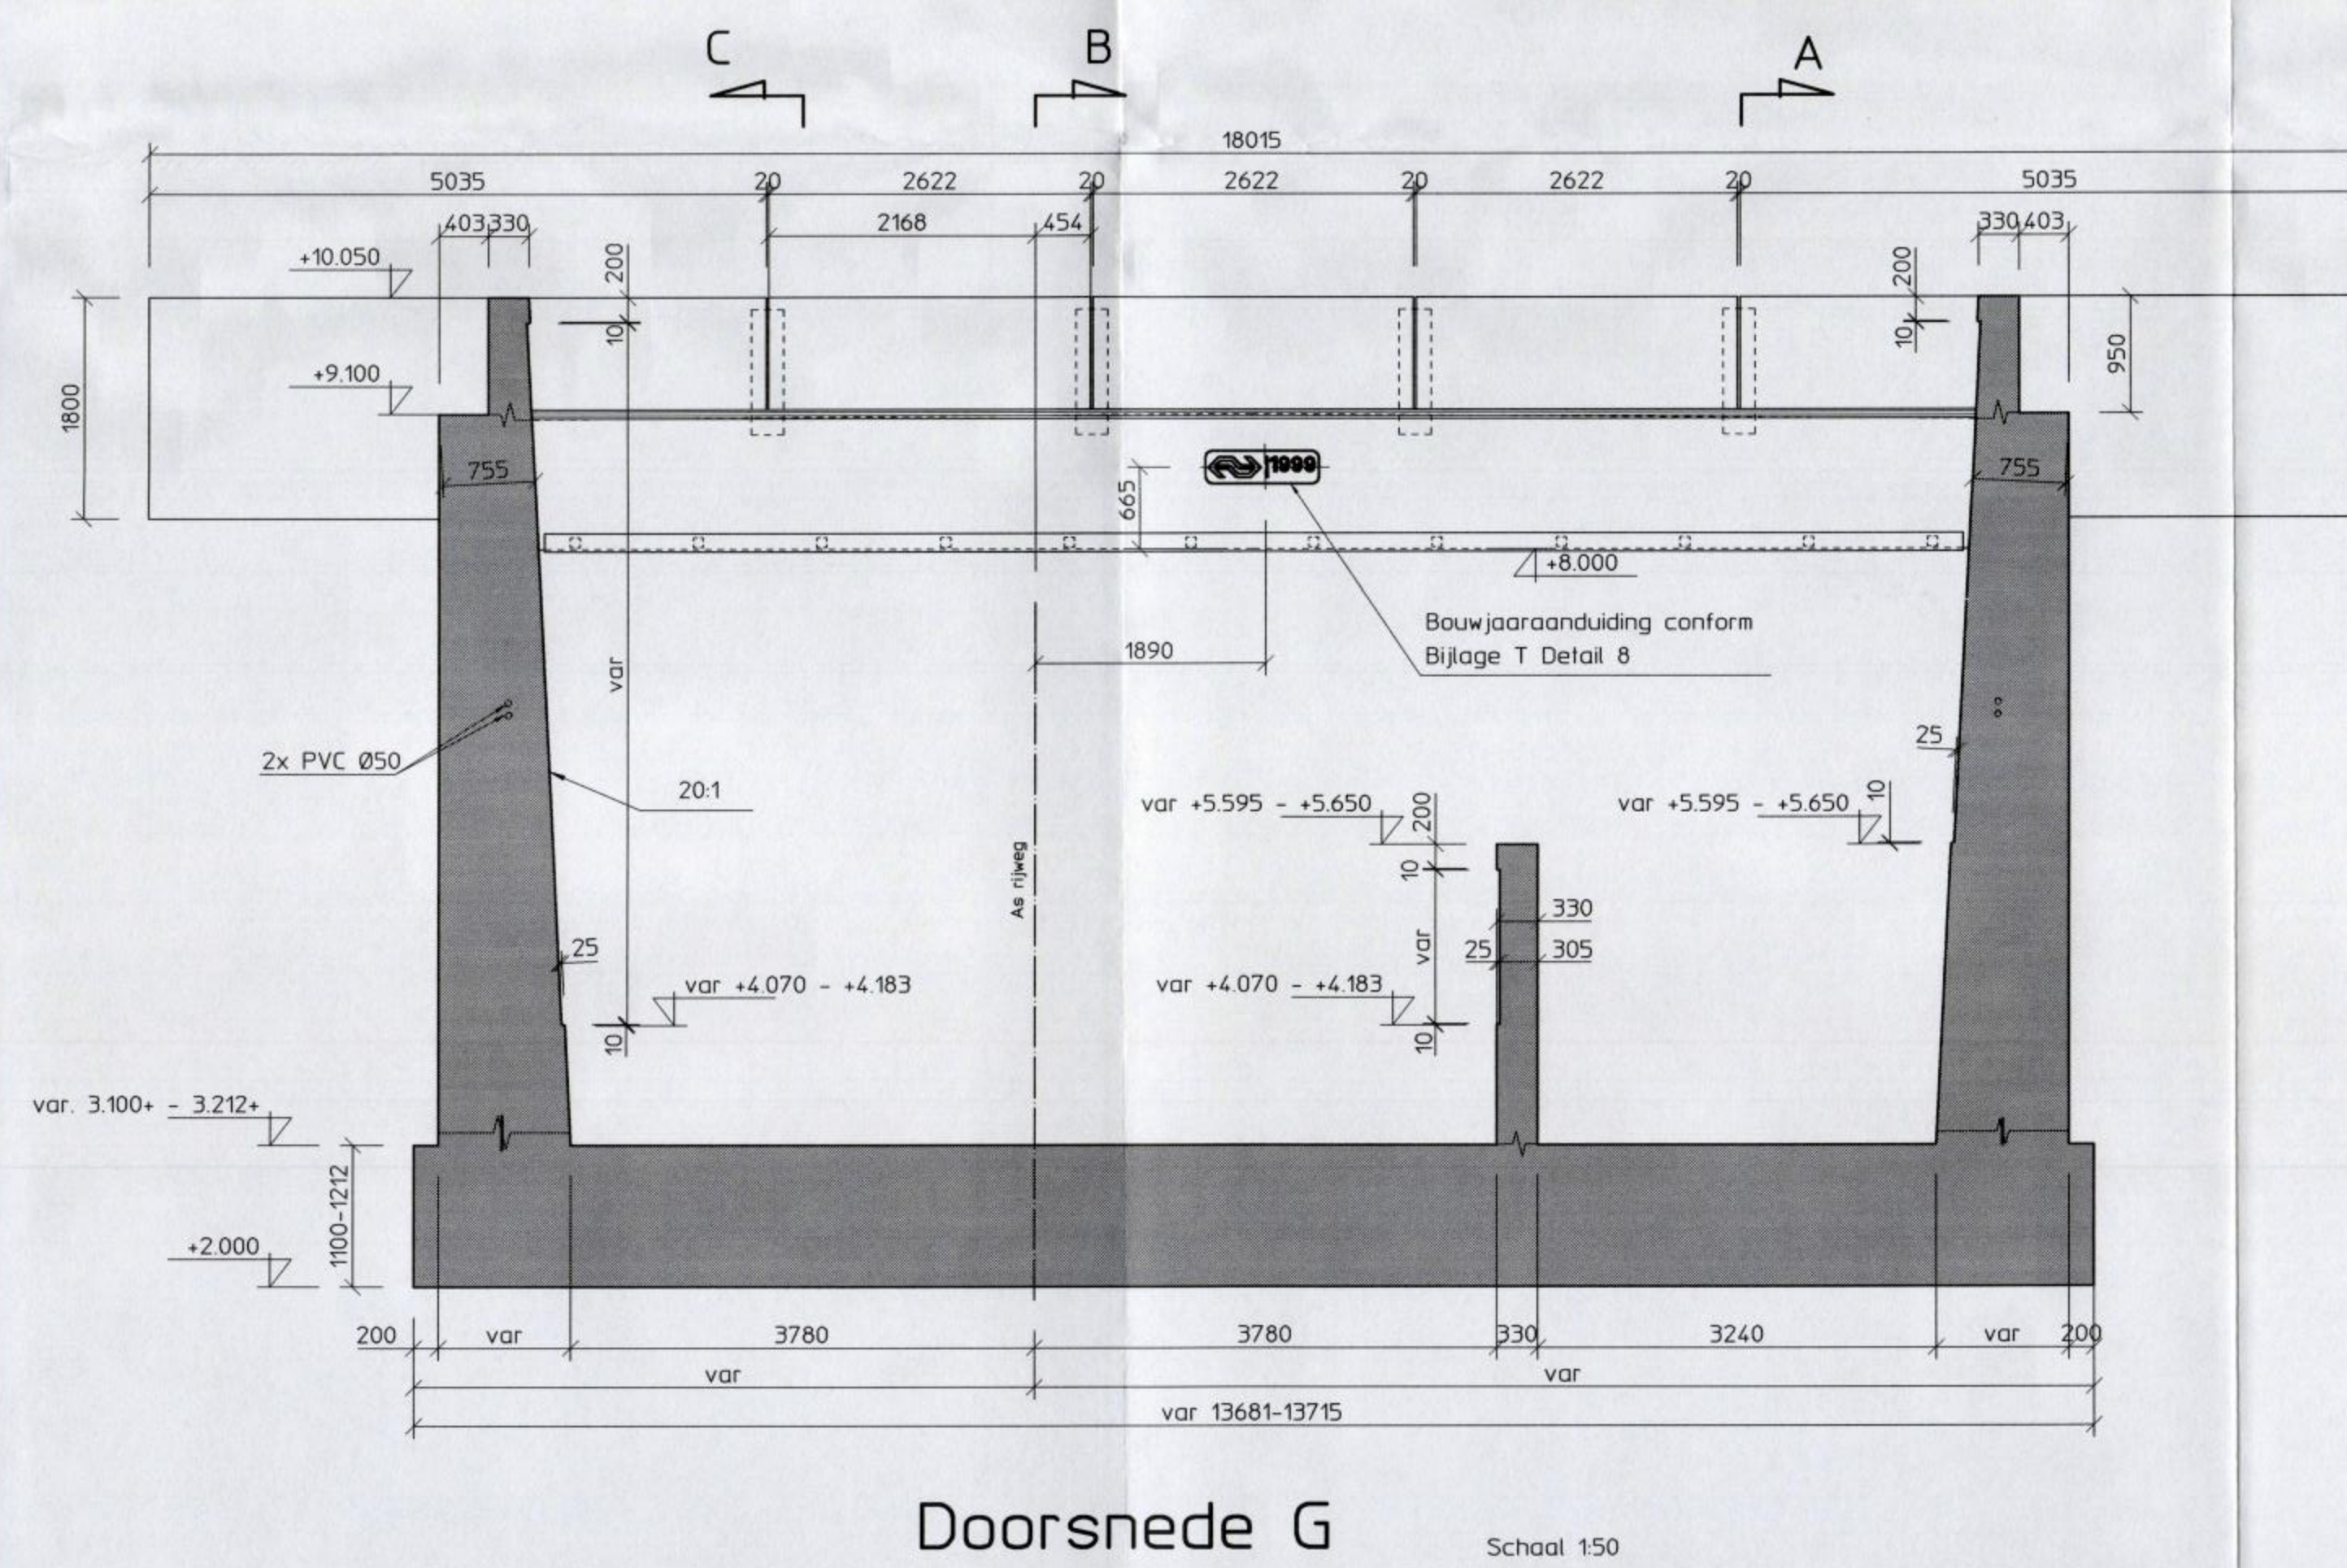
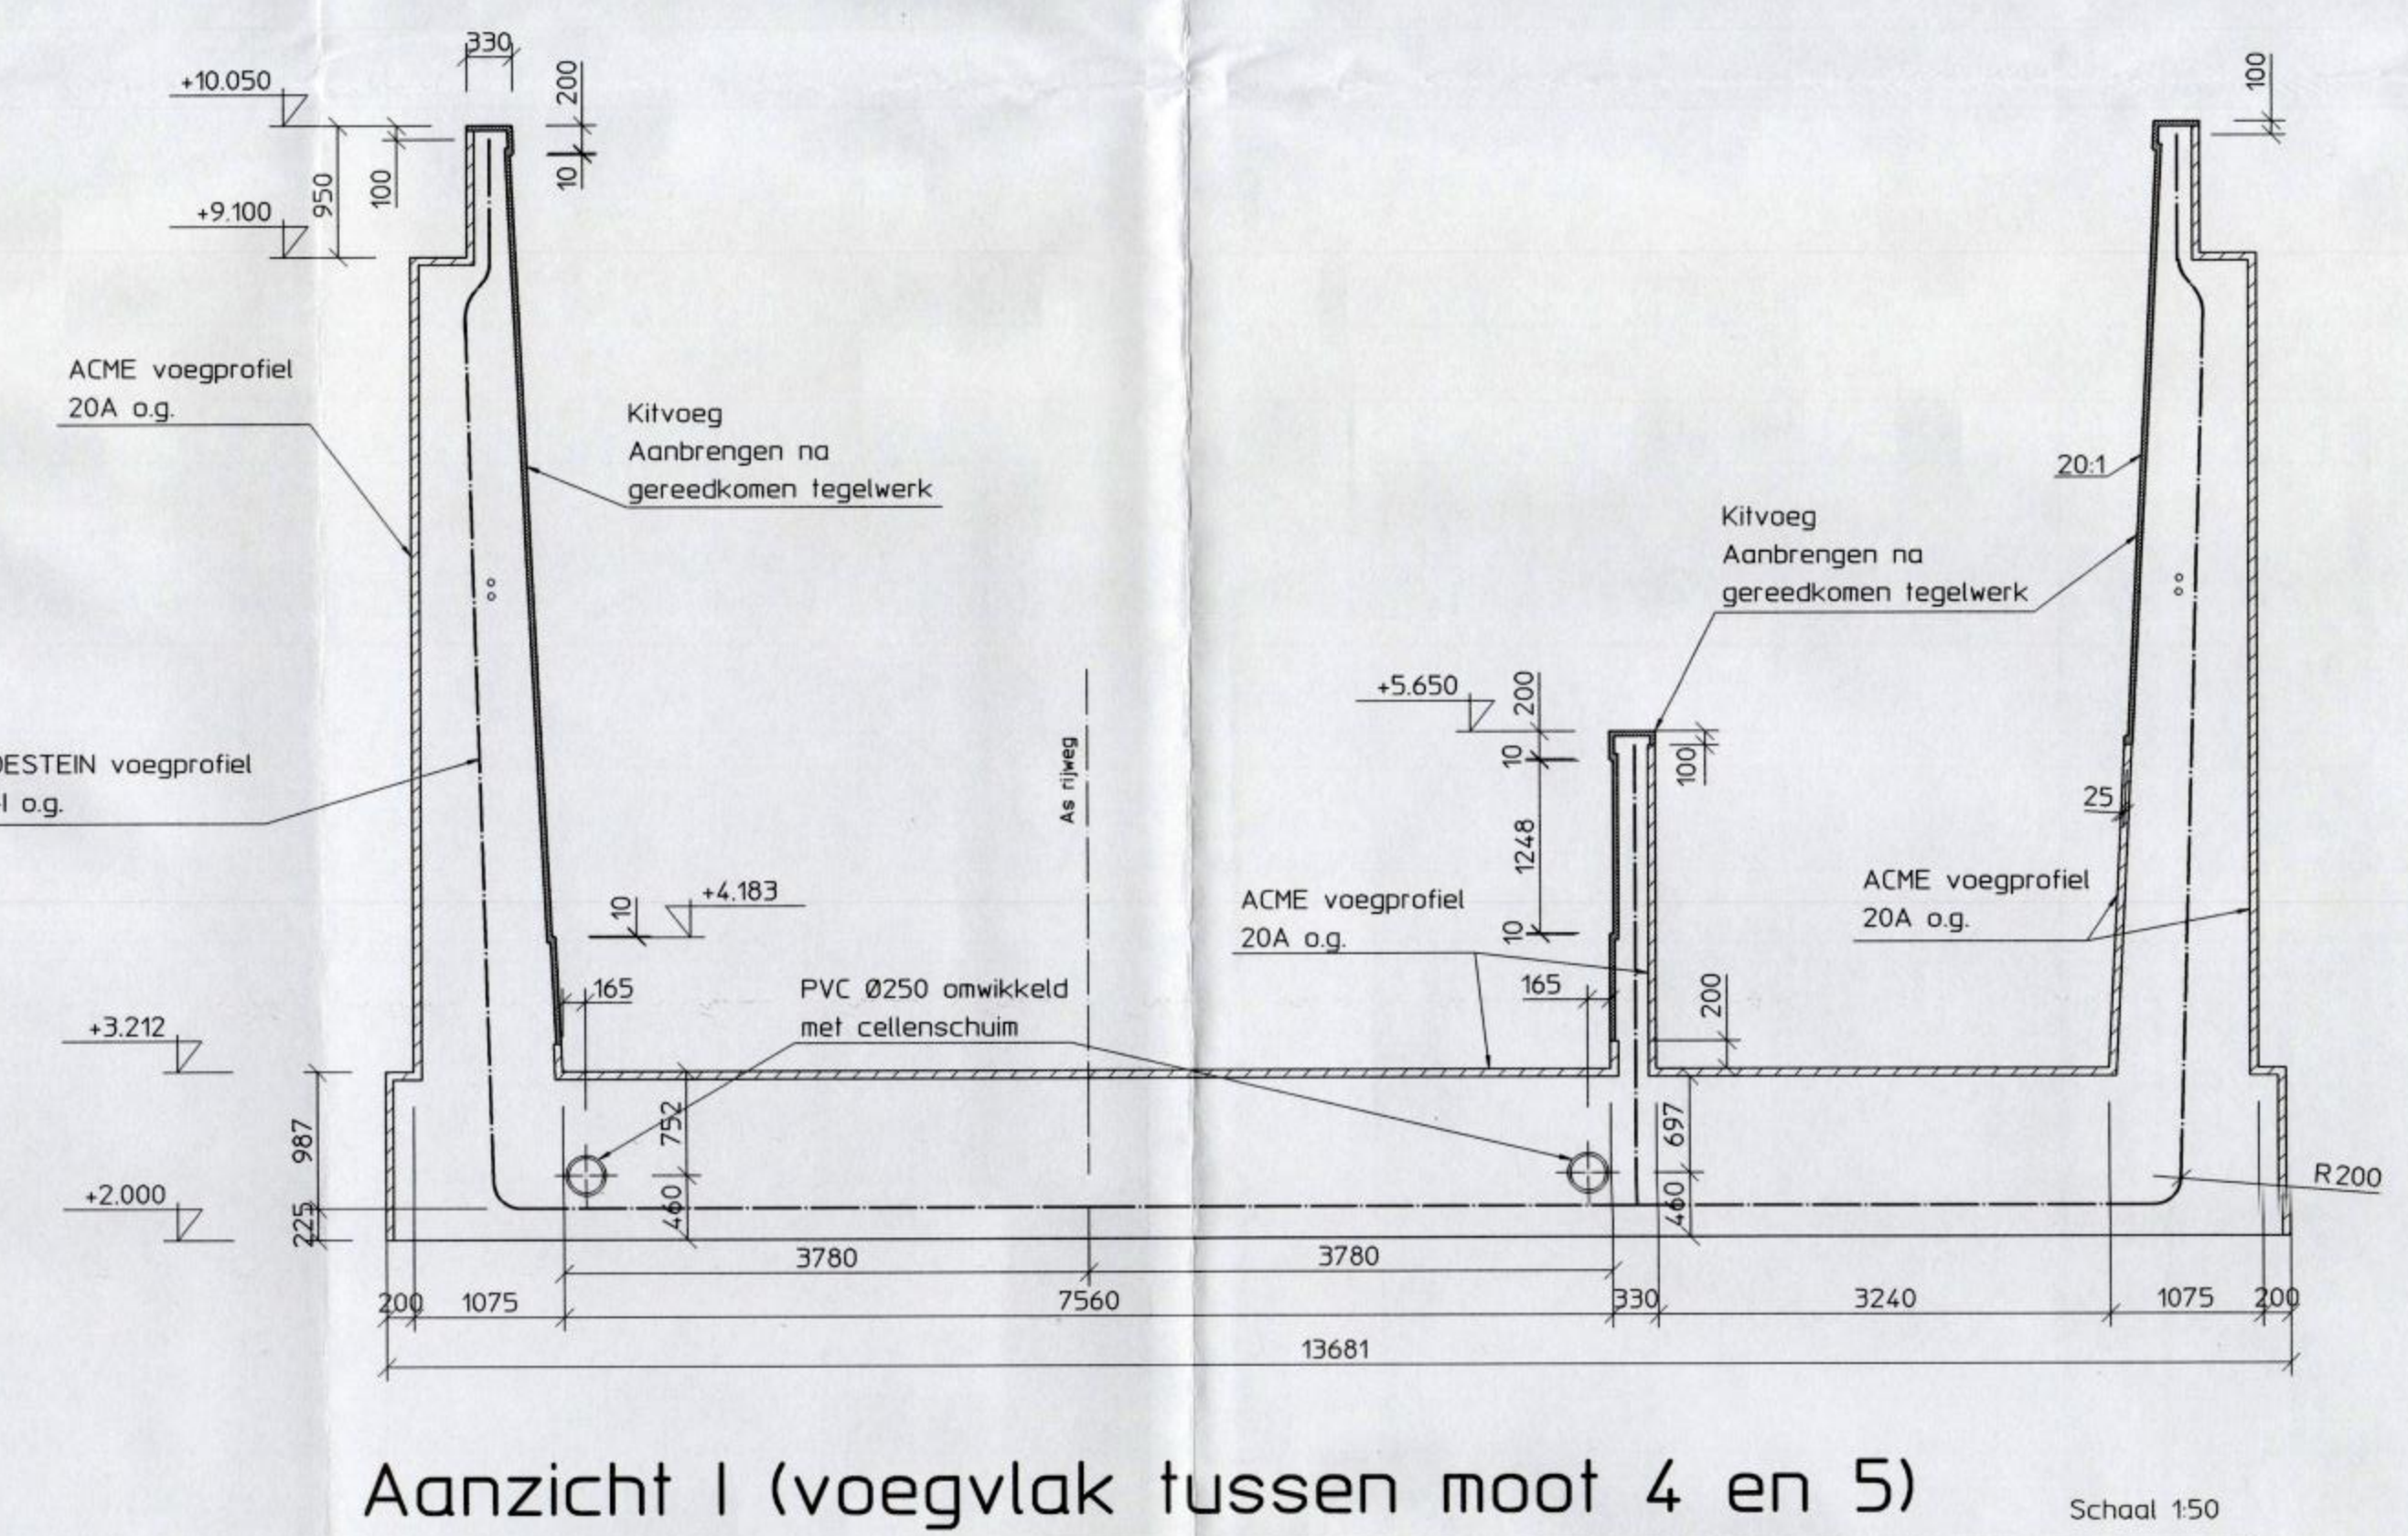
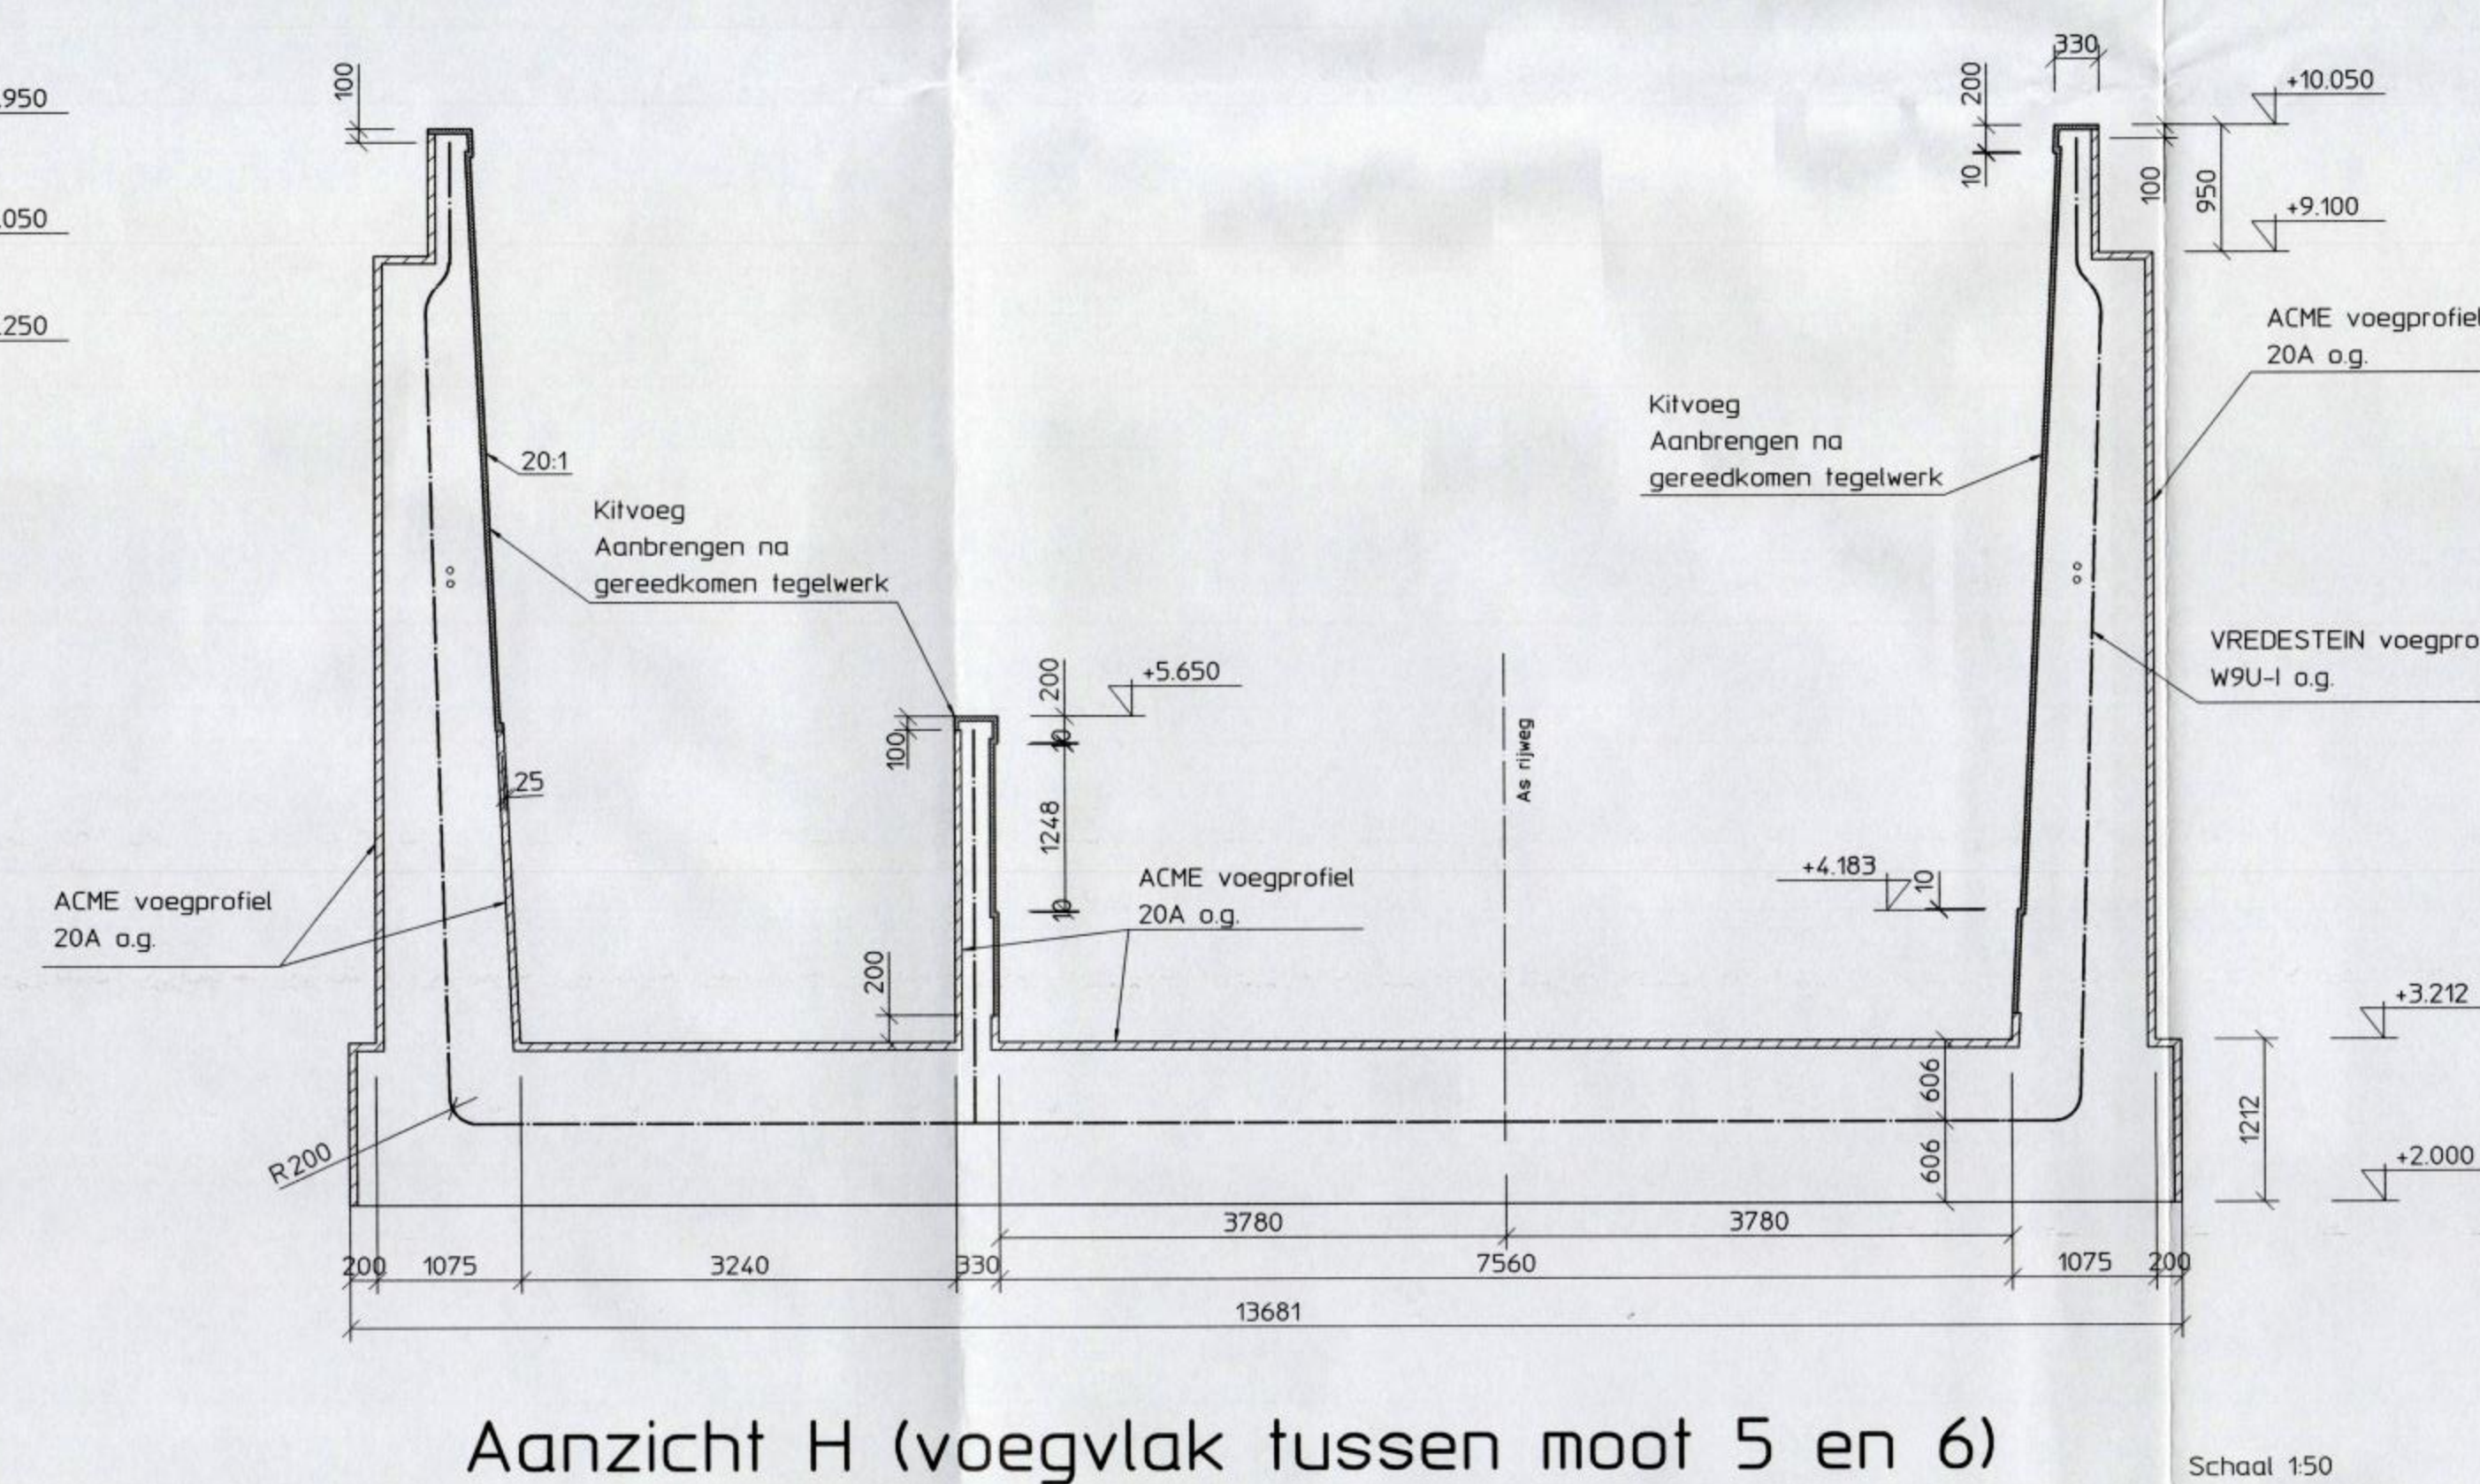
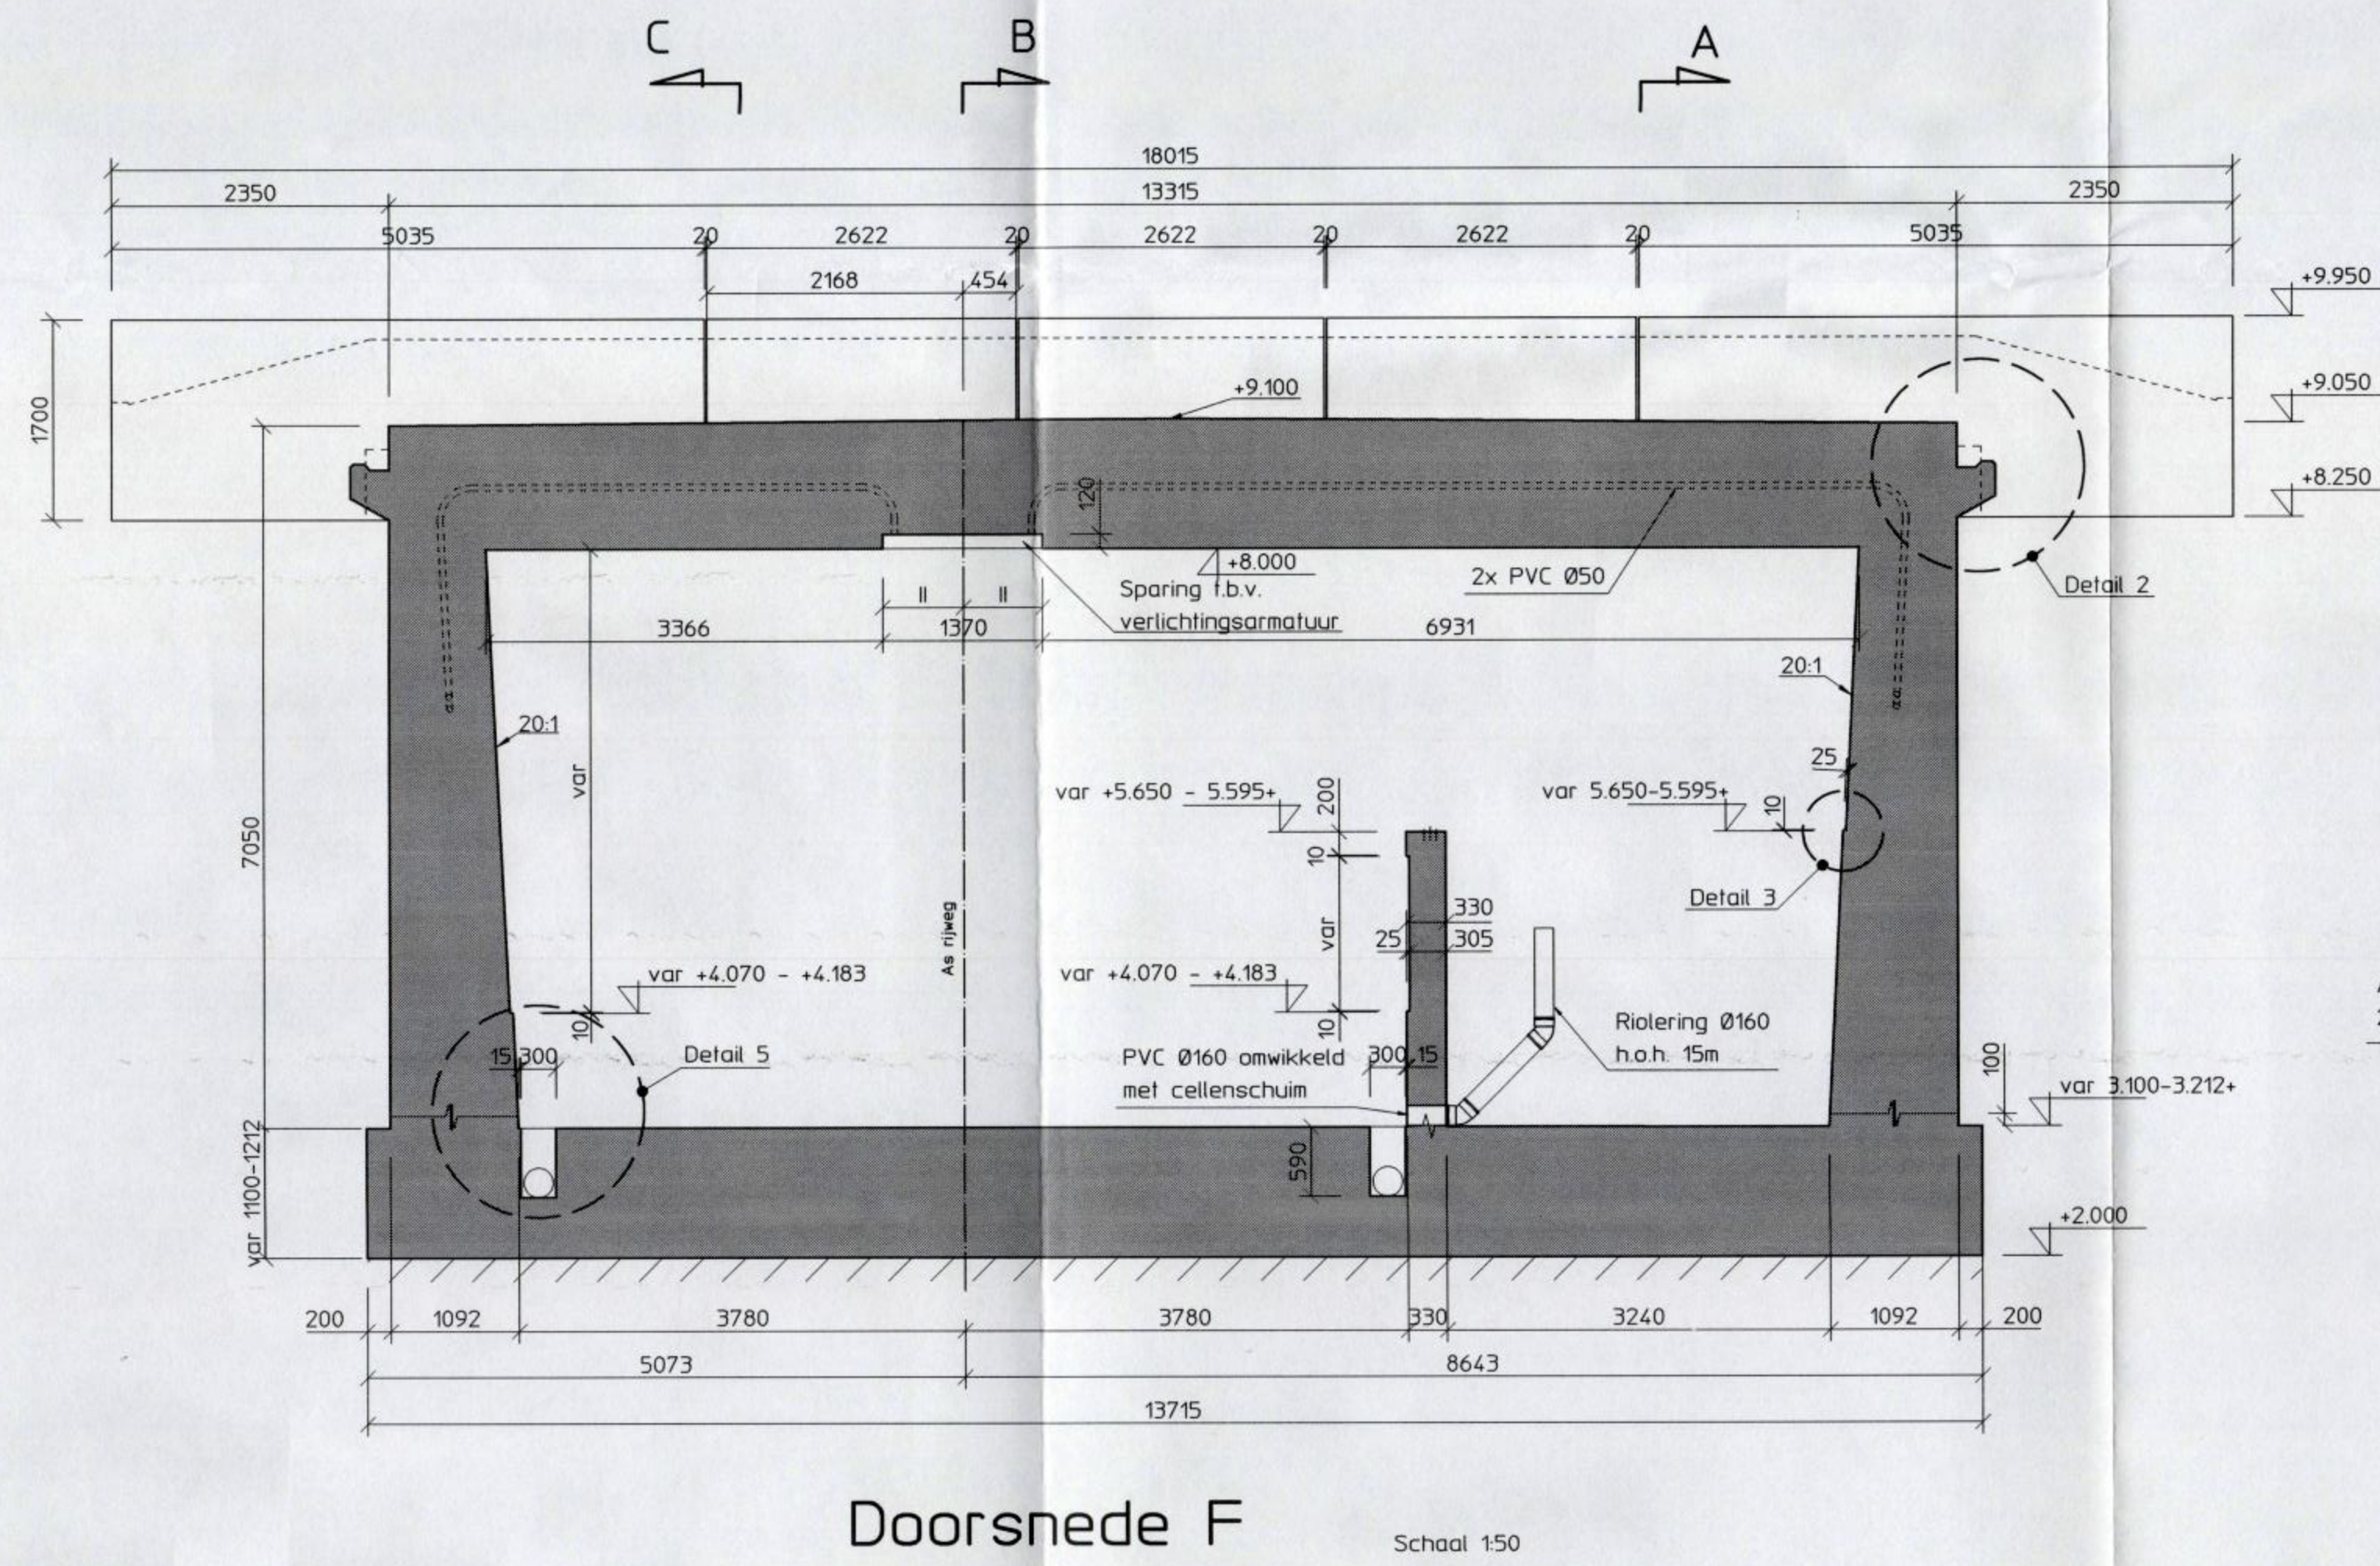
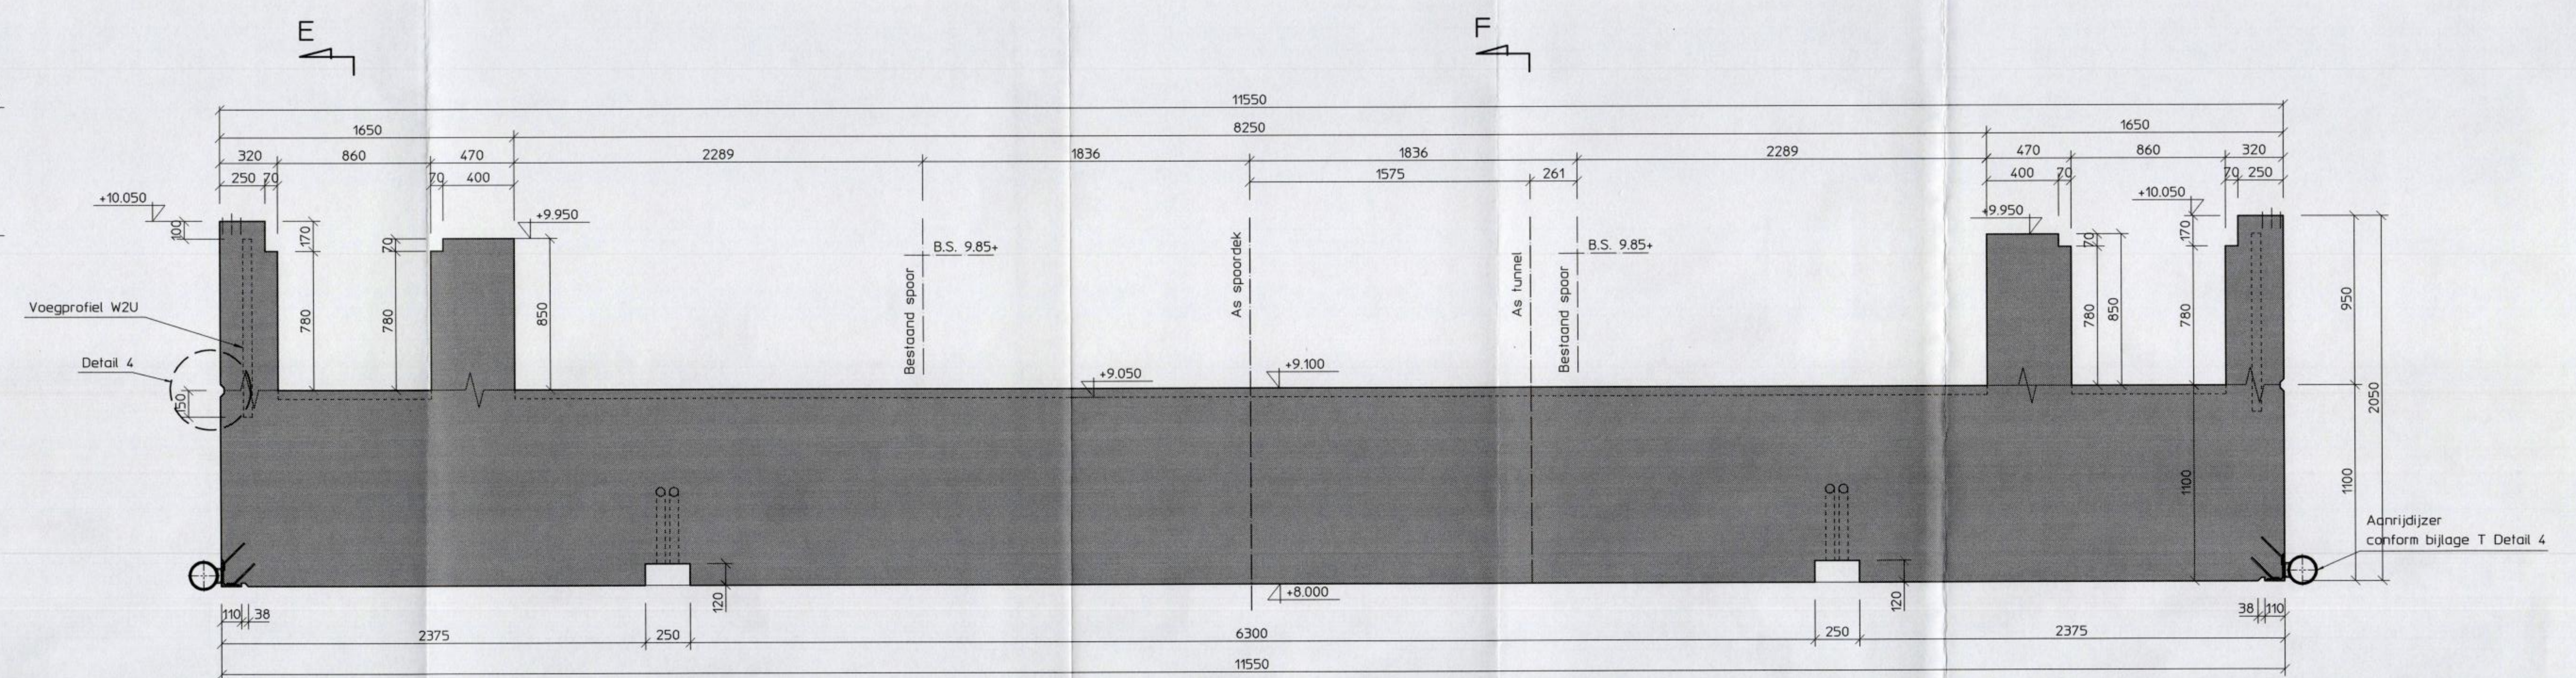
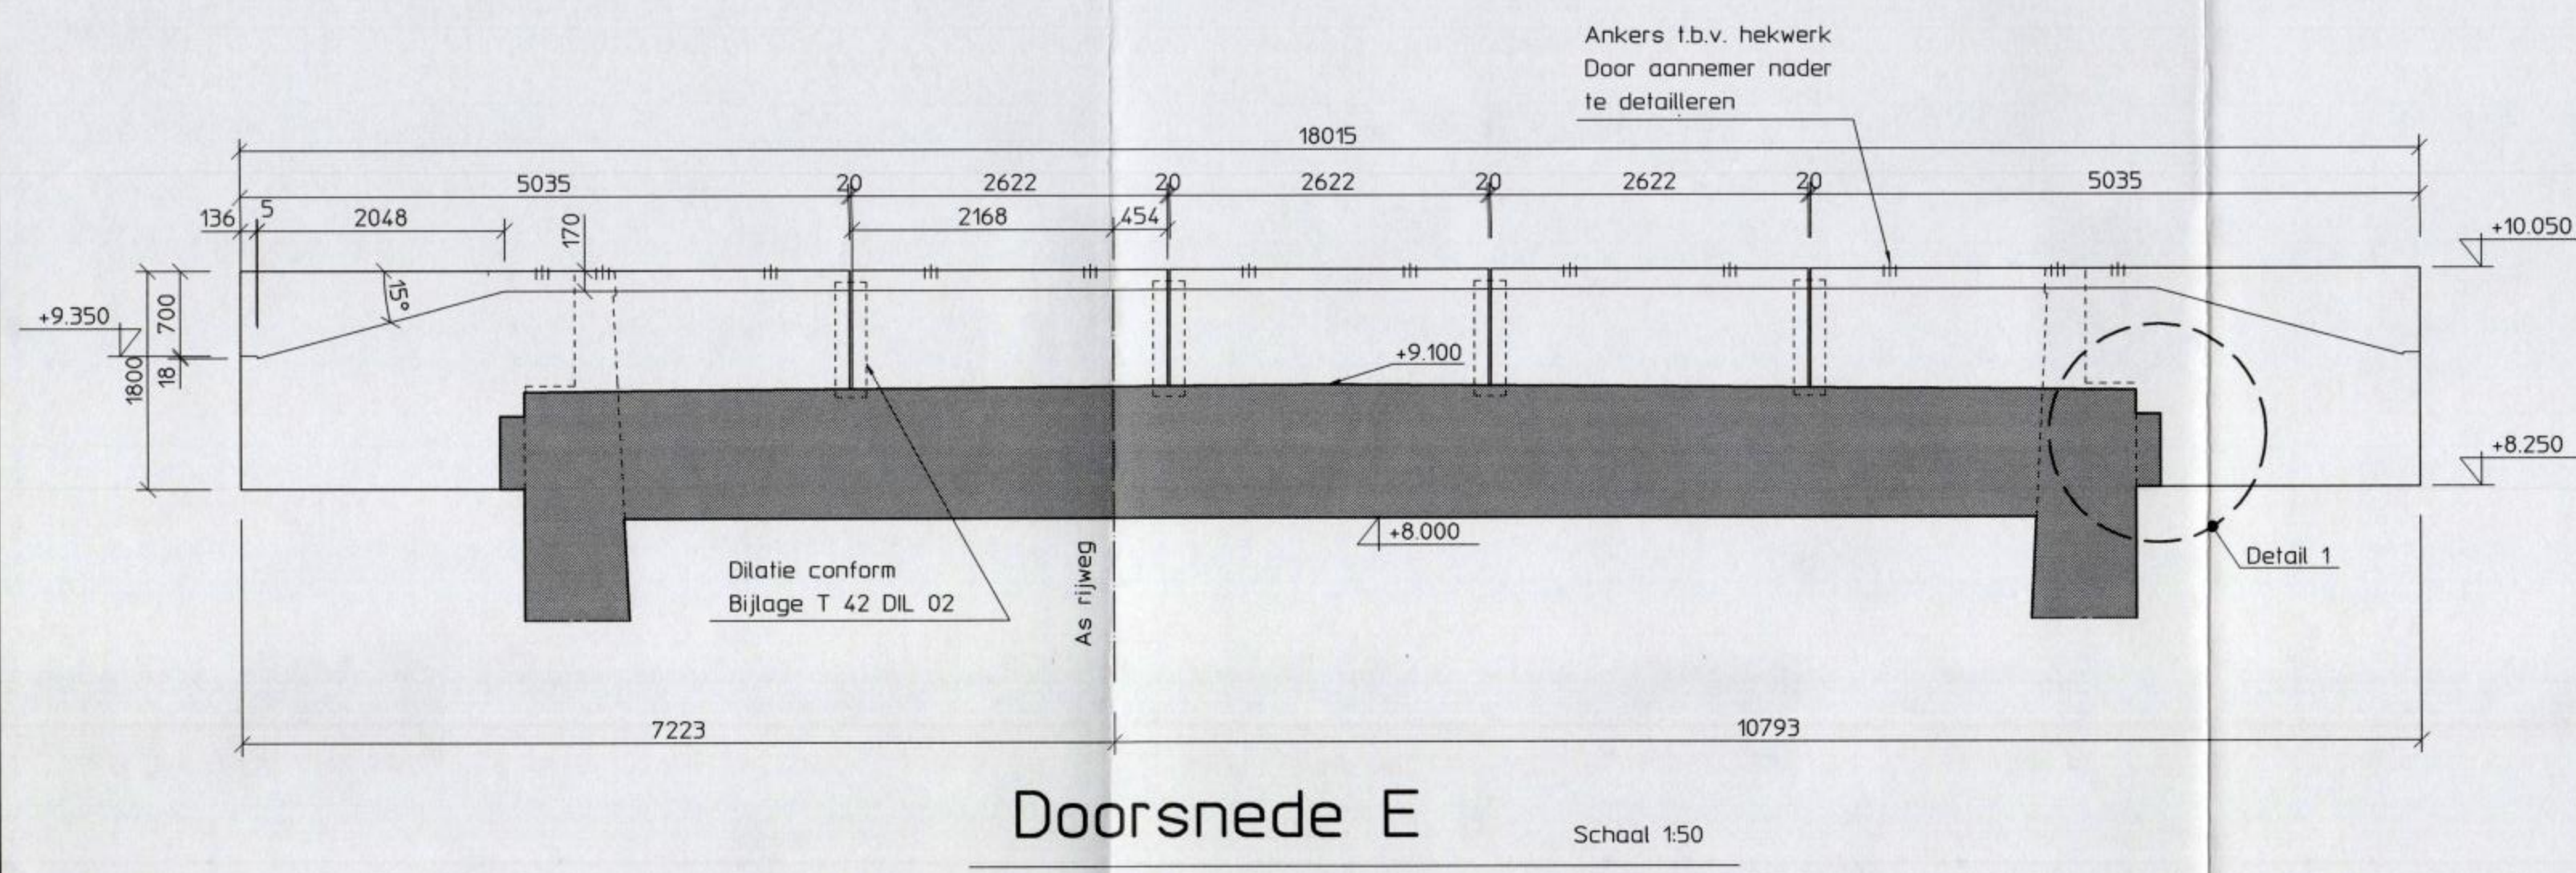


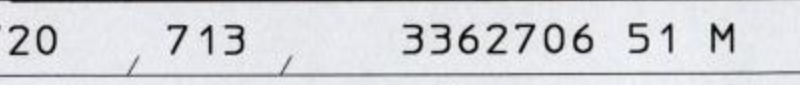

- maatvoering in mm
- hoogtemaatvoering in m t.o.v. N.A.P.
- voor bovenaanzicht en doorsneden A, B en C zie tek.3362706 50 M

(Status: REVISIE d.d. 17-12-1999 14:49:06)

noan		par	datum	Maatvoering Mael 5 Blad 2		
galekend	M.W. Griller # de Boeck		17-12-99			
proiectide	C.F. Venk					
proiectre	3362706	versie	10			
bestekne	V00B/09450			NS Railinfraabeheer Regio Zuid Gilze Rijen Onderdoorgang Europaalaan		
formaat	A0					
schoal	ze Nek.					
420		123	11.720	713	3362706	51 M
VA, CT PG 82 Postbus 2855 3500 KH Utrecht Telefoon 030 - 235 89 58 Telefax 030 - 235 72 12 E-mail: info@hollandrailconsult.nl						
						
plaatsen / Am0_dwa1c1r123xw0t1720p3362706/c047u51v / M.W. Griller # CT A80G 1 23-bf-1999 13.6.28						