



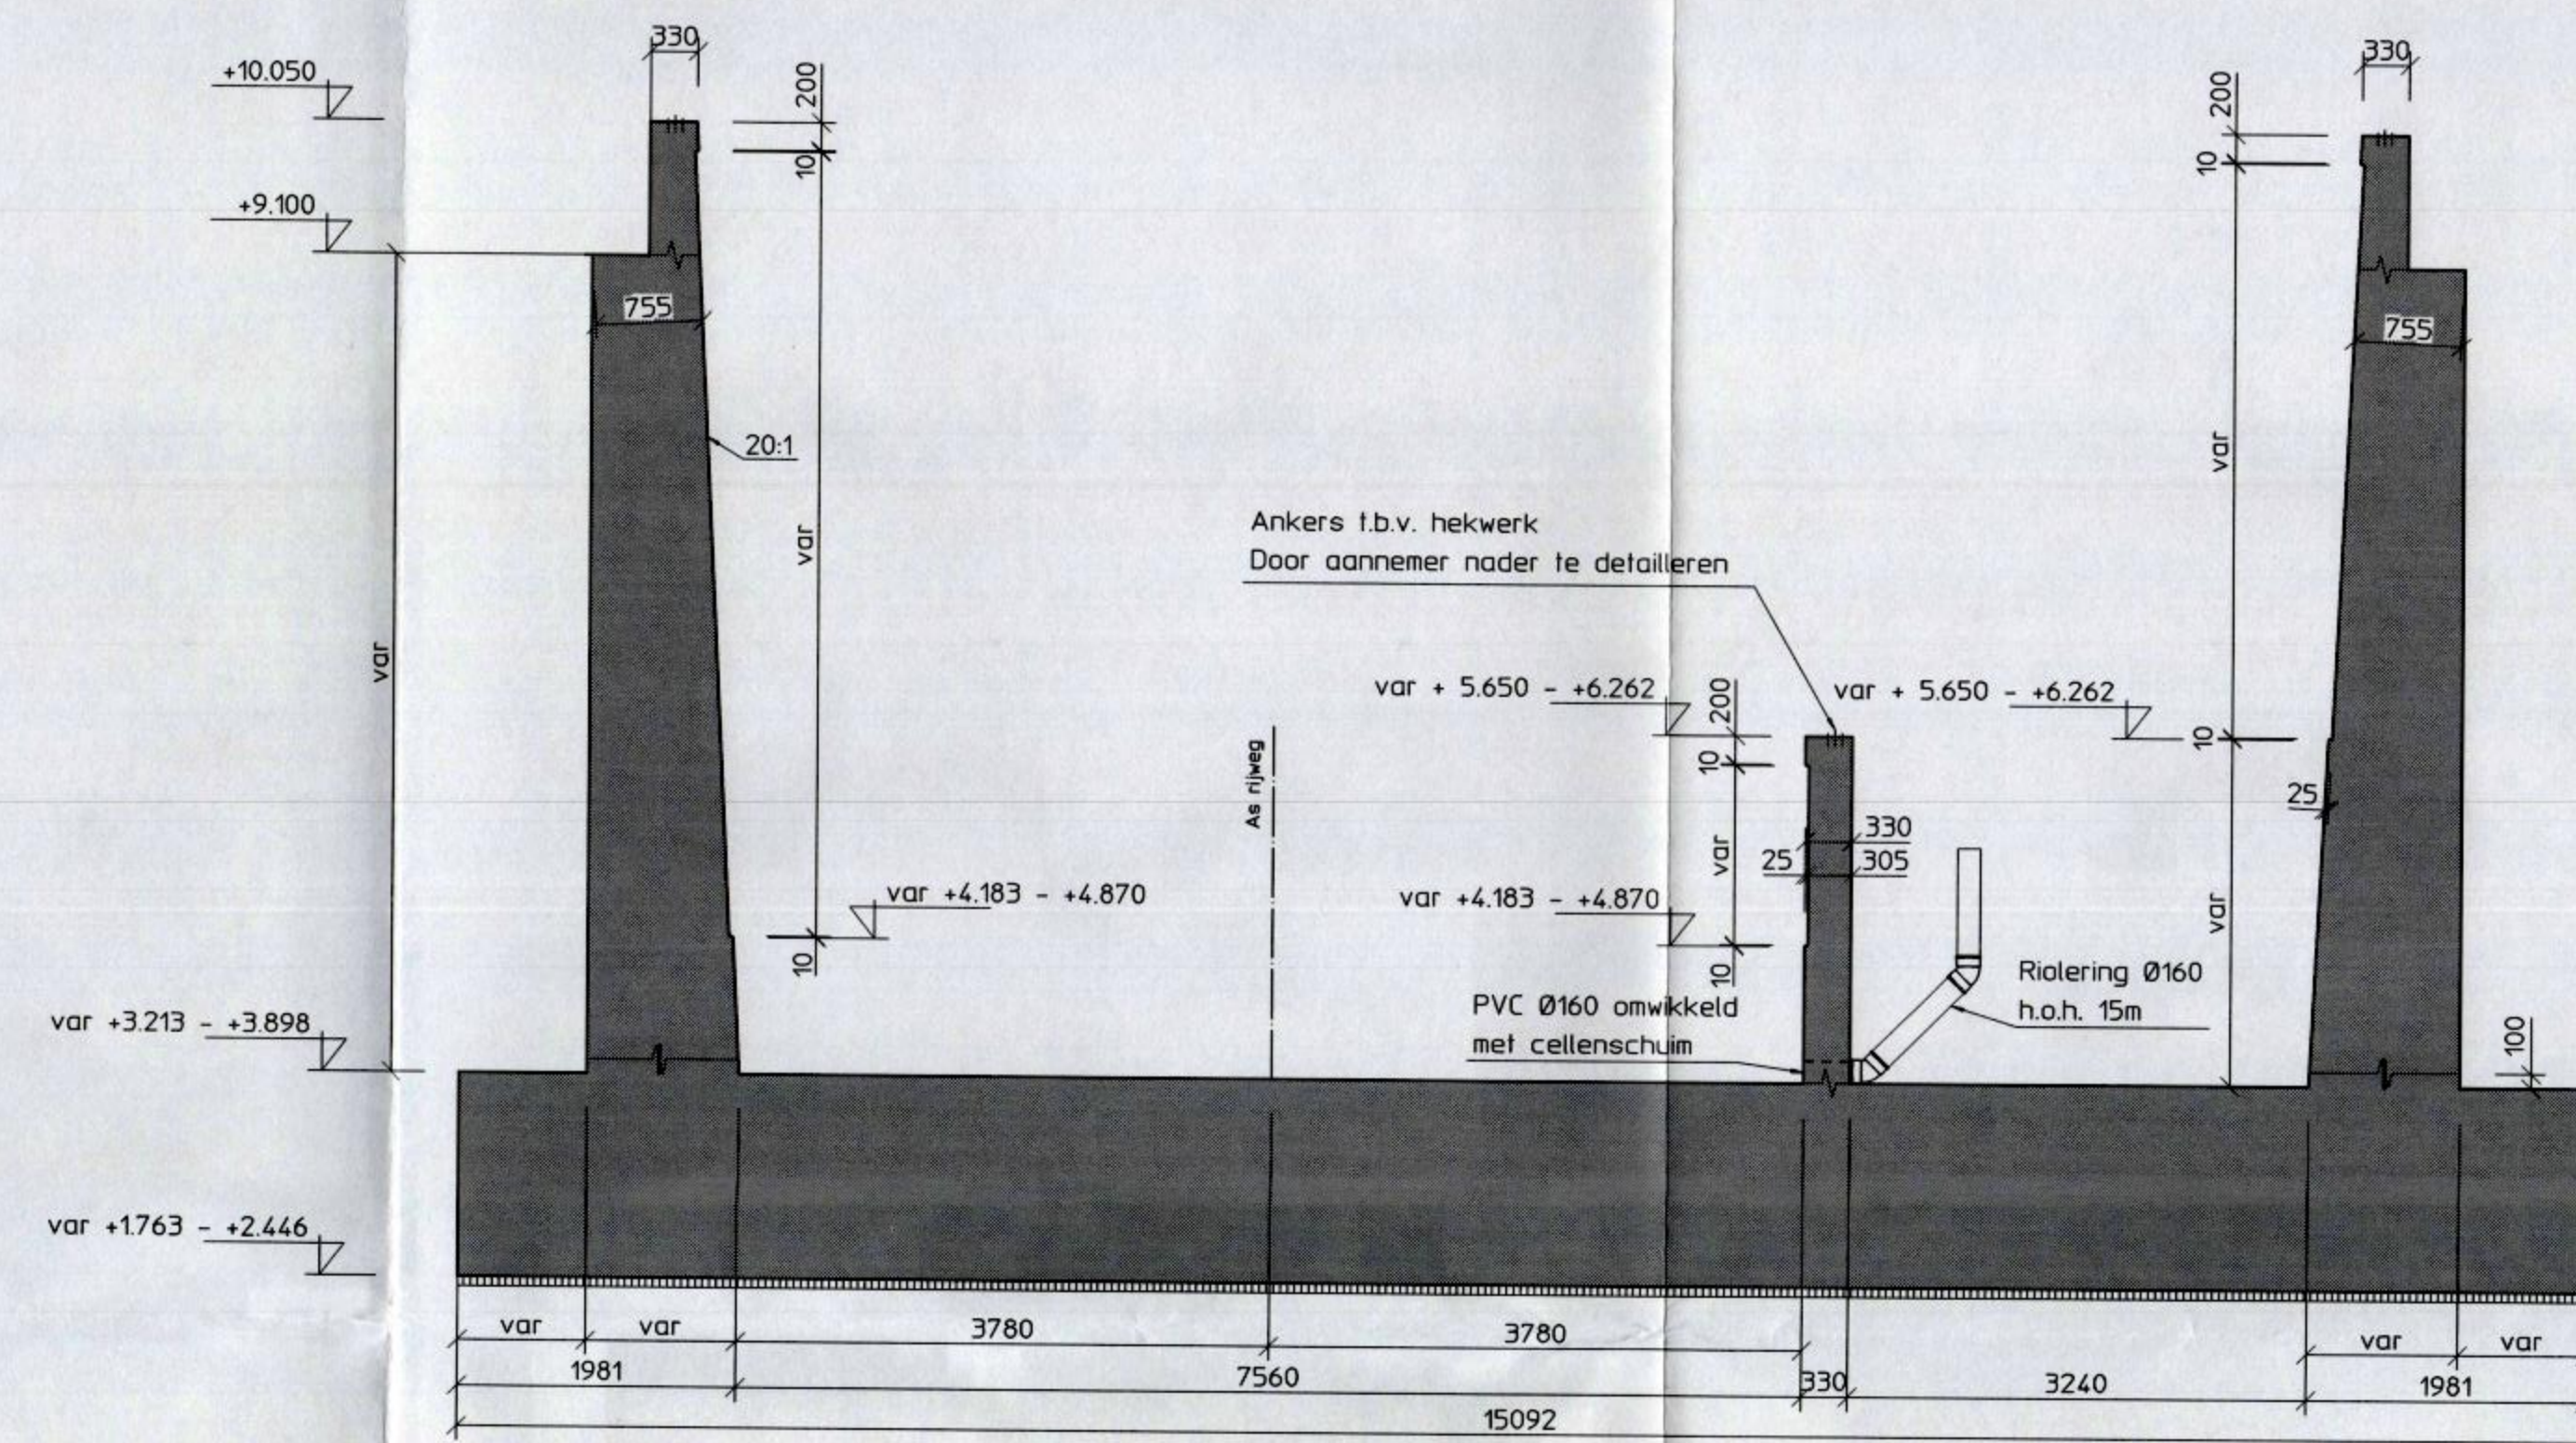


Doorsnede D

Schaal 150

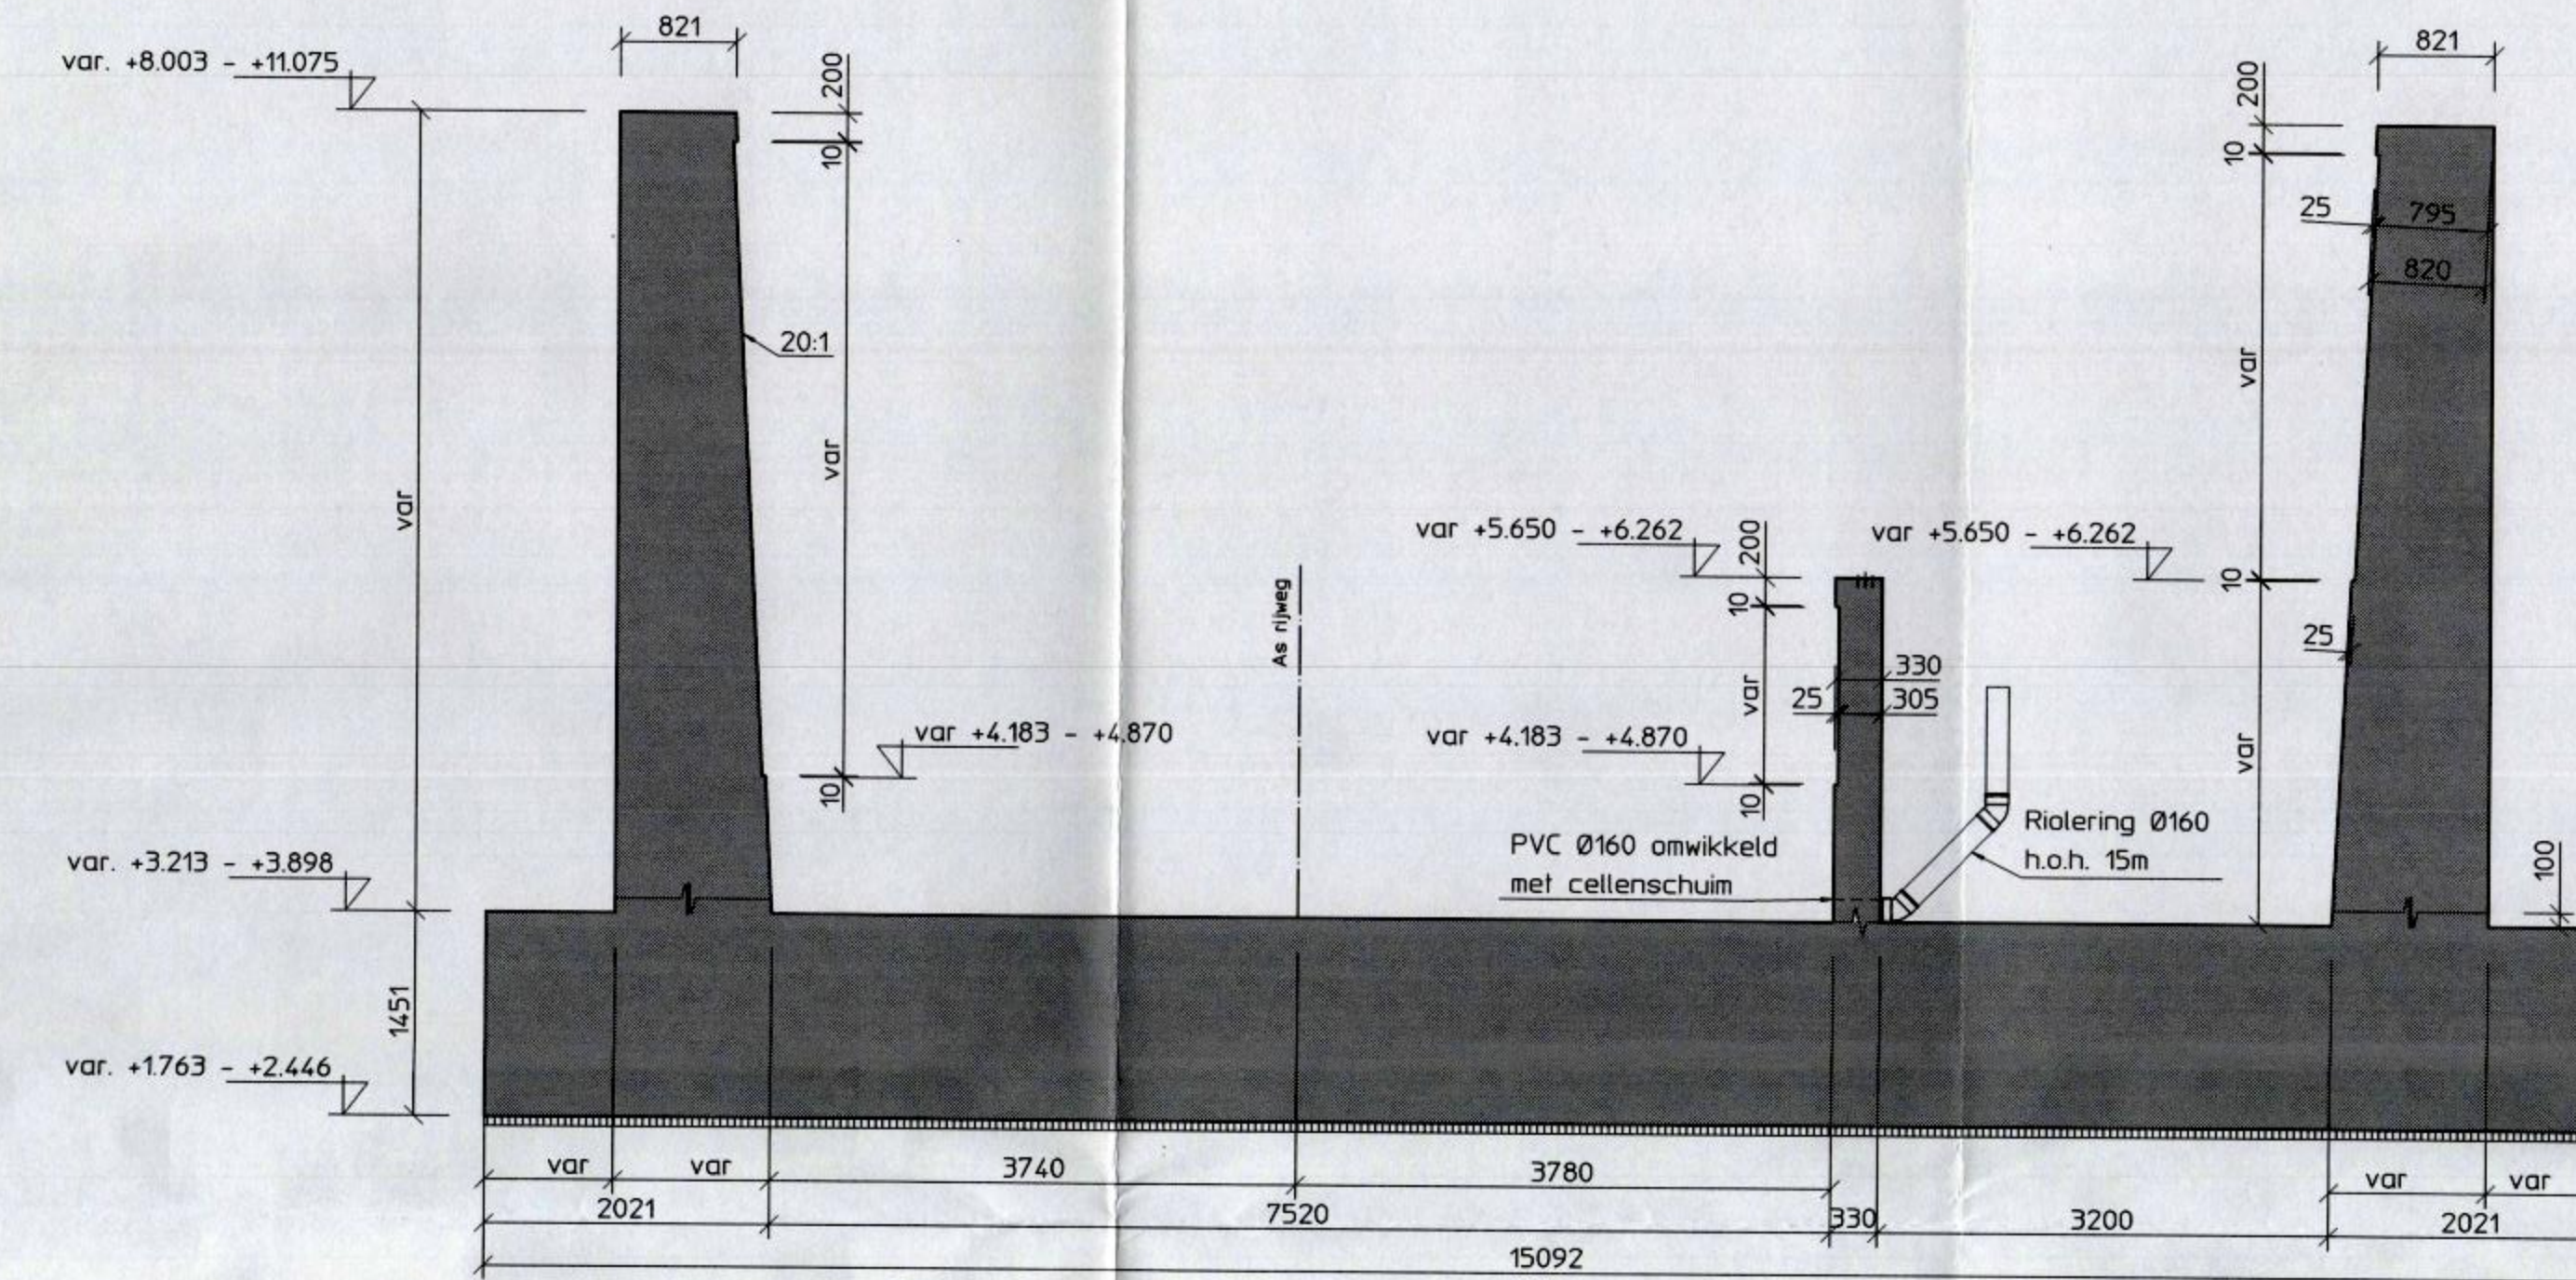


Doorsnede E

Schaal 150

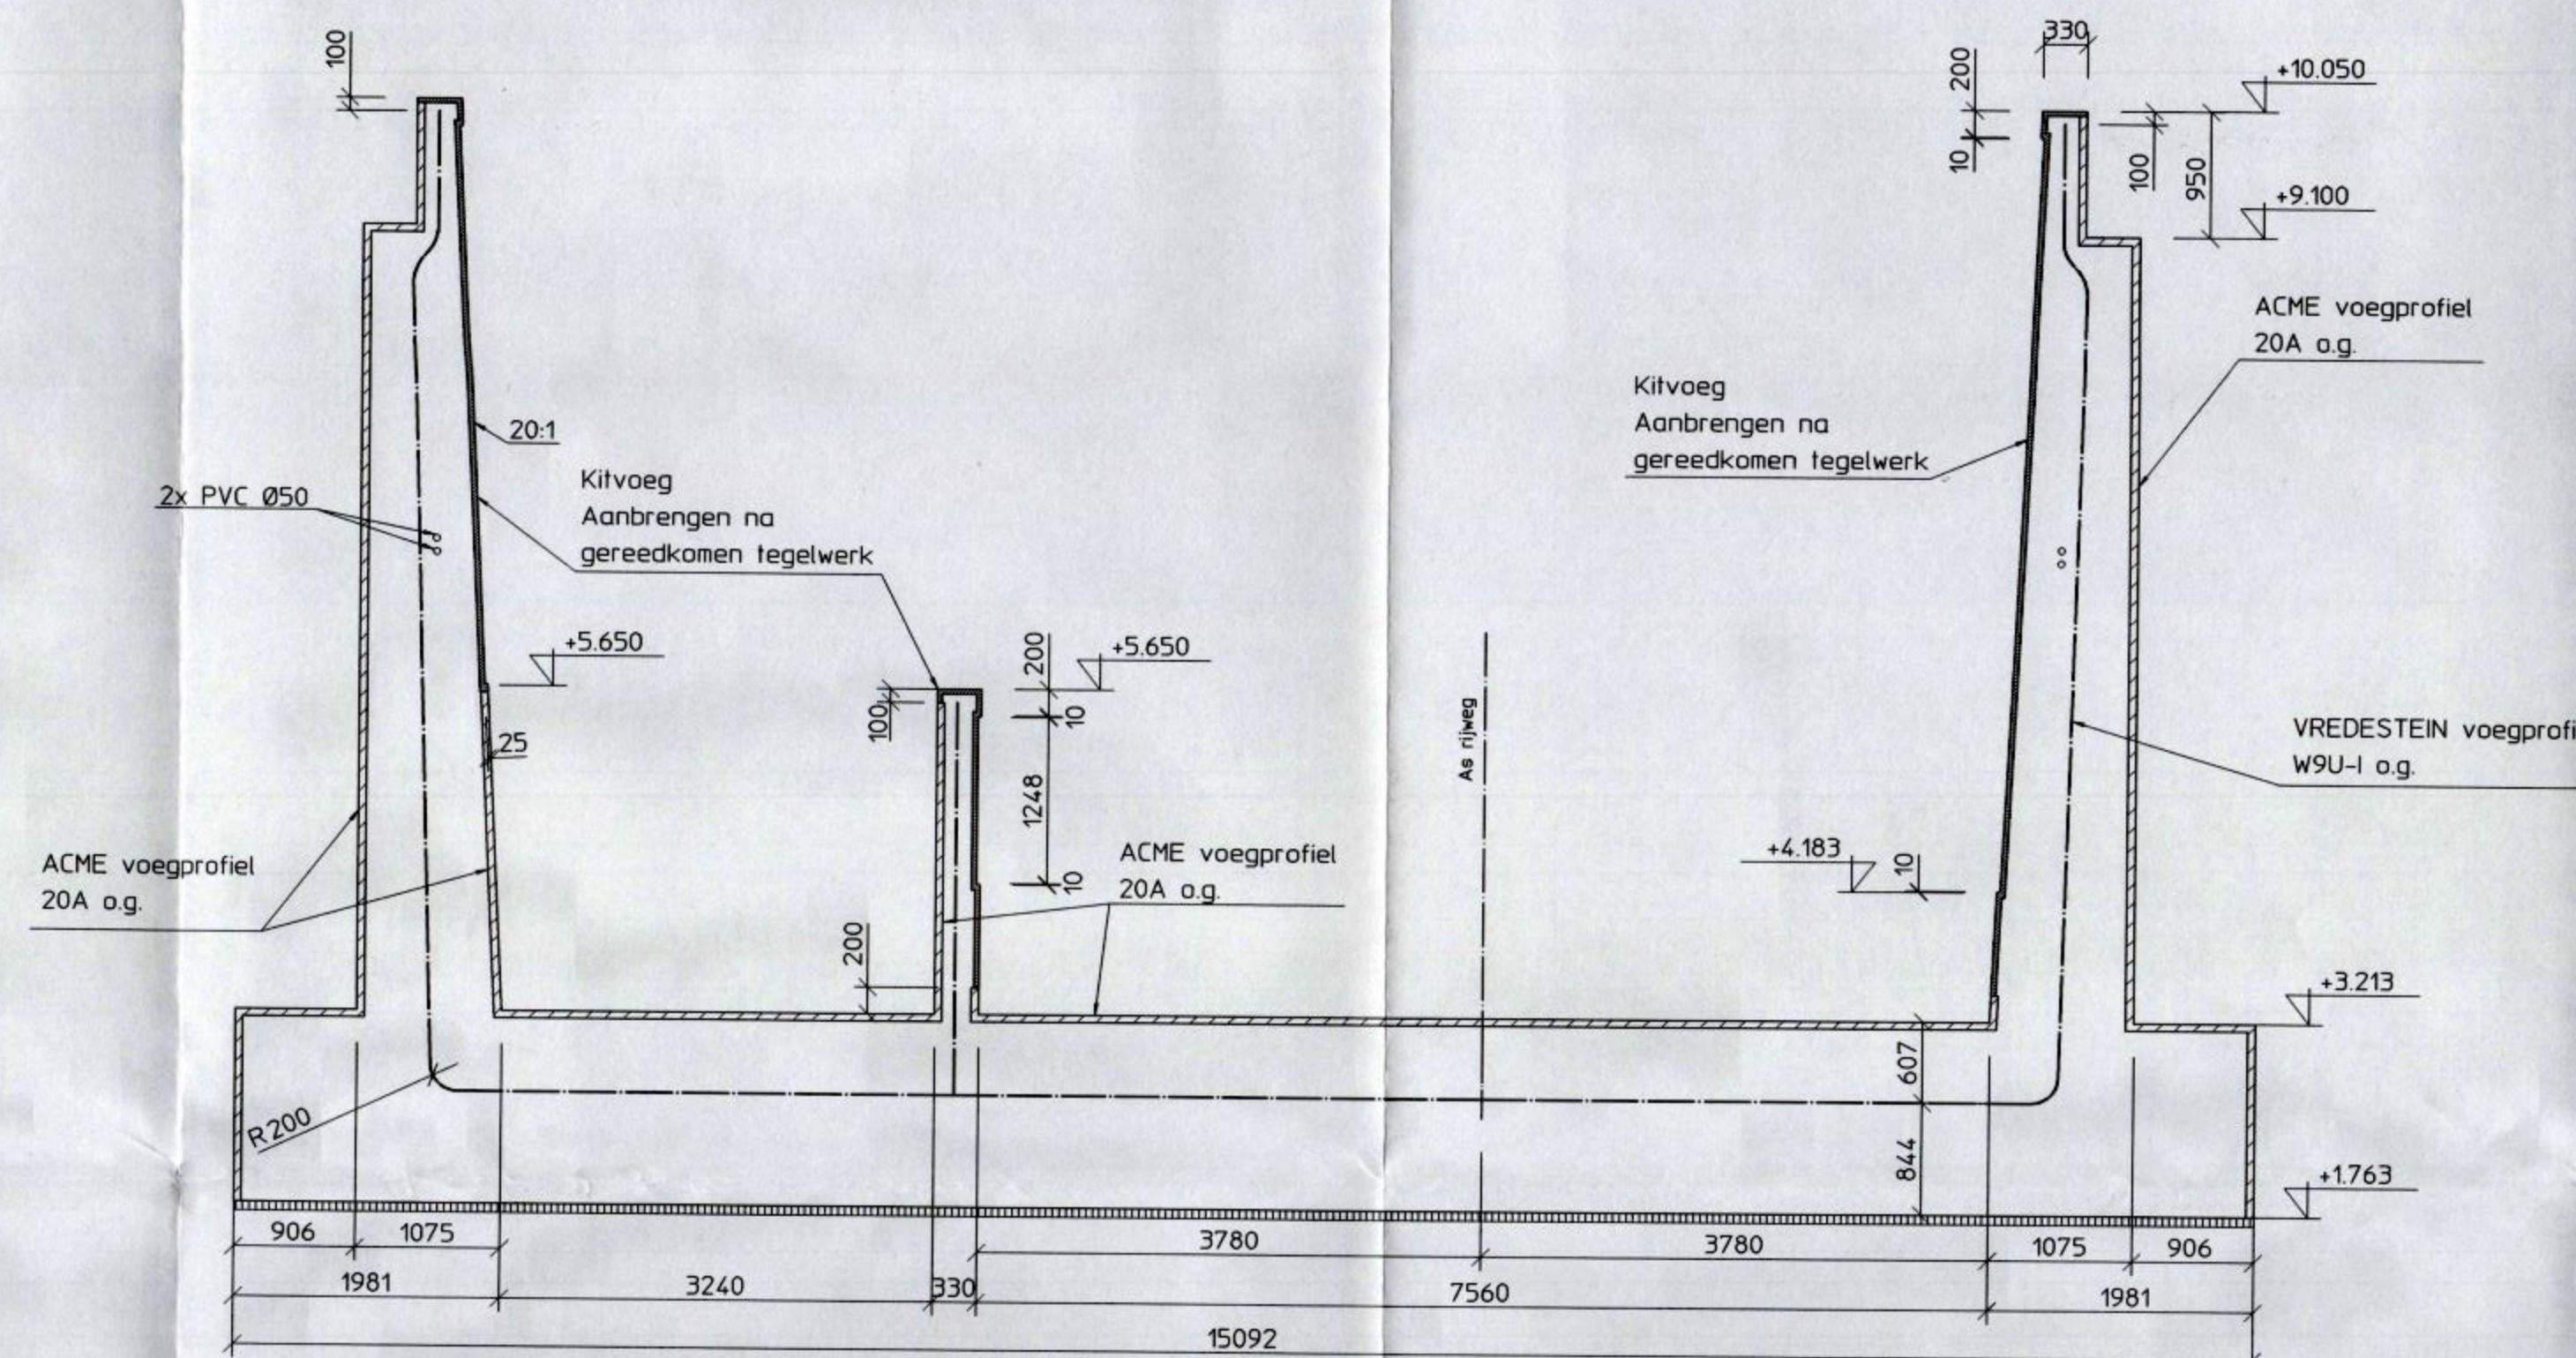


Aanzicht F

Schaal 150

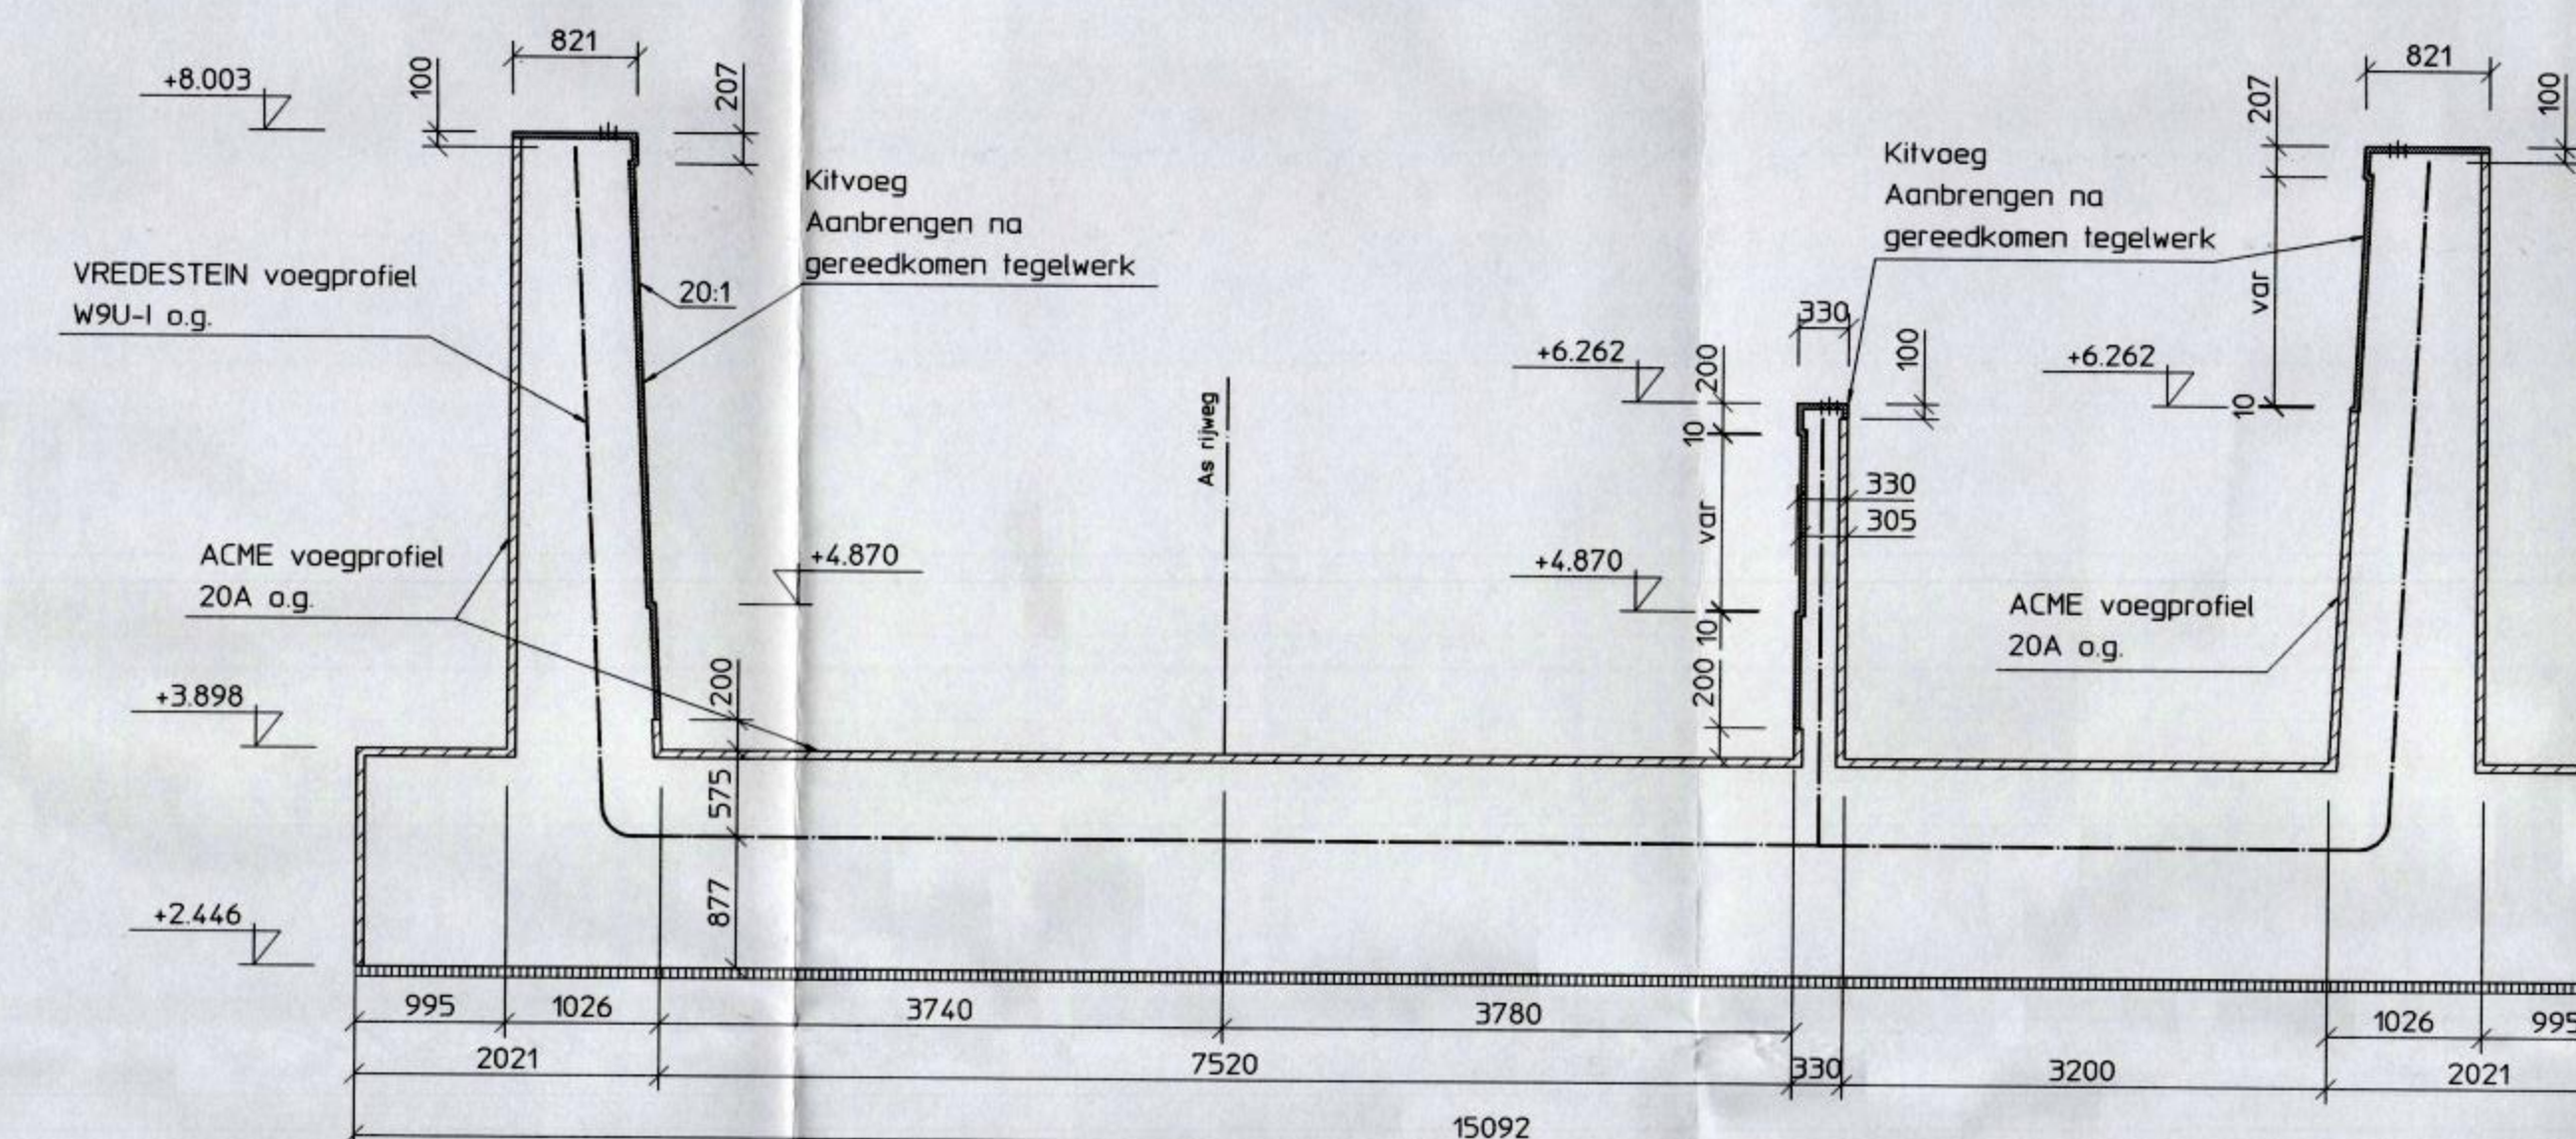

Aanzicht G

schaal 150

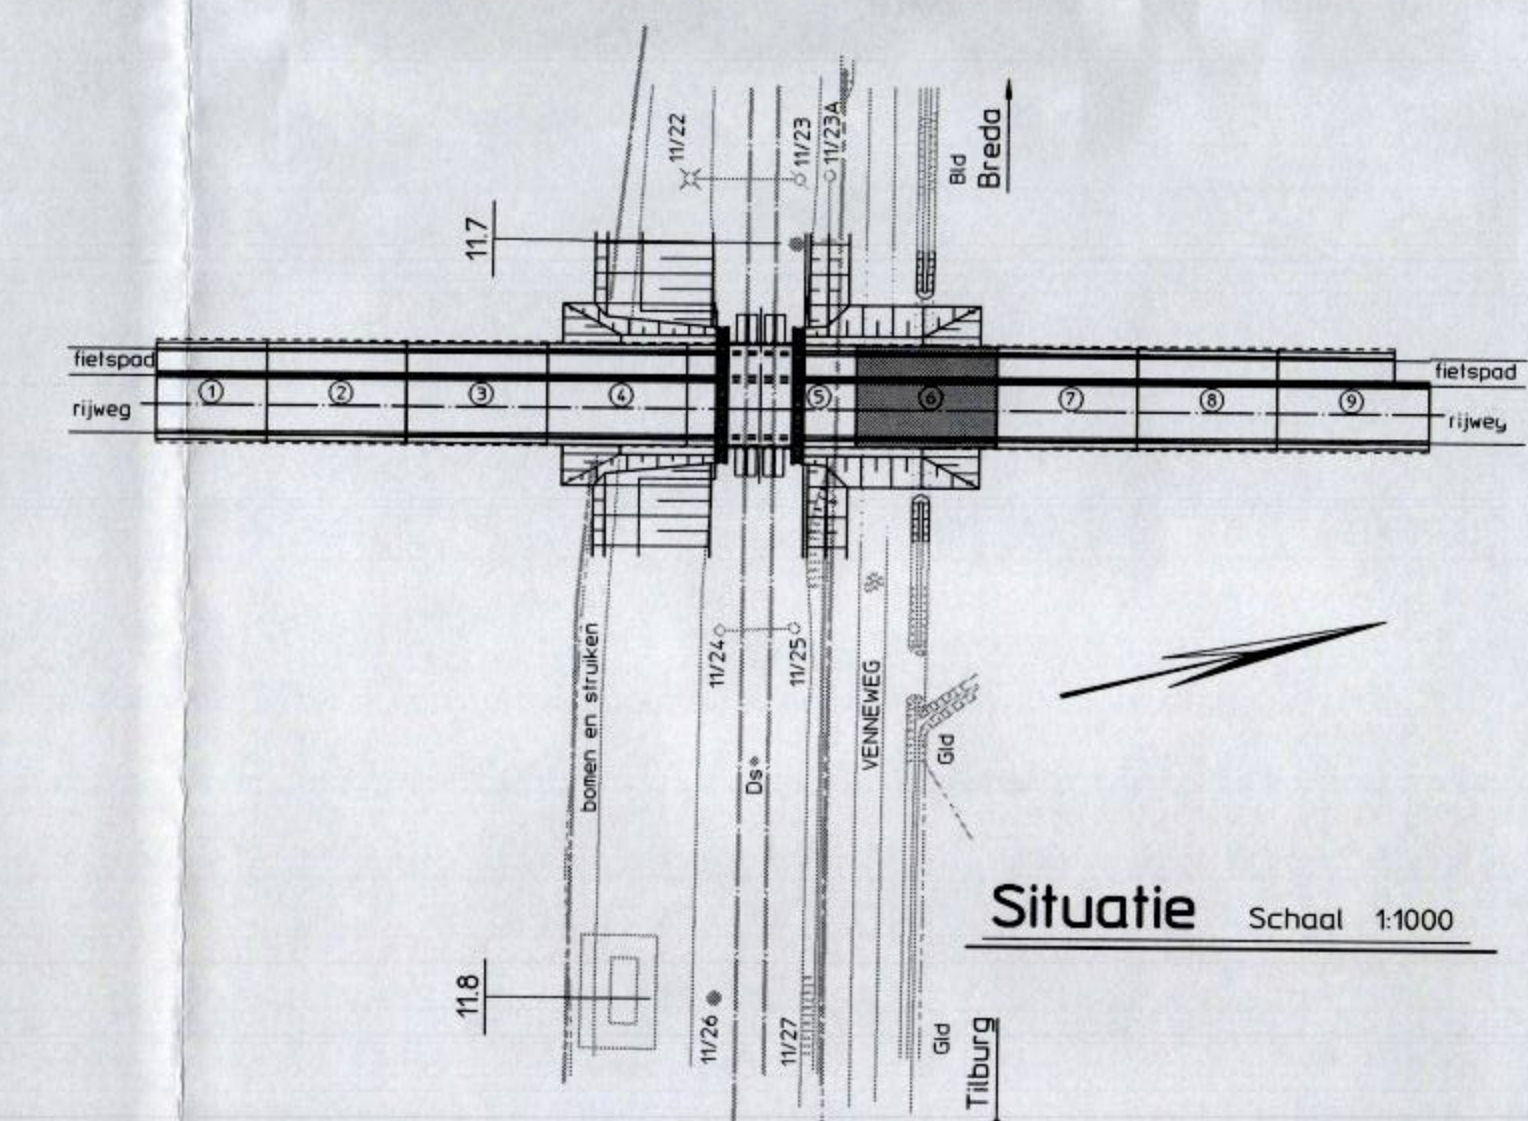

Situatie

Schaal 1:1000

- maatvoering in mm
- hoogtemaatvoering in m t.o.v. N.A.P.
- voor bovenaanzicht en doorsneden A t/m C zie blad 3362706 60 M

(Status: REVISIE d.d. 17-12-1999 14:52:29)

naam	par	datum	Maatvoering maat 6 Blad 2
getekend H.W. Gritter	17-12-99		
projectleider C.F. Vink			
projectnr 3362706	versie 1.0		
bestelnr V008009450			
formaat A0			
schaal zie tek.			
VA CT PG 82 Postbus 2855 3500 DR Utrecht Telefoon 030 - 235 89 58 Telefax 030 - 235 72 29			
420	123	11.720	713
			3362706 61 M
Holland Railconsult			