



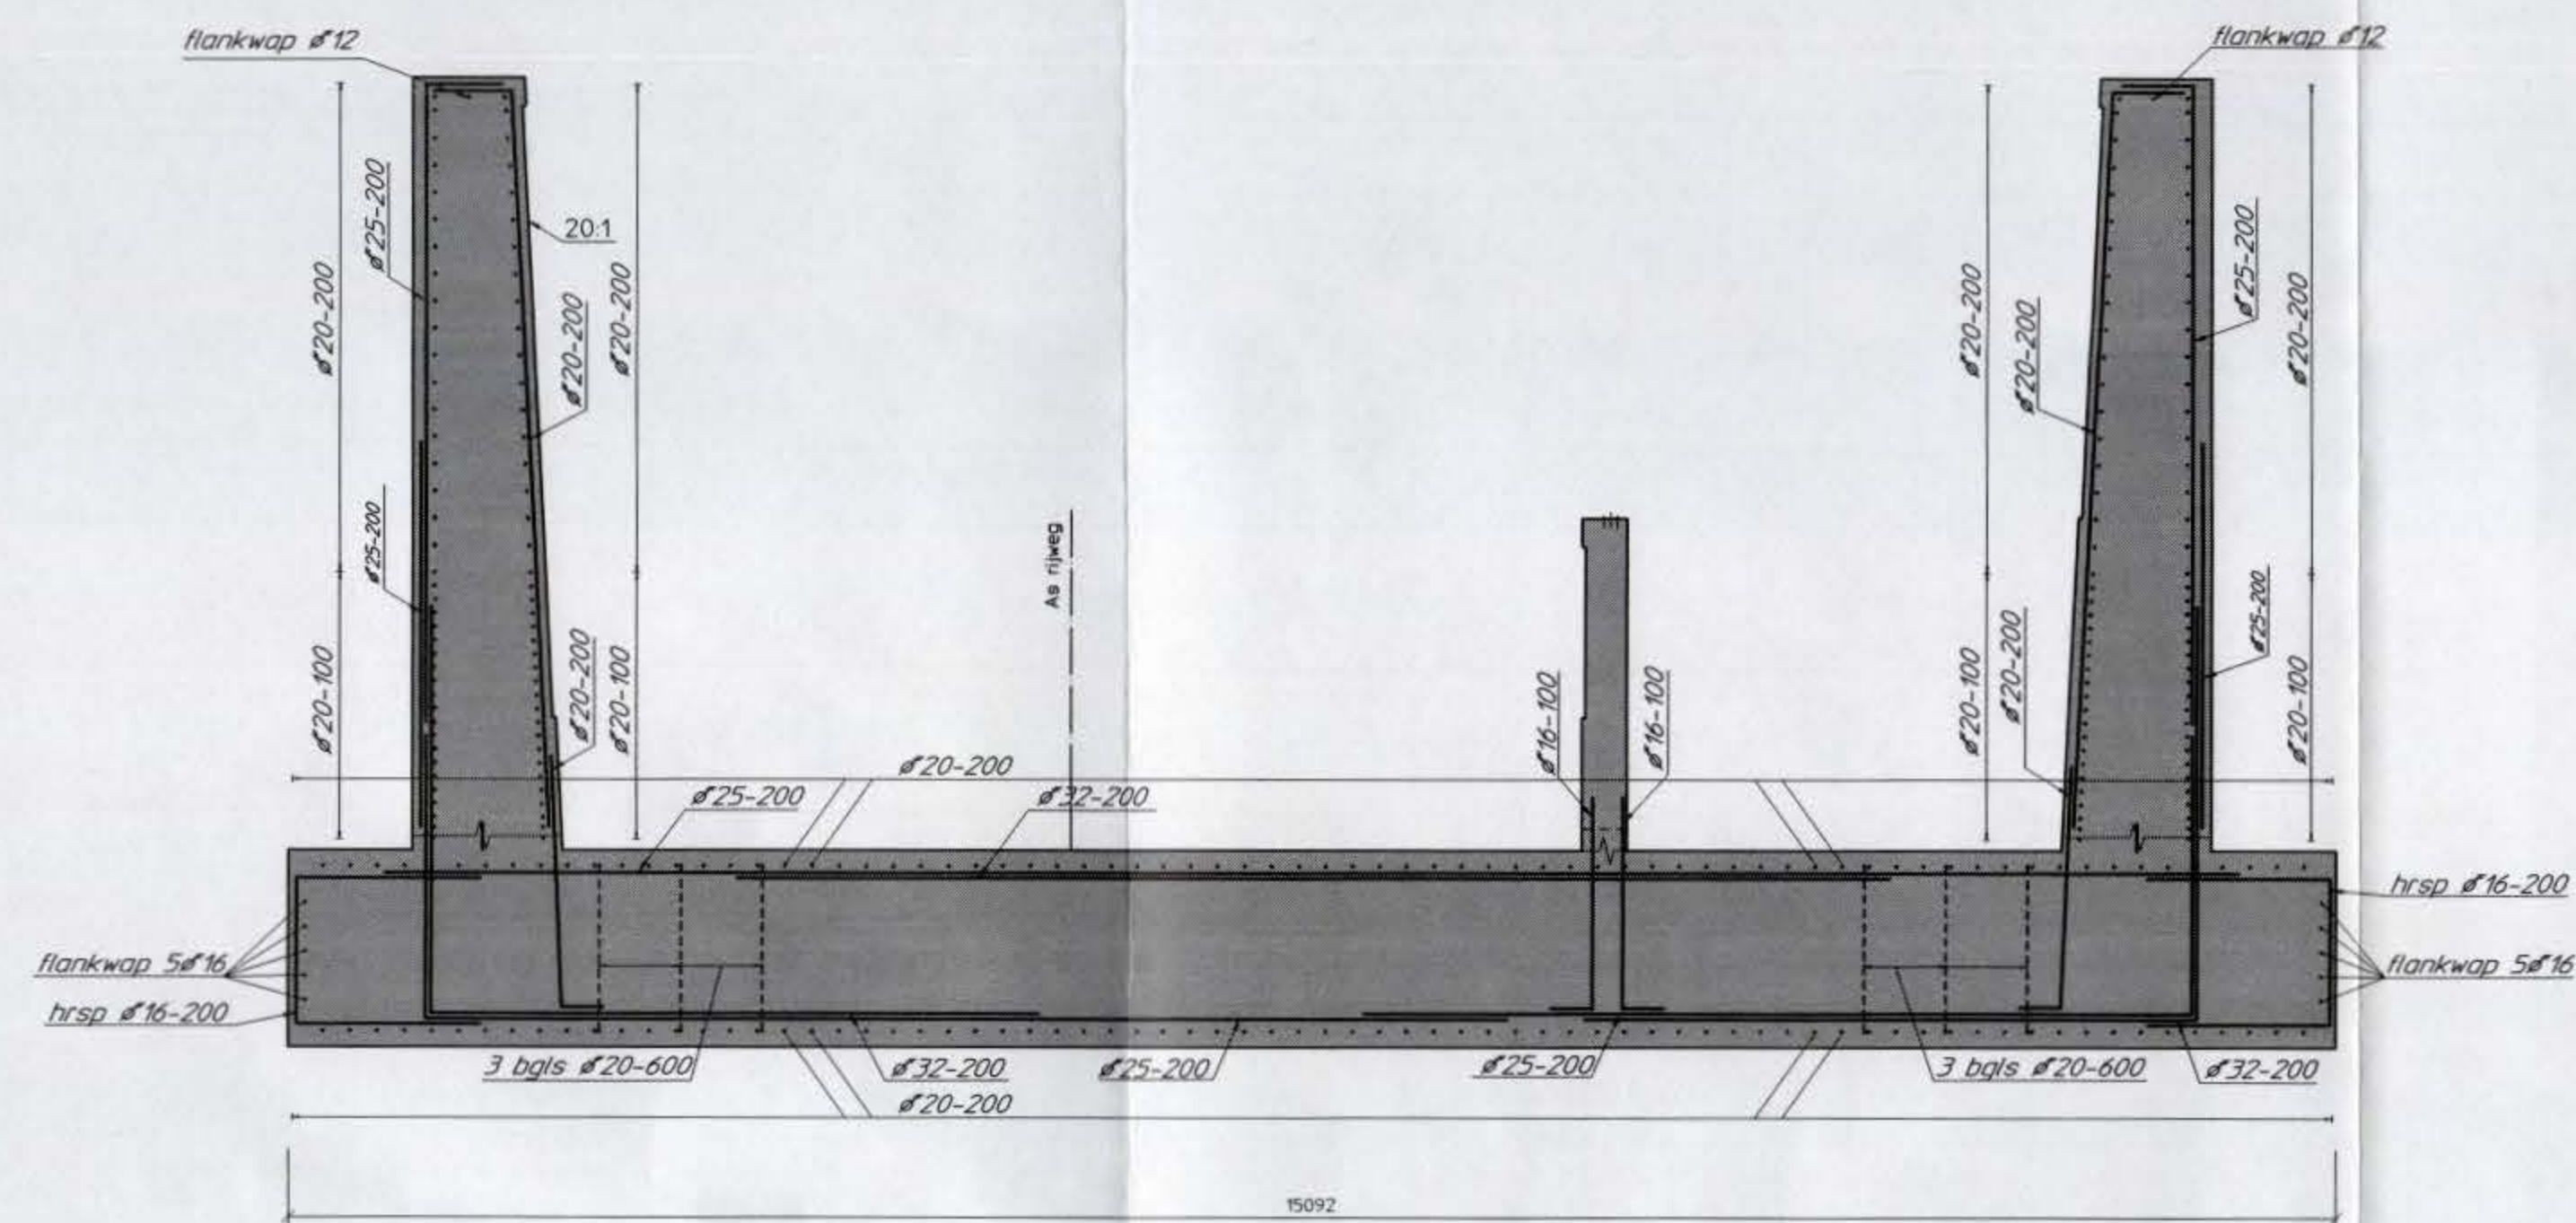


Doorsnede E-E

Schaal 150

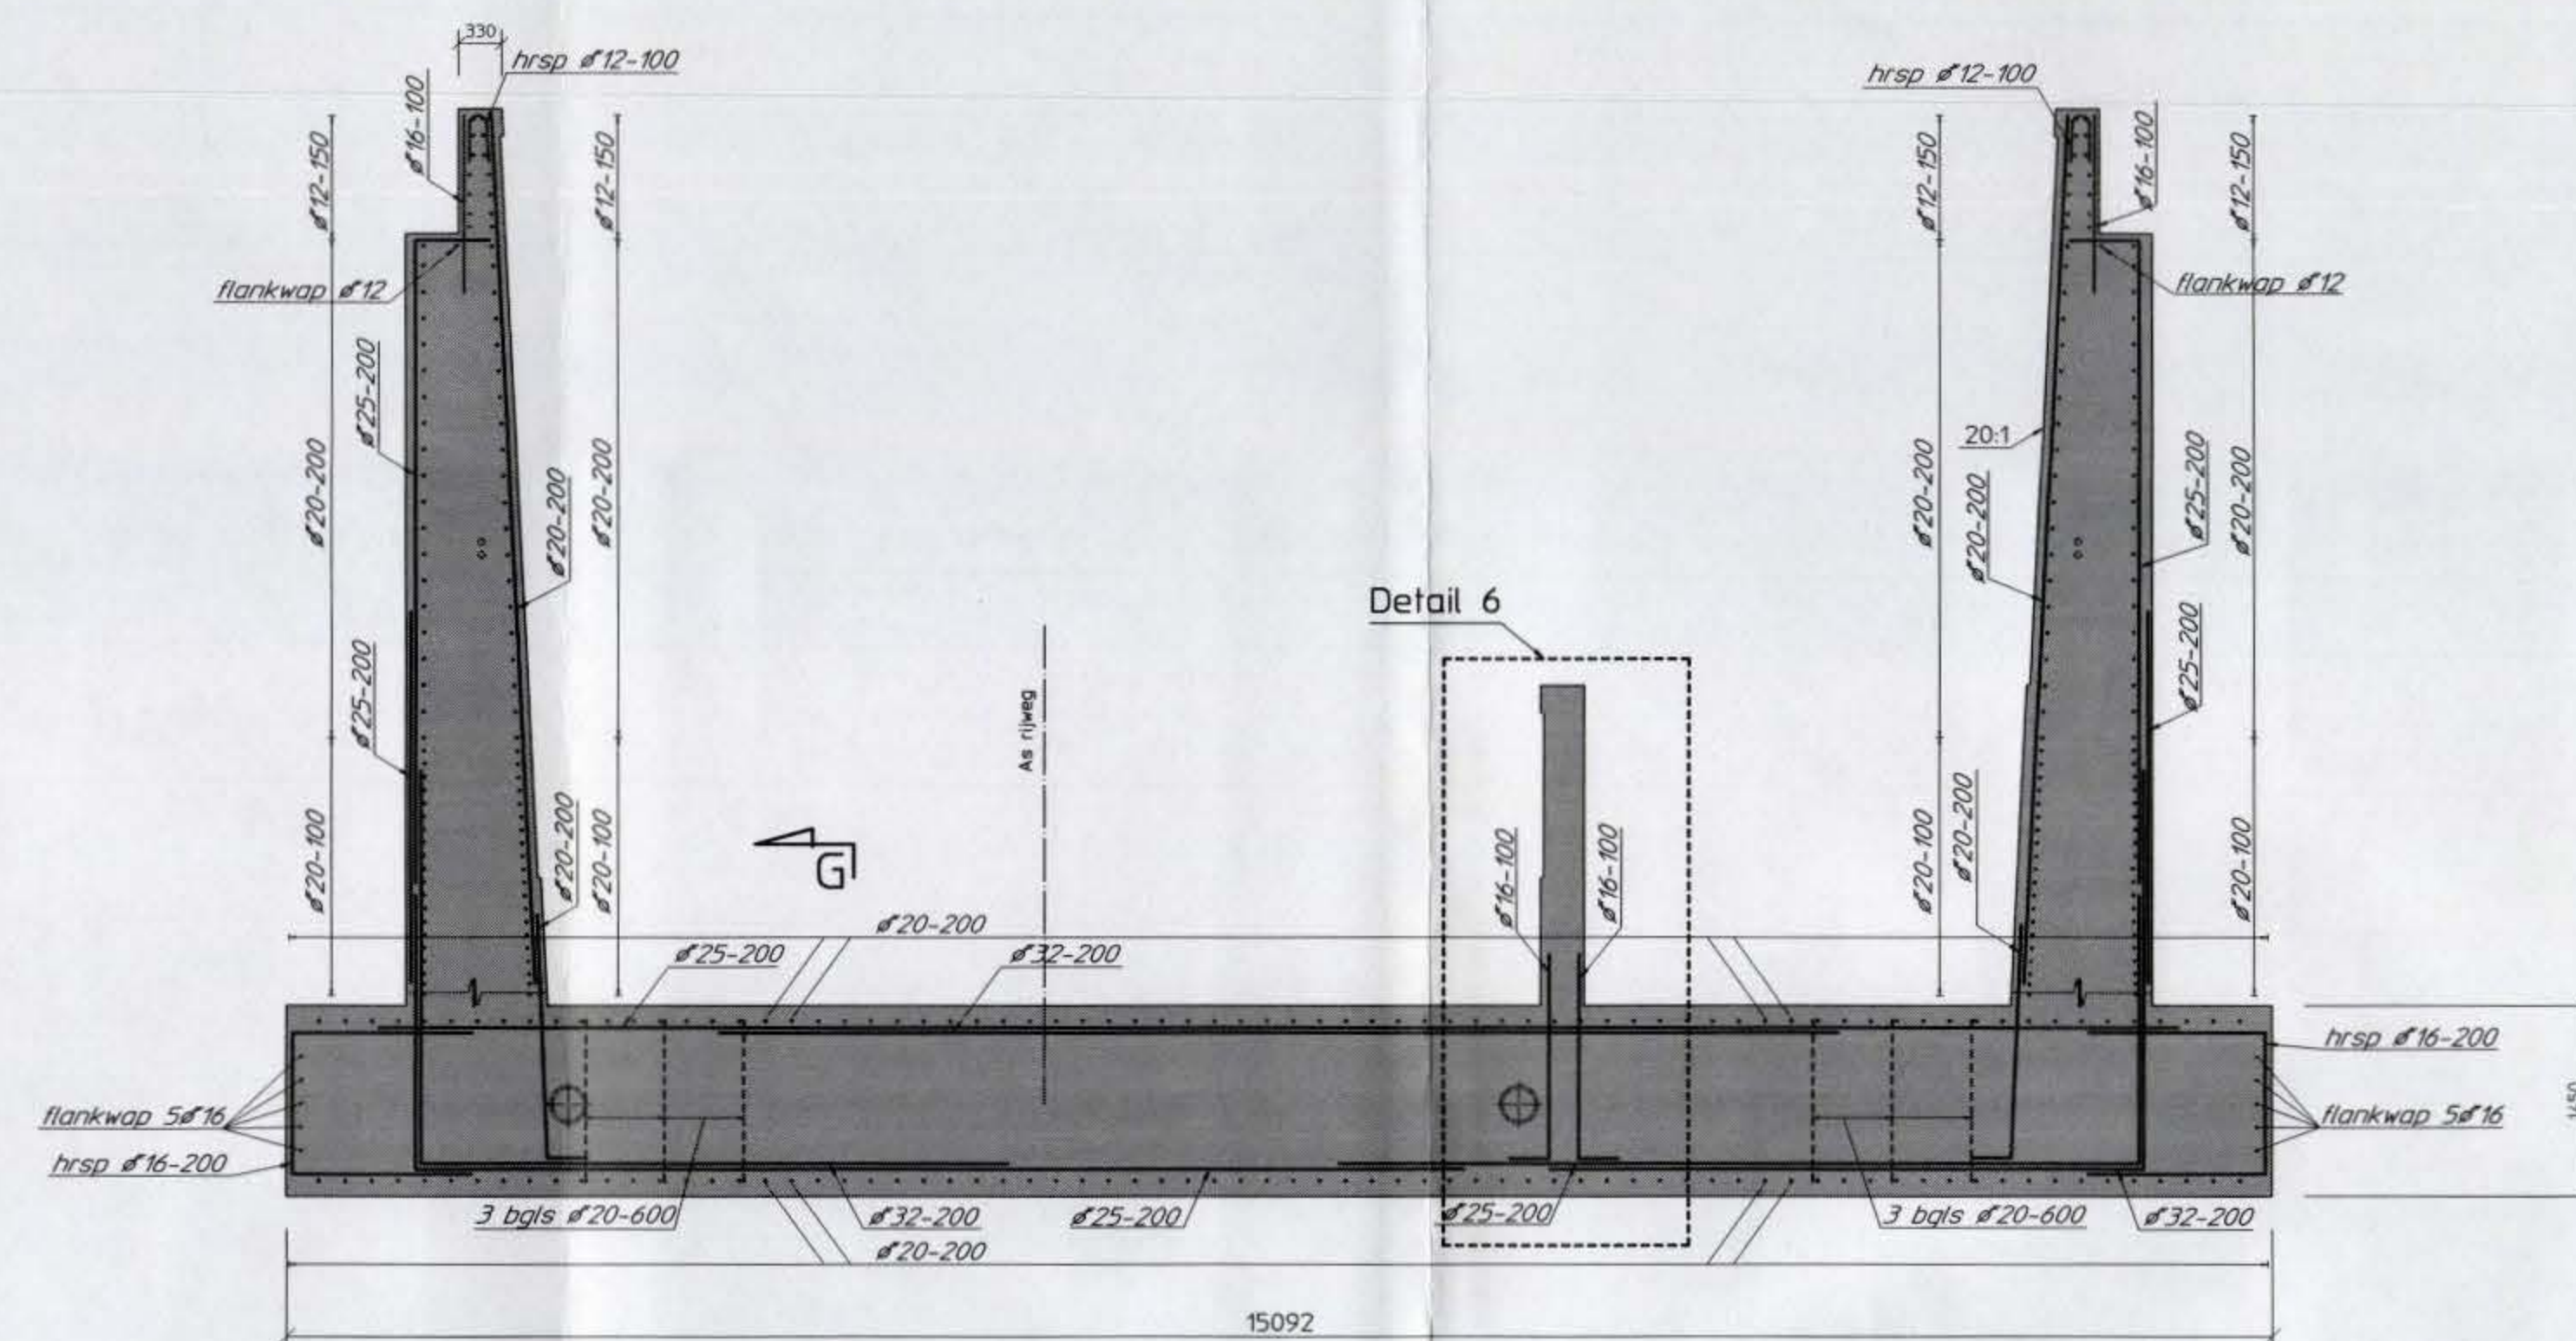


Doorsnede F-F

Schaal 150

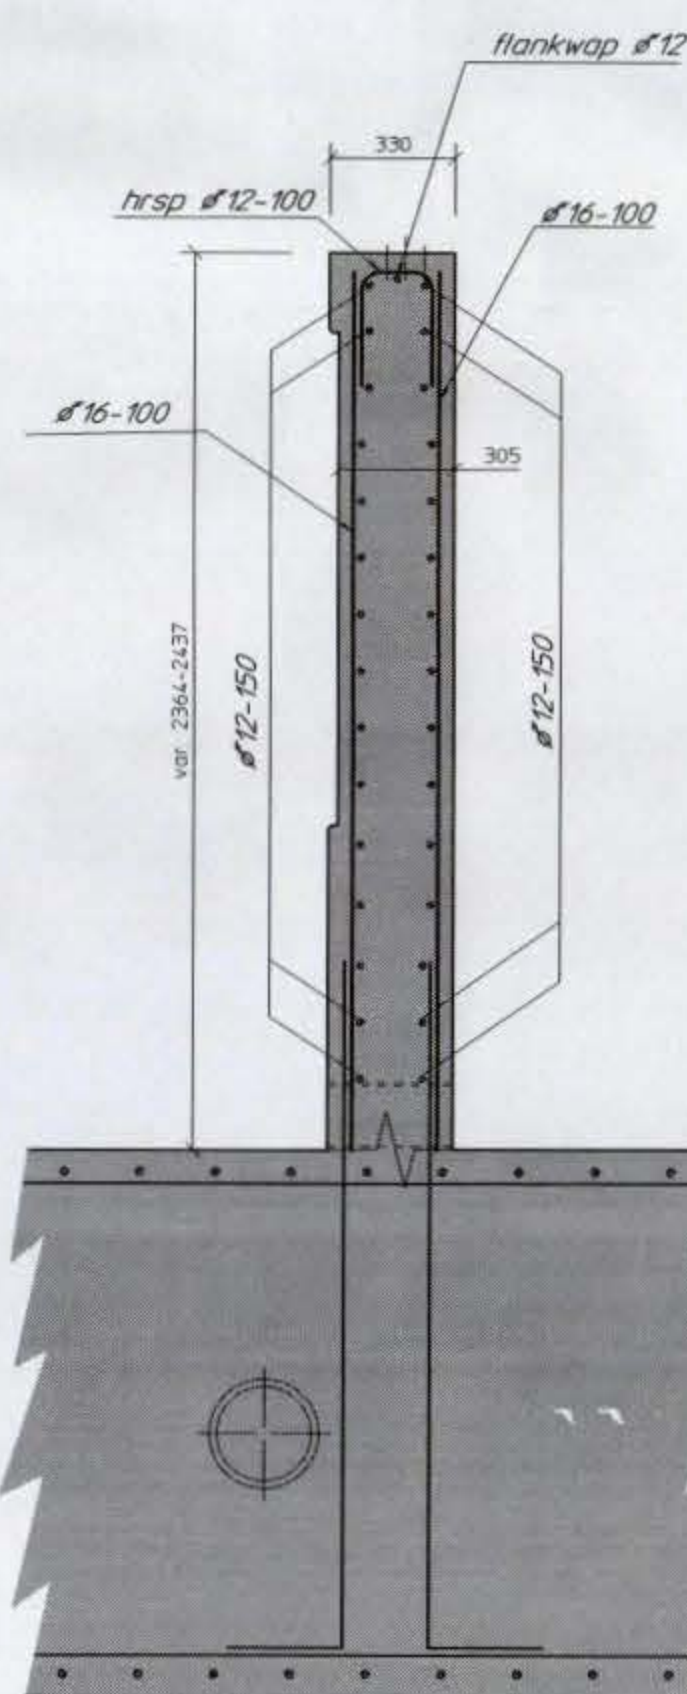

Detail 1


Schaal 1:20

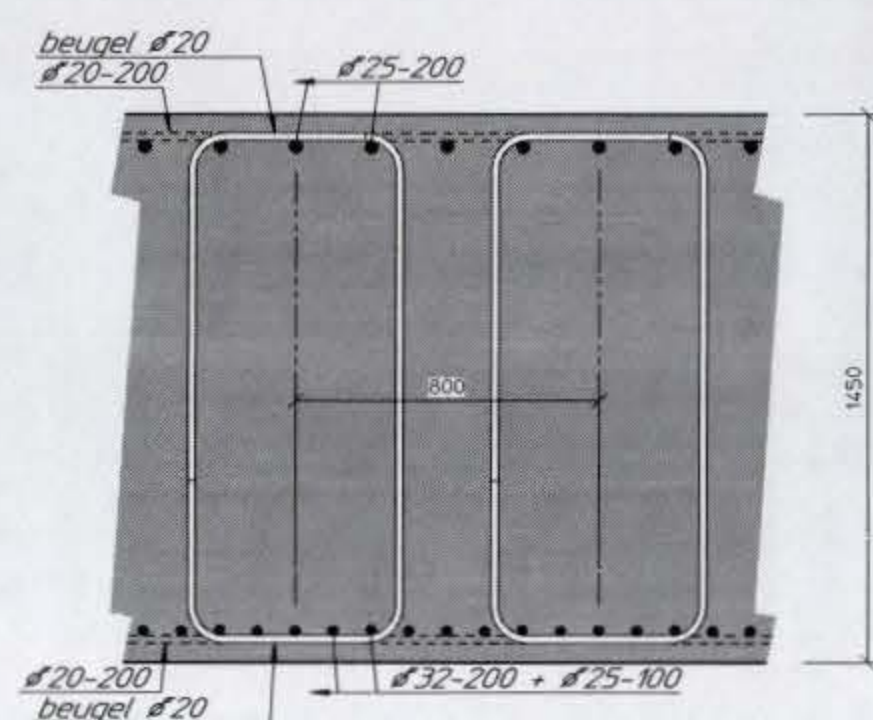

Doorsnede G-G

Schaal 1:20

Beugels in vloer

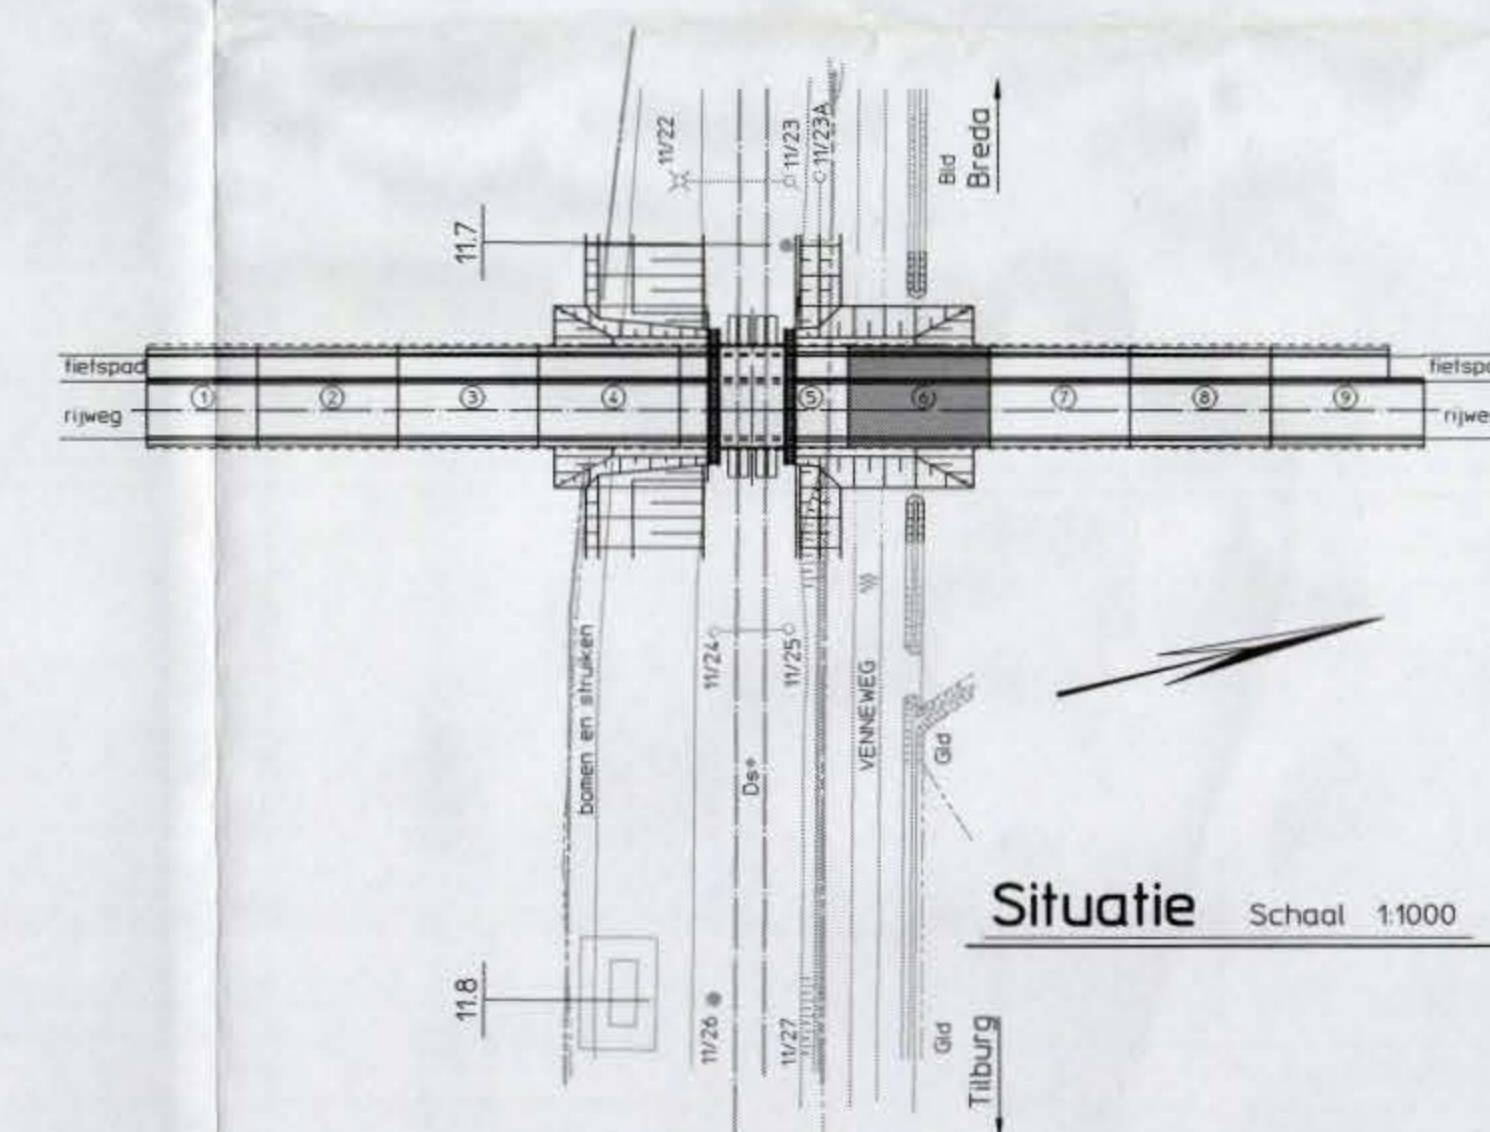

Situatie

Schaal 1:1000

Legenda

- maatvoering in mm
- hoogtemaatvoering in m t.o.v. NAP.
- voor overige doorsneden zie blad 3362706 60 W
- voor maatvoering zie tek. 3362706 60 M & 61 M
- MVL = met verspringende las
- var. = variabel

(Status: REVISIE d.d. 17-12-1999 14:53:37)

betondekkingstabel		
betonstaal : - FeB 500 HWL en/of HK NEN 6008		
beton : - sterkteklasse B 35		
- milieuklasse 3 (vloer) / 5b (wanden)		
- cement CEM III/B LH		
constructiedeel	betondekking in mm	
	controleerbaar	oncontroleerbaar
vloer	50	55
wand	50	55
op- en aanstorten	35	40

verankeringslengten		
ø10	*	
ø12	270	
ø14	*	
ø16	420	
ø20	570	
ø25	760	
ø28	*	
ø32	1280	
ø40	*	

naam	par	datum	Wapening moot 6 Blad 2
getekend	T. Brandt	17-12-99	
gecheckt	J.P. de Boeck		
projecteur	CF. Vink		
projectnr	3362706	versie	1.0
besteknr.	V40BK09450		
formaat	A1		
schaal	zie tek.		
420 123 11.720 713 3362706 61 W			NS Railinfrabeheer Regio Zuid Gilze Rijen Onderdoorgang Europaalaan