
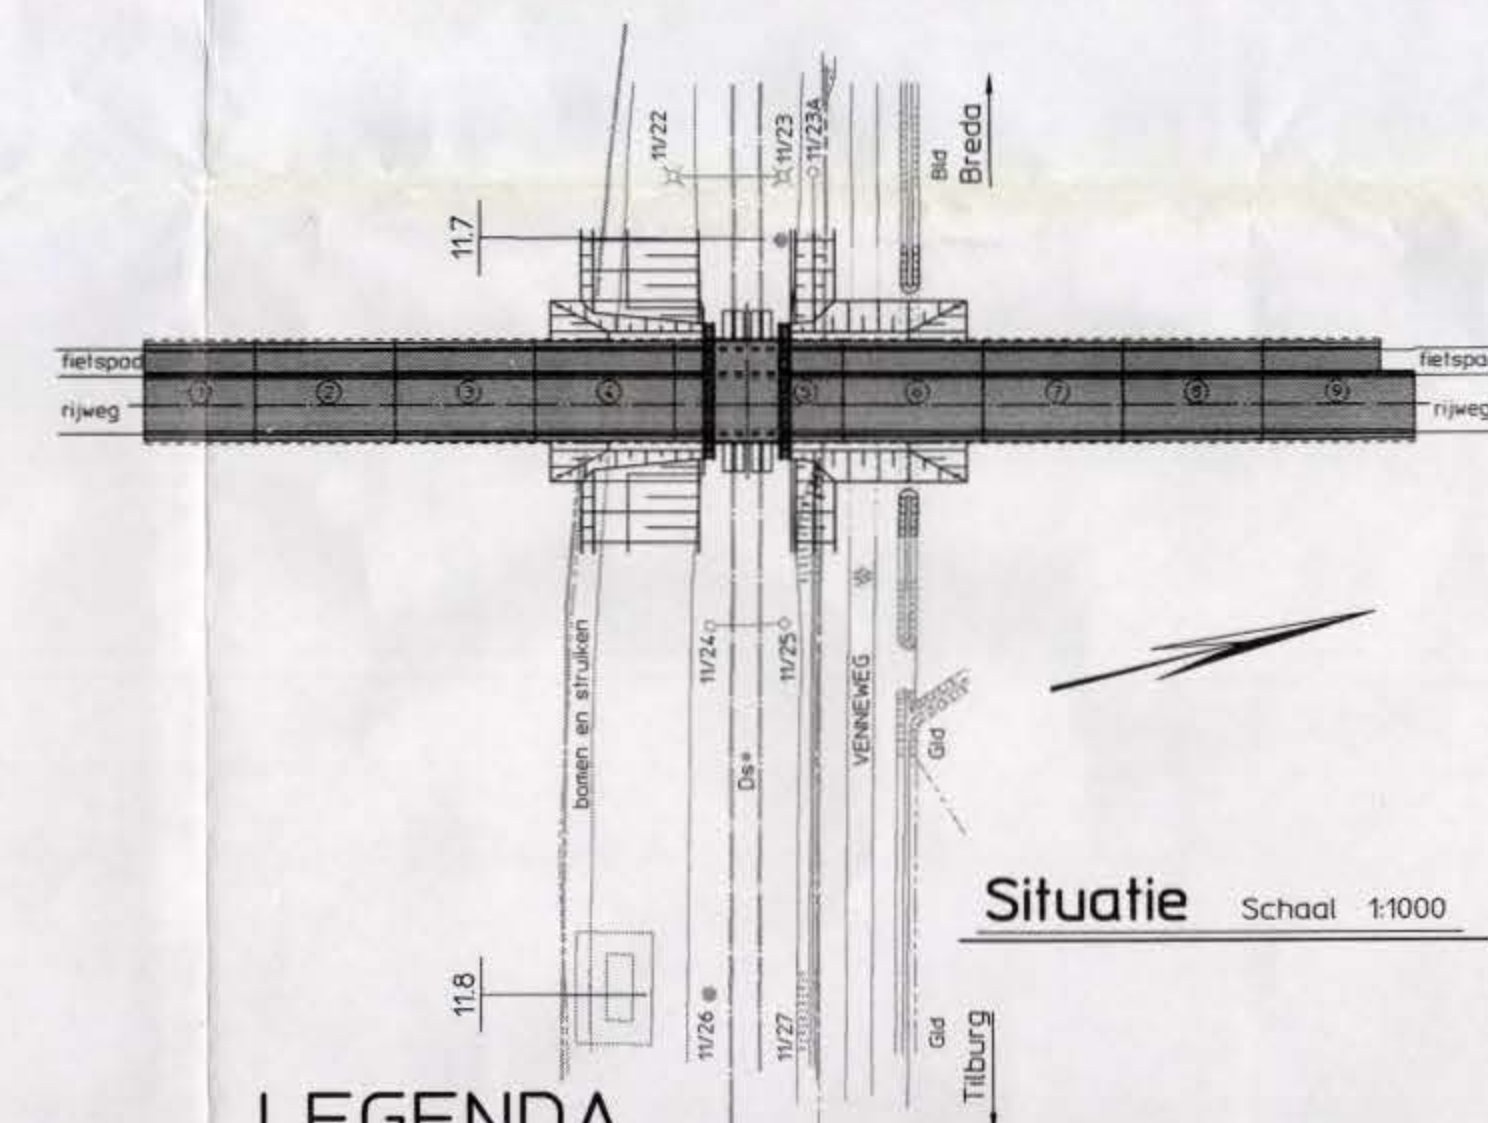
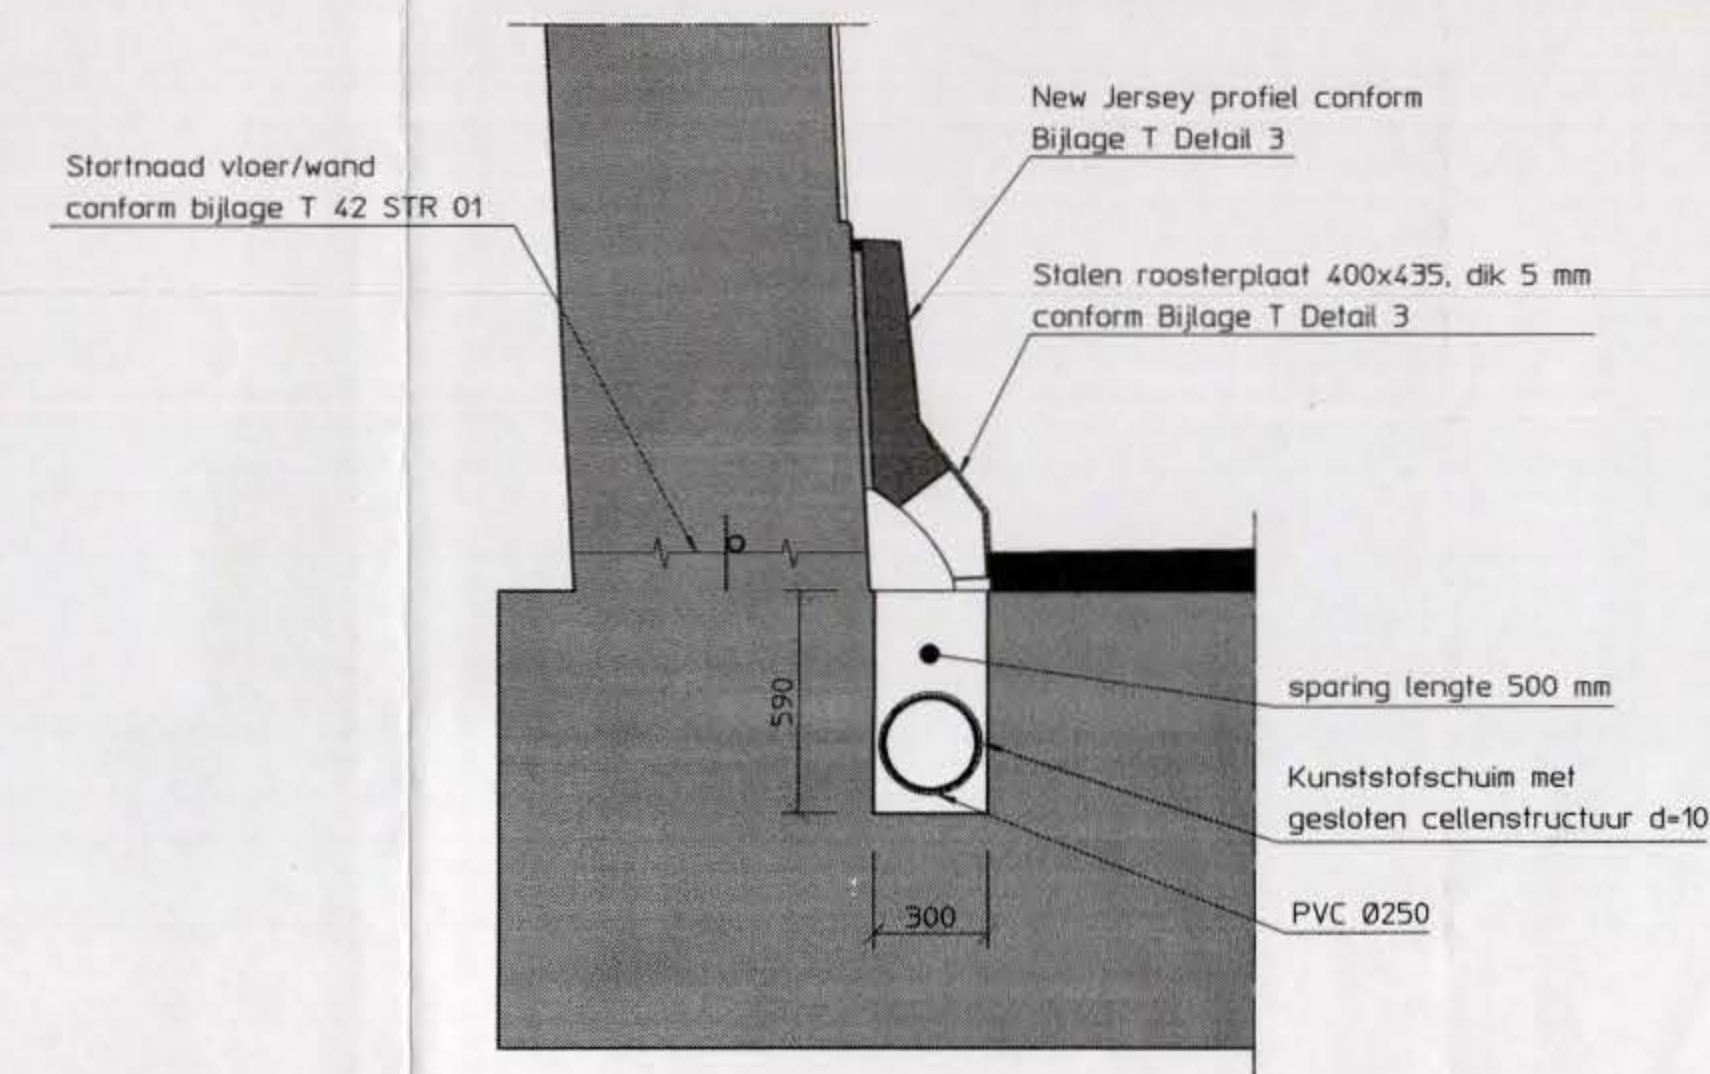
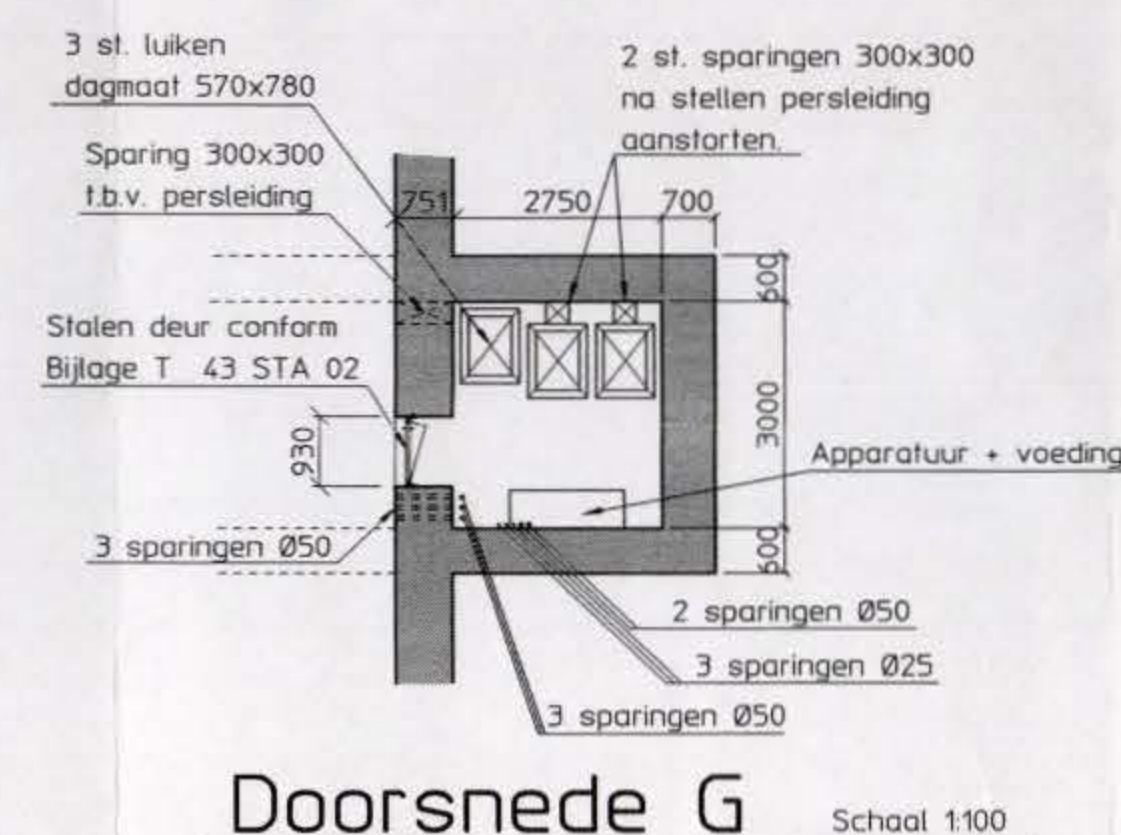
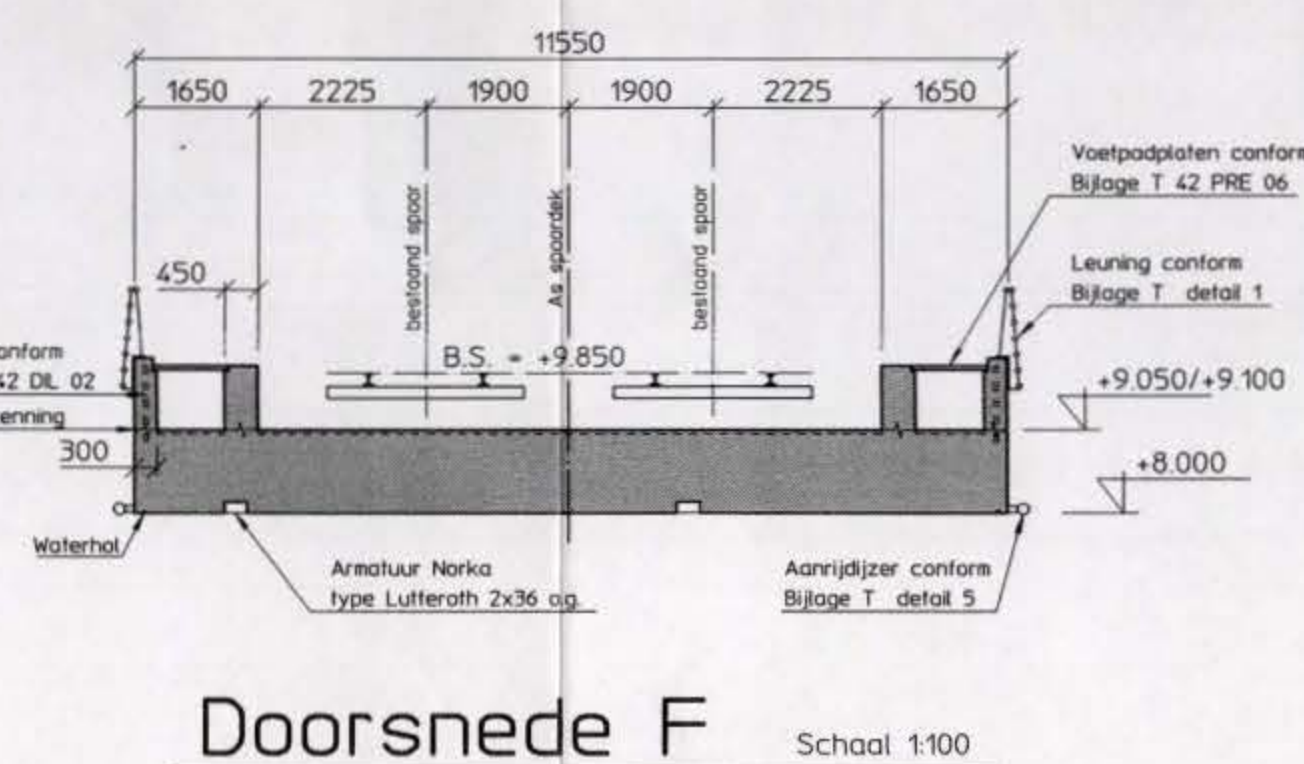
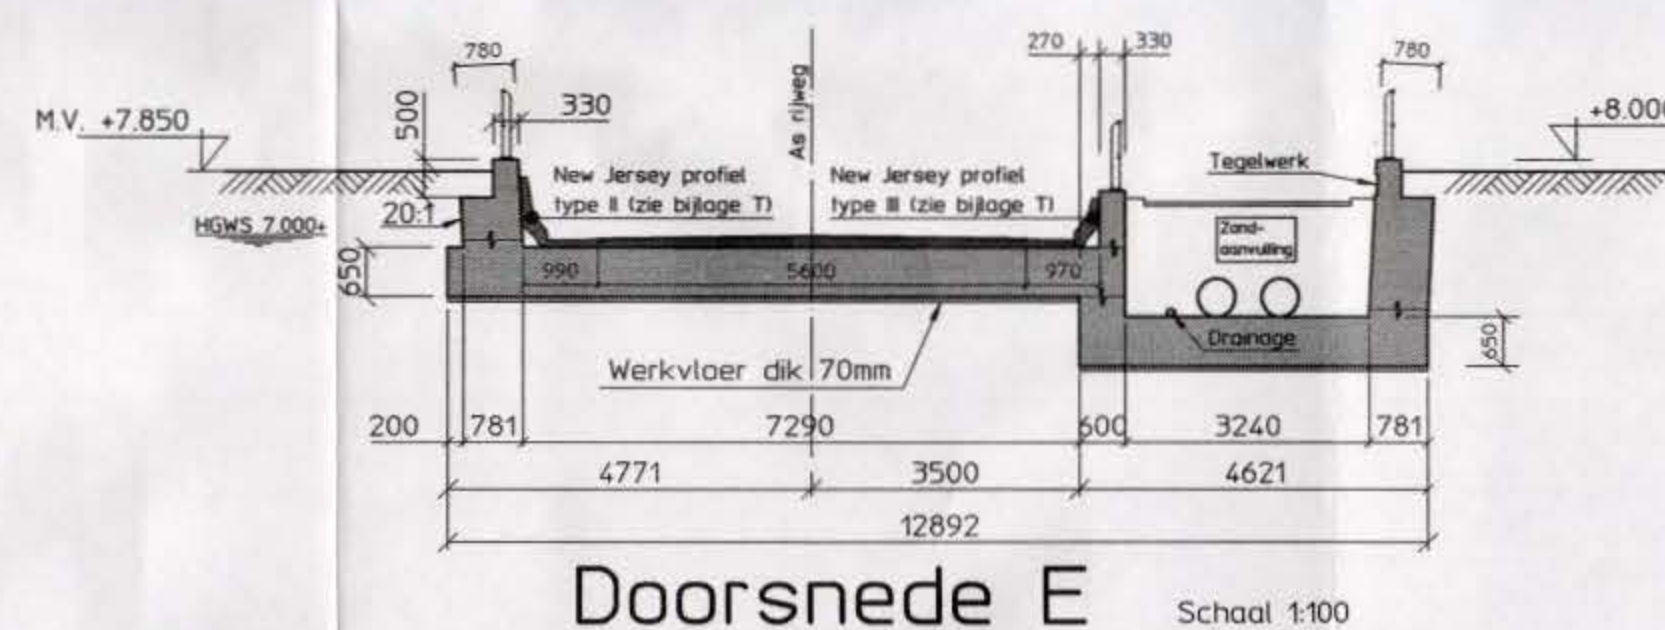
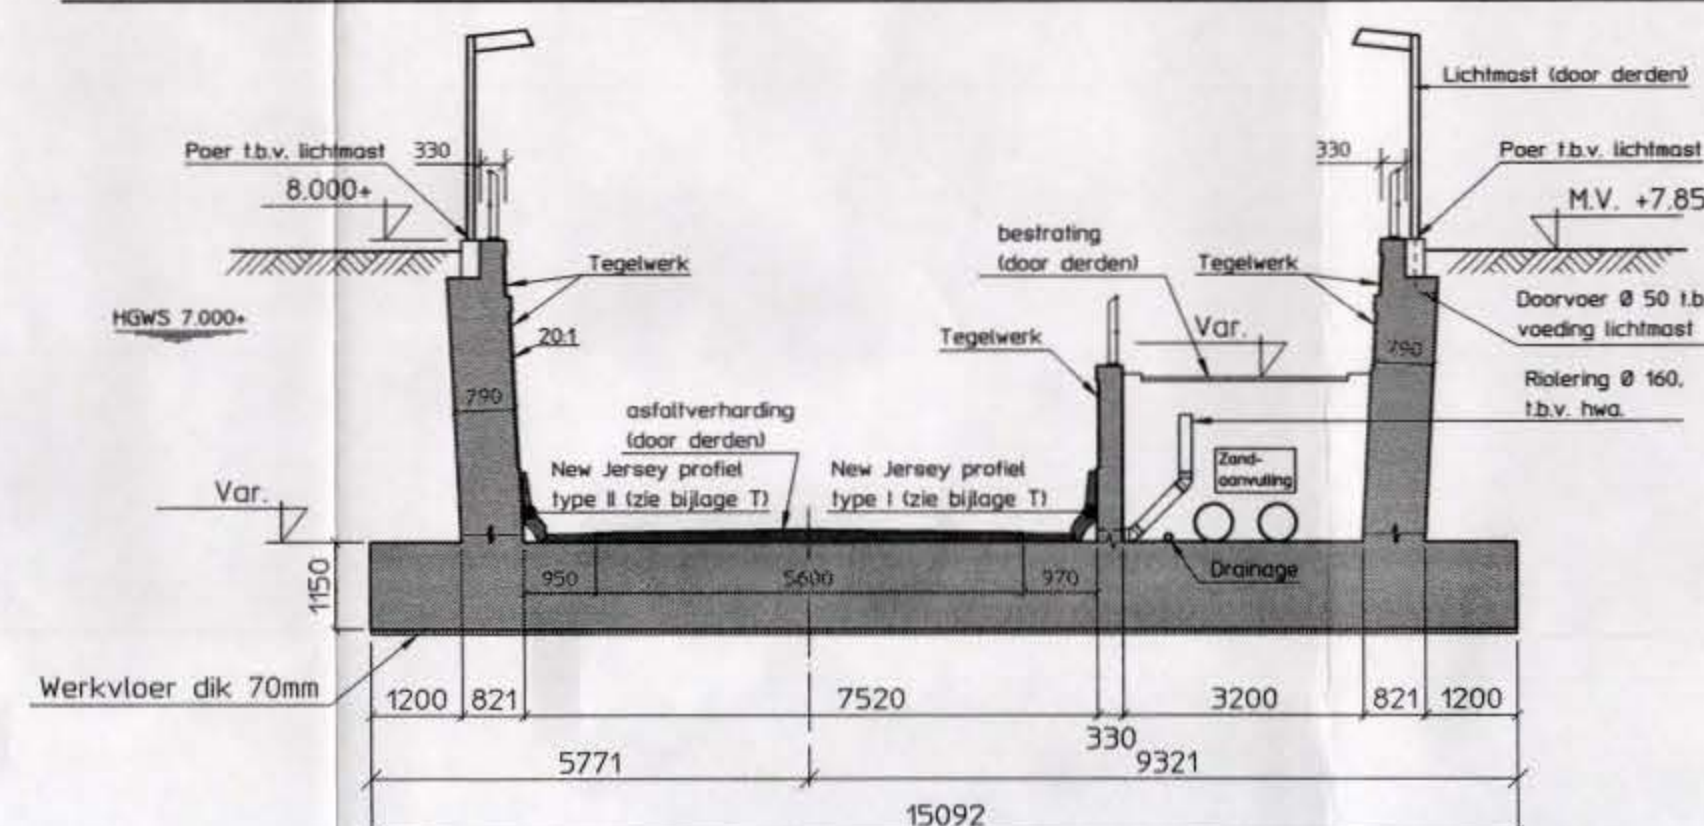
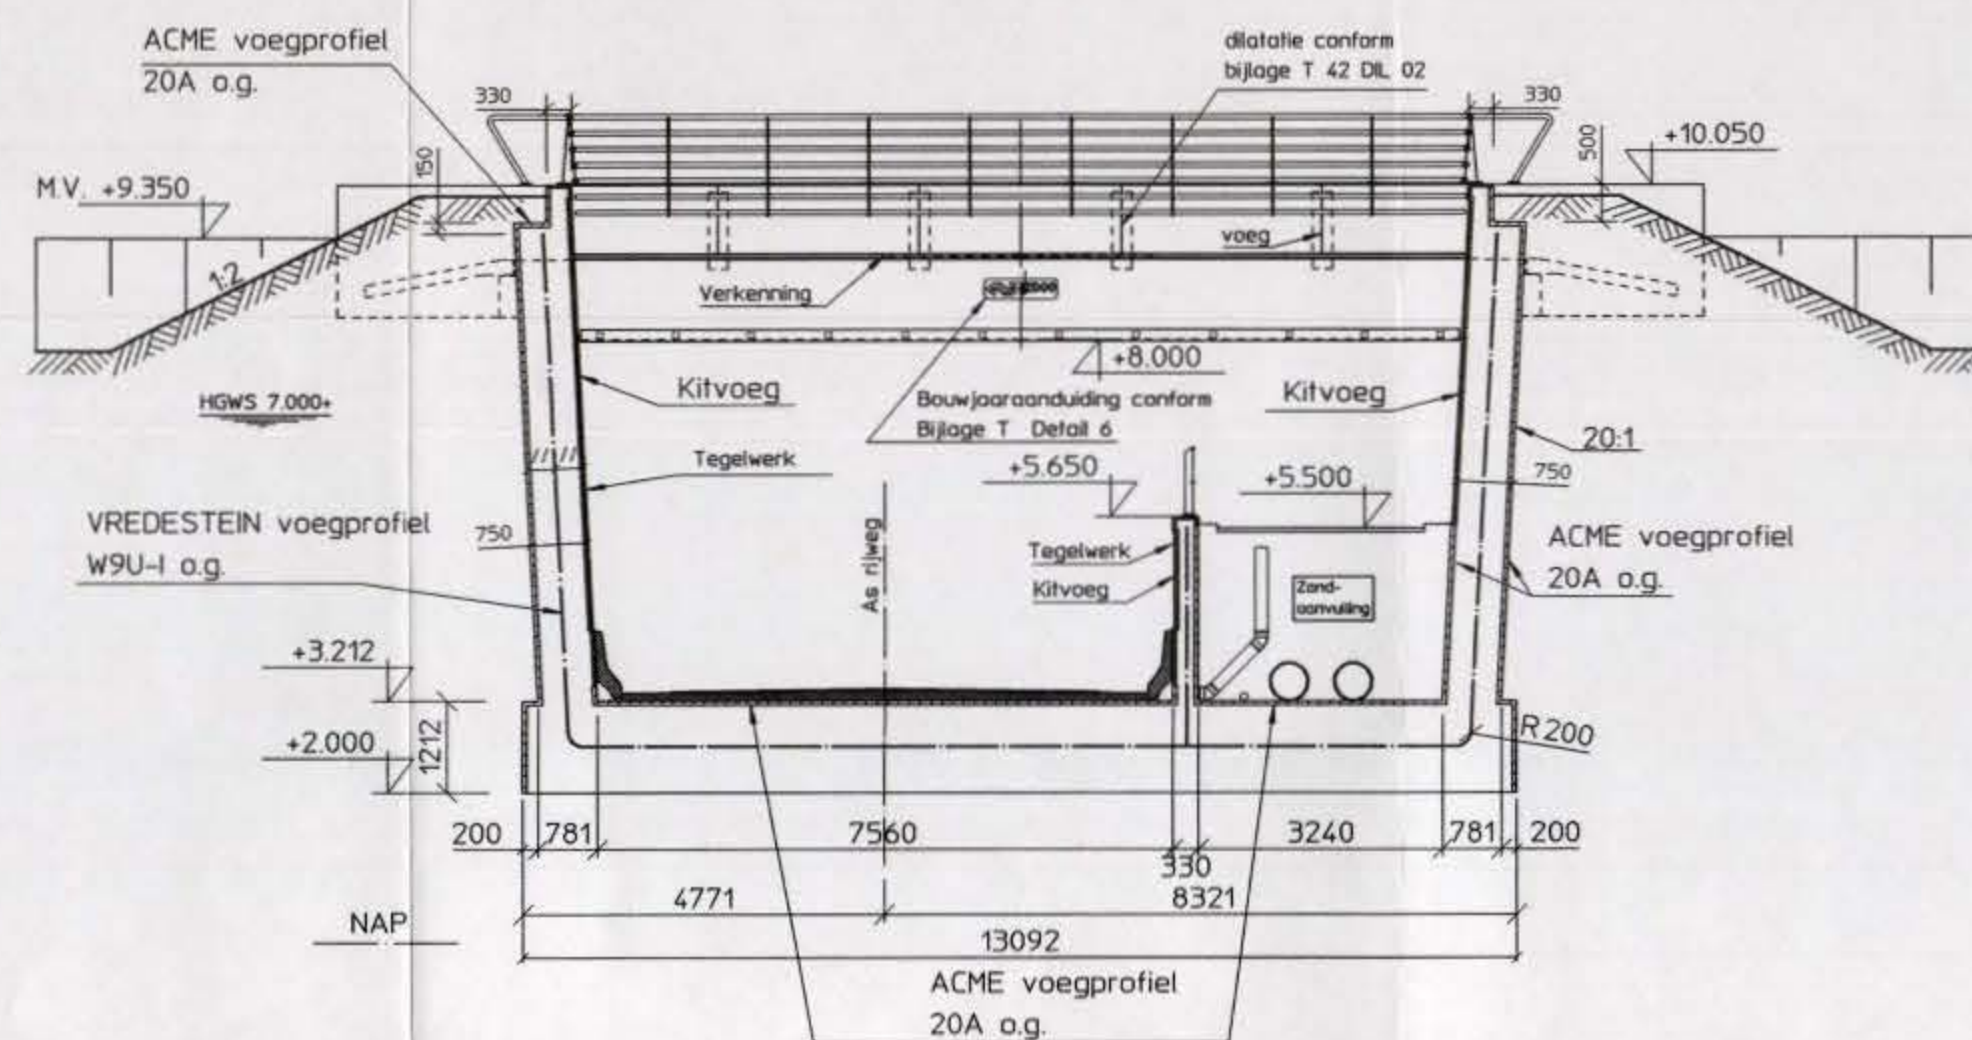
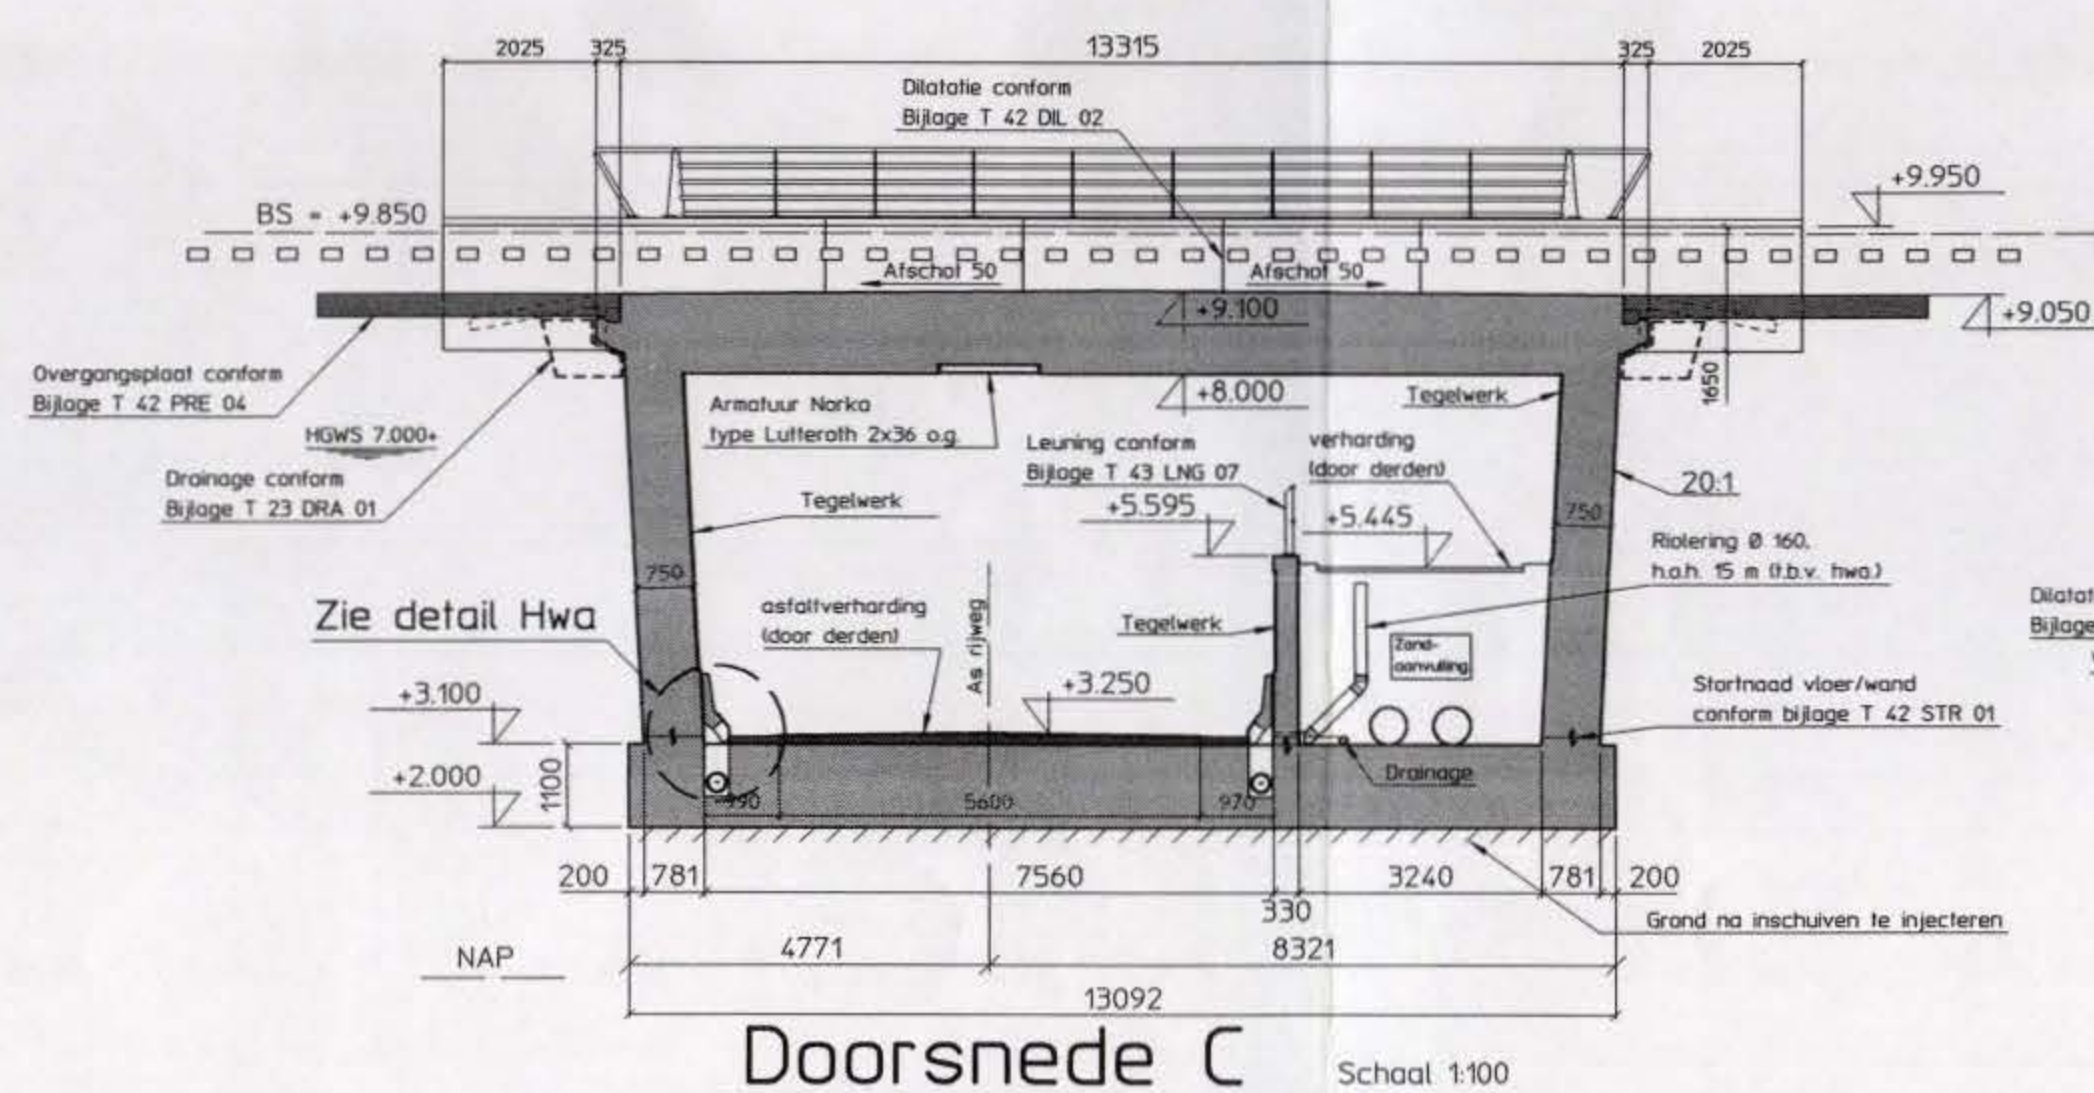
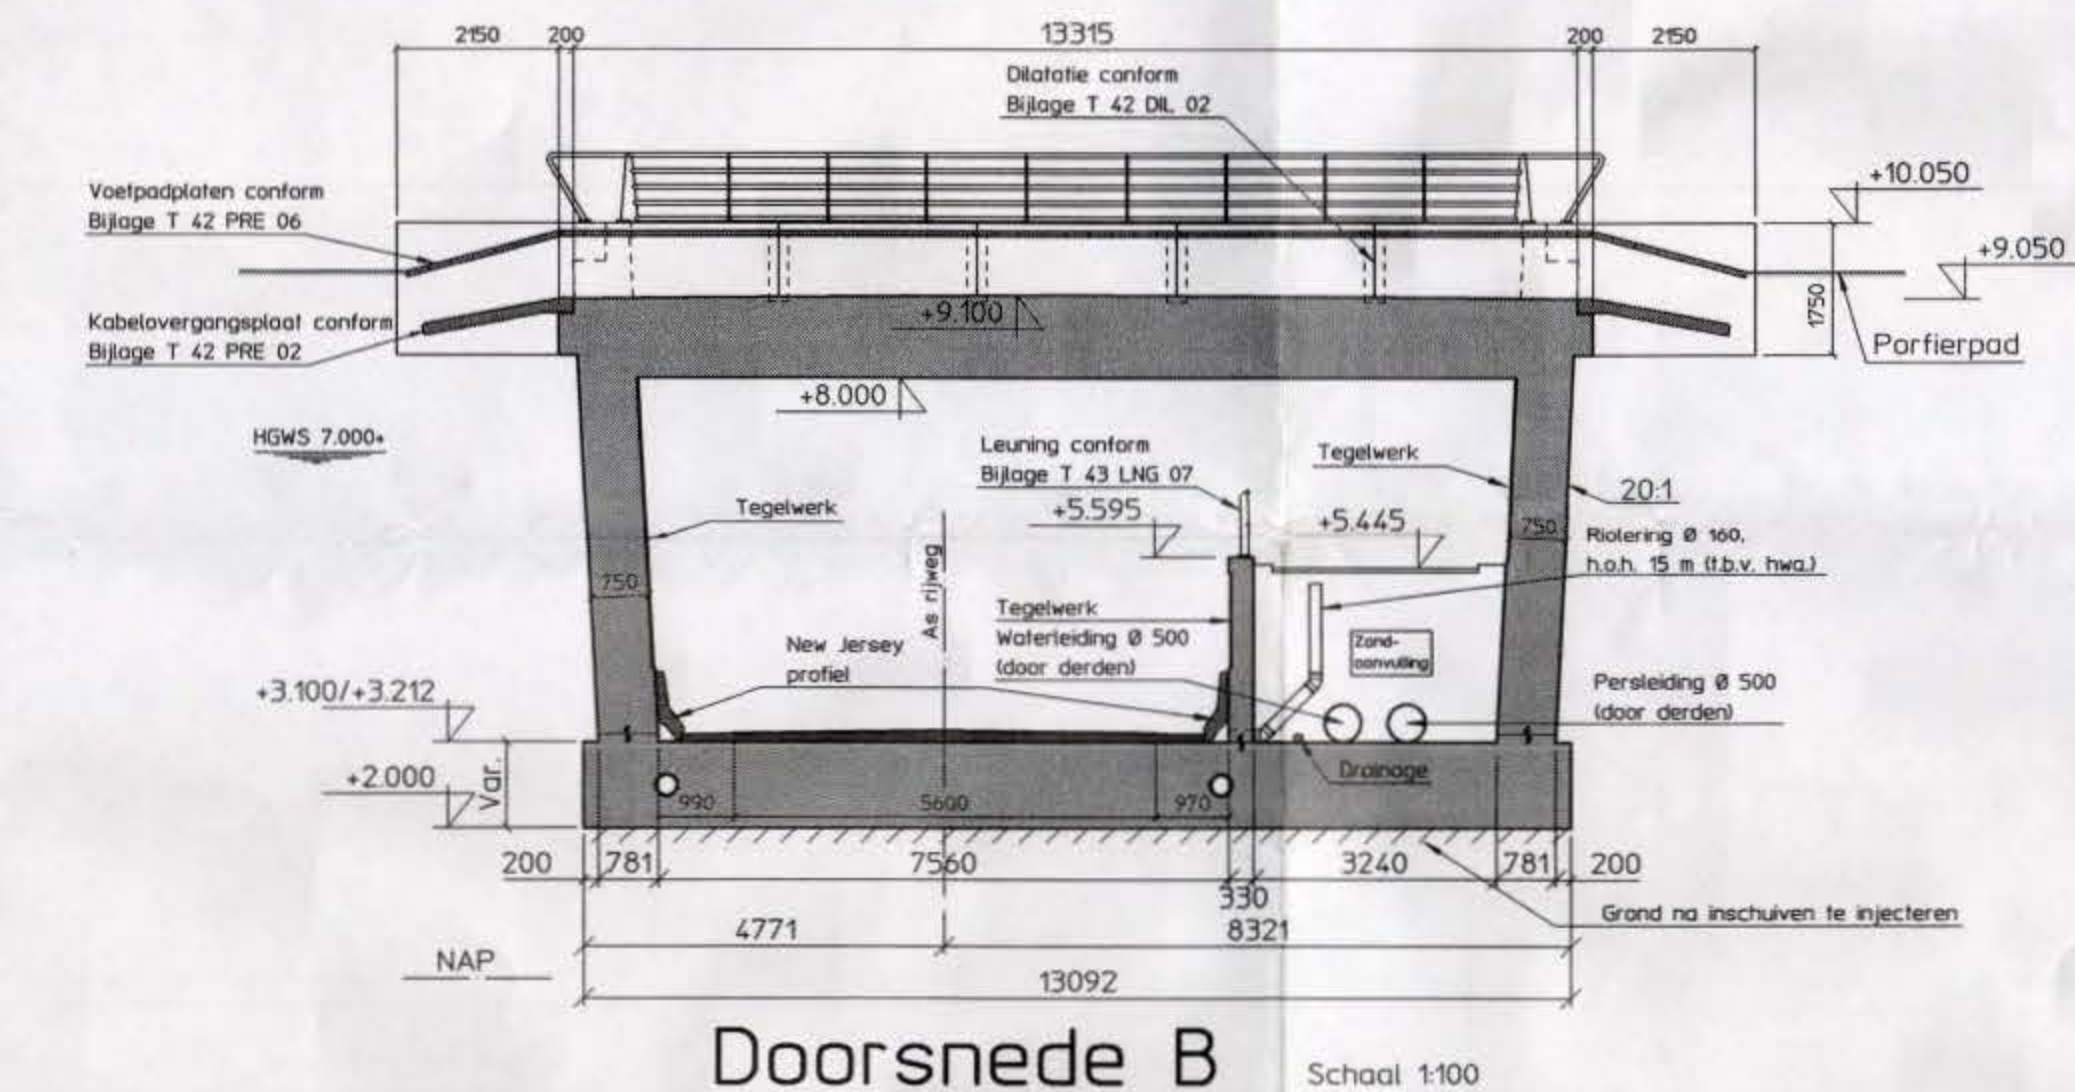


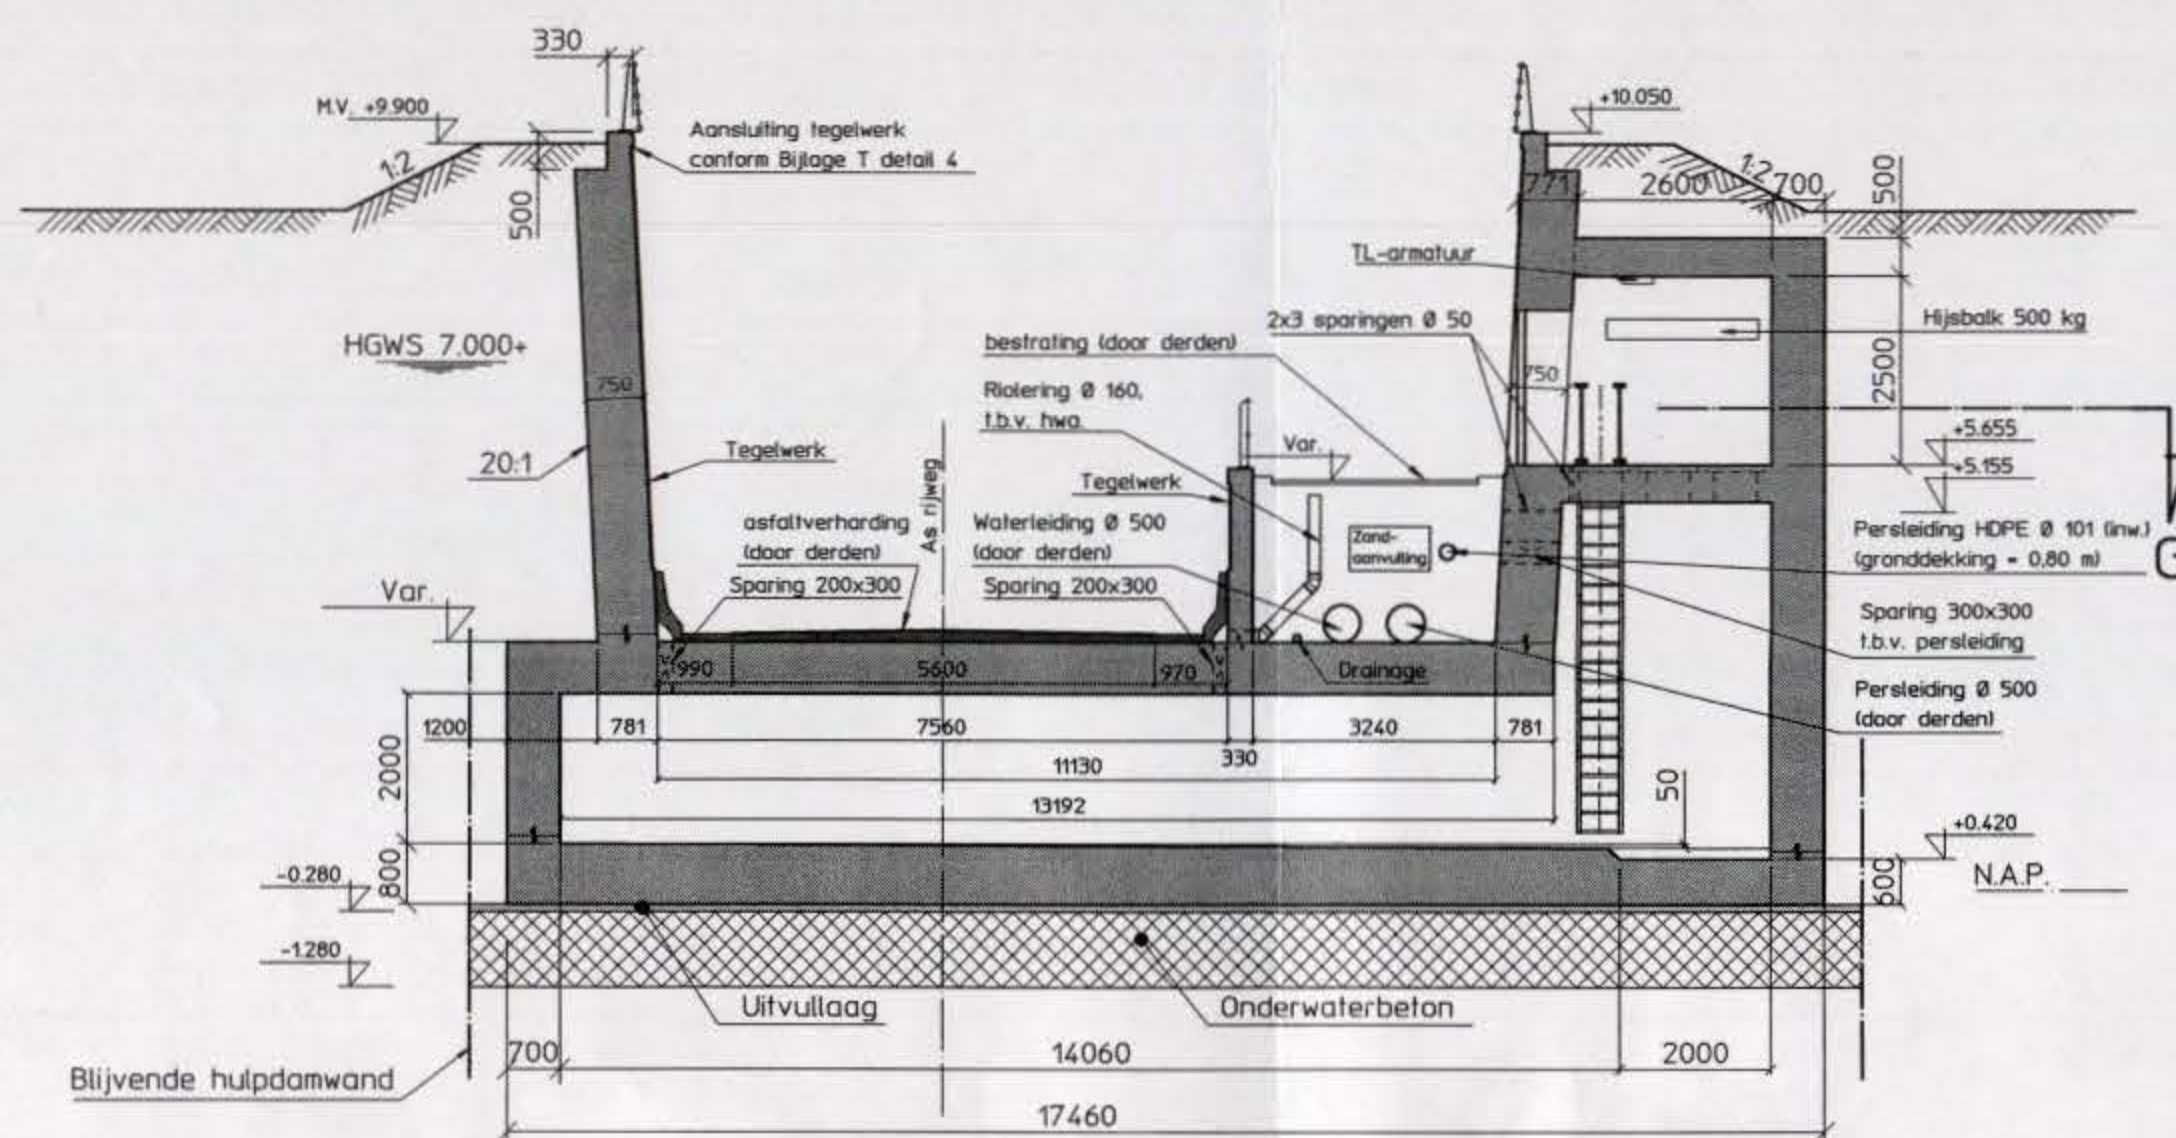


LEGENDA

Maten in millimeters, tenzij anders aangegeven
Hoogtematen in meters t.o.v. NAP, tenzij anders aangegeven

-  : gewapend beton
 : prefab beton
 : onderwaterbeton

Ontwerpsnelheid: V= 160 km/h
 Voor bovenaanzicht & langsdoorsneden zie blad B-1

(Status: REVISIE d.d. 13-04-2000 09:14:33)

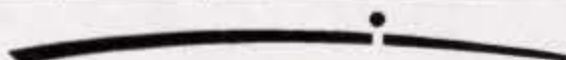	naam	por	datum	Bestekstekening Doorsnede A t/m G & Details
getekend	V. Winkelaar		25-11-'98	
projectleider	C.F. Vink			
projectnr.	3362704	versie	1.0	
besteknr.	V40BK09450			NS Railinfrabeheer Regio Zuid Gilze Rijen Onderdoorgang Europalaan
formaat	A1			
schaal	div.			
420 / 123 / 11.720 / 713 / 3362704 B-2				
VA CT PG B2 Postbus 2855 3500 GW Utrecht Telefoon 030 - 235 89 58 Telefax 030 - 235 72 29				
 Holland Railconsult				
dnlno: jme10 dwo/clt/cit3/km011720/no336270.4/noc714/h. 2 revisie boeckx ct k 13-04-2000 09:24:07				