

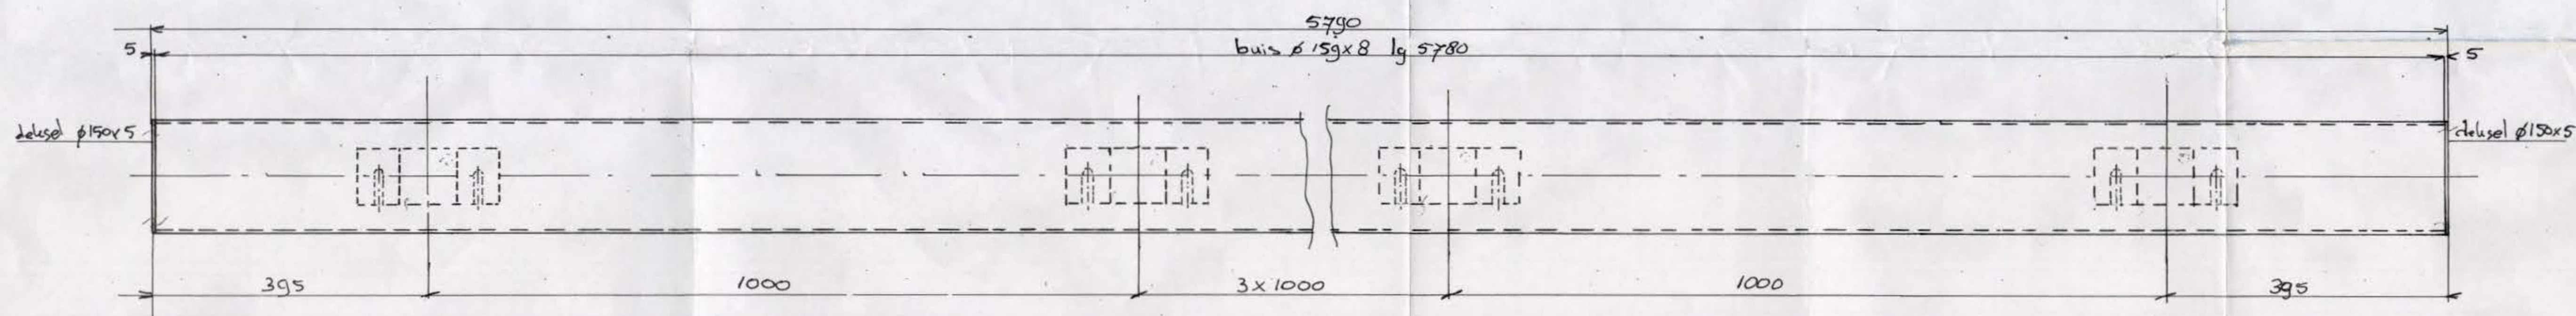


Merk A 4x uitvo. als get.  
Merk B 4x uitvo. sp. beeld van A

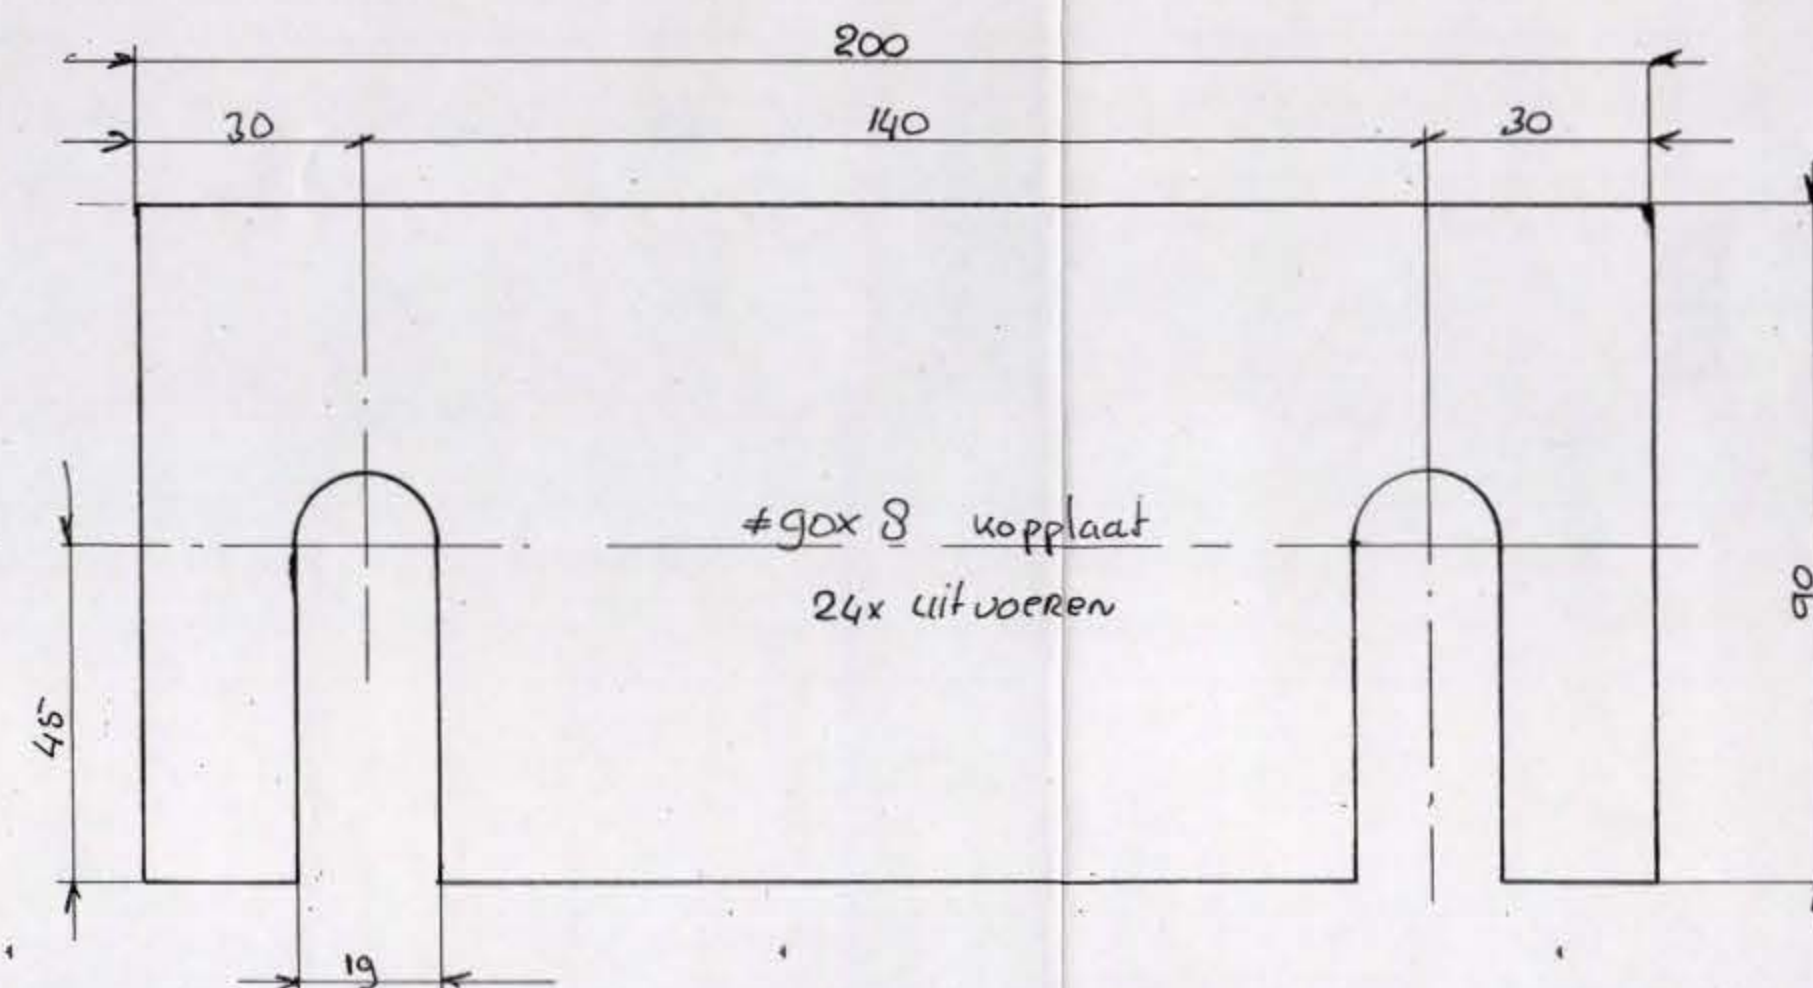

Merk C 4x uitvoeren

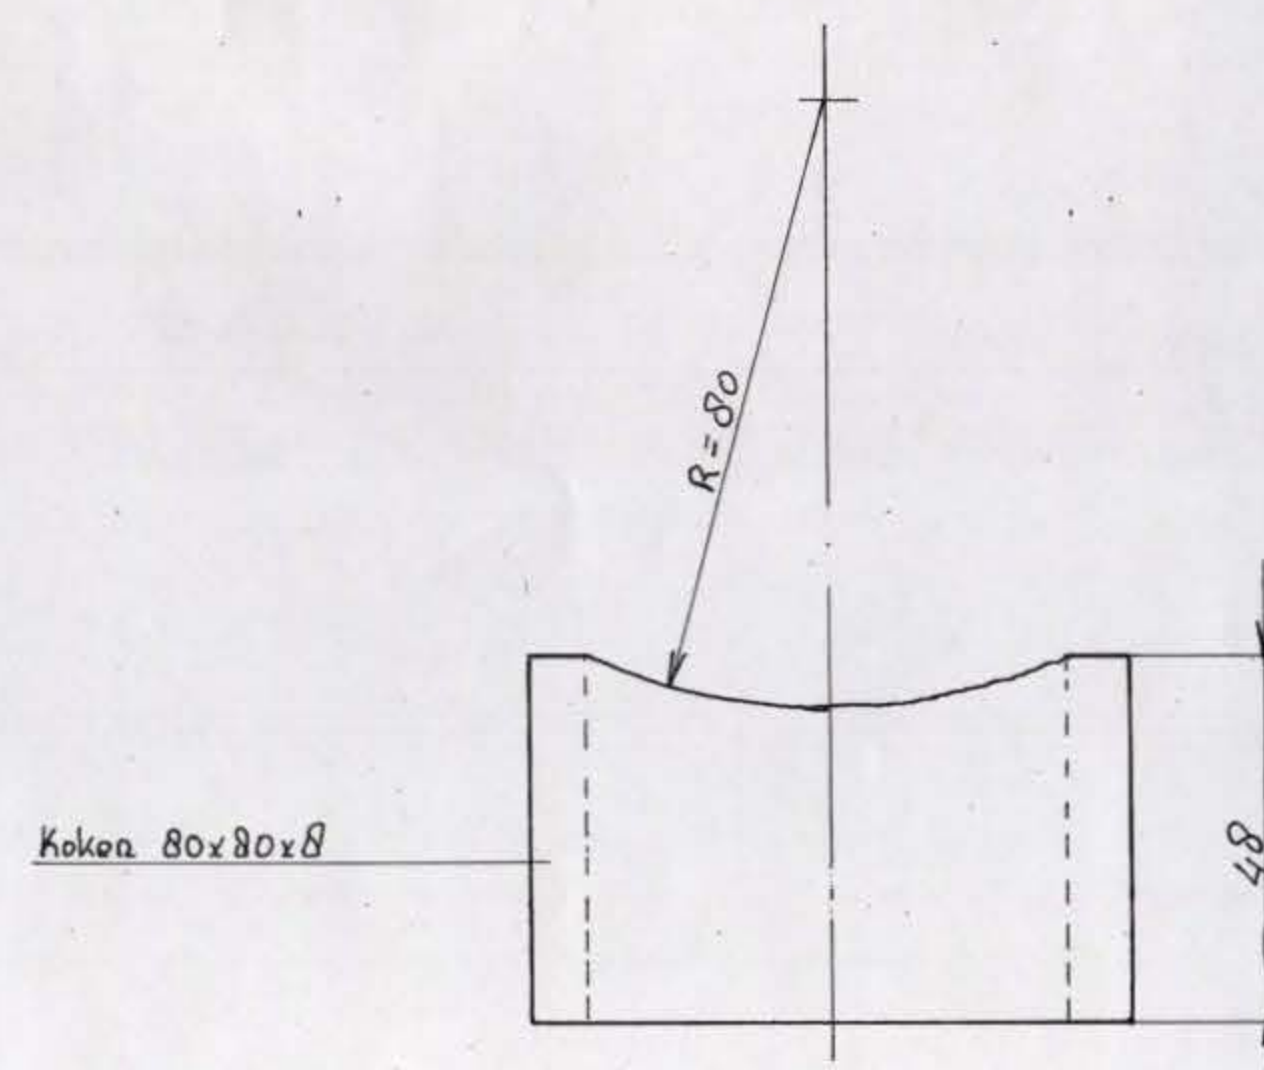

conservering: Thermisch verzinken

denk aan ontluuchtingsgaten

| POS.   | AANTAL     | PROFIEL | LENGTE    | TOT. IN MM                                                               | GEW. EENH. | TOT. GEWICHT | BOUEN | OPMERKINGEN |     |
|---|------------|---------|-----------|--------------------------------------------------------------------------|------------|--------------|-------|-------------|-----|
| Status: REVISIE d.d. 20-12-1999 pjl: .....                                                                    |            |         |           |                                                                          |            |              |       |             |     |
|   |            |         |           | AANRIJDIJZER                                                             |            |              |       |             |     |
| getekend   | naam       | par     | datum     | NS Railinfrabeheer Regio Zuid<br>Gilze Rijen<br>Onderdoorgang Europalaan |            |              |       |             |     |
|   | PaB        |         | 24-03--99 |                                                                          |            |              |       |             |     |
| projectleider                                                                                                 | C.F. Vink  |         |           |                                                                          |            |              |       |             |     |
| projectnr.   | 3362706    | versie  | 1.0       |                                                                          |            |              |       |             |     |
| besteknr.   | V40BK09450 |         |           |                                                                          |            |              |       |             |     |
| formaat   | A0         |         |           |                                                                          |            |              |       |             |     |
| schaal   | zie tek.   |         |           |                                                                          |            |              |       |             |     |
| 420   |            | 123     |           | 11.720                                                                   |            | 713          |       | 33622706    | 075 |
| Div *** Afd *** Grp ***<br>Postbus 2855<br>3500 GW Utrecht<br>Telefoon 030 - 265 ***<br>Telefax 030 - 265 *** |            |         |           |                                                                          |            |              |       |             |     |
| Holland Railconsult                                                                                           |            |         |           |                                                                          |            |              |       |             |     |

Holland Railconsult