


# DETAIL-BOEK

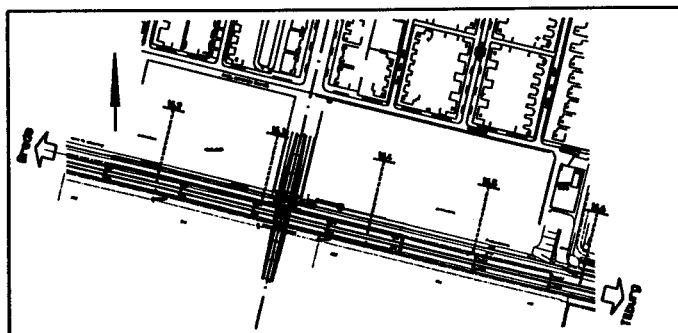

## REVISIE TOEGEPAST

datum: 28-2-'01  
paraaf: *R*



### ARCADIS BOUW/INFRA

Berkenweg 7  
Postbus 220, 3800 AE Amersfoort  
Telefoon 033 460 44 00  
Telefax 033 460 44 06

Project  
**Tilburg**  
o.d.g. Campenhoef-Witbrant

| Uitg. | Datum    | Getekend    | Opmerkingen |
|-------|----------|-------------|-------------|
| R     | 20-02-01 | A. Beukers  | revisie     |
| R-1   | 18-01-01 | v.oostende  | revisie     |
| A     | 12-01-00 | B. Visscher |             |

Onderdeel  
**Bestek**

Details

Codering derden :

Status :

Goedgekeurd :  
A. Viergever

Vrijgegeven :  
J.W.M. Hagen

Schaal : 1:20, 1:10, 1:100

Formaat : A4



⊕ In bewerking  
⊙ Conceptversie  
⊕ Goedgekeurd  
● Vrijgegeven


Tekeningnummer:

Tb 42/3/1

304-V

T:\Acad\PROJECTS\61688214\reviste\detailboekv-R\A01-R.dwg  
Xref:

ARCADIS Bouw/Infra BV is ontstaan uit Articon, Grabowsky&Poort,  
Heidemij Advies Bouw, Bureau Jongen, Starke Diekstra en Van der Mast

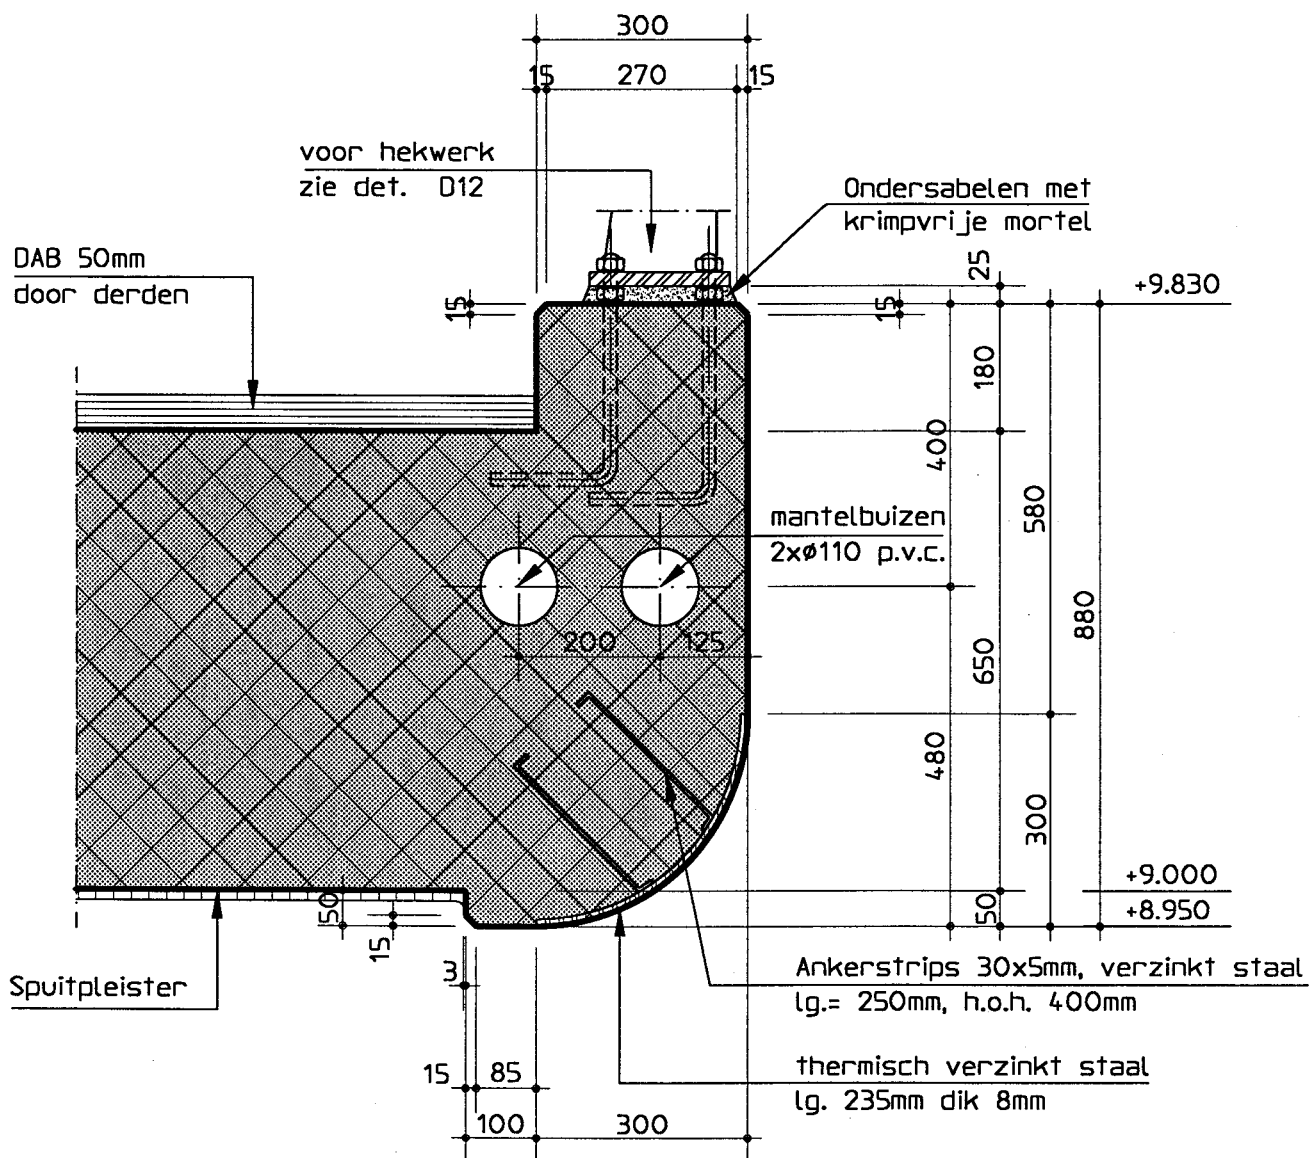

# REVISIE TOEGEPAST

datum: 28-02-'01  
paraaf: *R*

**ARCADIS** BOUW/INFRA



**Project** : Tilburg o.d.g. Campenhoef - Witbrant

**Tek.nr.**

**Onderdeel** : Bescherm-ijzer dek


**D01**

**Schaal** : 1:10

**Bestandsnaam** : T:\ACAD\PROJECTS\61688214\DETAILB\D01.DWG

**Xref-naam** : GEEN



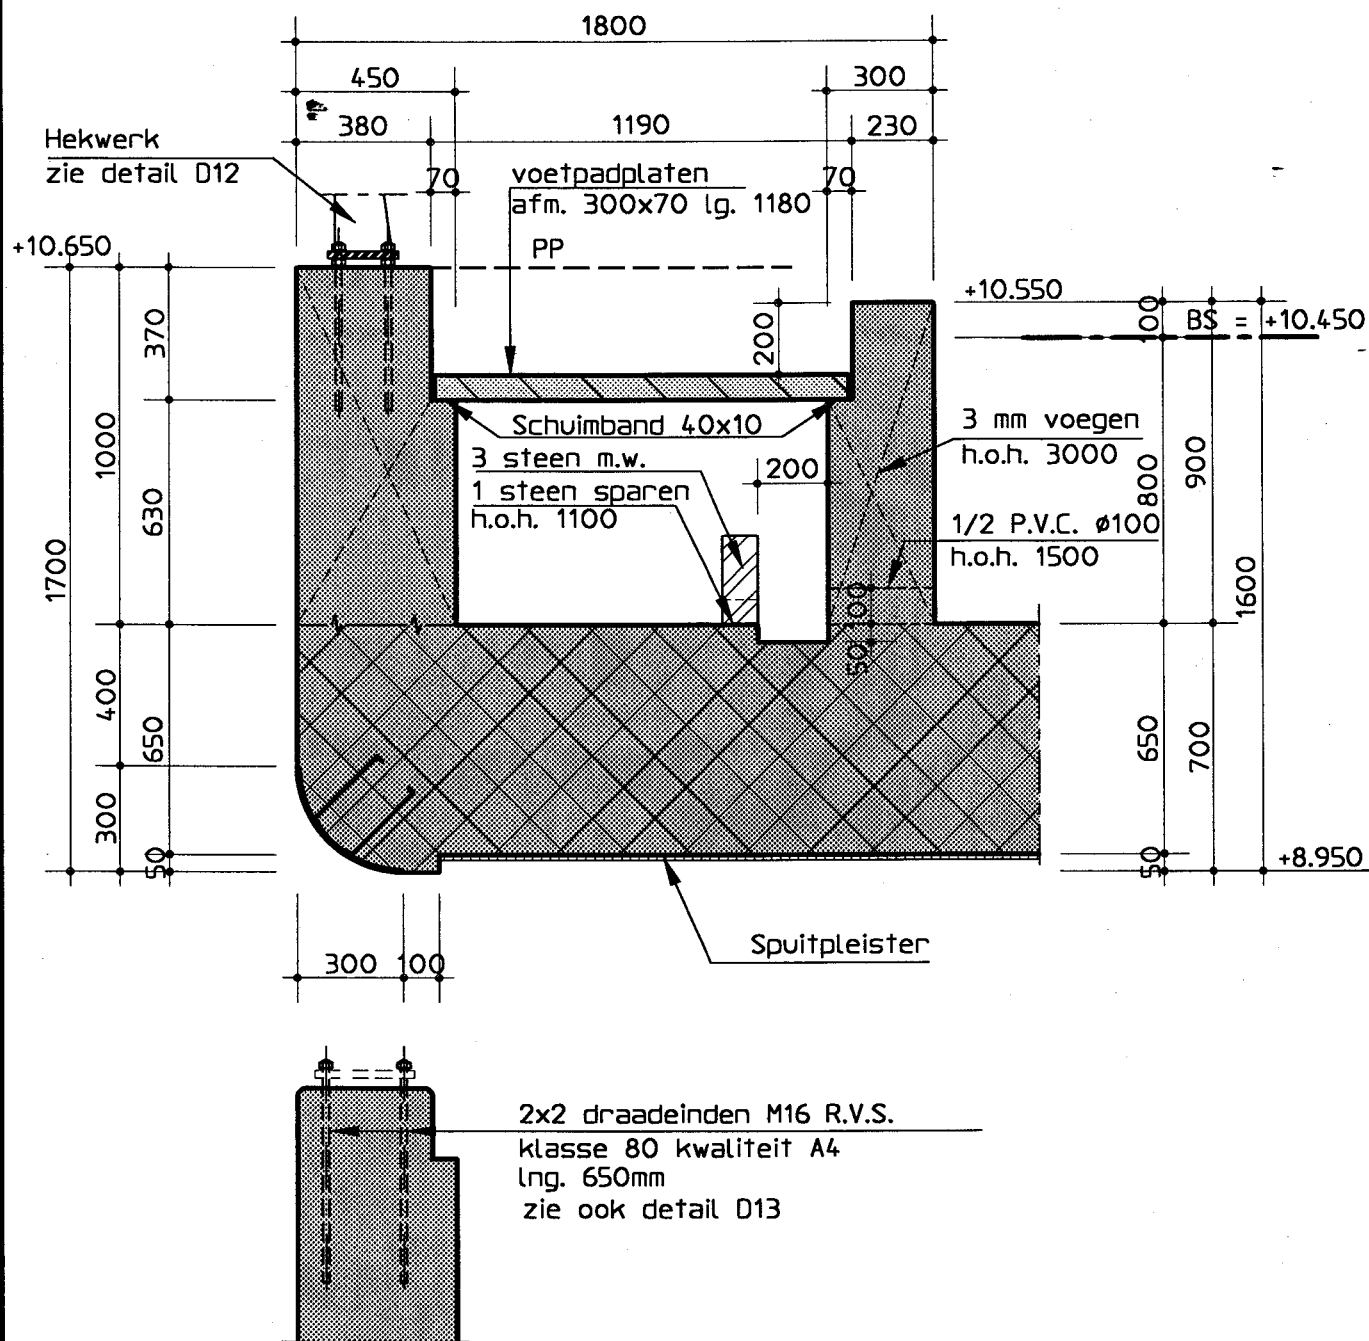

## Detail bij tijdelijk geluidscherm

1:20

N.B. In opstort zuidzijde spoordek zowel  
ankers t.b.v. hekwerk als voor tijdelijk geluidscherm opnemen

# REVISIE TOEGEPAST

datum:  
28-02-'01  
paraaf:

**ARCADIS** BOUW/INFRA



Project : Tilburg o.d.g. Campenhoef - Witbrant

Tek.nr.

Onderdeel : Detail kabelkoker


D03

Schaal : 1:20

Bestandsnaam : T:\ACAD\PROJECTS\61688214\DETAILB\D03.DWG

Xref-naam : GEEN



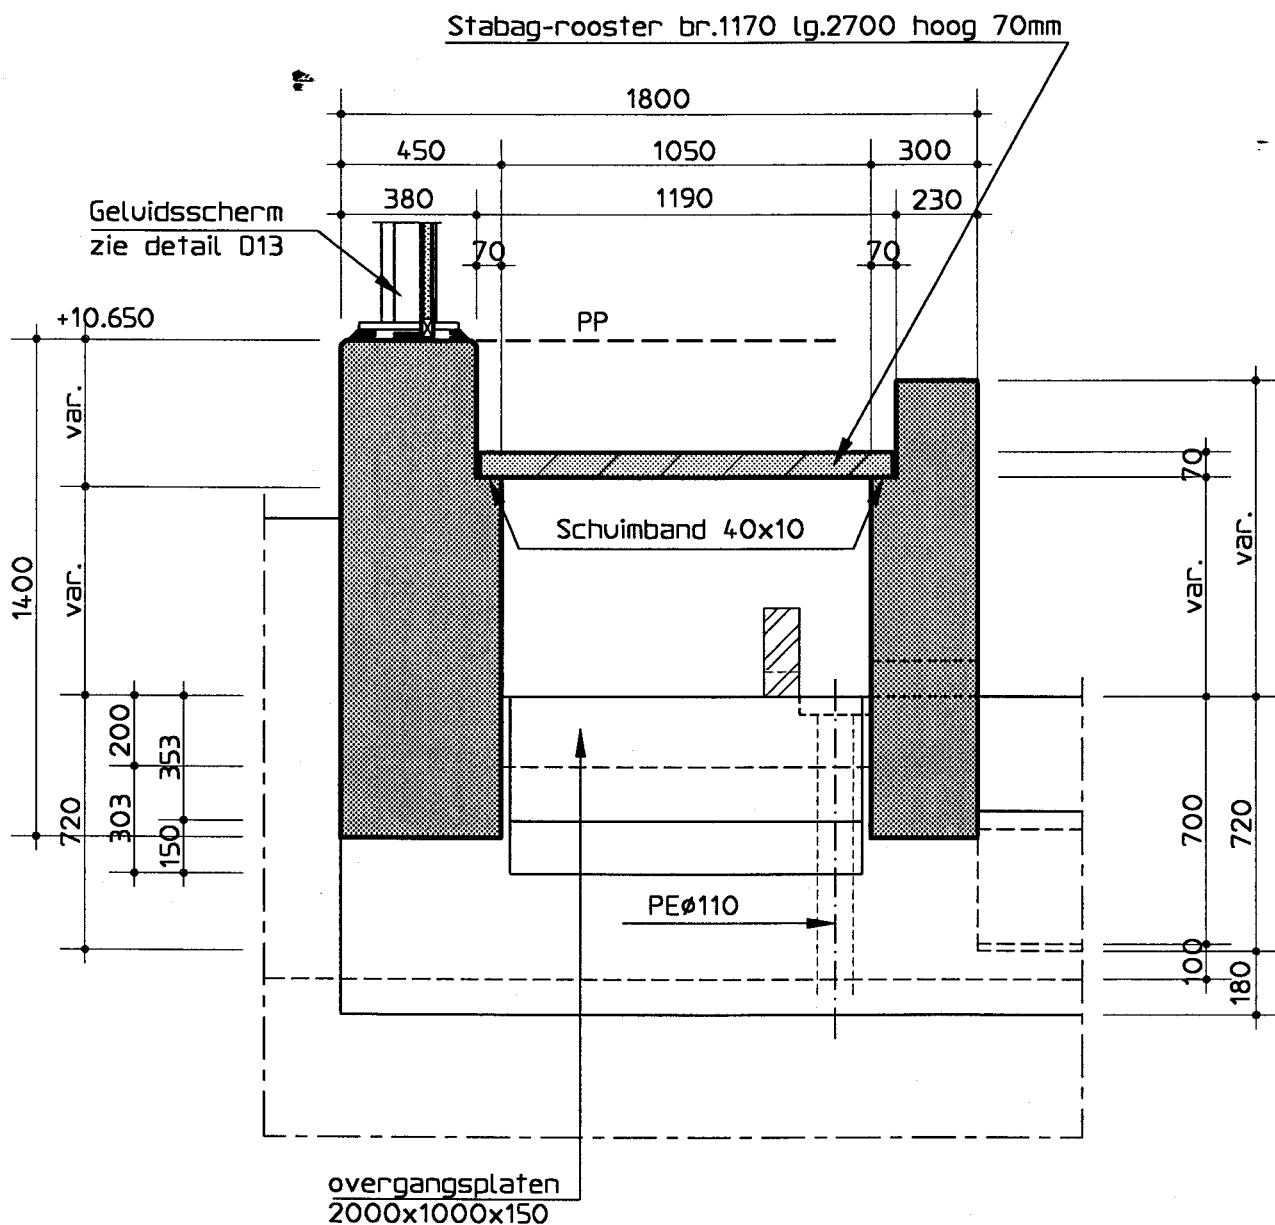

# REVISIE TOEGEPAST

datum: 28-02-01  
paraaf: [Handwritten Signature]

**ARCADIS** BOUW/INFRA



**Project** : Tilburg o.d.g. Campenhoef - Witbrant

**Tek.nr.**

**Onderdeel** : Beeindiging kabelkoker t.b.v. overgangsplaat

**D05**

**Schaal** : 1:20

**Bestandsnaam** : T:\ACAD\PROJECTS\61688214\DETAILB\D05.DWG

**Xref-naam** : GEEN

a

+10.650

Stabag-rooster br.1170 lg.2700 hoog 70mm

b.k. wand spoorzijde

Bol rooster

overgangsplaten  
2000x1000x150

PEØ110

drainagezand

filtergrind  
2-6mm.

nylondoek

PEØ250 b.o.b.= +8.050

Oplegblok  
300x200x52mm2

# REVISIE TOEGEPAST

datum:

28-02-'01

paraaf:

R

**ARCADIS** BOUW/INFRA



**Project** : Tilburg o.d.g. Campenhoef - Witbrant

**Onderdeel** : Eindkabelkoker


**Tek.nr.**

**D06**

**Schaal** : 1:20

**Bestandsnaam** : T:\ACAD\PROJECTS\61688214\DETAILB\D06.DWG

**Xref-naam** : GEEN

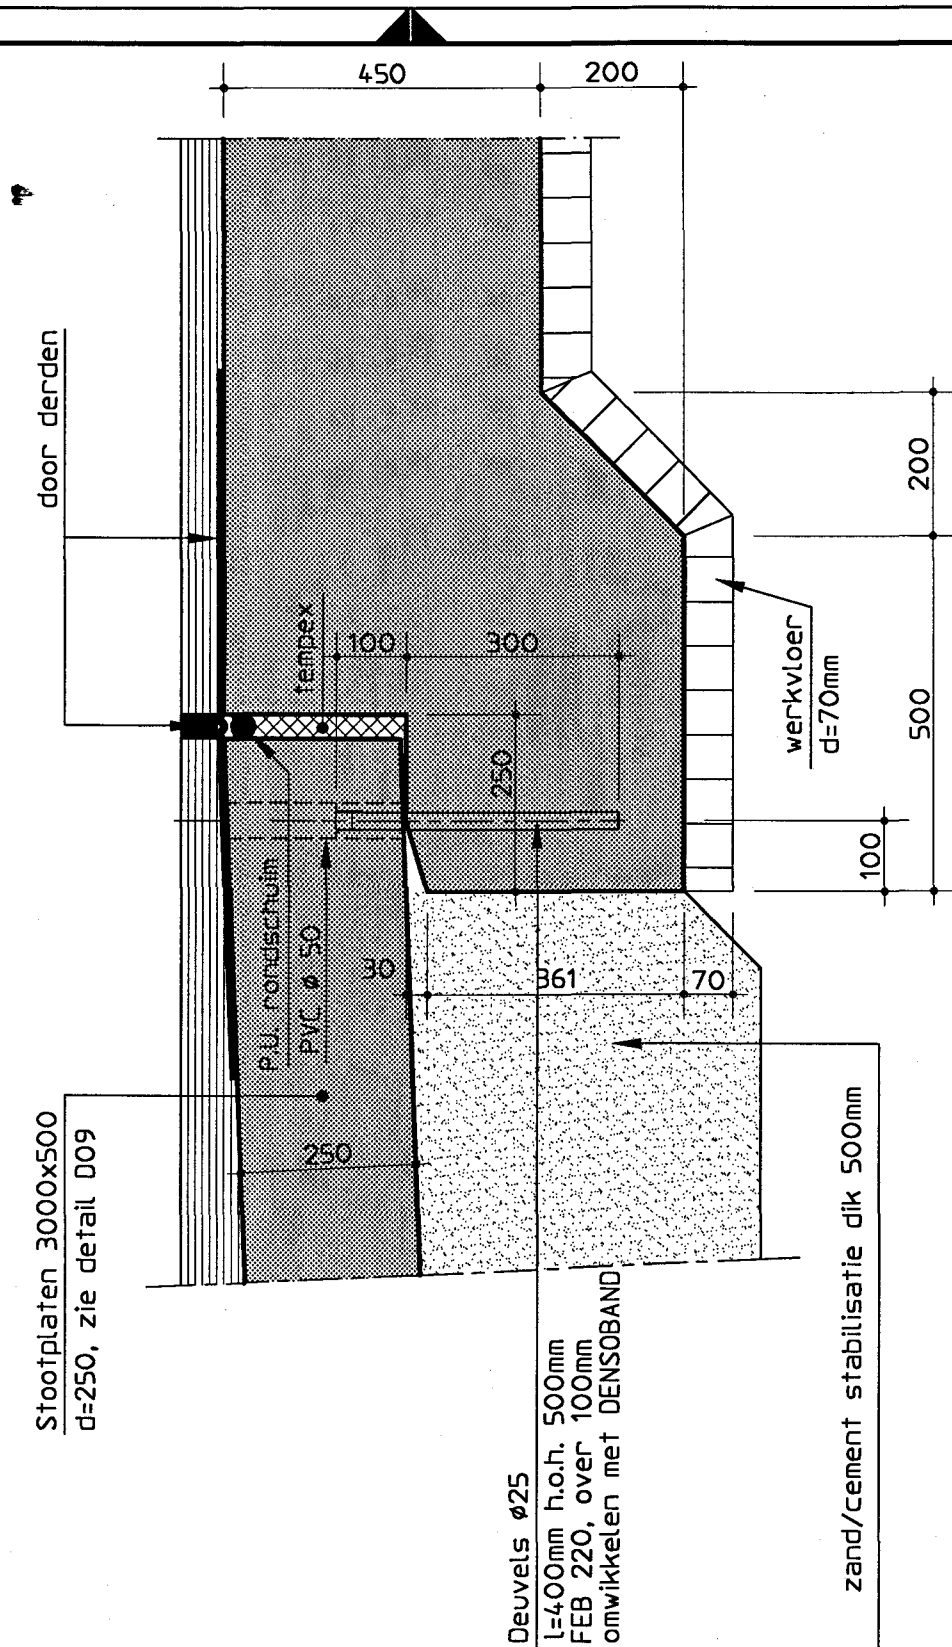

# REVISIE TOEGEPAST

datum: 28-02-01  
paraaf: *[Signature]*

**ARCADIS** BOUW/INFRA



**Project** : Tilburg o.d.g. Campenhoef - Witbrant

**Tek.nr.**


**Onderdeel** : Oplegging stootplaten t.p.v. rijwielpad

**D07**

**Schaal** : 1:10

**Bestandsnaam** : T:\ACAD\PROJECTS\61688214\DETAILB\D07.DWG

**Xref-naam** : GEEN

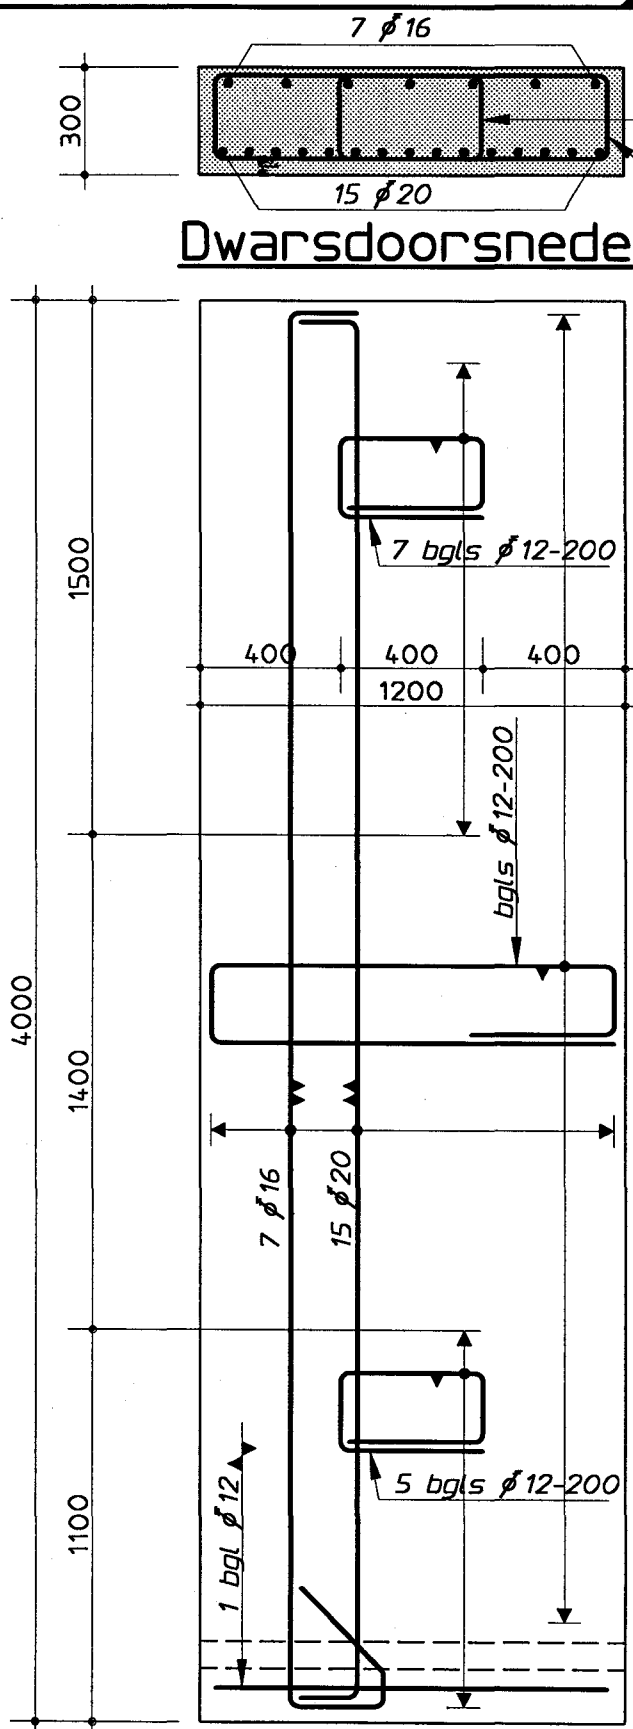


**Dwarsdoorsnede**

**Bovenaanzicht**

dekking 35 mm rondom

Totaal 18 st. ( 12 st. op het spoordek  
6 st. op het dek t.b.v. fietsverkeer )

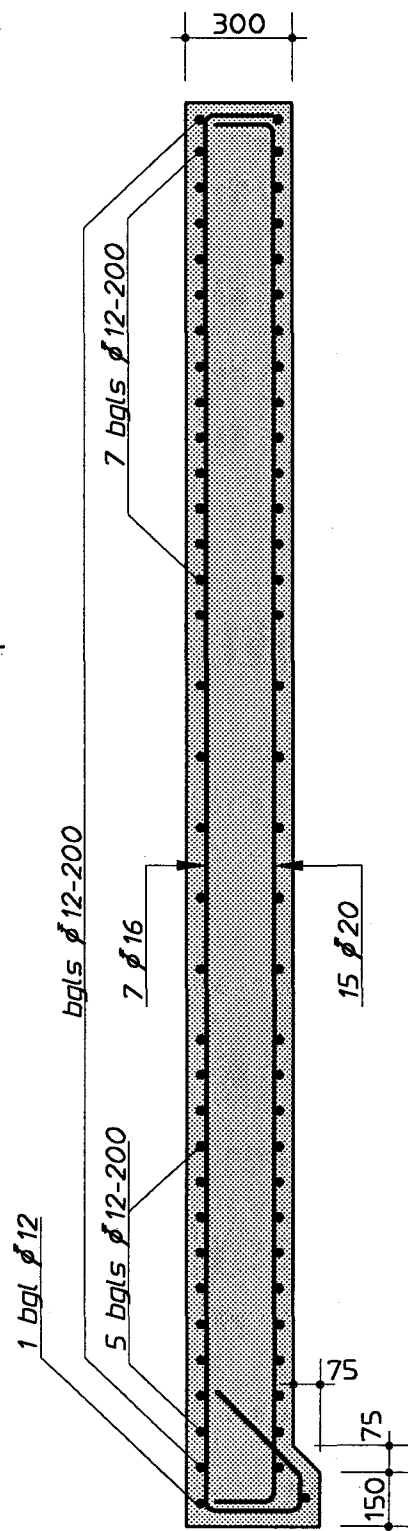

**Langsdoorsnede**

datum: 28-02-01  
paraaf: [signature]

**REVISIE TOEGEPAST**

**ARCADIS BOUW/INFRA**

Project : Tilburg o.d.g. Campenhoef - Witbrant

Onderdeel : Overgangsplaten spoor

Schaal : 1:20


Bestandsnaam : T:\ACAD\PROJECTS\61688214\DETAILB\008.DWG

Xref-naam : GEEN


Tek.nr.

**D08**



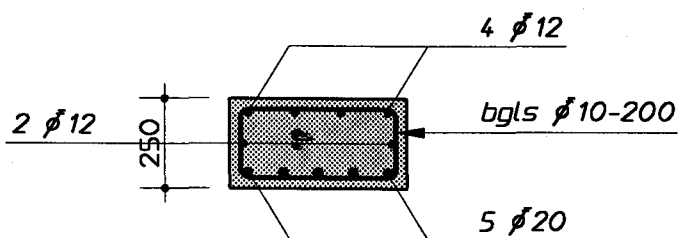


Dwarsdoorsnede

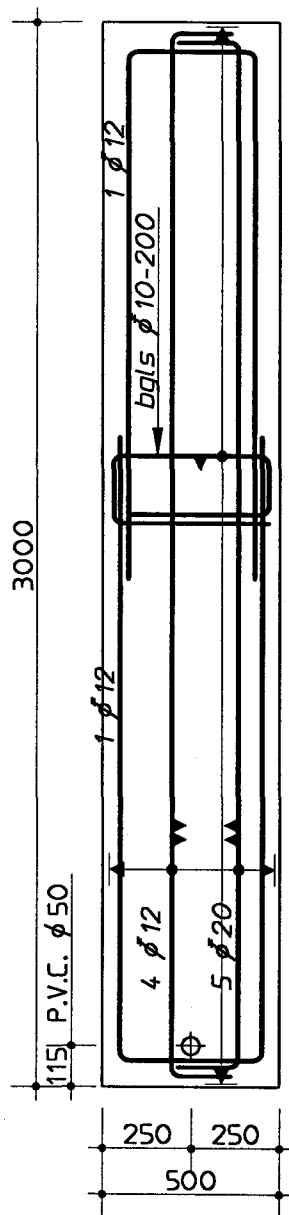

Bovenaanzicht

dekking 30 mm rondom

Totaal 14 st.

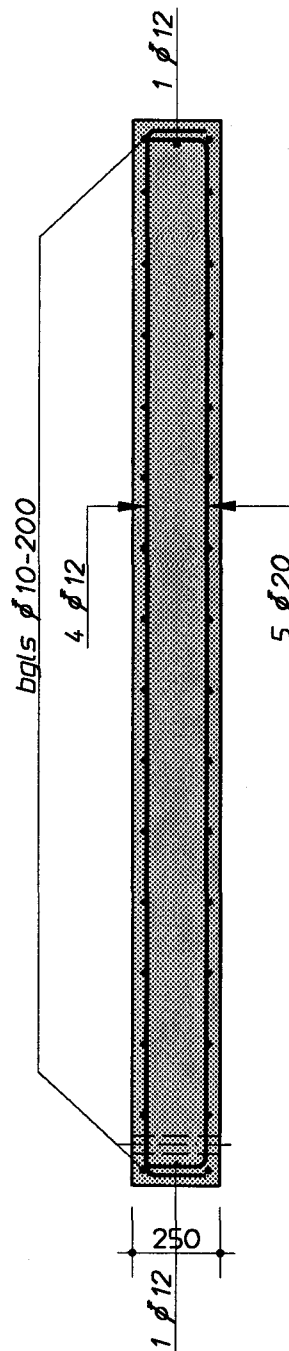

Langsdoorsnede

**REVISIE TOEGEPAST**

datum: 20-02-'01  
paraaf:

**ARCADIS** BOUW/INFRA



Project : Tilburg o.d.g. Campenhoef - Witbrant

Tek.nr.


Onderdeel : Overgangsplaten fietspad

**D09**

Schaal : 1:20

Bestandsnaam : T:\ACAD\PROJECTS\61688214\DETAILB\D09.DWG



Xref-naam : GEEN

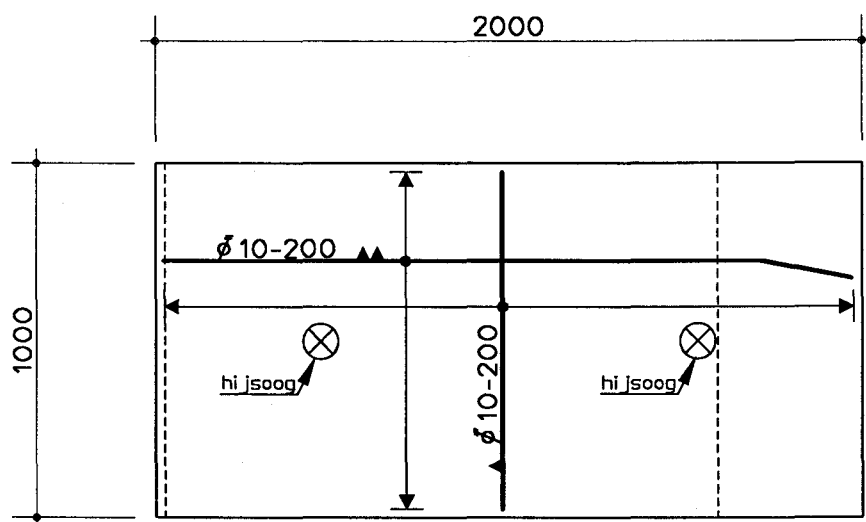

## Bovenaanzicht

1:20

4x uitv.

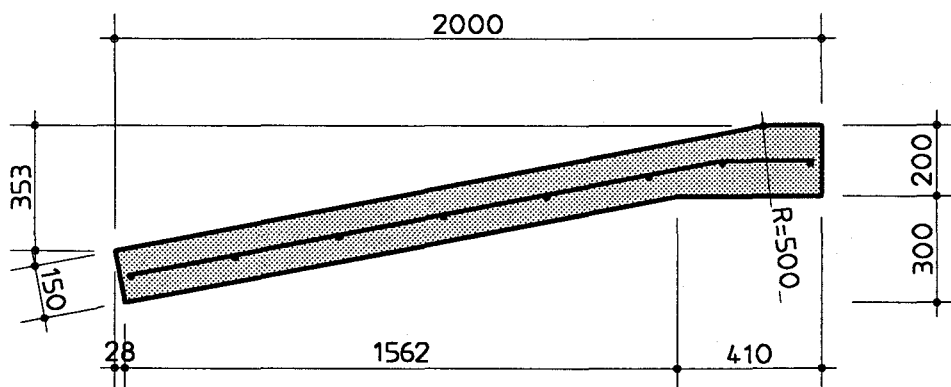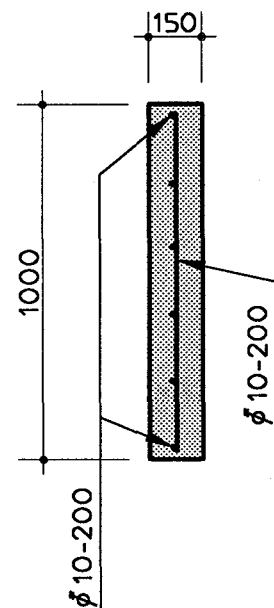

# REVISIE TOEGEPAST

datum: 28-02-'01  
paraaf: R

**ARCADIS** BOUW/INFRA



**Project** : Tilburg o.d.g. Campenhoef - Witbrant

**Tek.nr.**


**Onderdeel** : Overgangsplaten kabelgoot

**D10**

**Schaal** : 1:20


**Bestandsnaam** : T:\ACAD\PROJECTS\61688214\DETAILB\D10.DWG

**Xref-naam** : GEEN

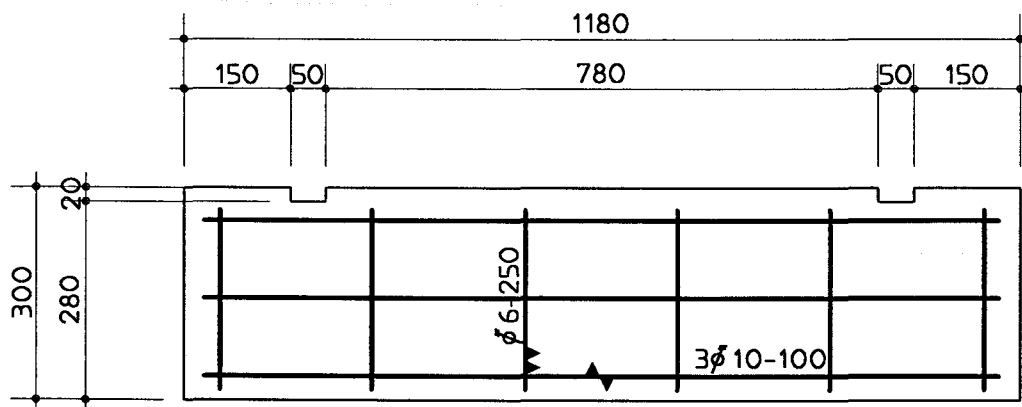


Bovenaanzicht

118x uitv.

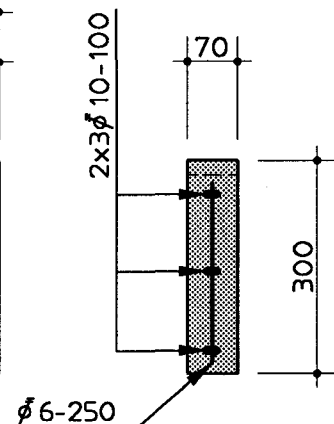

Dwarsdoorsn.

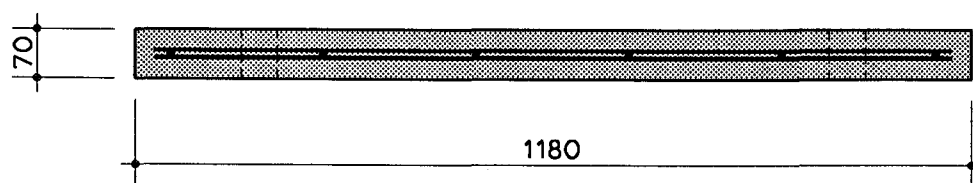

Langsdoorsnede

- maten in mm
- voetpadplaten opleggen op stroken schuimband met gesloten cellenstructuur 40x10
- stroken vooraf vastlijmen over de gehele lengte met watervaste kit

# REVISIE TOEGEPAST

datum: 28-02-01  
paraaf:

**ARCADIS** BOUW/INFRA



**Project** : Tilburg o.d.g. Campenhoef - Witbrant

**Tek.nr.**

**Onderdeel** : Voetpadplaten

**D11**


**Schaal** : 1:20

**Bestandsnaam** : T:\ACAD\PROJECTS\61688214\DETAILB\ D11.DWG

**Xref-naam** : GEEN


# REVISIE TOEGEPAST

datum: 28-02-'01  
paraaf:

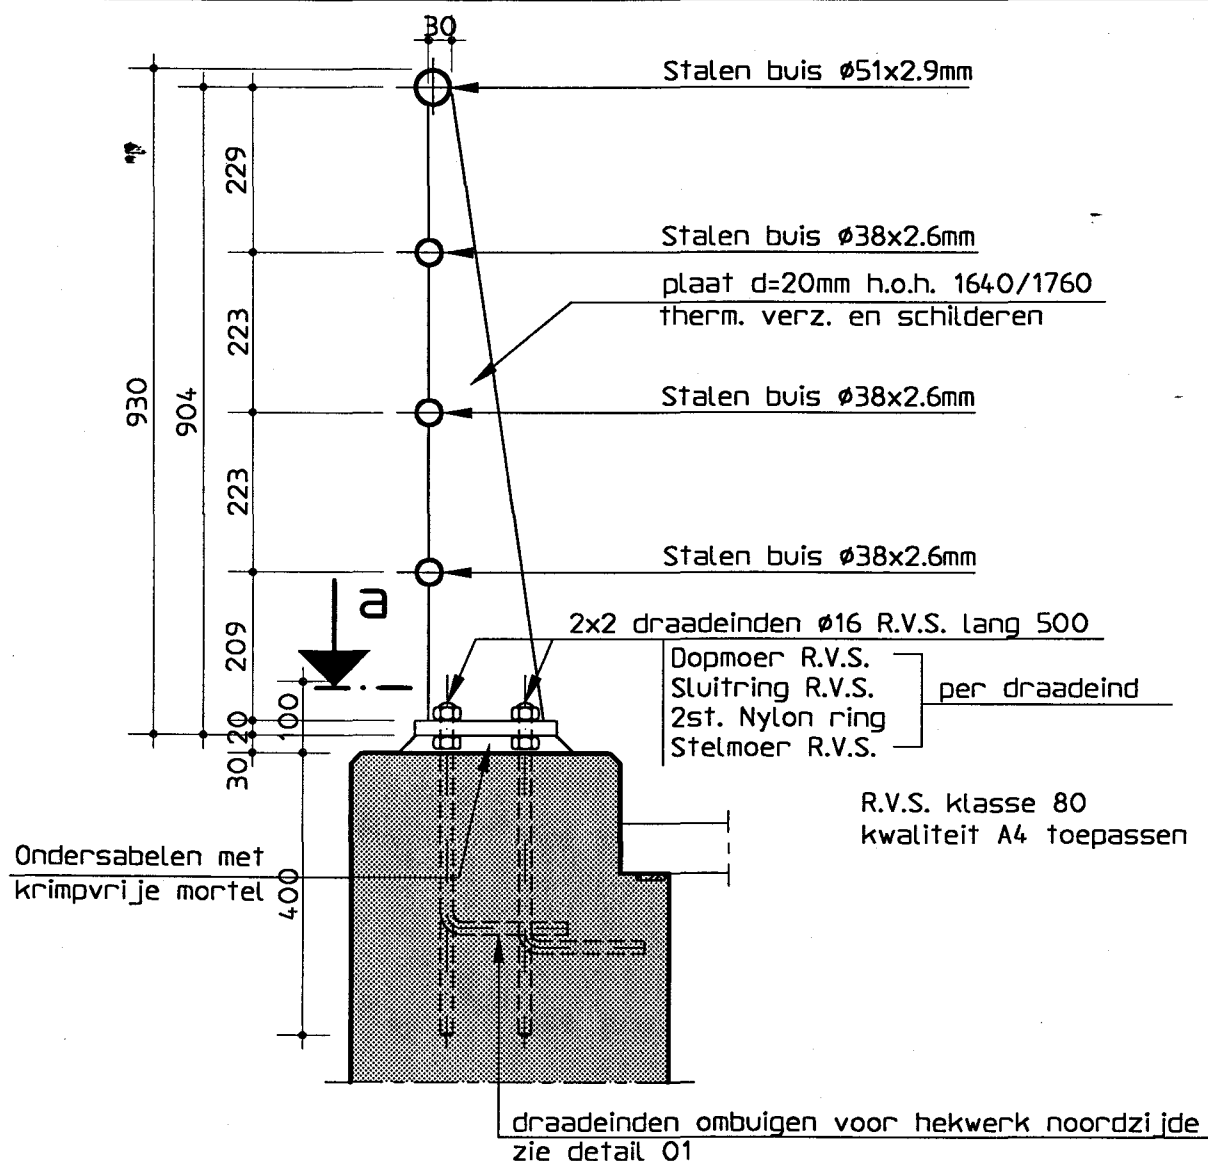


voetplaat (therm. verz.)  
200X150x20 mm

4 gaten ø 20  
t.b.v. M16

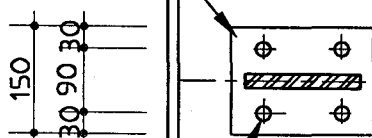

**Aanzicht a**  
1:10

4 gaten ø 20  
t.b.v. M16

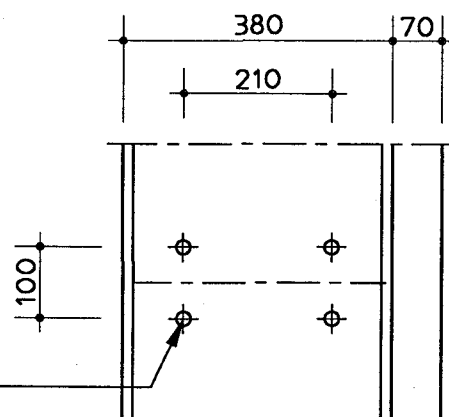

ankers geluidsscherm  
t.p.v. zuidzijde dek

**ARCADIS** BOUW/INFRA



**Project** : Tilburg o.d.g. Campenhoef - Witbrant

**Tek.nr.**


**Onderdeel** : Hekwerk t.b.v. tunneldek

**D12**

**Schaal** : 1:10

**Bestandsnaam** : T:\ACAD\PROJECTS\61688214\DETAILB\D12.DWG

**Xref-naam** : GEEN

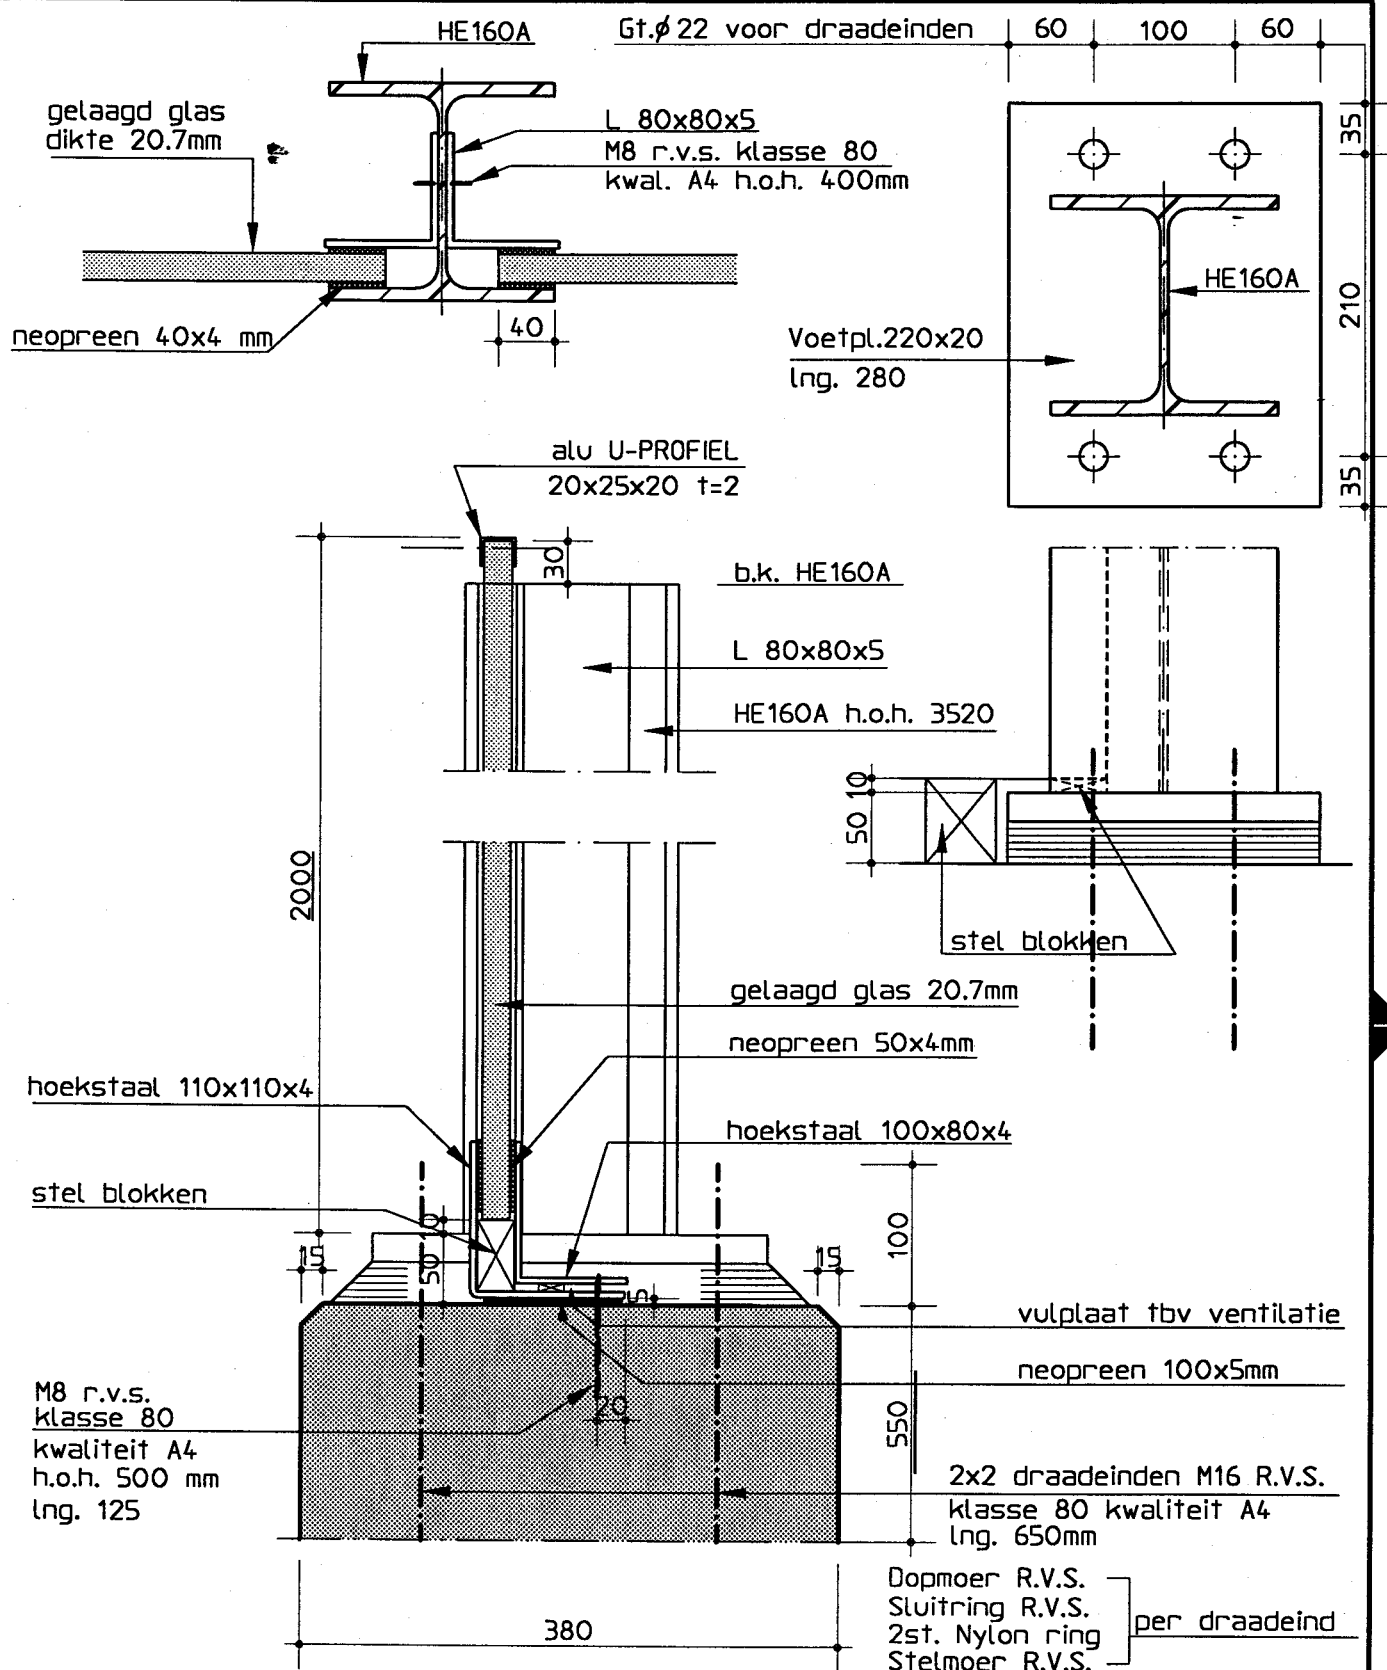

**REVISIE TOEGEPAST**

datum: 28-02-01  
paraaf: *[Signature]*

**ARCADIS BOUW/INFRA**



**Project** : Tilburg o.d.g. Campenhoef - Witbrant

**Tek.nr.**


**Onderdeel** : Geluidscherm

**D13**

**Schaal** : 1:5

**Bestandsnaam** : T:\ACAD\PROJECTS\61688214\DETAILB\D13.DWG

**Xref-naam** : GEEN

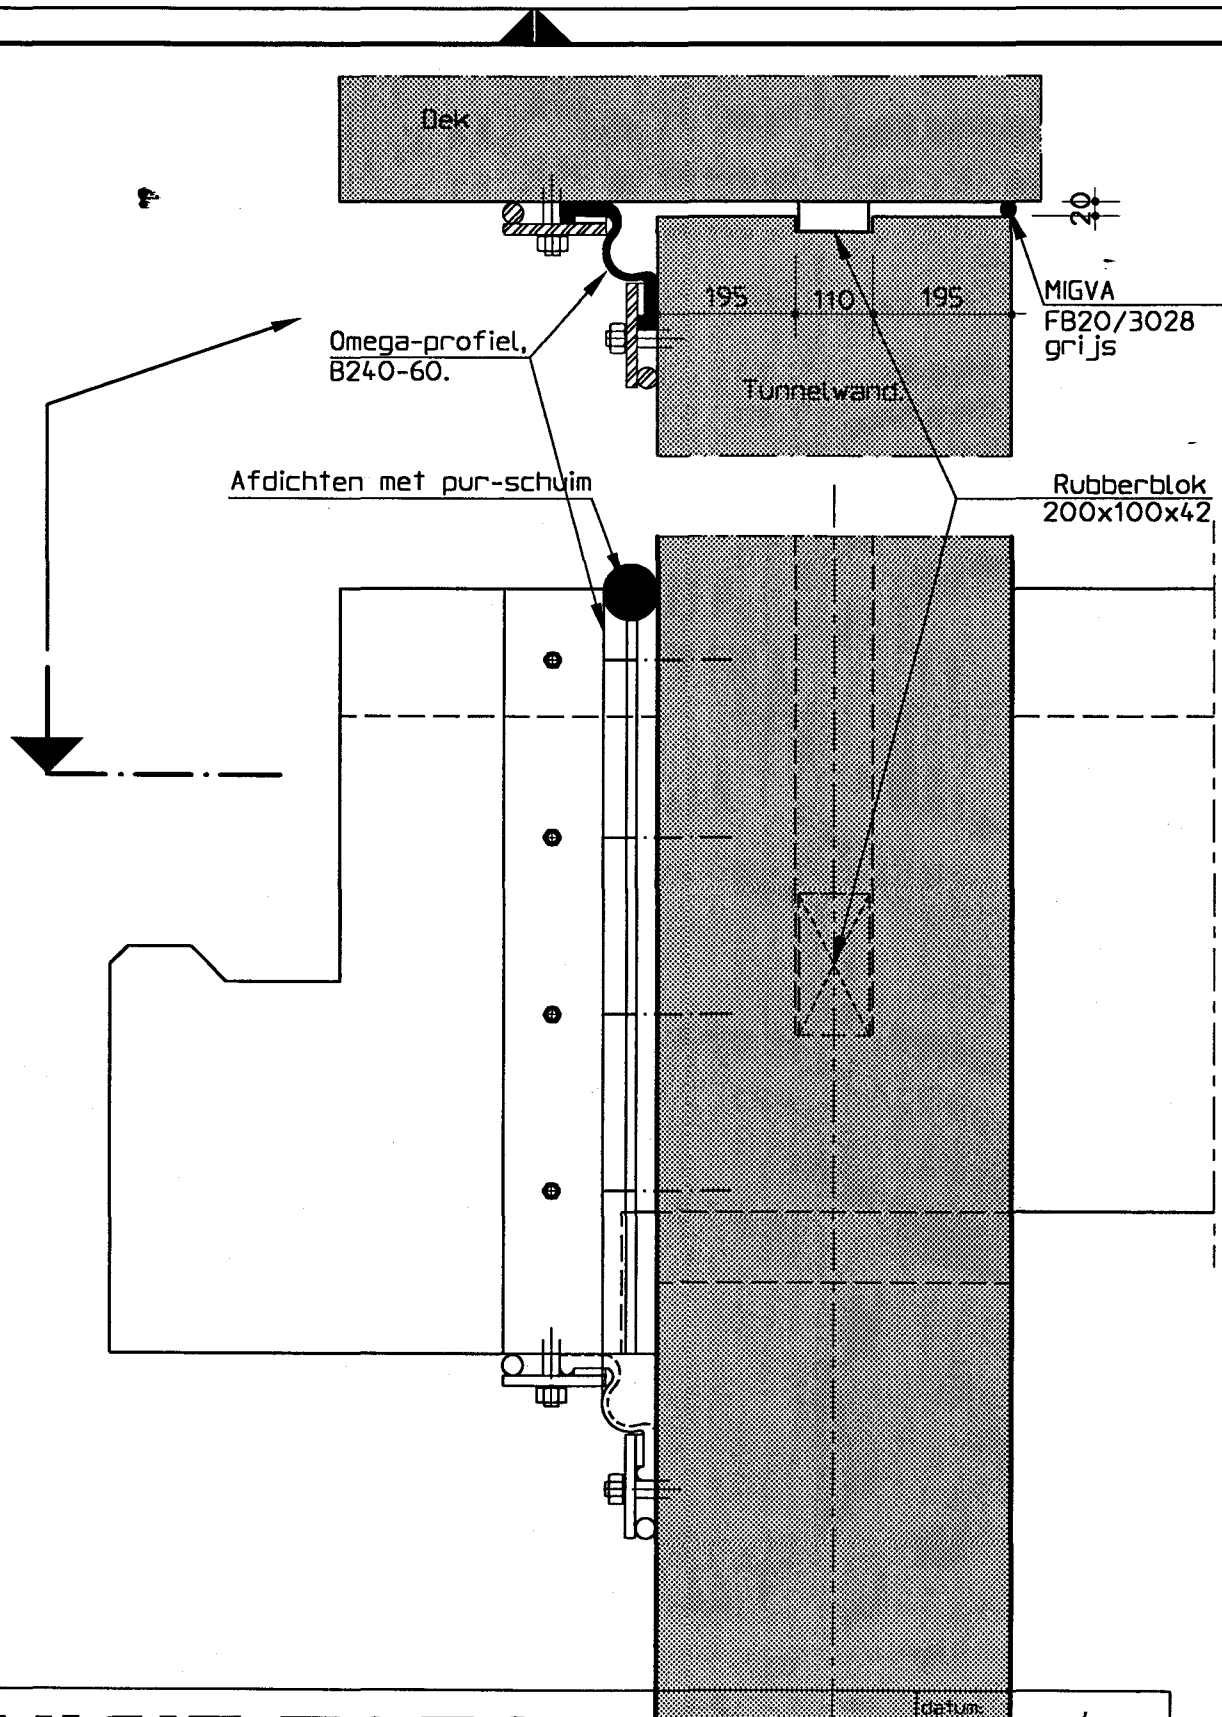

# REVISIE TOEGEPAST

datum: 28-02-'01

paraaf: *R*

**ARCADIS** BOUW/INFRA



Project : Tilburg o.d.g. Campenhoef - Witbrant

Tek.nr.



Onderdeel : Omega-profiel

D14

Schaal : 1:10

Bestandsnaam : T:\ACAD\PROJECTS\61688214\DETAILB\D14.DWG

Xref-naam : GEEN

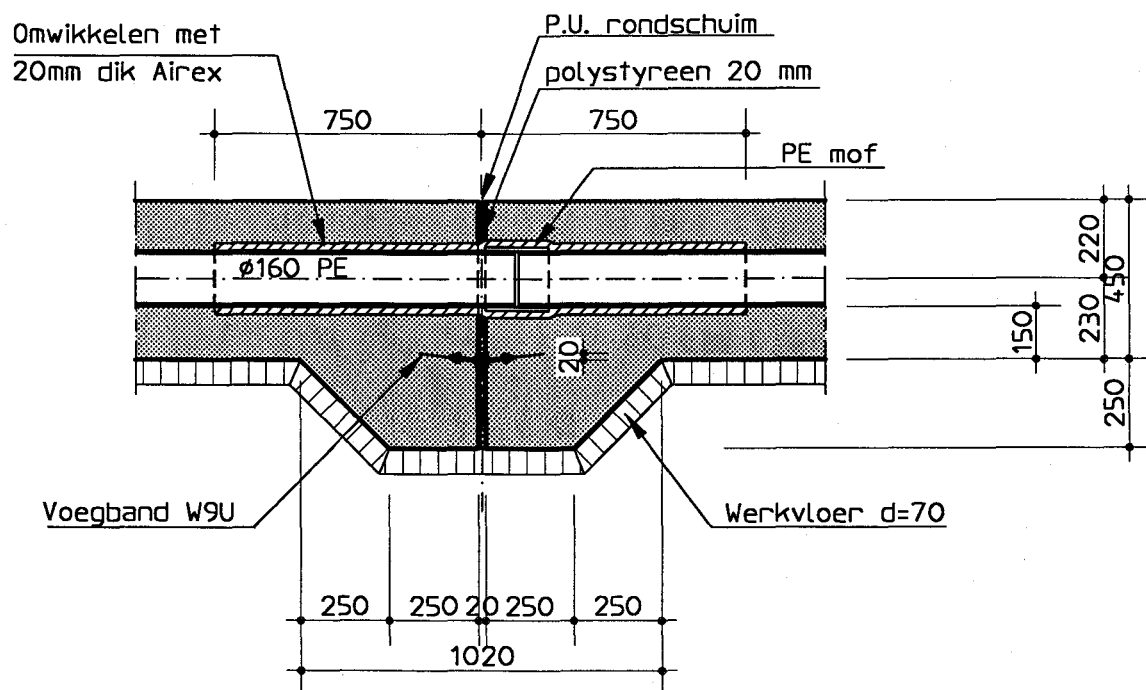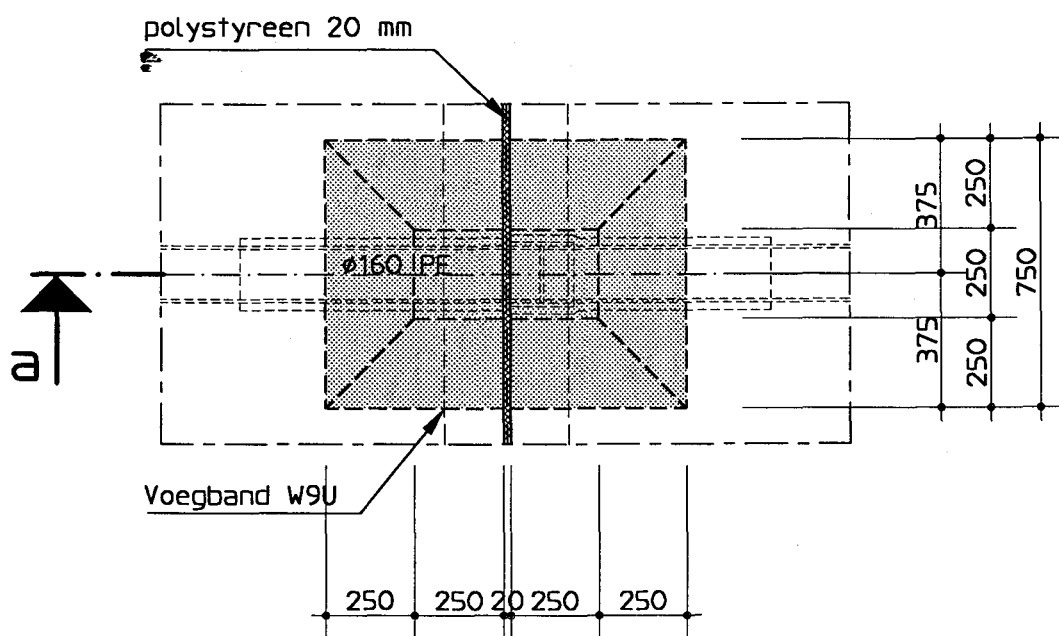

Dsn a  
1:10

# REVISIE TOEGEPAST

datum: 28-02-'01  
paraaf: *[Signature]*

**ARCADIS** BOUW/INFRA



Project : Tilburg o.d.g. Campenhoef - Witbrant

Tek.nr.


Onderdeel : Vloerverzwaring t.b.v. dilatatievoeg

D15

Schaal : 1:20

Bestandsnaam : T:\ACAD\PROJECTS\61688214\DETAILB\D15.DWG

Xref-naam : GEEN

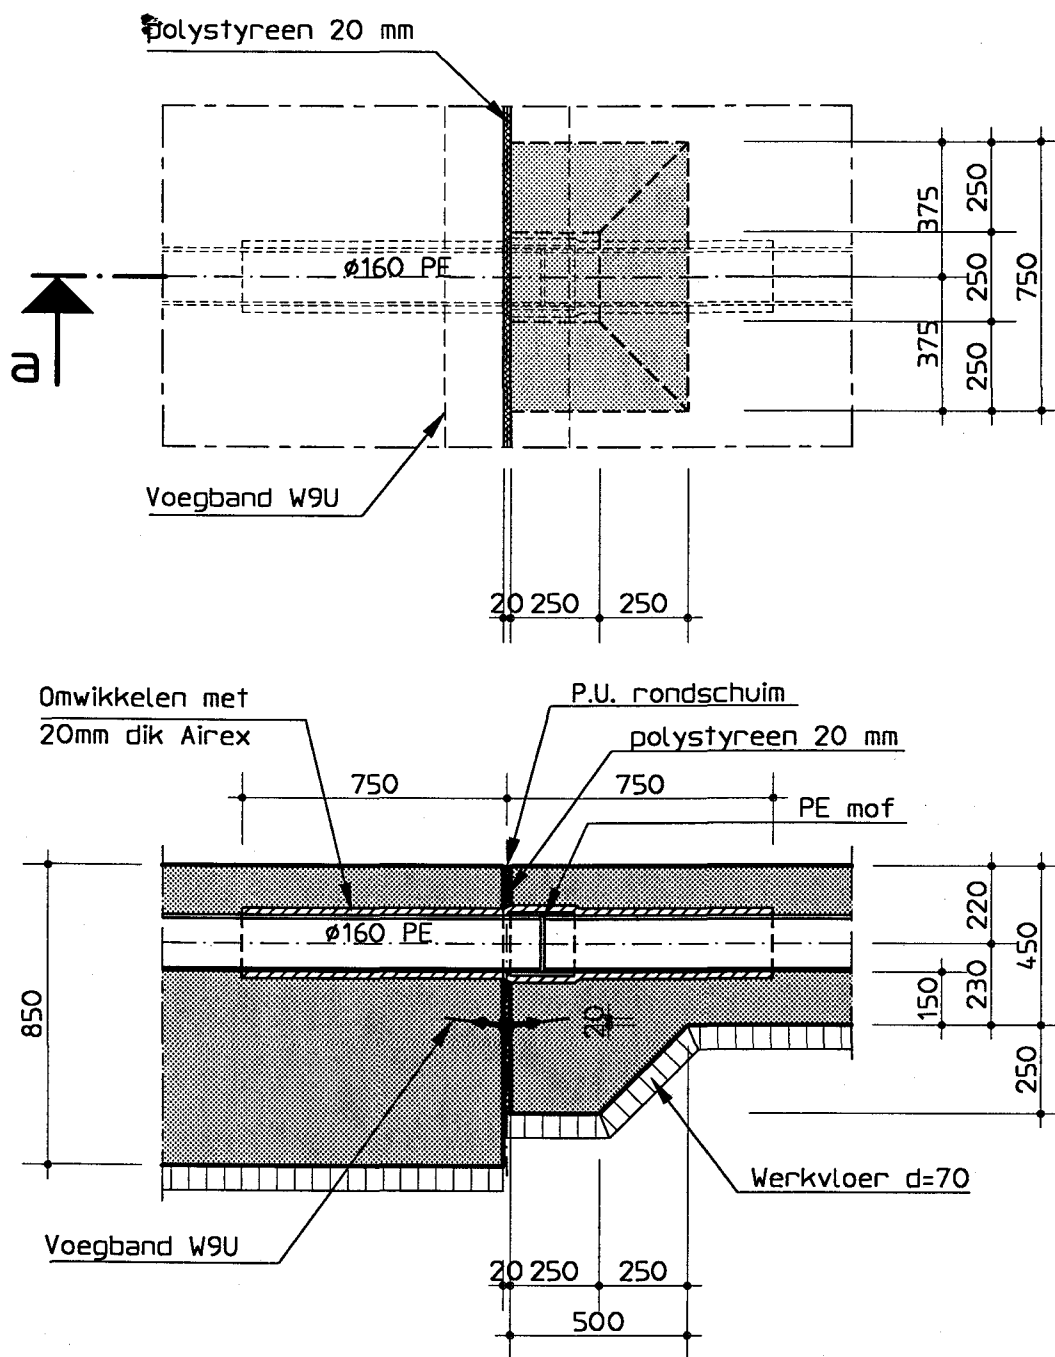

**Dsn a**  
1:10

# REVISIE TOEGEPAST

datum: 20-02-'01  
paraaf: *R*

**ARCADIS** BOUW/INFRA



**Project** : Tilburg o.d.g. Campenhoef - Witbrant

**Tek.nr.**

**Onderdeel** : Vloerverzwareing t.b.v. voeg

**D16**

**Schaal** : 1:20


**Bestandsnaam** : T:\ACAD\PROJECTS\61688214\DETAILB\D16.DWG

**Xref-naam** : GEEN

Binnenzi jde

Migua FB20/3028 grijs

vanaf 100mm onderbovenkant  
basalton

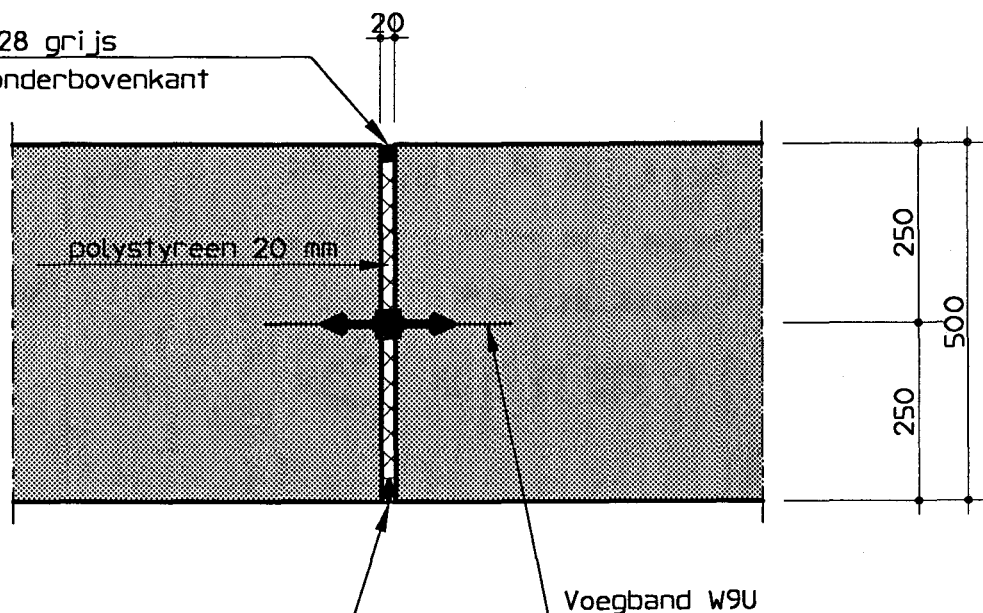


Schrumpf no. 65 tot 250mm onder M.V.

Migua FB20/3028

Baselton

Migua FB20/3028

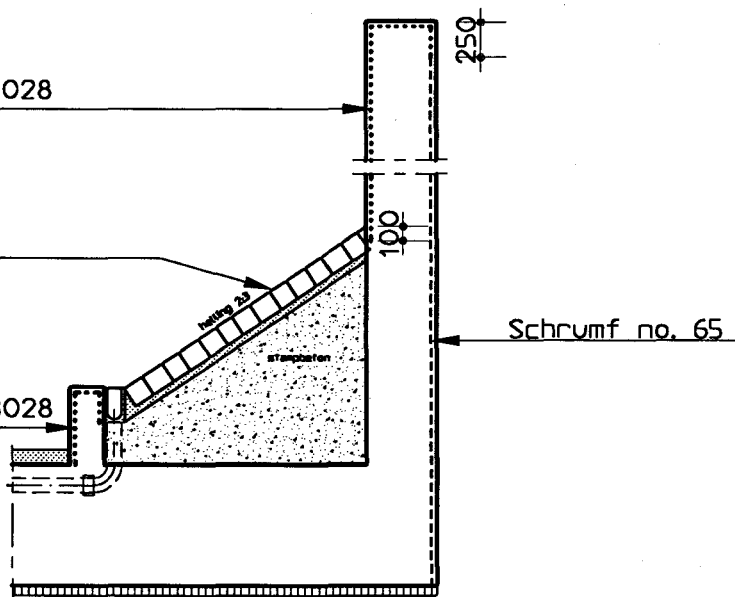

# REVISIE TOEGEPAST

datum:

20-2-'01

paraaf:

*[Handwritten signature]*



**ARCADIS** BOUW/INFRA

**Project** : Tilburg o.d.g. Campenhoef - Witbrant

**Onderdeel** : Voegdichting in de wand



**Schaal** : 1:10

**Bestandsnaam** : T:\ACAD\PROJECTS\61688214\DETAILB\017.DWG


**Xref-naam** : GEEN

**Tek.nr.**

**D17**

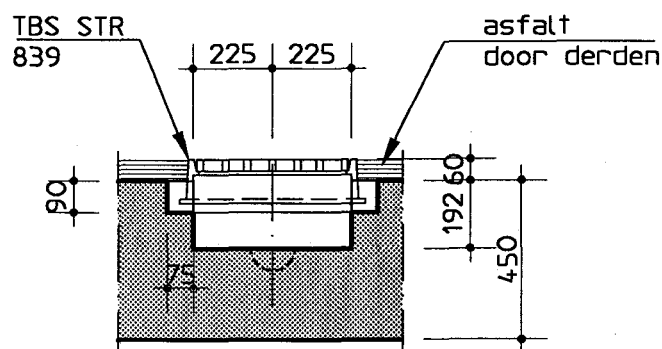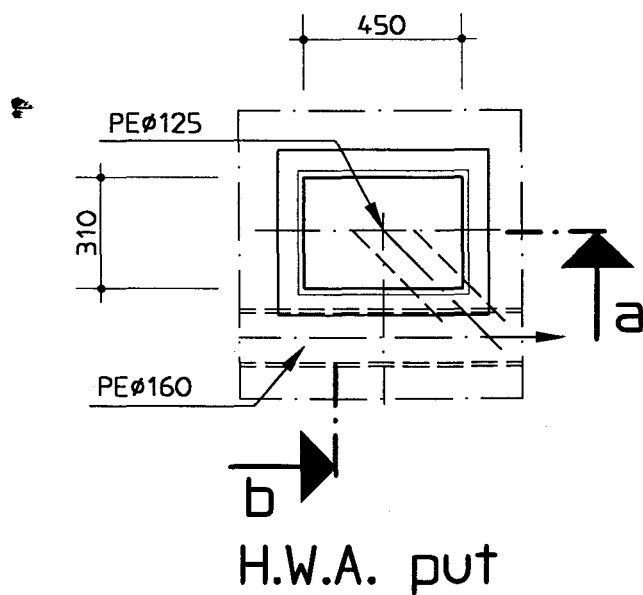

**Detail a**  
1:20

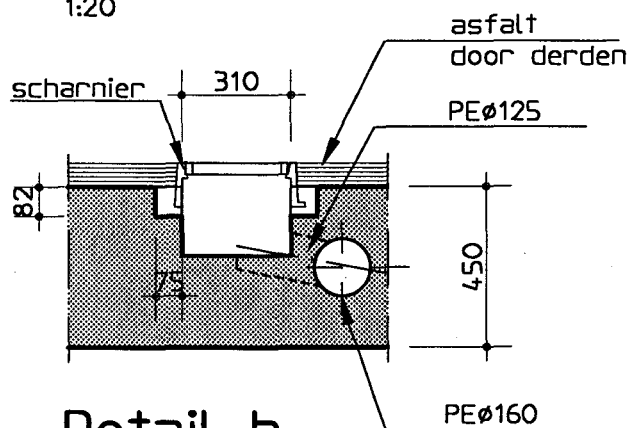

**Detail b**  
1:20

# REVISIE TOEGEPAST

datum: 28-02-'01  
paraaf: *[Signature]*

**ARCADIS** BOUW/INFRA



**Project** : Tilburg o.d.g. Campenhoef - Witbrant

**Tek.nr.**

**Onderdeel** : Hemelwaterafvoer put

**D18**


**Schaal** : 1:20

**Bestandsnaam** : T:\ACAD\PROJECTS\61688214\DETAILB\D18.DWG

**Xref-naam** : GEEN

# REVISIE TOEGEPAST

datum: 28-03-01  
paraaf: *[Handwritten Signature]*

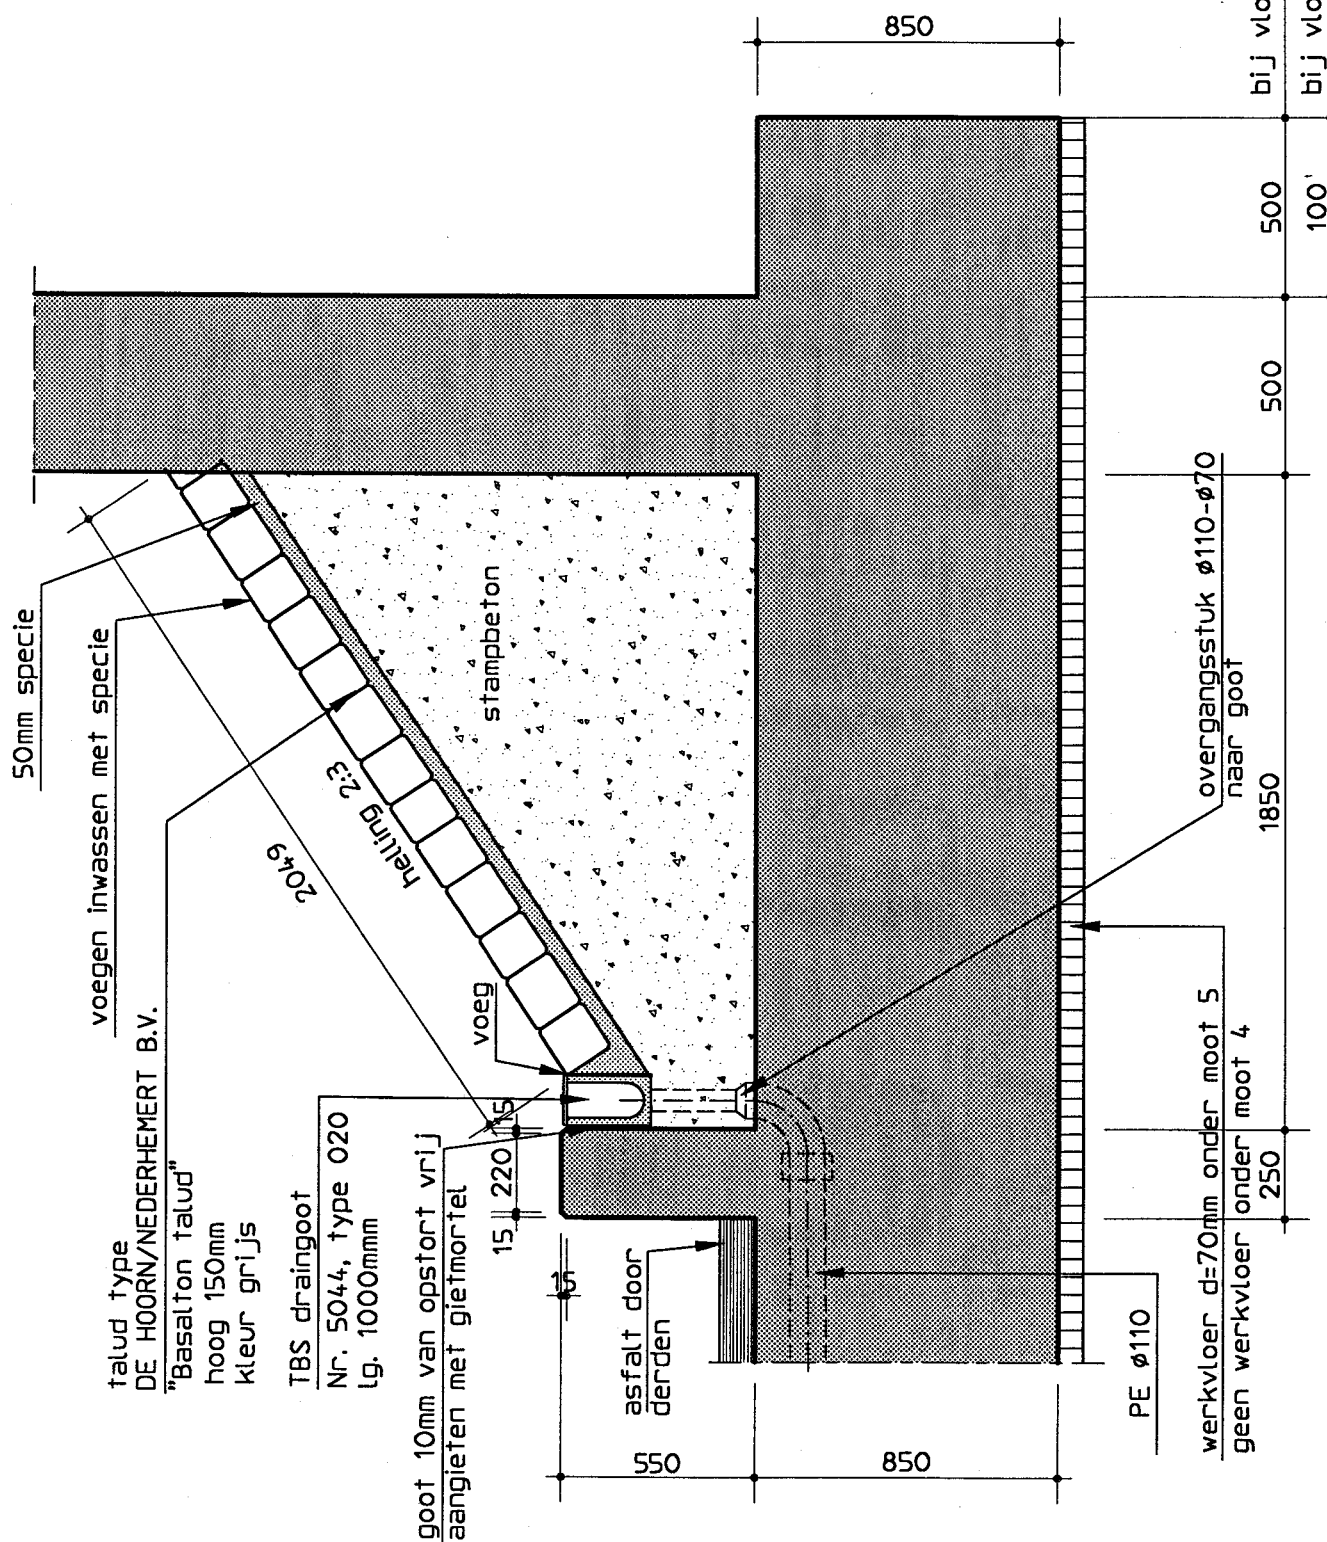

**ARCADIS** BOUW/INFRA



Project : Tilburg o.d.g. Campenhoef - Witbrant

Tek.nvr.

Onderdeel : Basalton talud

D19

Schaal : 1:20

Bestandsnaam : T:\ACAD\PROJECTS\61688214\DETAILB\D19.DWG

Xref-naam : GEEN

14X2 Demu-Vemo stekankers  
nr. 2010  $\emptyset$ 16x550

4x2, en 4x2 Demu-Vemo  
stekeinden nr.2020  
 $\emptyset$ 16x770

a

3x2, en 3x2 Demu-Vemo  
stekeinden nr.2020  
 $\emptyset$ 16x770

3x2, en 3x2 Demu-Vemo  
stekeinden nr.2020  
 $\emptyset$ 16x770

14X2 Demu-Vemo stekankers  
nr. 2010  $\emptyset$ 16x550

Pakor slang

4x2, en 4x2 Demu-Vemo  
stekeinden nr.2020  
 $\emptyset$ 16x770

14X2 Demu-Vemo stekankers  
nr. 2010  $\emptyset$ 16x550

4x2, en 4x2 Demu-Vemo  
stekeinden nr.2020  
 $\emptyset$ 16x770

aanvullen met beton

rondgaande strip  
200x5mm

Tempex dik 100mm

Stalen hulppaal  
minimaal 100mm onder vloernivo  
afbranden, ruimte opvullen  
met zand

VERVALLEN

ARCADIS BOUW/INFRA



Project : Tilburg o.d.g. Campenhoef - Witbrant

Tek.nr.


Onderdeel : Afdichting t.p.v. hulppaal

D20

Schaal : 1:20

Bestandsnaam : T:\ACAD\PROJECTS\61688214\DETAILB\020.DWG

Xref-naam : GEEN

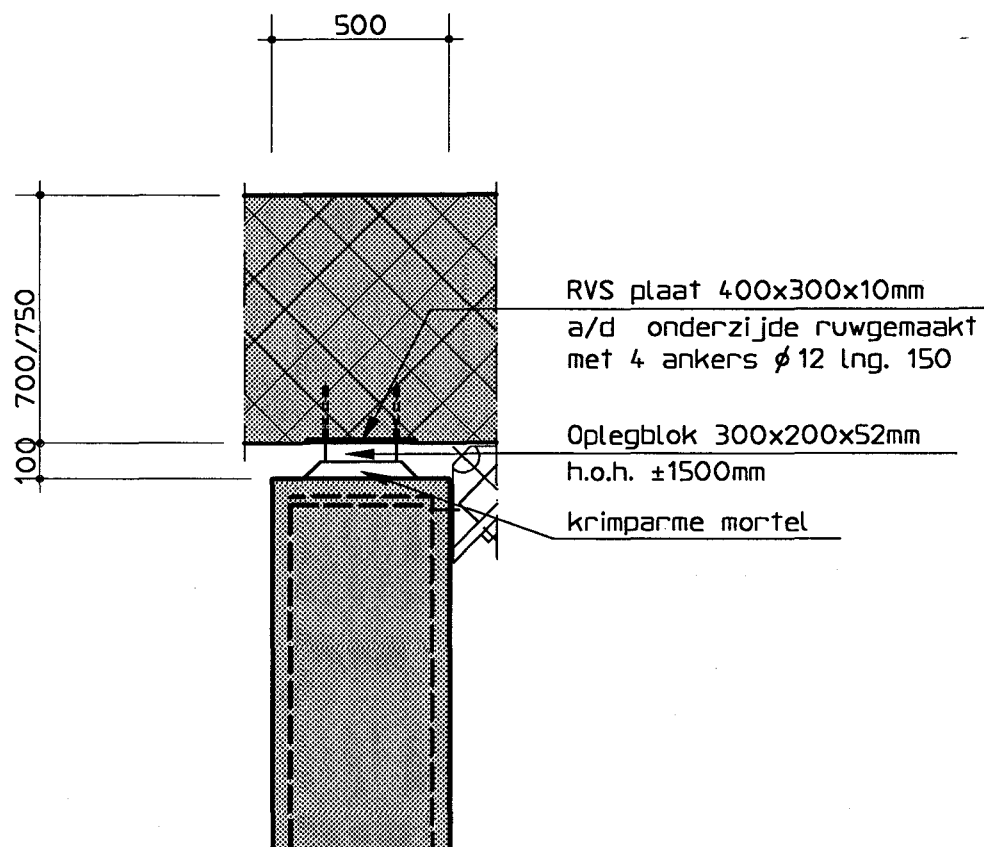

# REVISIE TOEGEPAST

datum: 28-02-'01  
paraaf: *[Handwritten signature]*

**ARCADIS** BOUW/INFRA



**Project** : Tilburg o.d.g. Campenhoef - Witbrant

**Tek.nr.**


**Onderdeel** : Aansluiting dek-wand spoordeel

**D21**

**Schaal** : 1:20


**Bestandsnaam** : T:\ACAD\PROJECTS\61688214\DETAILB\021.DWG

**Xref-naam** : GEEN

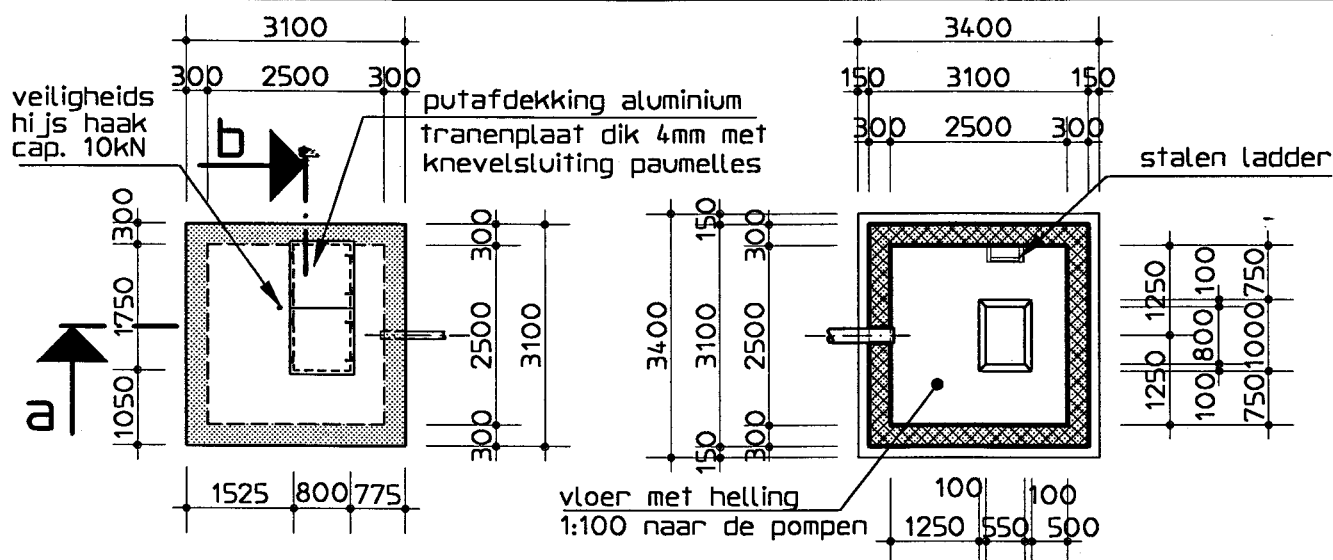

**Bovenaanzicht put**  
1:100

**Dsn c**  
1:100

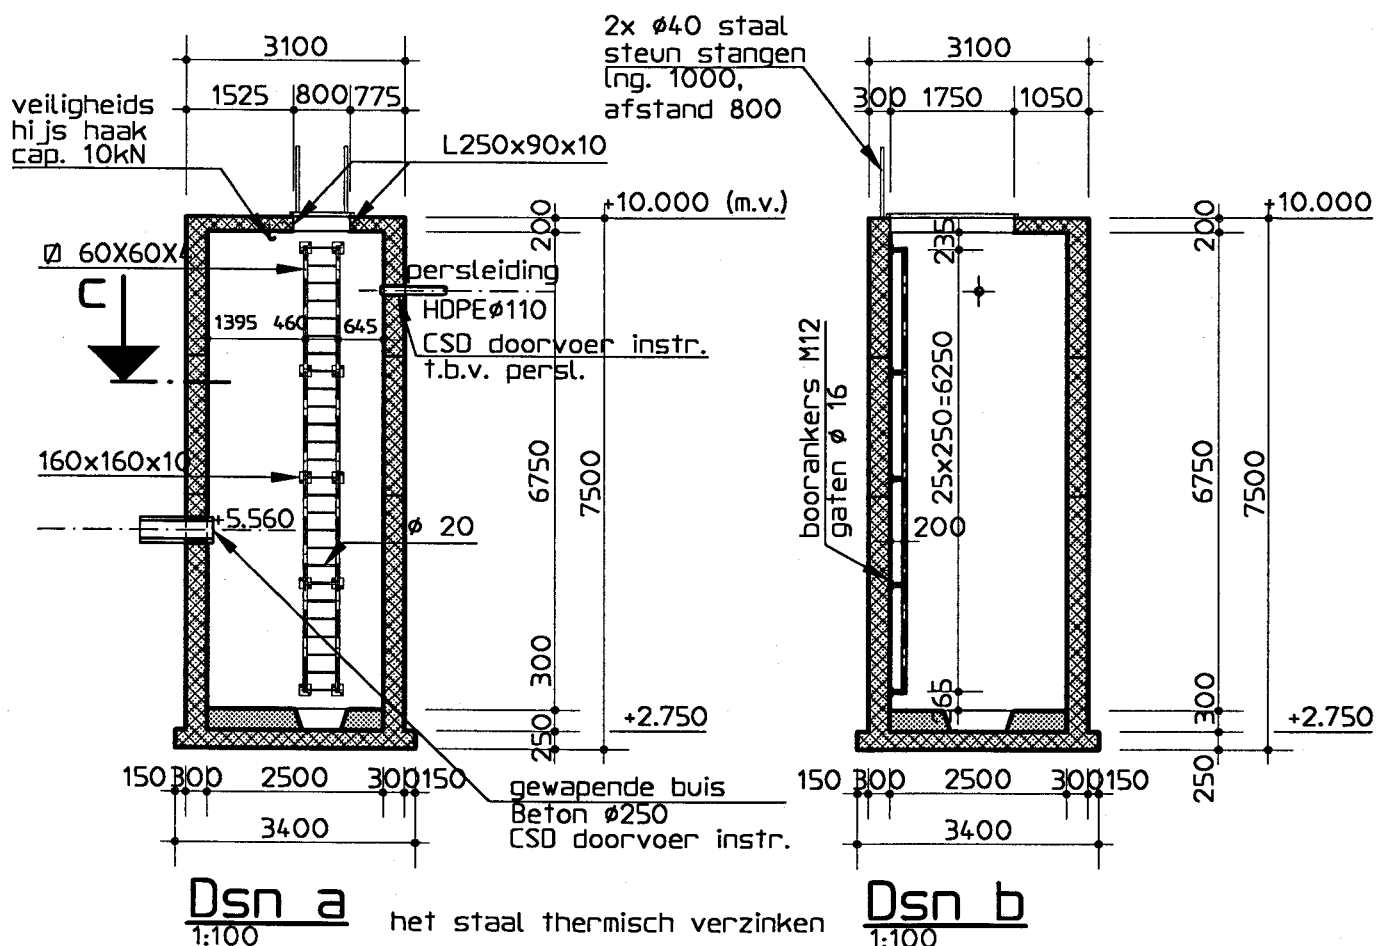

**Dsn a**  
1:100

**Dsn b**  
1:100

**REVISIE TOEGEPAST**

datum: 28-02-01  
paraaf: [signature]

**ARCADIS BOUW/INFRA**



**Project** : Tilburg o.d.g. Campenhoef - Witbrant

**Tek.nr.**


**Onderdeel** : Prefab-pompput

**D22**

**Schaal** : 1:100

**Bestandsnaam** : T:\ACAD\PROJECTS\61688214\DETAILB\022.DWG

**Xref-naam** : GEEN

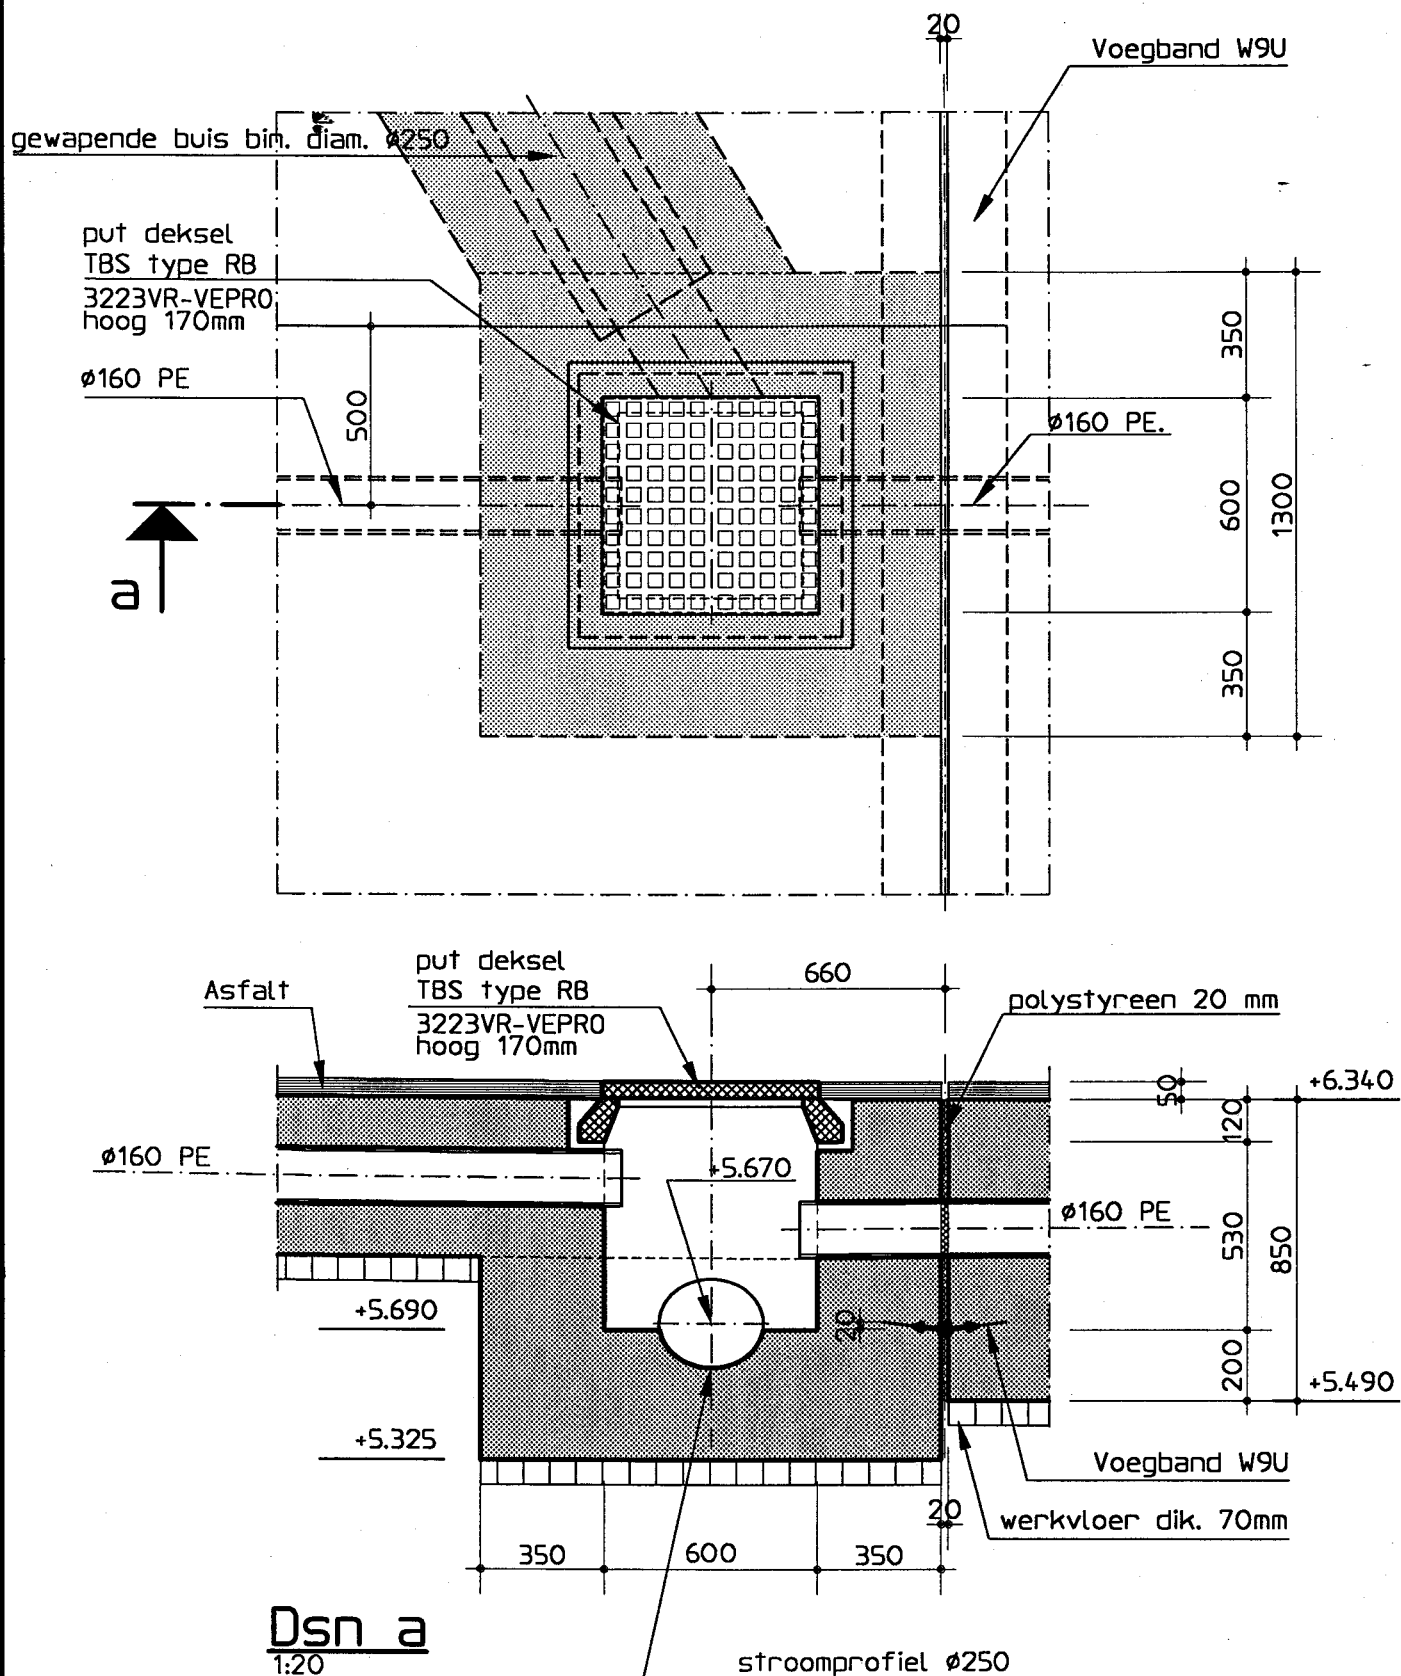

ARCADIS BOUW/INFRA

REVISIE TOEGEPAST

datum  
28-02-01  
paraaf



Project : Tilburg o.d.g. Campenhoef - Witbrant

Tek.nr.


Onderdeel : Afvoerput

D23

Schaal : 1:20

Bestandsnaam : T:\ACAD\PROJECTS\61688214\DETAILB\D23.DWG

Xref-naam : GEEN

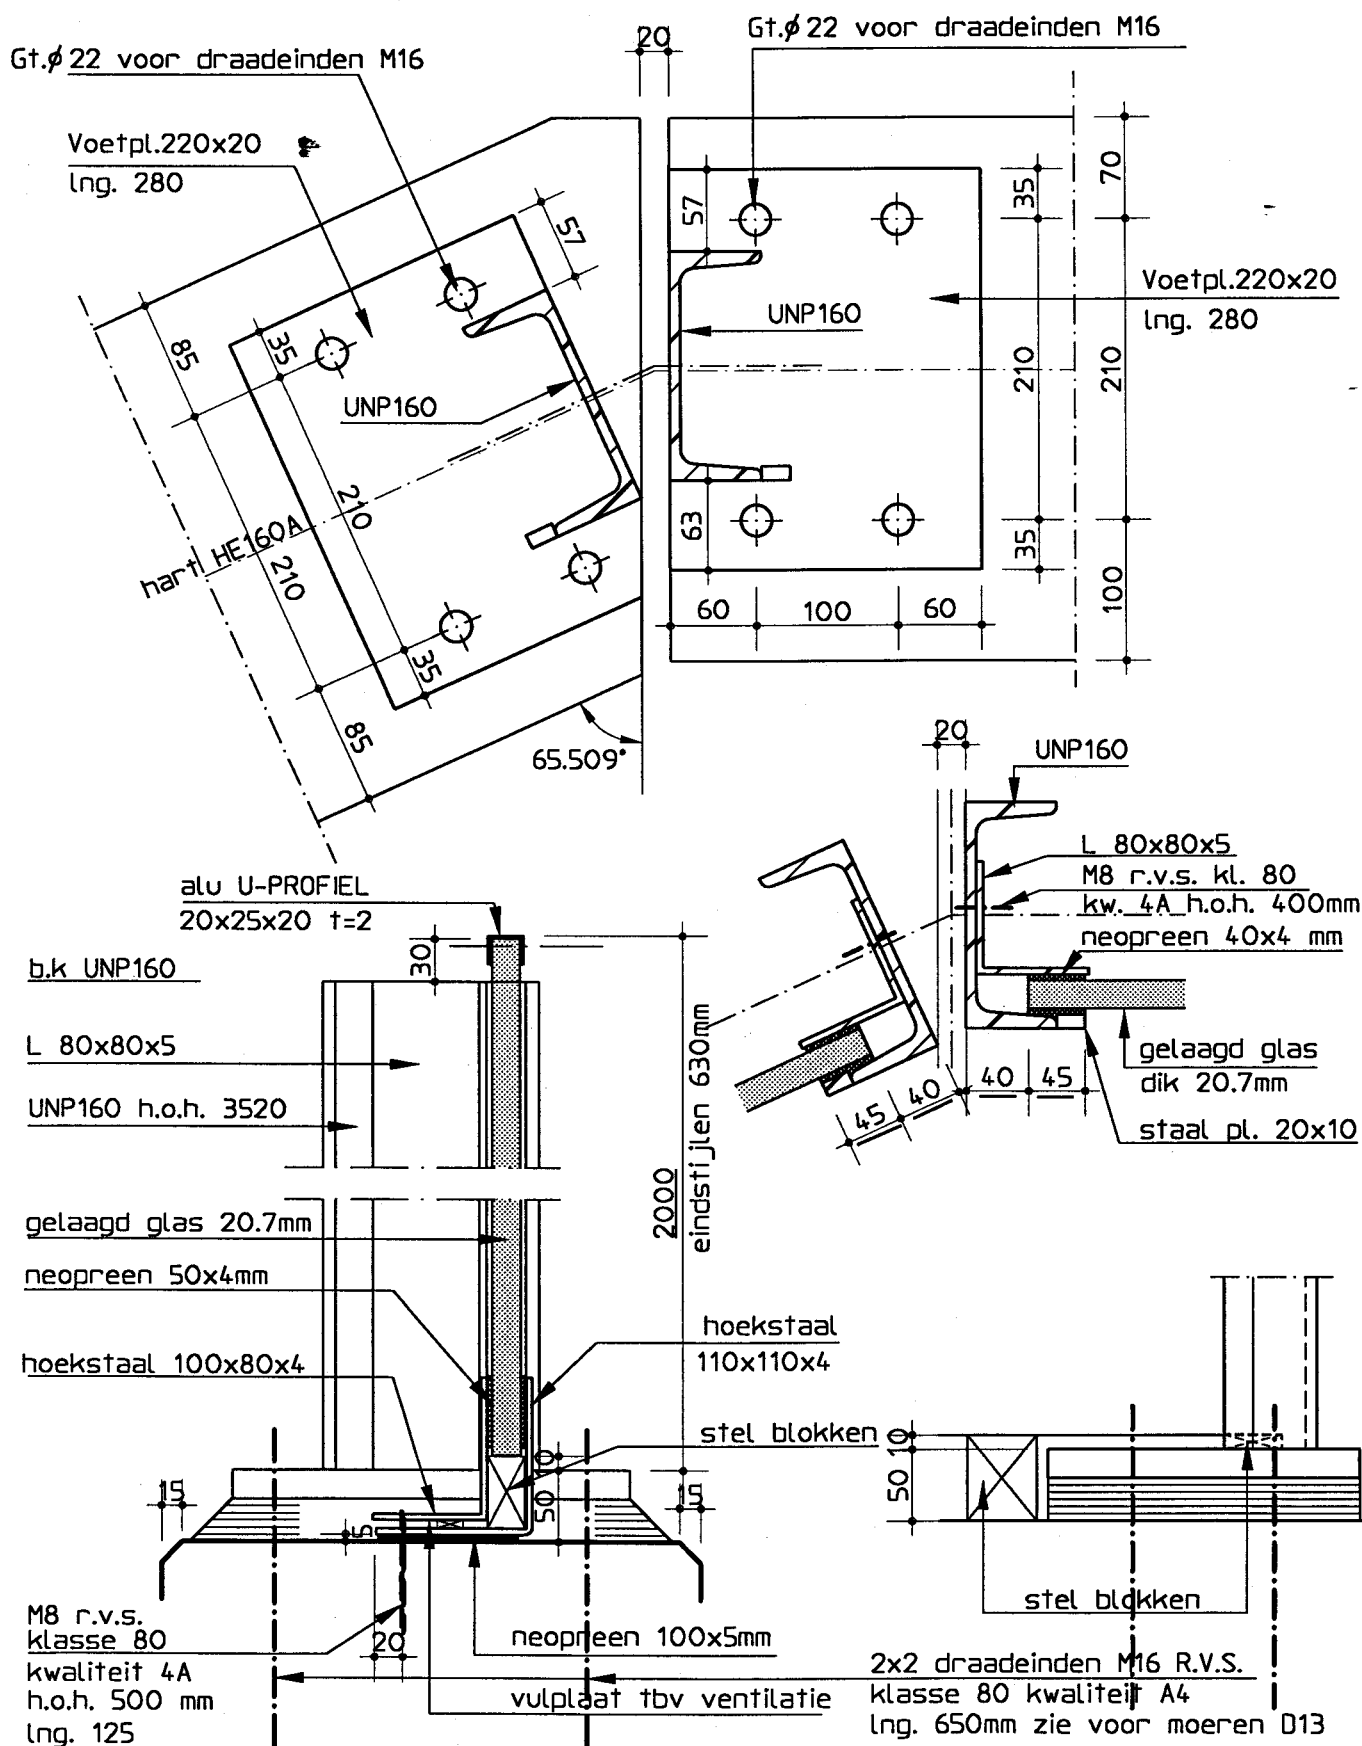

**ARCADIS** BOUW/INFRA

**REVISIE TOEGEPAST**

datum: 20-29-01  
paraaf:



**Project** : Tilburg o.d.g. Campenhoef - Witbrant

**Tek.nr.**


**Onderdeel** : Geluidscherm t.p.v. dilatatievoeg

**D24**

**Schaal** : 1:5


**Bestandsnaam** : T:\ACAD\PROJECTS\61688214\DETAILB\D24.DWG

**Xref-naam** : GEEN

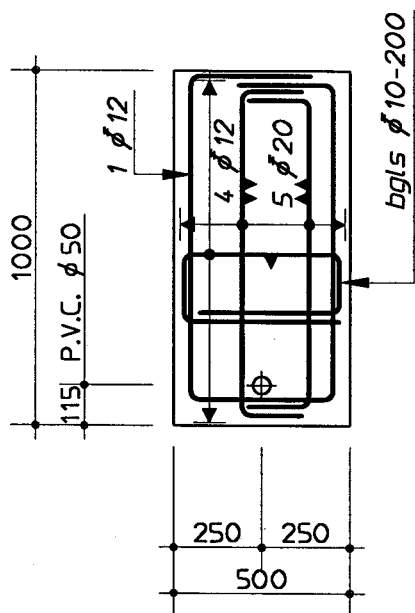


## Bovenaanzicht

dekking 30 mm rondom  
4x uitv.

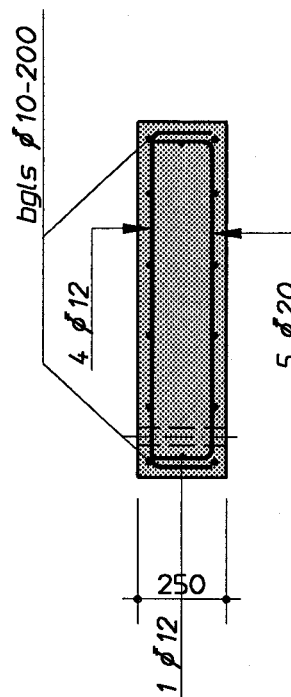

## Langsdoorsnede

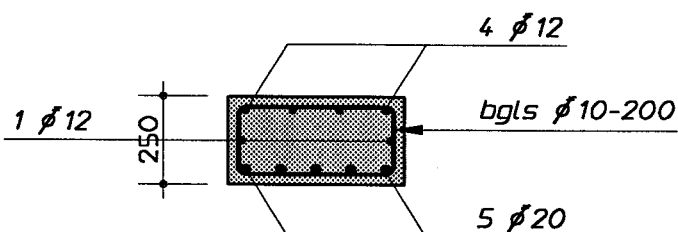

## Dwarsdoorsnede

# VERVALLEN

**ARCADIS** BOUW/INFRA



**Project** : Tilburg o.d.g. Campenhoef - Witbrant

**Tek.nr.**

**Onderdeel** : Stootplaten t.b.v. buizen

**D25**

**Schaal** : 1:20

**Bestandsnaam** : T:\ACAD\PROJECTS\61688214\DETAILB\D25.DWG

**Xref-naam** : GEEN