




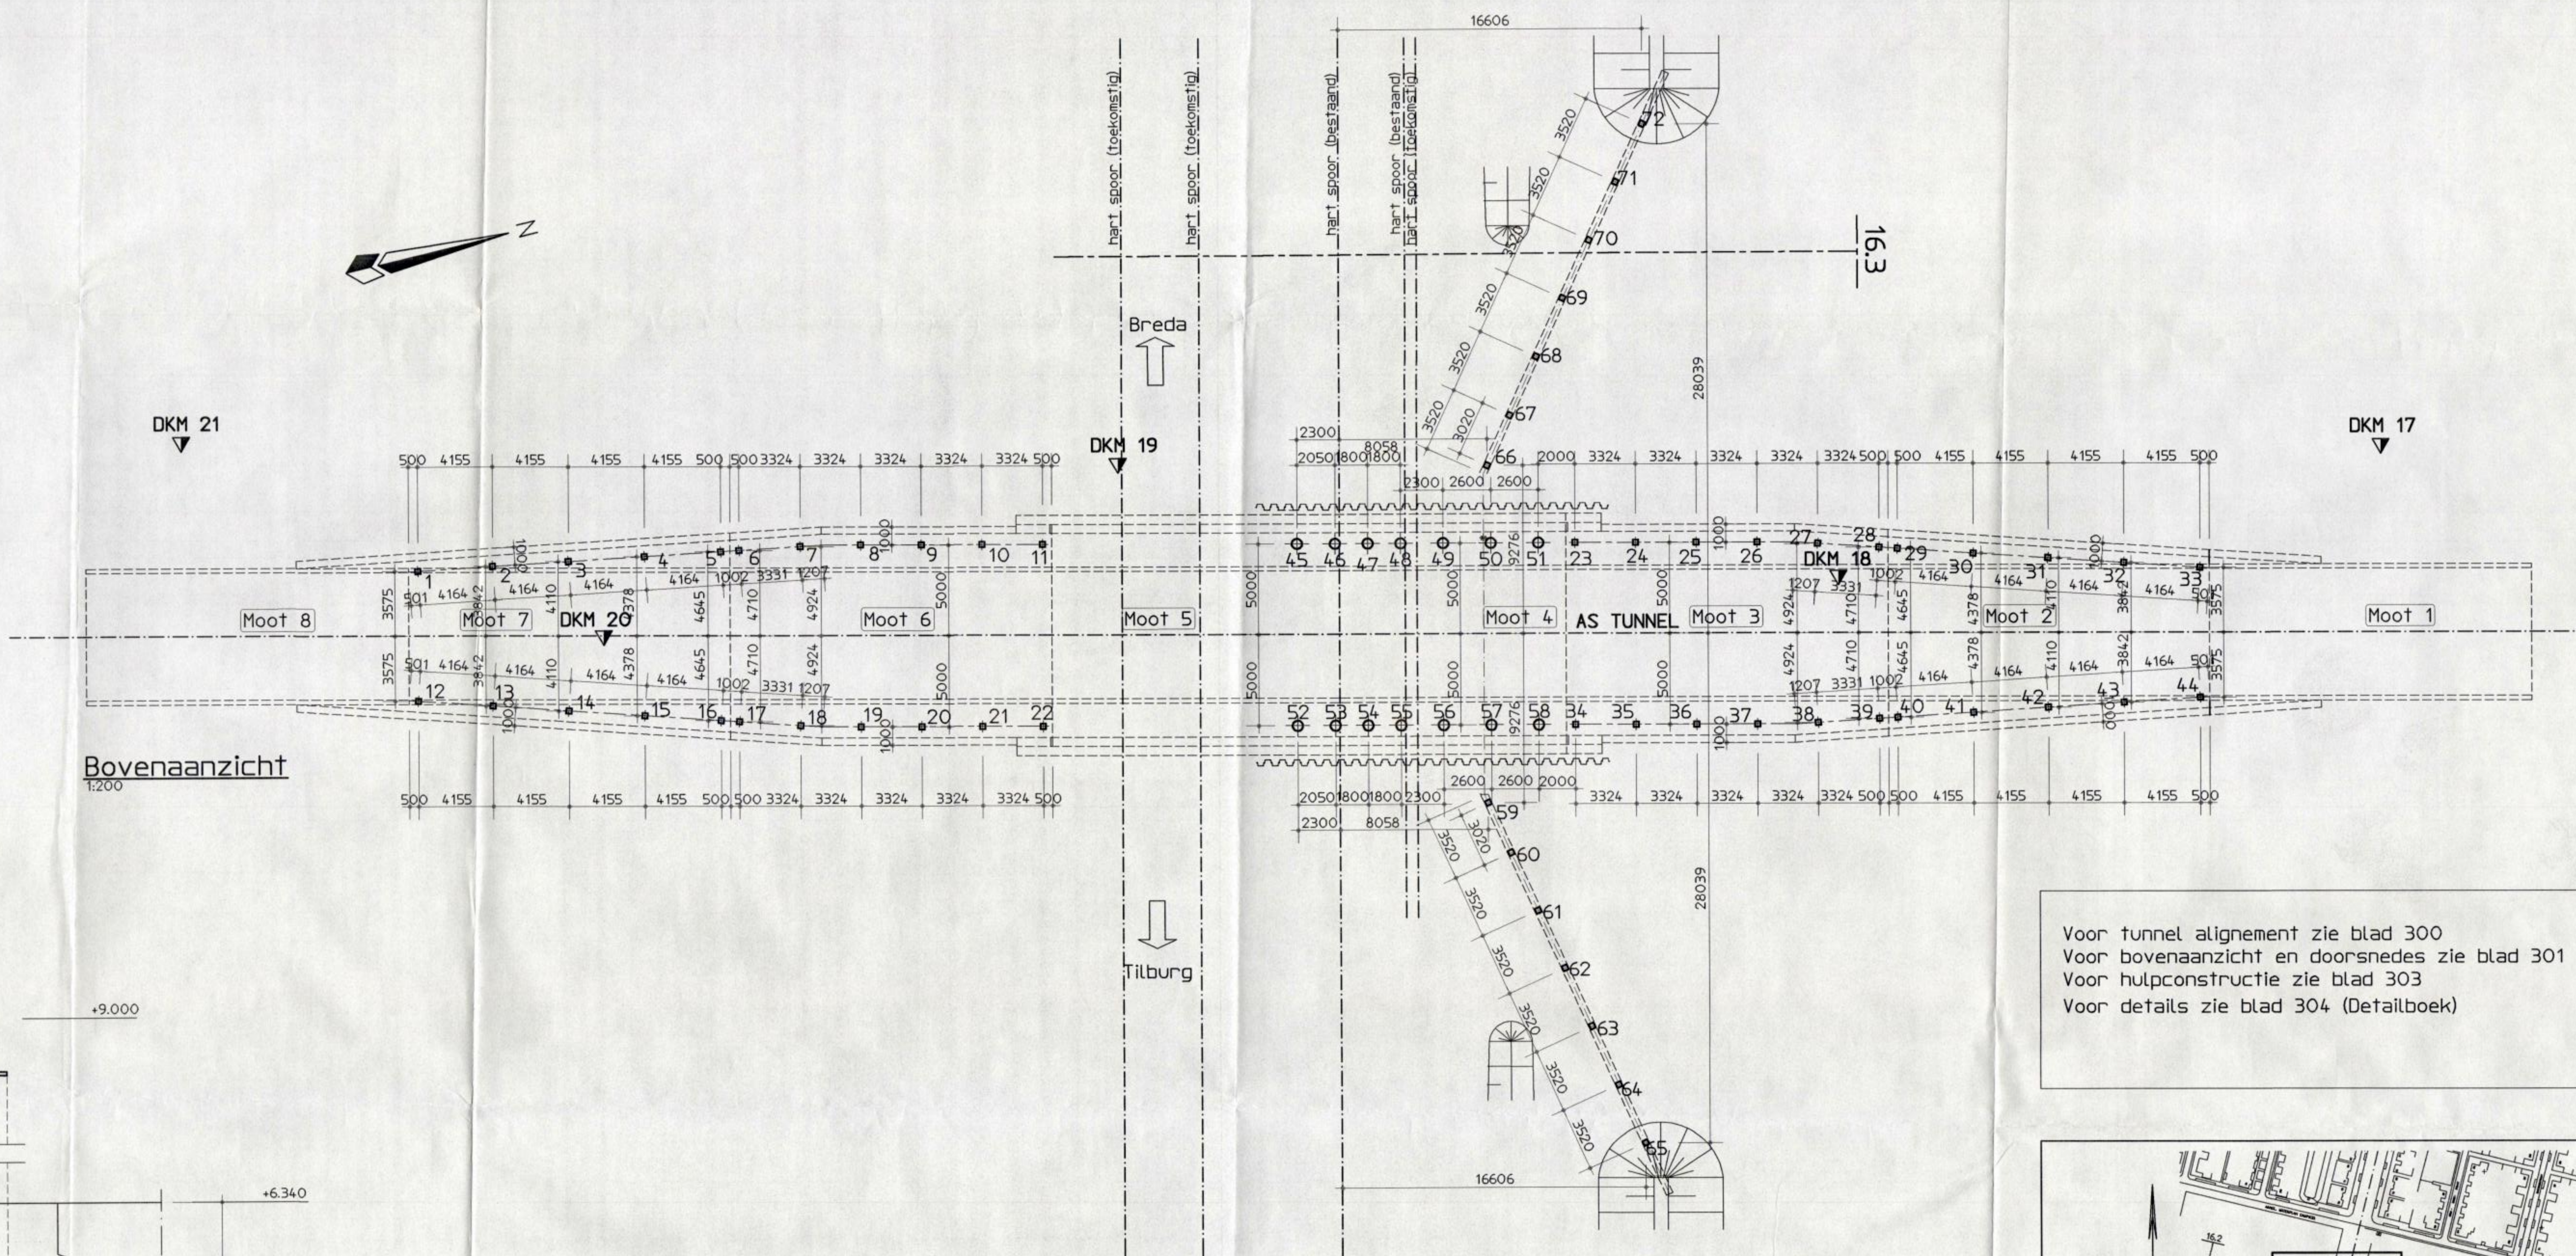

Bovenaanzicht
1:200

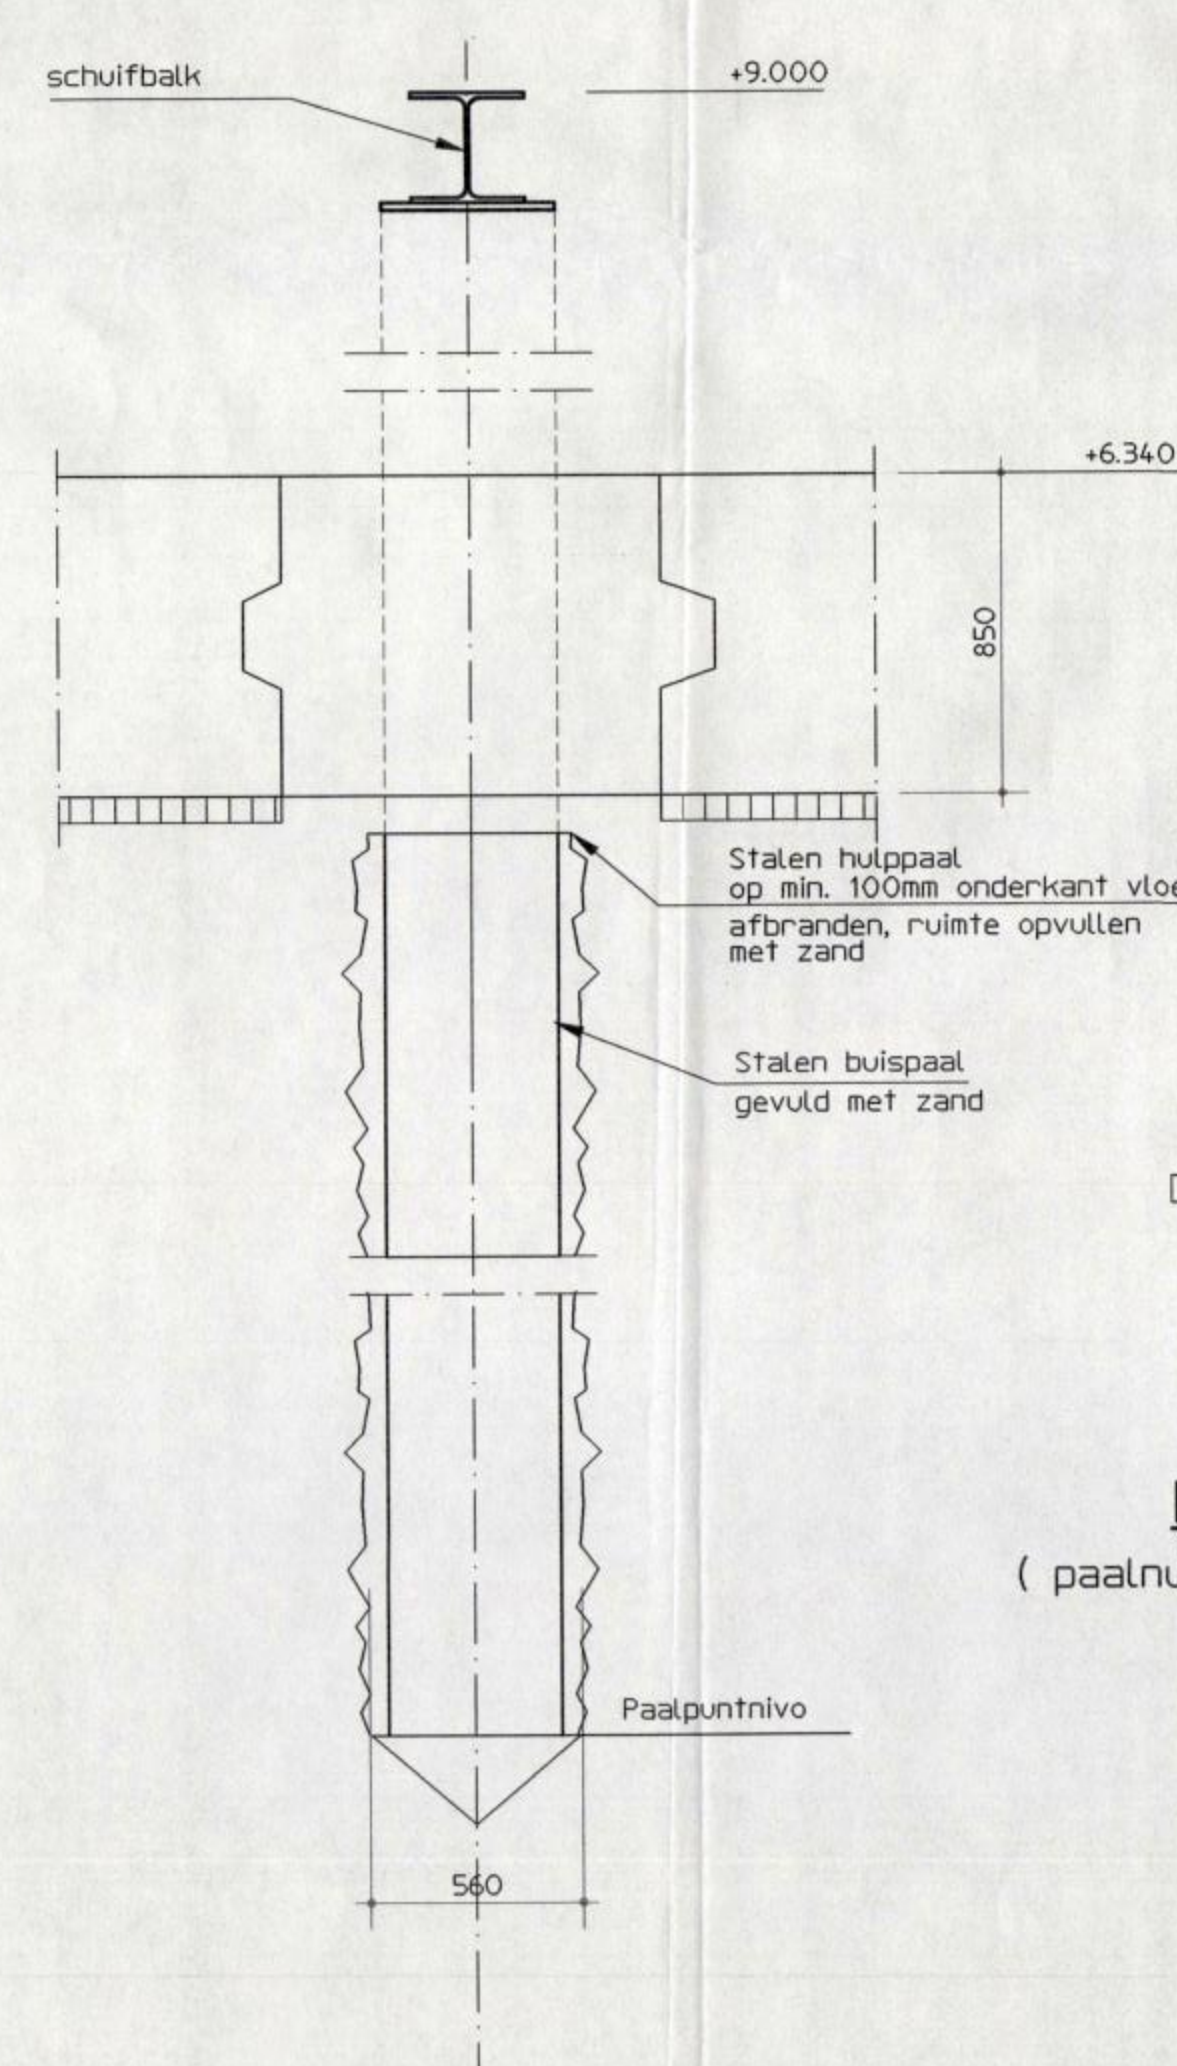

Detail Tubexpaal
1:20
In definitieve situatie

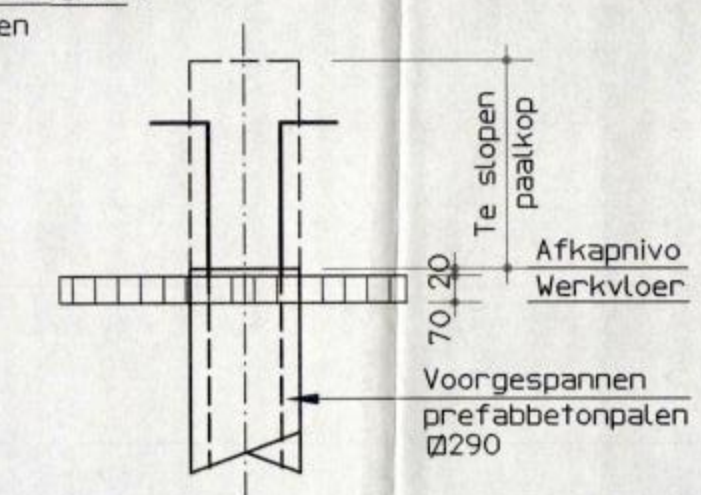

Detail paalkop
1:20
(paalnummer 1 t/m 44 en 59 t/m 72)


TUBEX met grouting
Buisdiameter ϕ 457 / Punt diameter ϕ 560

SYMBOL	PAALNUMMER	AFBRANDNIVO	PAALPUNTNIVO	PAALLENTE	AANT.	SCHOORSTAND	KOPWAPENING	OPMERKINGEN
	45, 46, 47, 48, 49, 50, 51, 52, 53, 54, 55, 56, 57, 58	o.k. schuifbaan	-8.500	17500	14	GEEN		

VOORGESPANNEN PREFABBTETONPALEN ϕ 290

SYMBOL	PAALNUMMER	AFKAPNIVO	PAALPUNTNIVO	PAALLENTE	AANT.	SCHOORSTAND	KOPWAPENING	OPMERKINGEN
	1, 12, 33, 44	+7.232	+0.500	7500	4	geen	4 ϕ 20 lmg. 2000 4 ϕ 20 lmg. 3000	
	2, 13, 32, 43	+7.051	+0.500	7000	4	"	"	
	3, 14, 31, 42	+6.870	+0.500	7000	4	"	"	
	4, 15, 30, 41	+6.690	+0.500	7000	4	"	"	
	5, 16, 29, 40	+6.509	+0.500	6500	4	"	"	
	6, 17, 28, 39	+6.466	+0.500	6500	4	"	"	
	7, 18, 27, 38	+6.321	+0.500	6500	4	"	"	
	8, 19, 26, 37	+6.177	+0.500	6500	4	"	"	
	9, 20, 25, 36	+6.038	+0.500	6000	4	"	"	
	10, 21, 24, 35	+5.947	+0.500	6000	4	"	"	
	11, 22, 23, 34	+5.911	+0.500	6000	4	"	"	
	59 t/m 72	+9.670	+5.670	4500	14	"	"	

Voor tunnel alignment zie blad 300
Voor bovenaanzicht en doorsneden zie blad 301
Voor hulpconstructie zie blad 303
Voor details zie blad 304 (Detailboek)

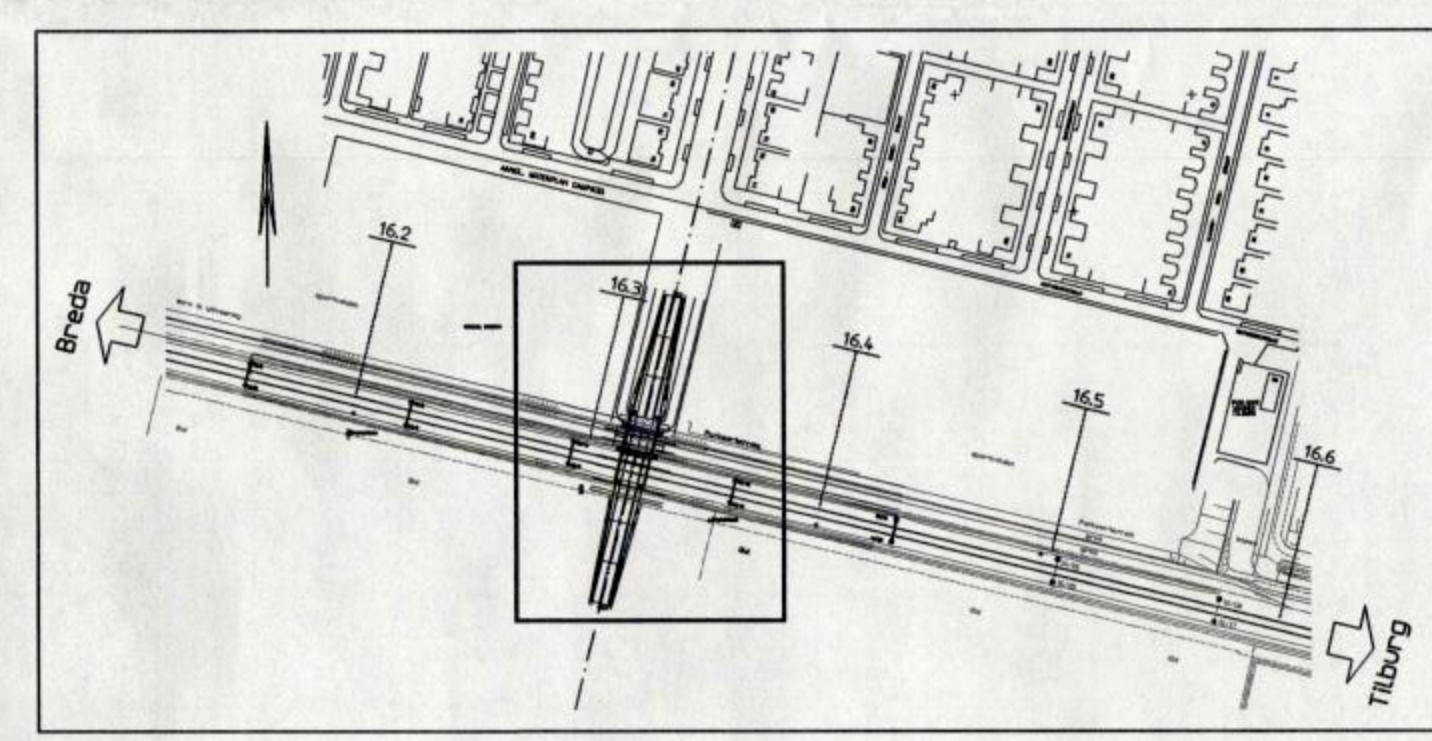

Opmerkingen
- alle maten in mm
- hoogtematen in m t.o.v. N.A.P.
- coördinaten t.o.v. Parijs stelsel

REVISIE TOEGEPAST

datum: 28-02-01
paraaf:

ARCADIS BOUW/INFRA

Berkenweg 7
Postbus 220, 3800 AE Amersfoort
Telefoon 033 460 44 00
Telefax 033 460 44 06

Project
Tilburg
o.d.g. Campenhoef-Witbrant

Onderdeel
Bestek
Palenplan

Codering derden:

Status:

18-01-01 v.oostende
07-12-98 Belay A. revisie

Uitg. Datum Getekend Opmerkingen

Goedgekeurd: F.J. Hovinga

Vrijgegeven: J.W.M. Hagen

Schaal: 1:200

Formaat: A1

Tekeningnummer:

Tb 42/3/1

302