



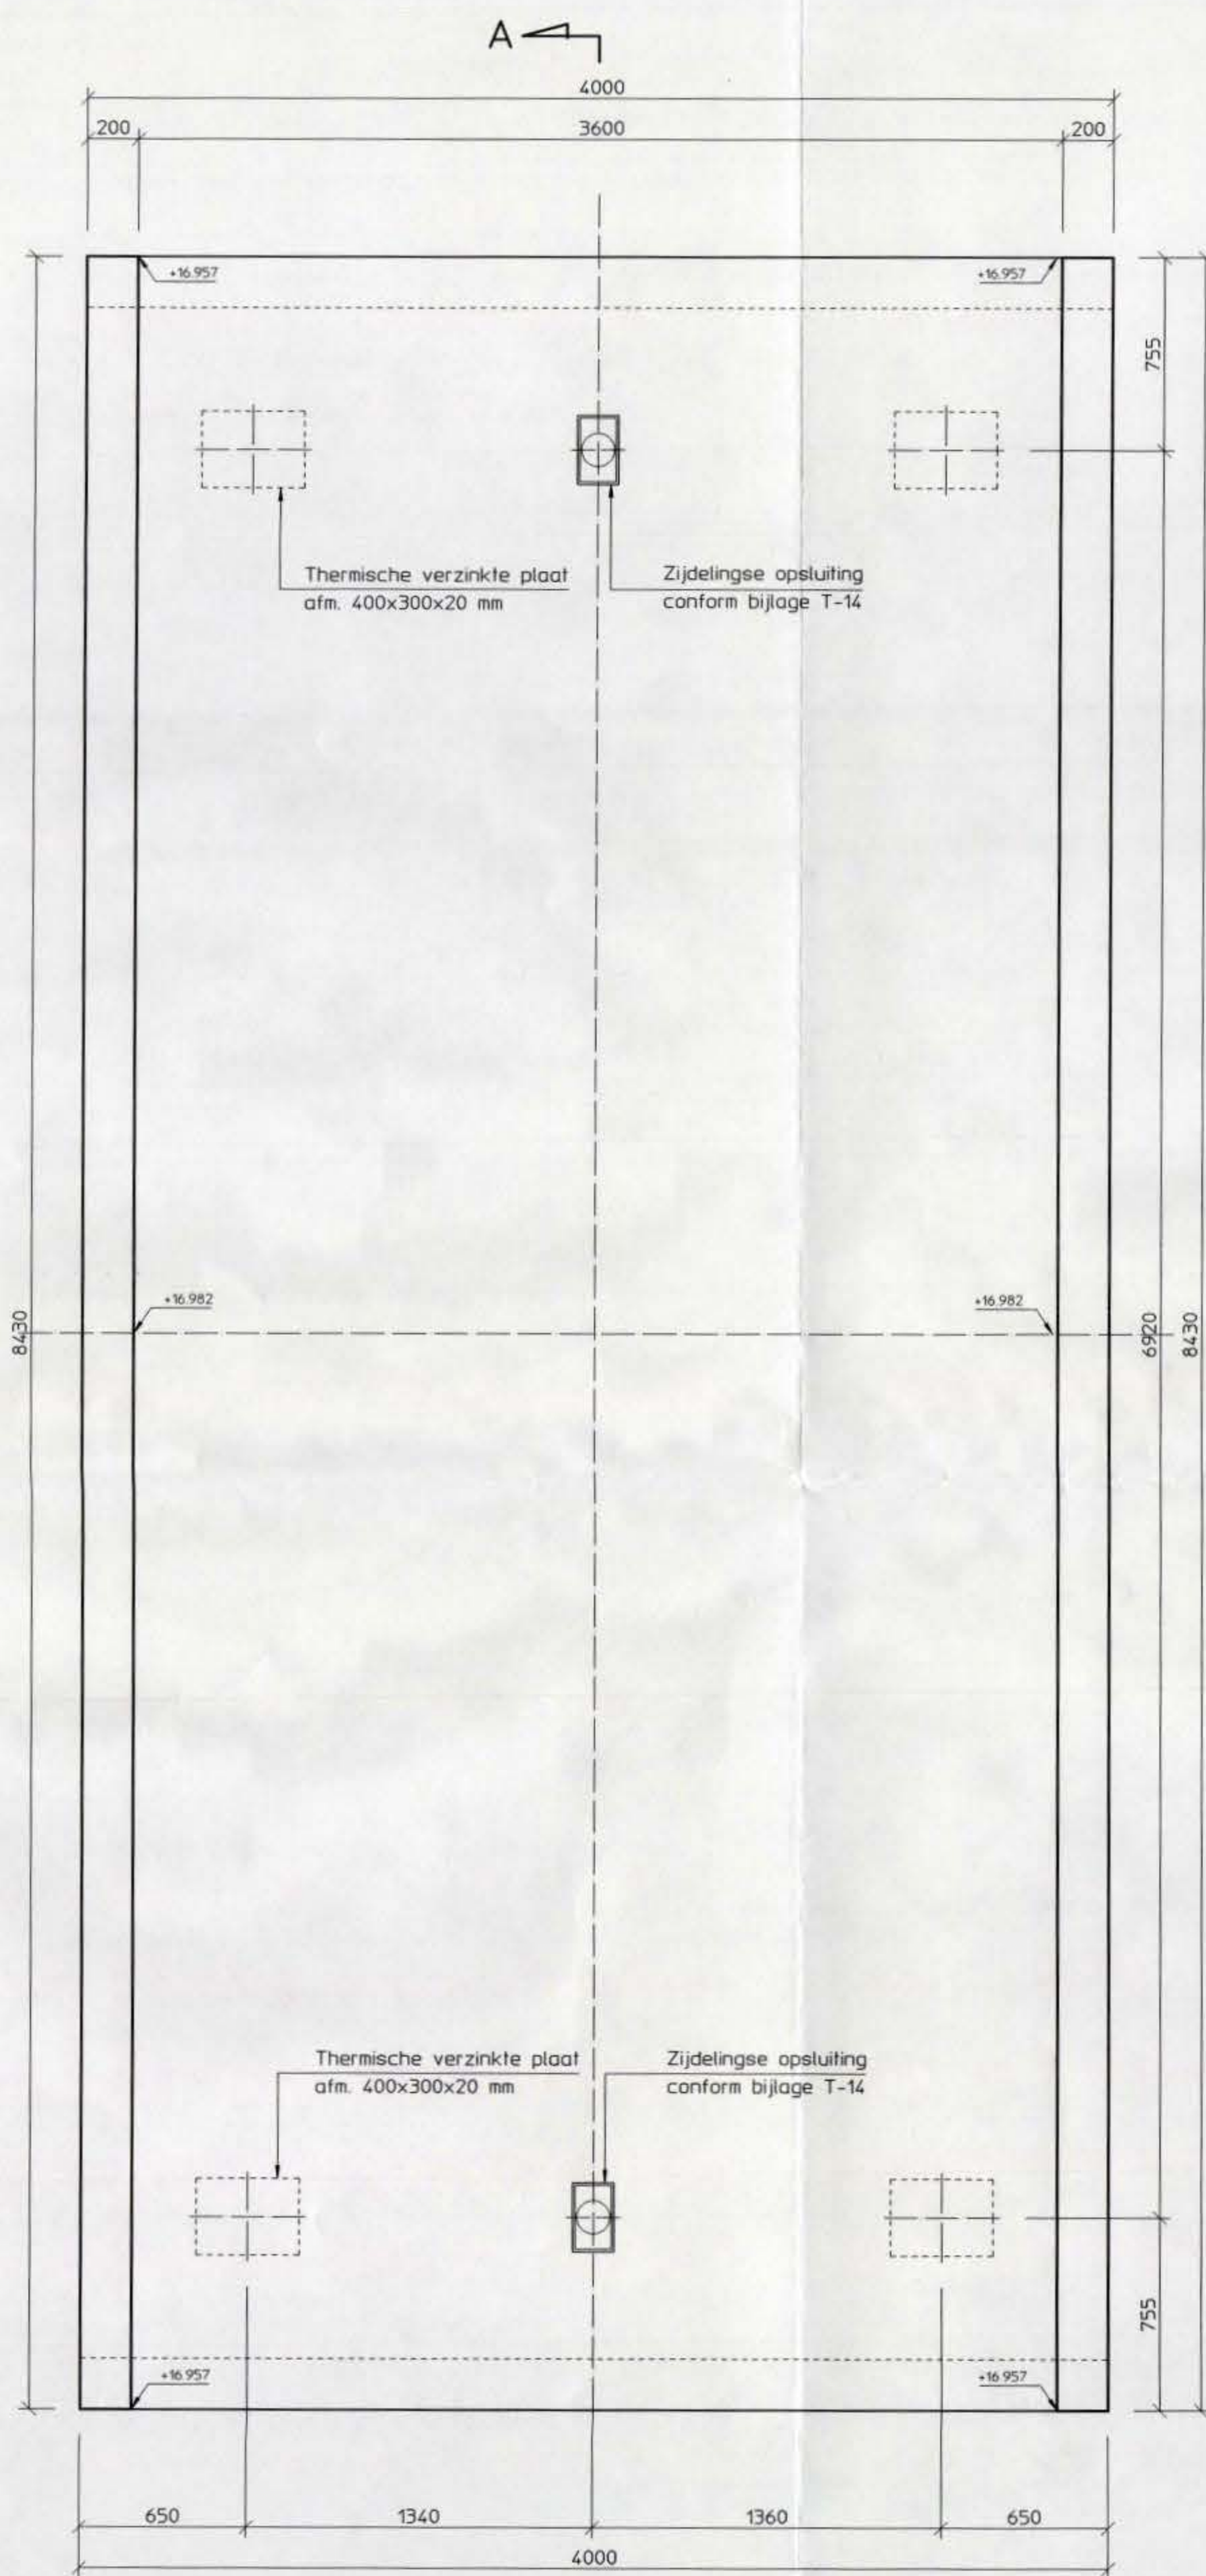


Bovenaanzicht
Schaal 1:20


Brugdek 2x uitvoeren

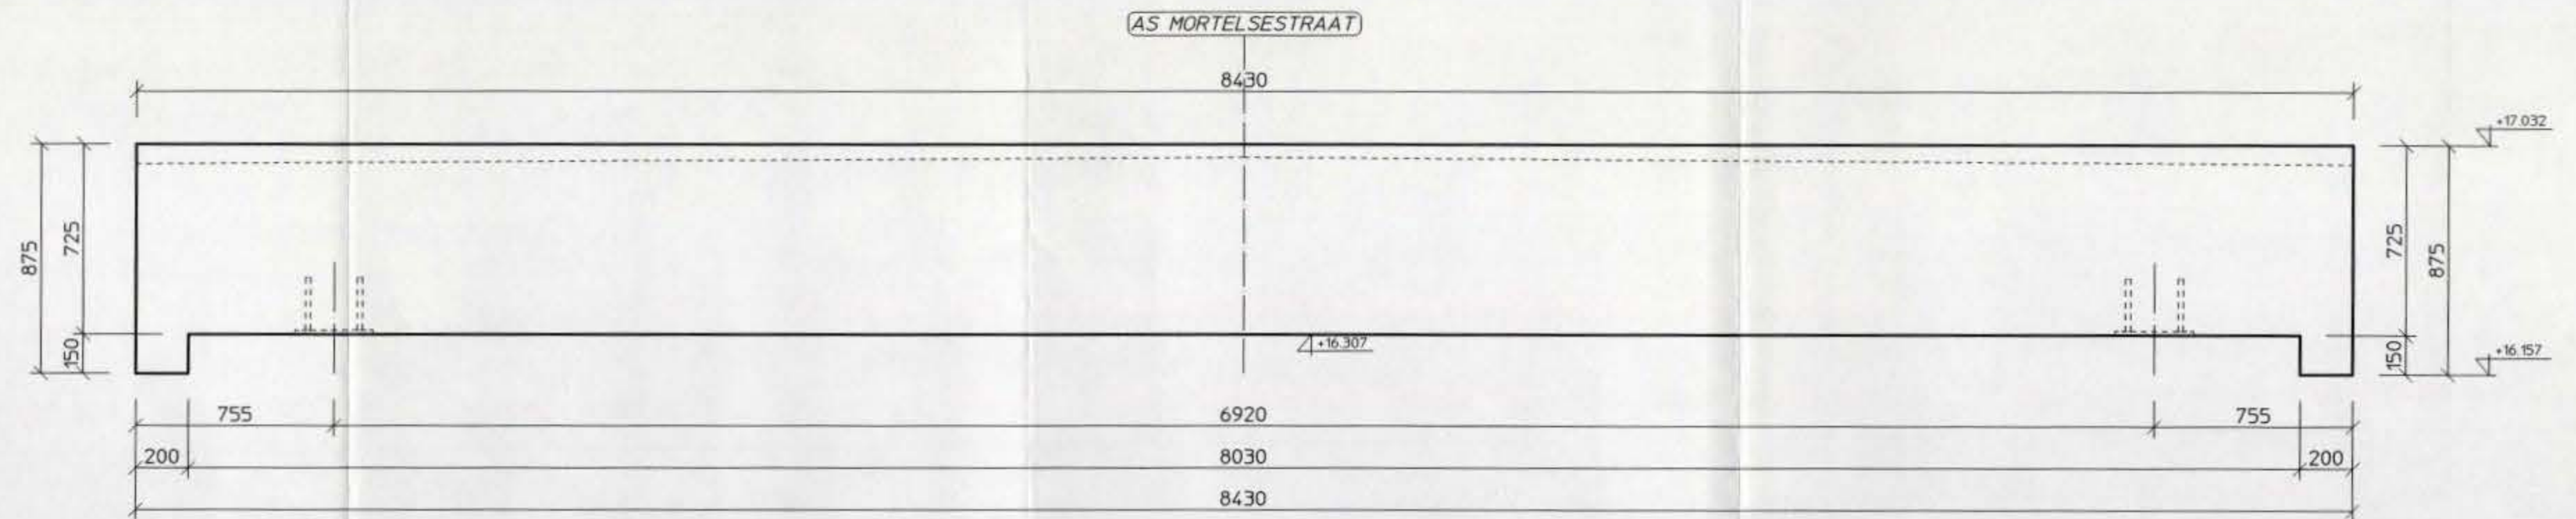


Vooraanzicht
Schaal 1:20

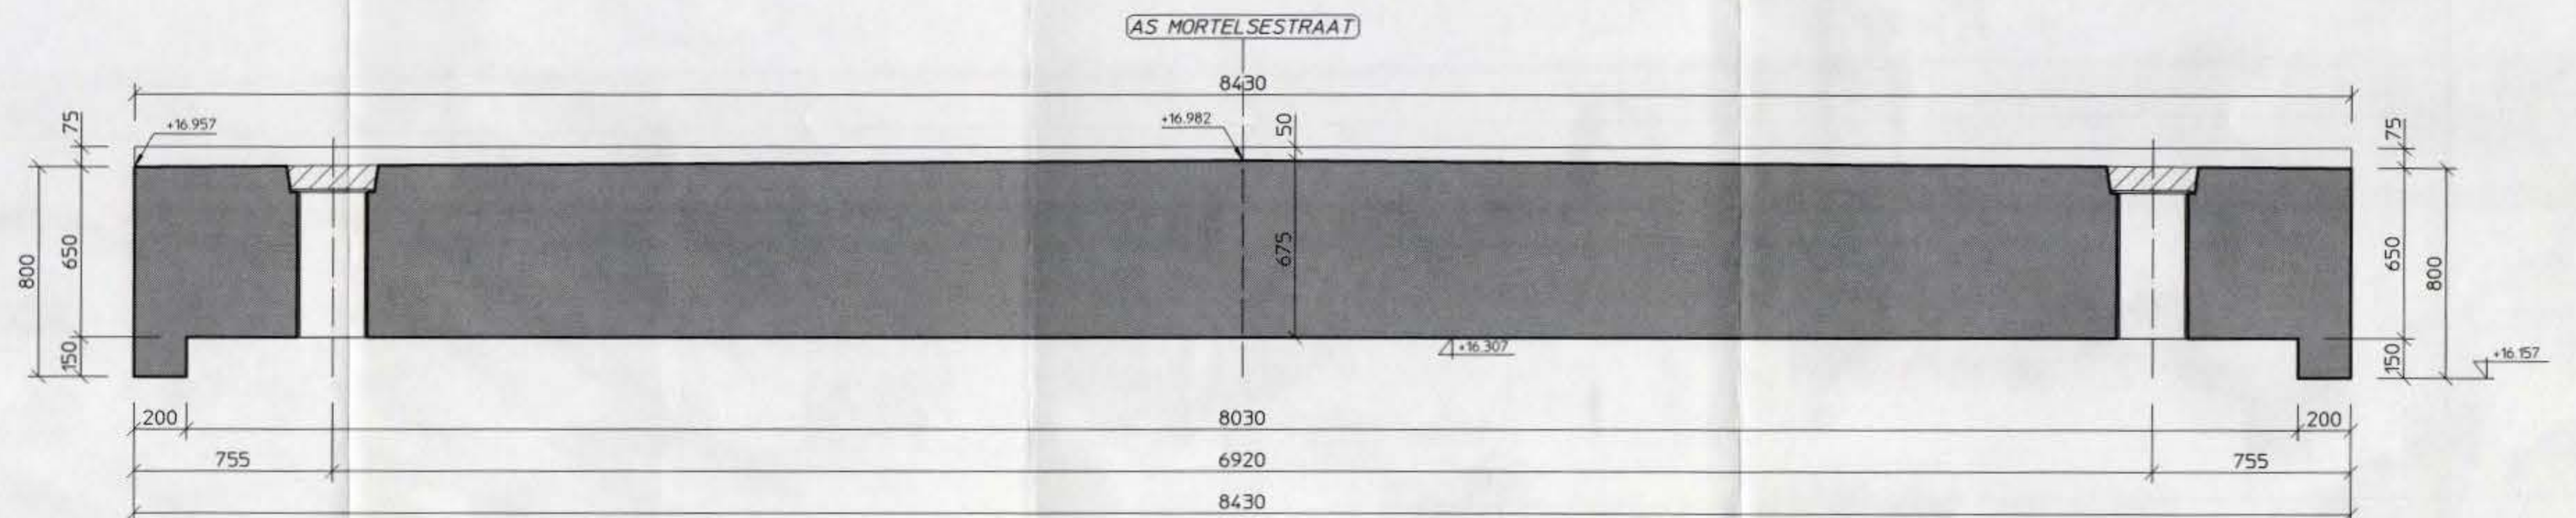

Doorsnede A-A
Schaal 1:20

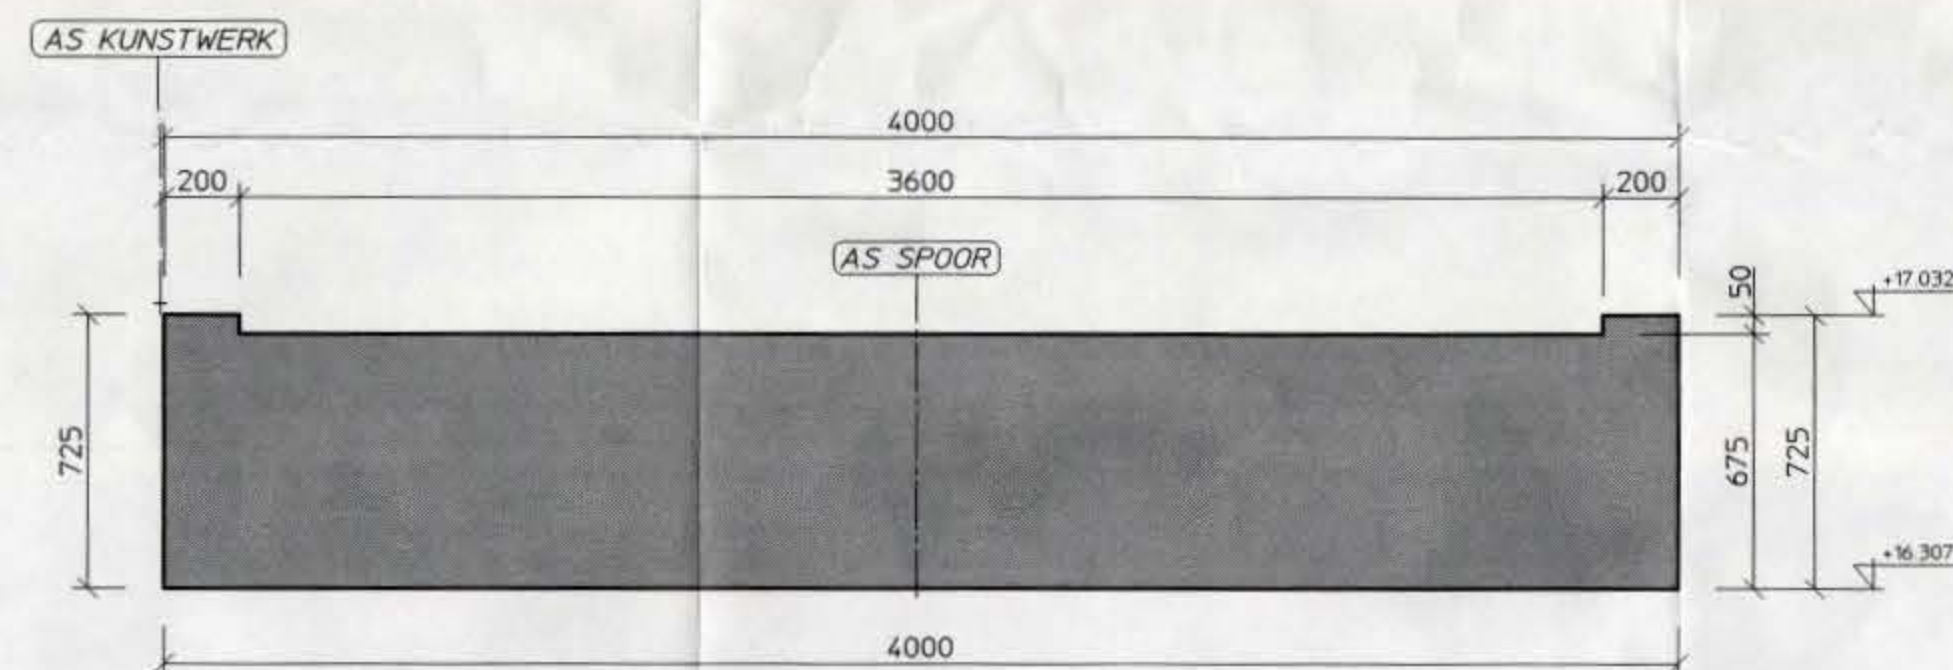


Doorsnede B-B
Schaal 1:20

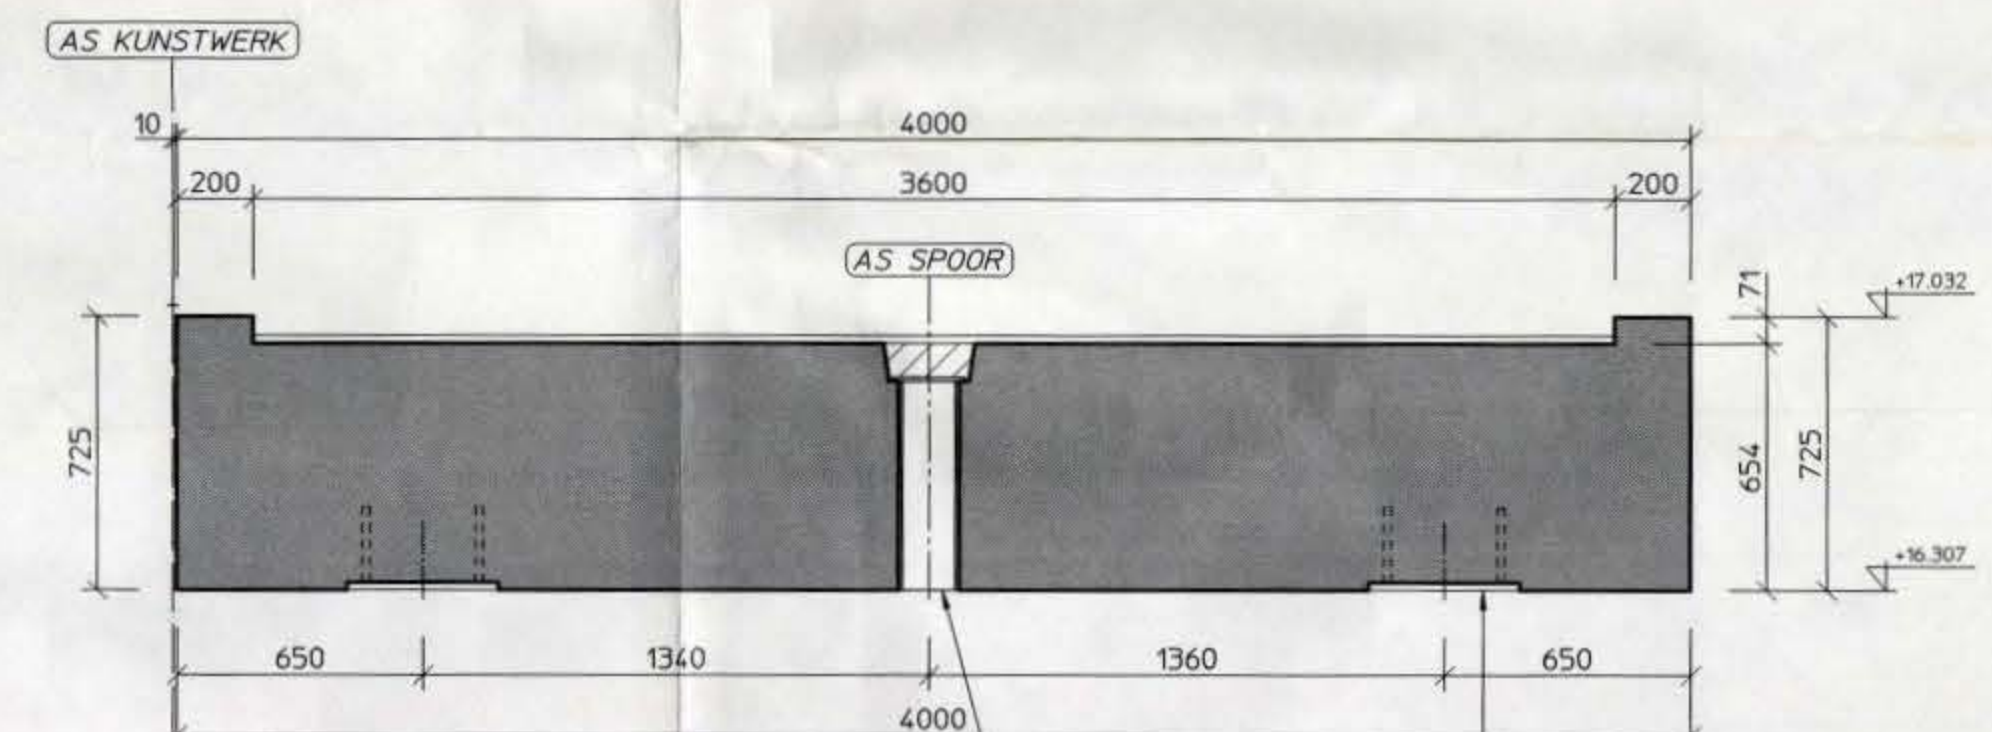

Doorsnede C-C
Schaal 1:20

Zijdelingse opsluiting conform bijlage T-14
Thermische verzinkte plaat afm. 400x300x20 mm zie detail 1

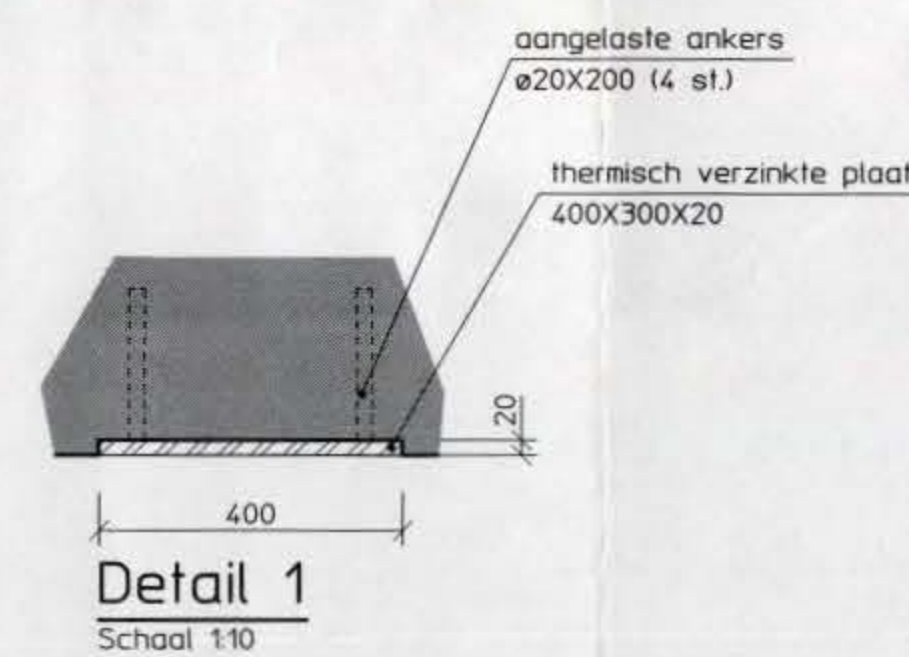

Detail 1
Schaal 1:10

Holland Railconsult

Civiele Techniek
Postbus 2855
3500 GW Utrecht

Revisie uitgevoerd door: B. Timmer
Utrecht d.d. 19-03-2002

Opmerkingen

- Maten in millimeters
- Hoogtematen in meters t.o.v. N.A.P.

(Status: REVISIE d.d. 19-03-2002 08:29:29)

naam	par	datum	Maatvoeringstekening Brugdekken
getekend E.J. Langendoen		05-09-2000	
projectleider W. Vermeulen			
projectnr. 7502026	versie	1.0	
besteknr. V40BK11666			
formaat A1			NS Railinfrabeheer Tilburg Verv. spoorbruggen Mortelsestraat
schaal 1:10, 1:20			
421 125 24.337 591 7502026 M - 12			
Div IF Ald CT Grp A+O-I Postbus 2855 3500 GW Utrecht Telefoon 030 - 265 43 98 Telefax 030 - 265 43 71			
plafina: *			



Holland Railconsult