

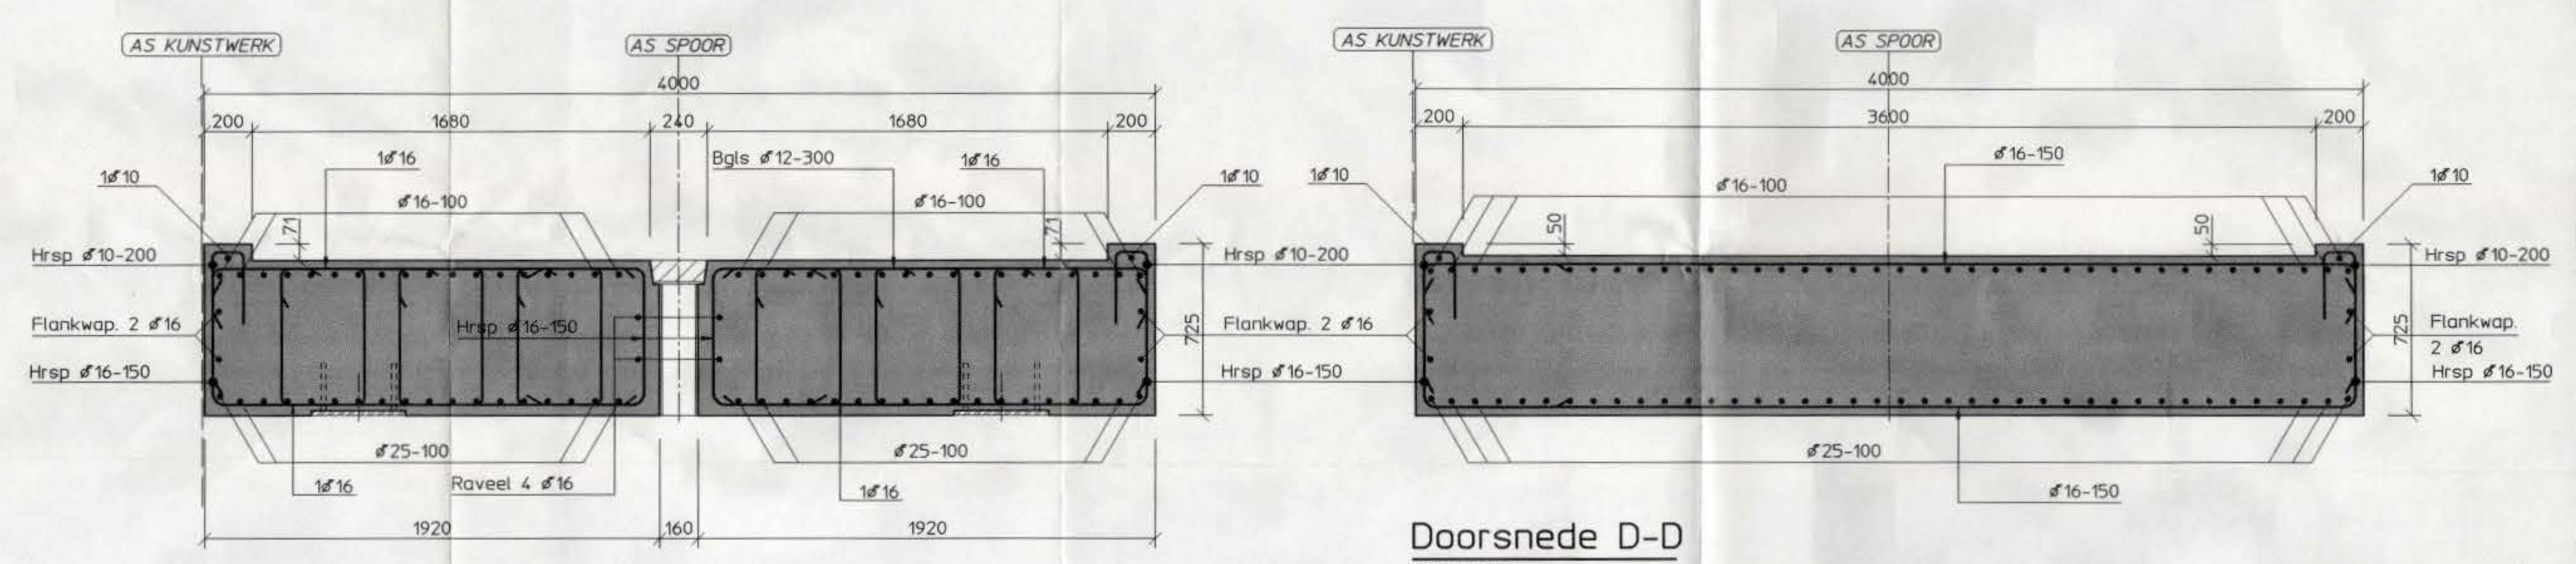
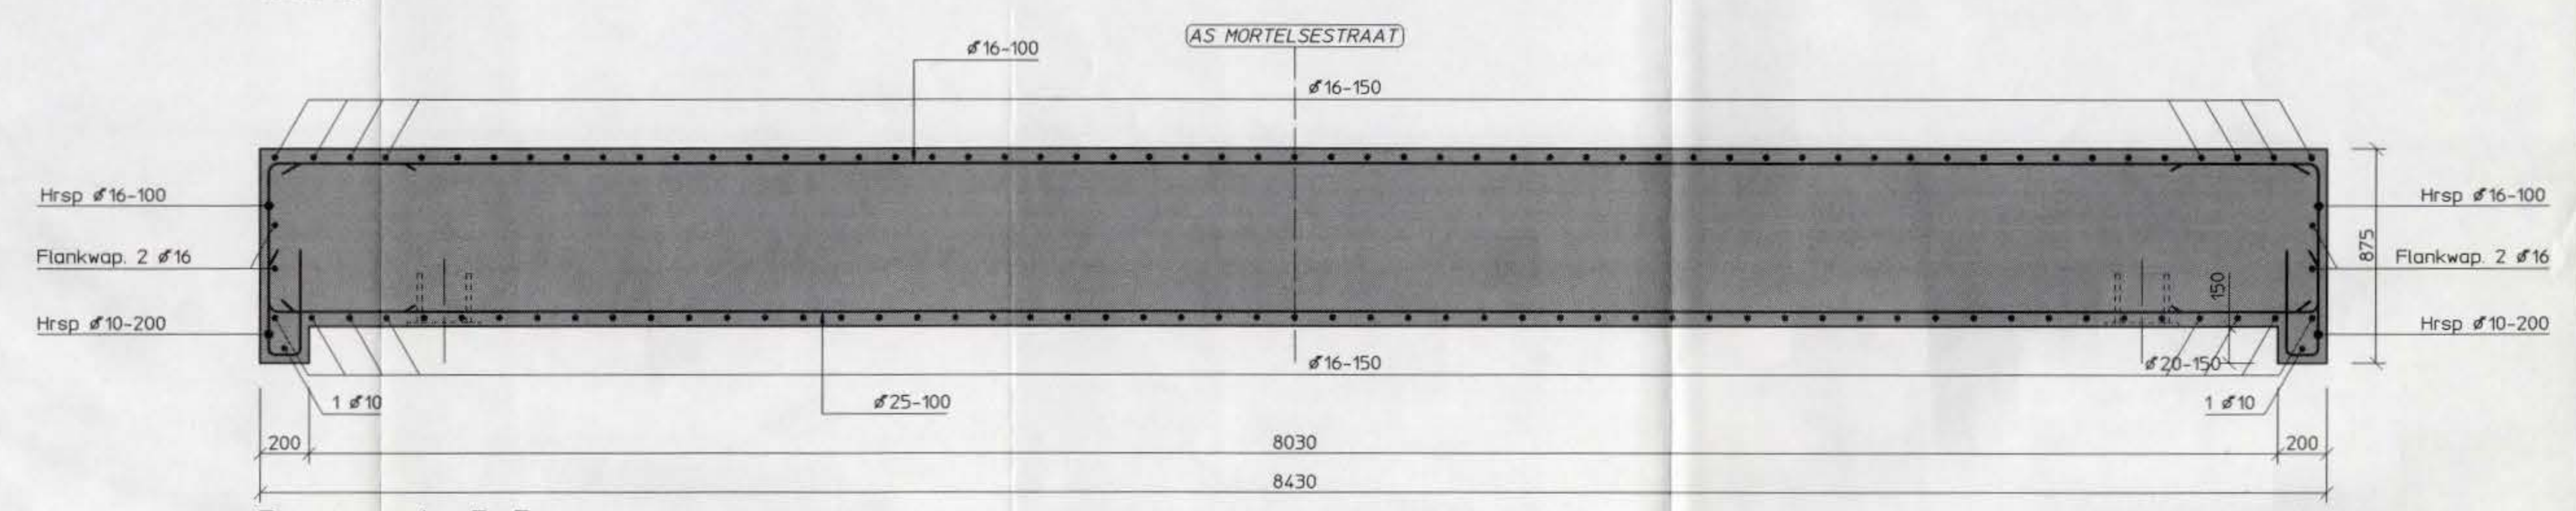
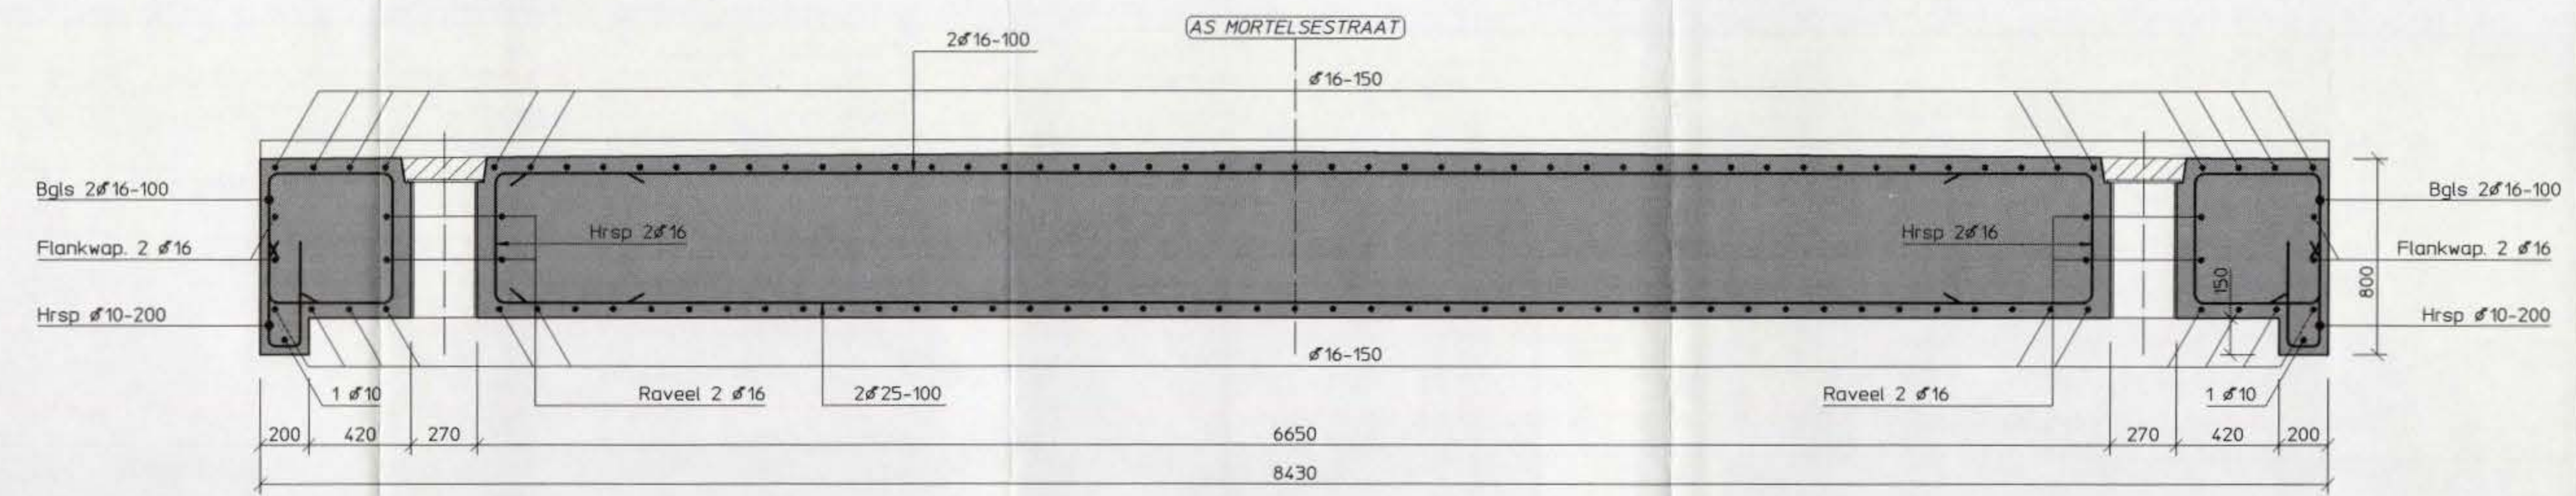


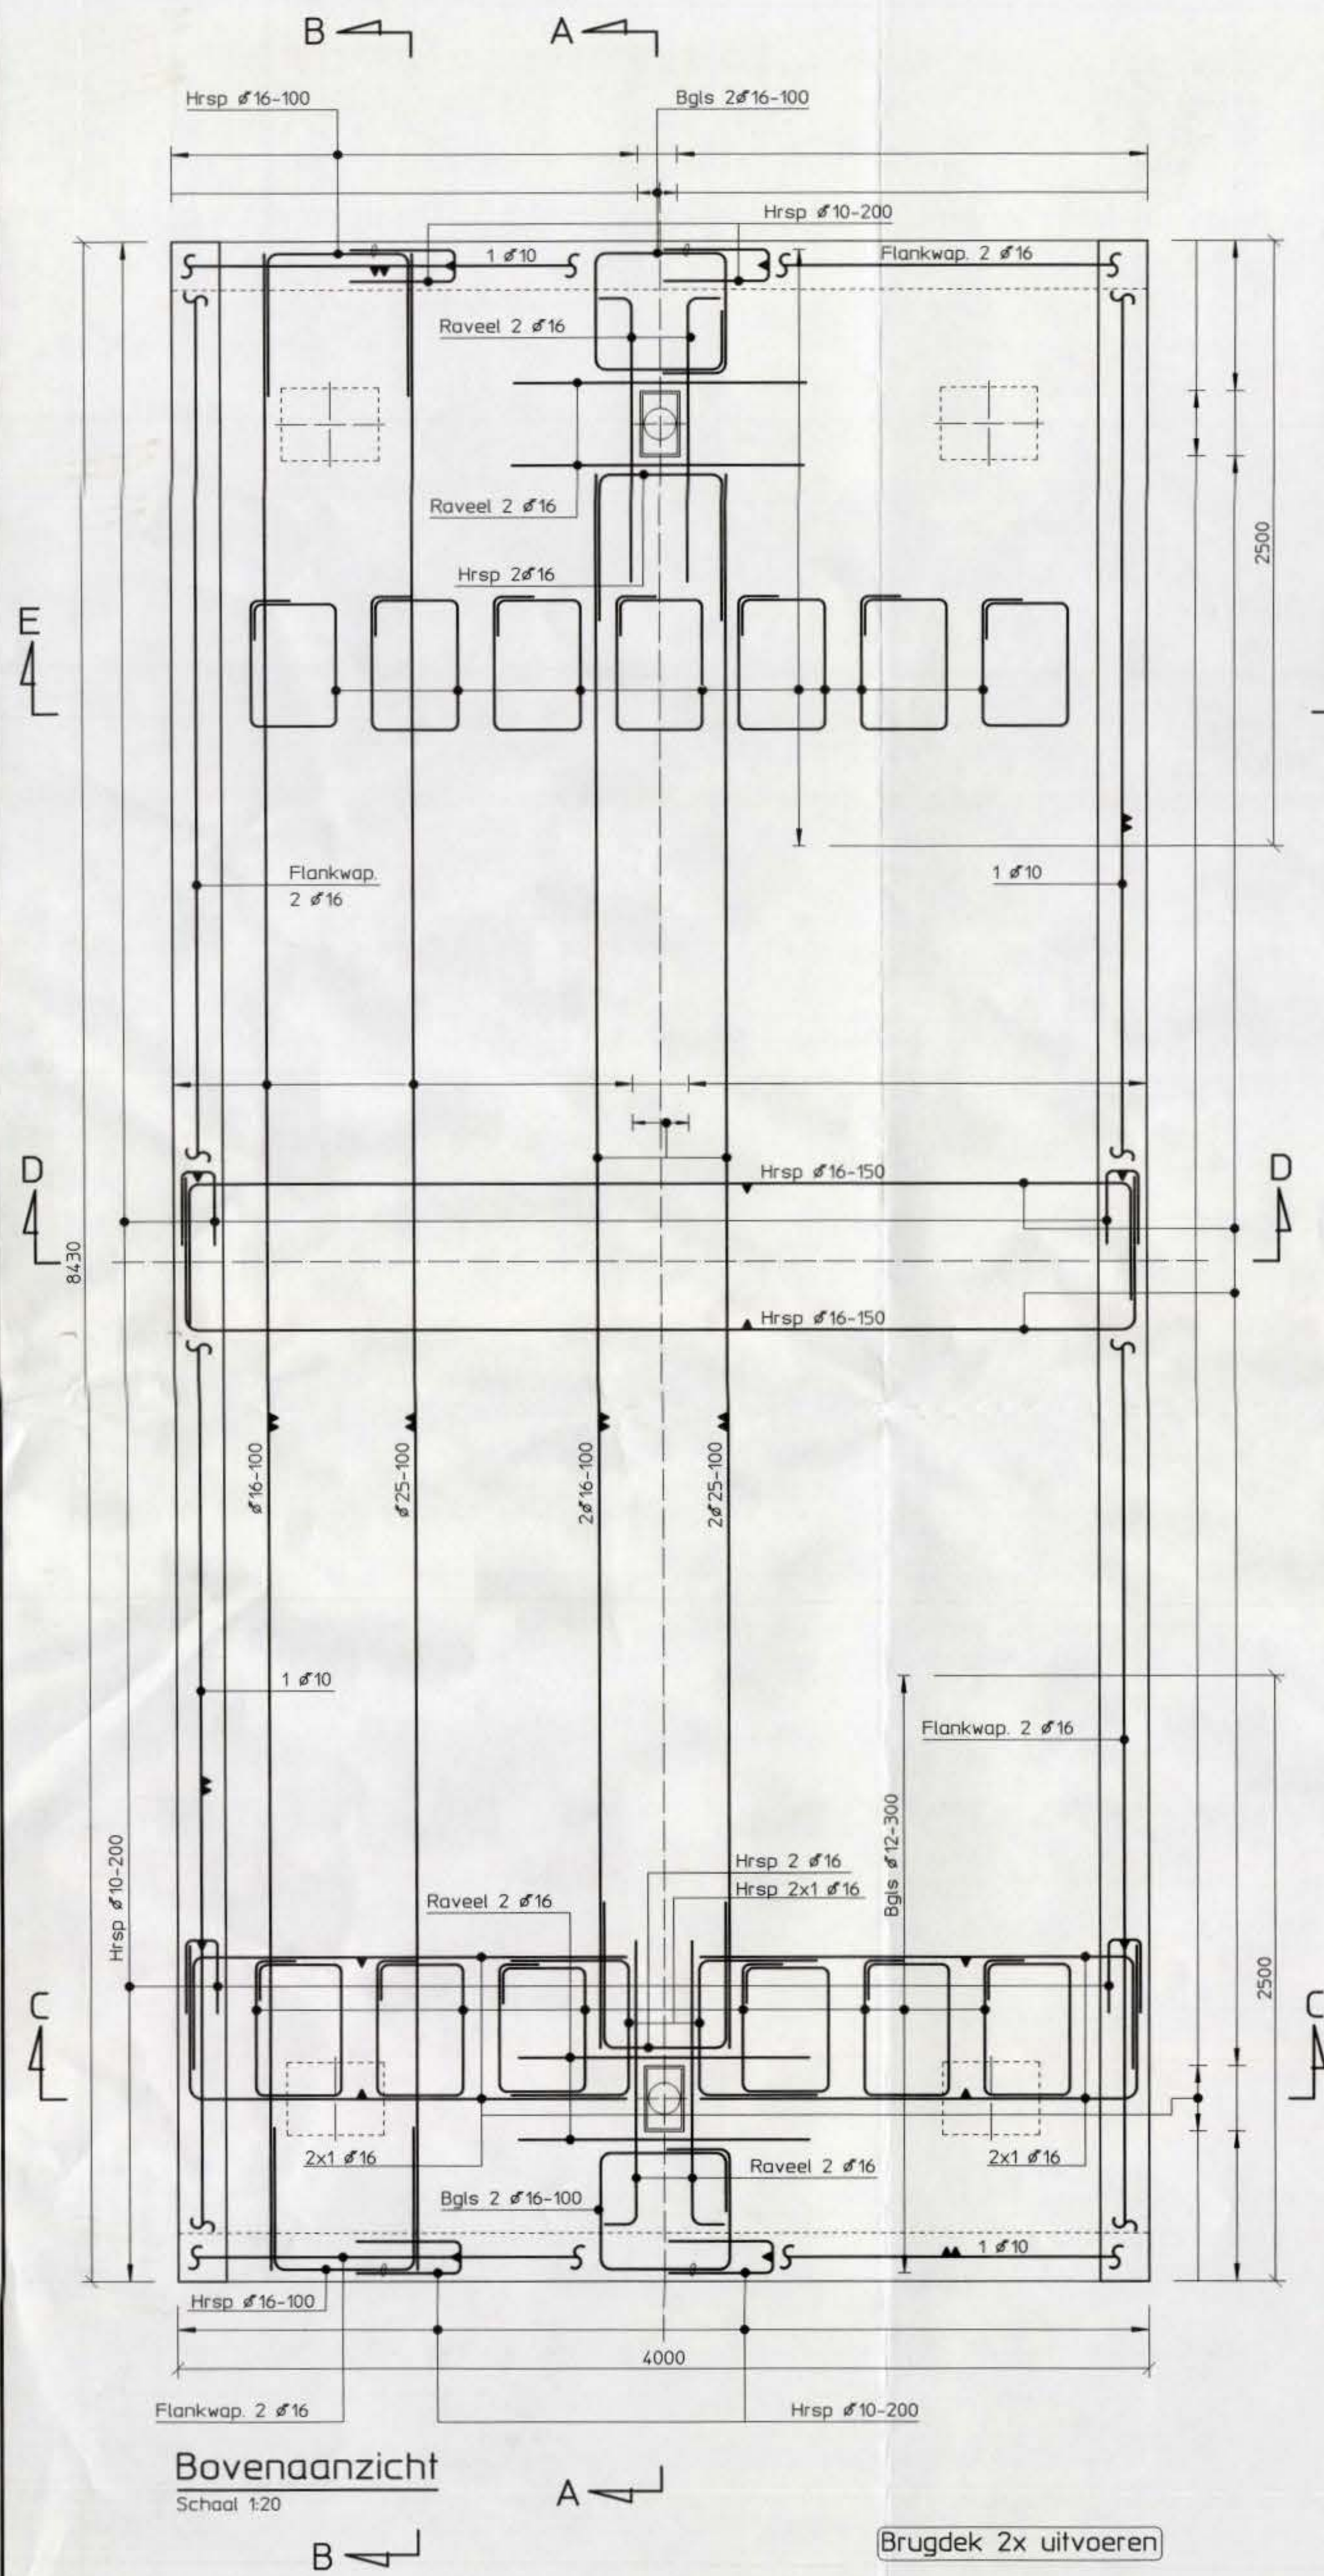

Doorsnede D-D
Schaal 1:20

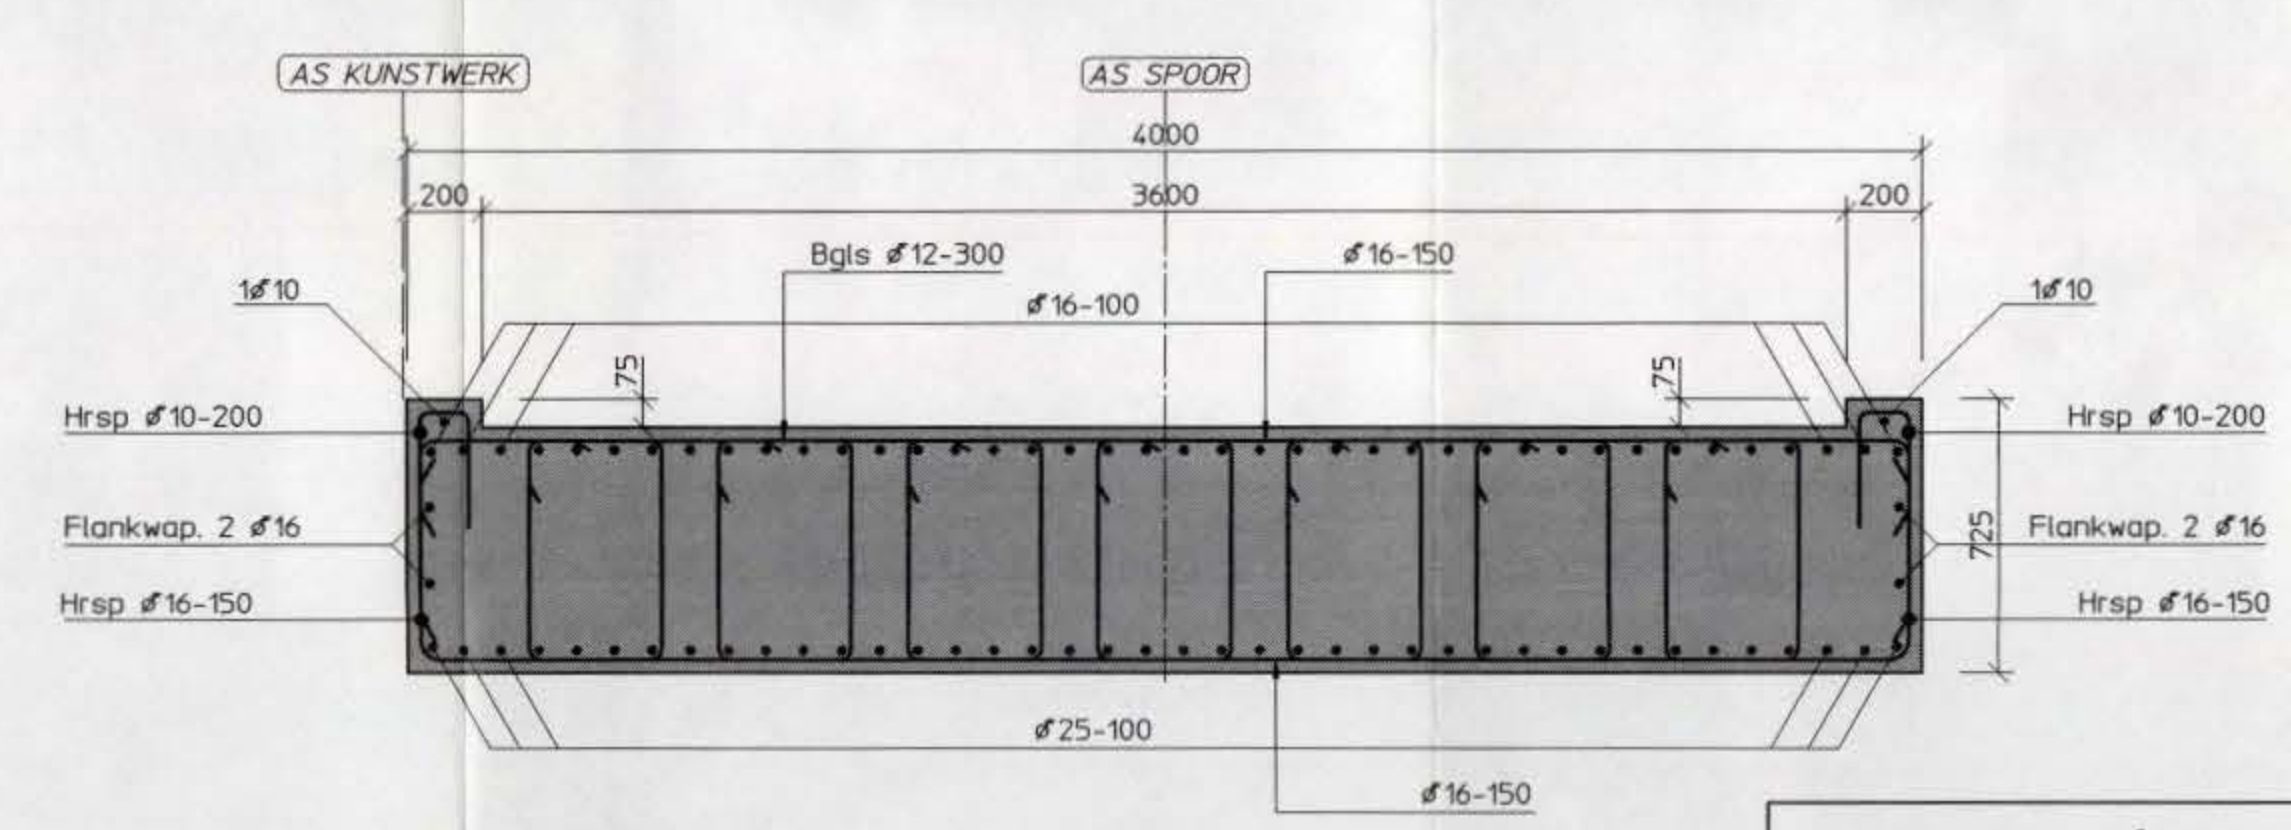

betondekkingstabel			verankeringslengten	
betonstaal	- FeB 500 HWL en/of HK	NEN 6008	ø10	500
beton	- sterkteklasse B 35		ø12	600
	- milieuklasse Sb		ø14	600
	- CEM III		ø16	600
constructie	betondekking in mm		ø20	900
	controleerbaar	oncontroleerbaar	ø25	900
Brugdek	35		ø28	
			ø32	
			ø40	

Opmerkingen
 - Maten in millimeters
 - Hoogtematen in meters t.a.v. N.A.P.

Status: REVISIE d.d. 26-03-2002 08:16:16

naam	par	datum	Wapeningstekening	
geleidend	E.J. Langendoen		Brugdekken	
projectleider	W. Vermeulen			
projectnr	7502026	versie	2.0	
bestelnr.	V40B11666			
formaat	A1			
schaal	1:10, 1:20			
			NS Railinfrabeheer	
			Tilburg	
			Verv. spoorbruggen Mortelsestraat	

421 125 24.337 591 7502026 W - 12

Div. F. Afd. CT Grp A+D-1
 Postbus 2855
 3500 GW Utrecht
 Telefoon 030 - 265 43 98
 Telefax 030 - 265 43 71
 plinto: *

Holland Railconsult

Holland Railconsult
 Civiele Techniek
 Postbus 2855
 3500 GW Utrecht

Revisie uitgevoerd door: B. Timmer
 Utrecht d.d. 28-03-2002

