




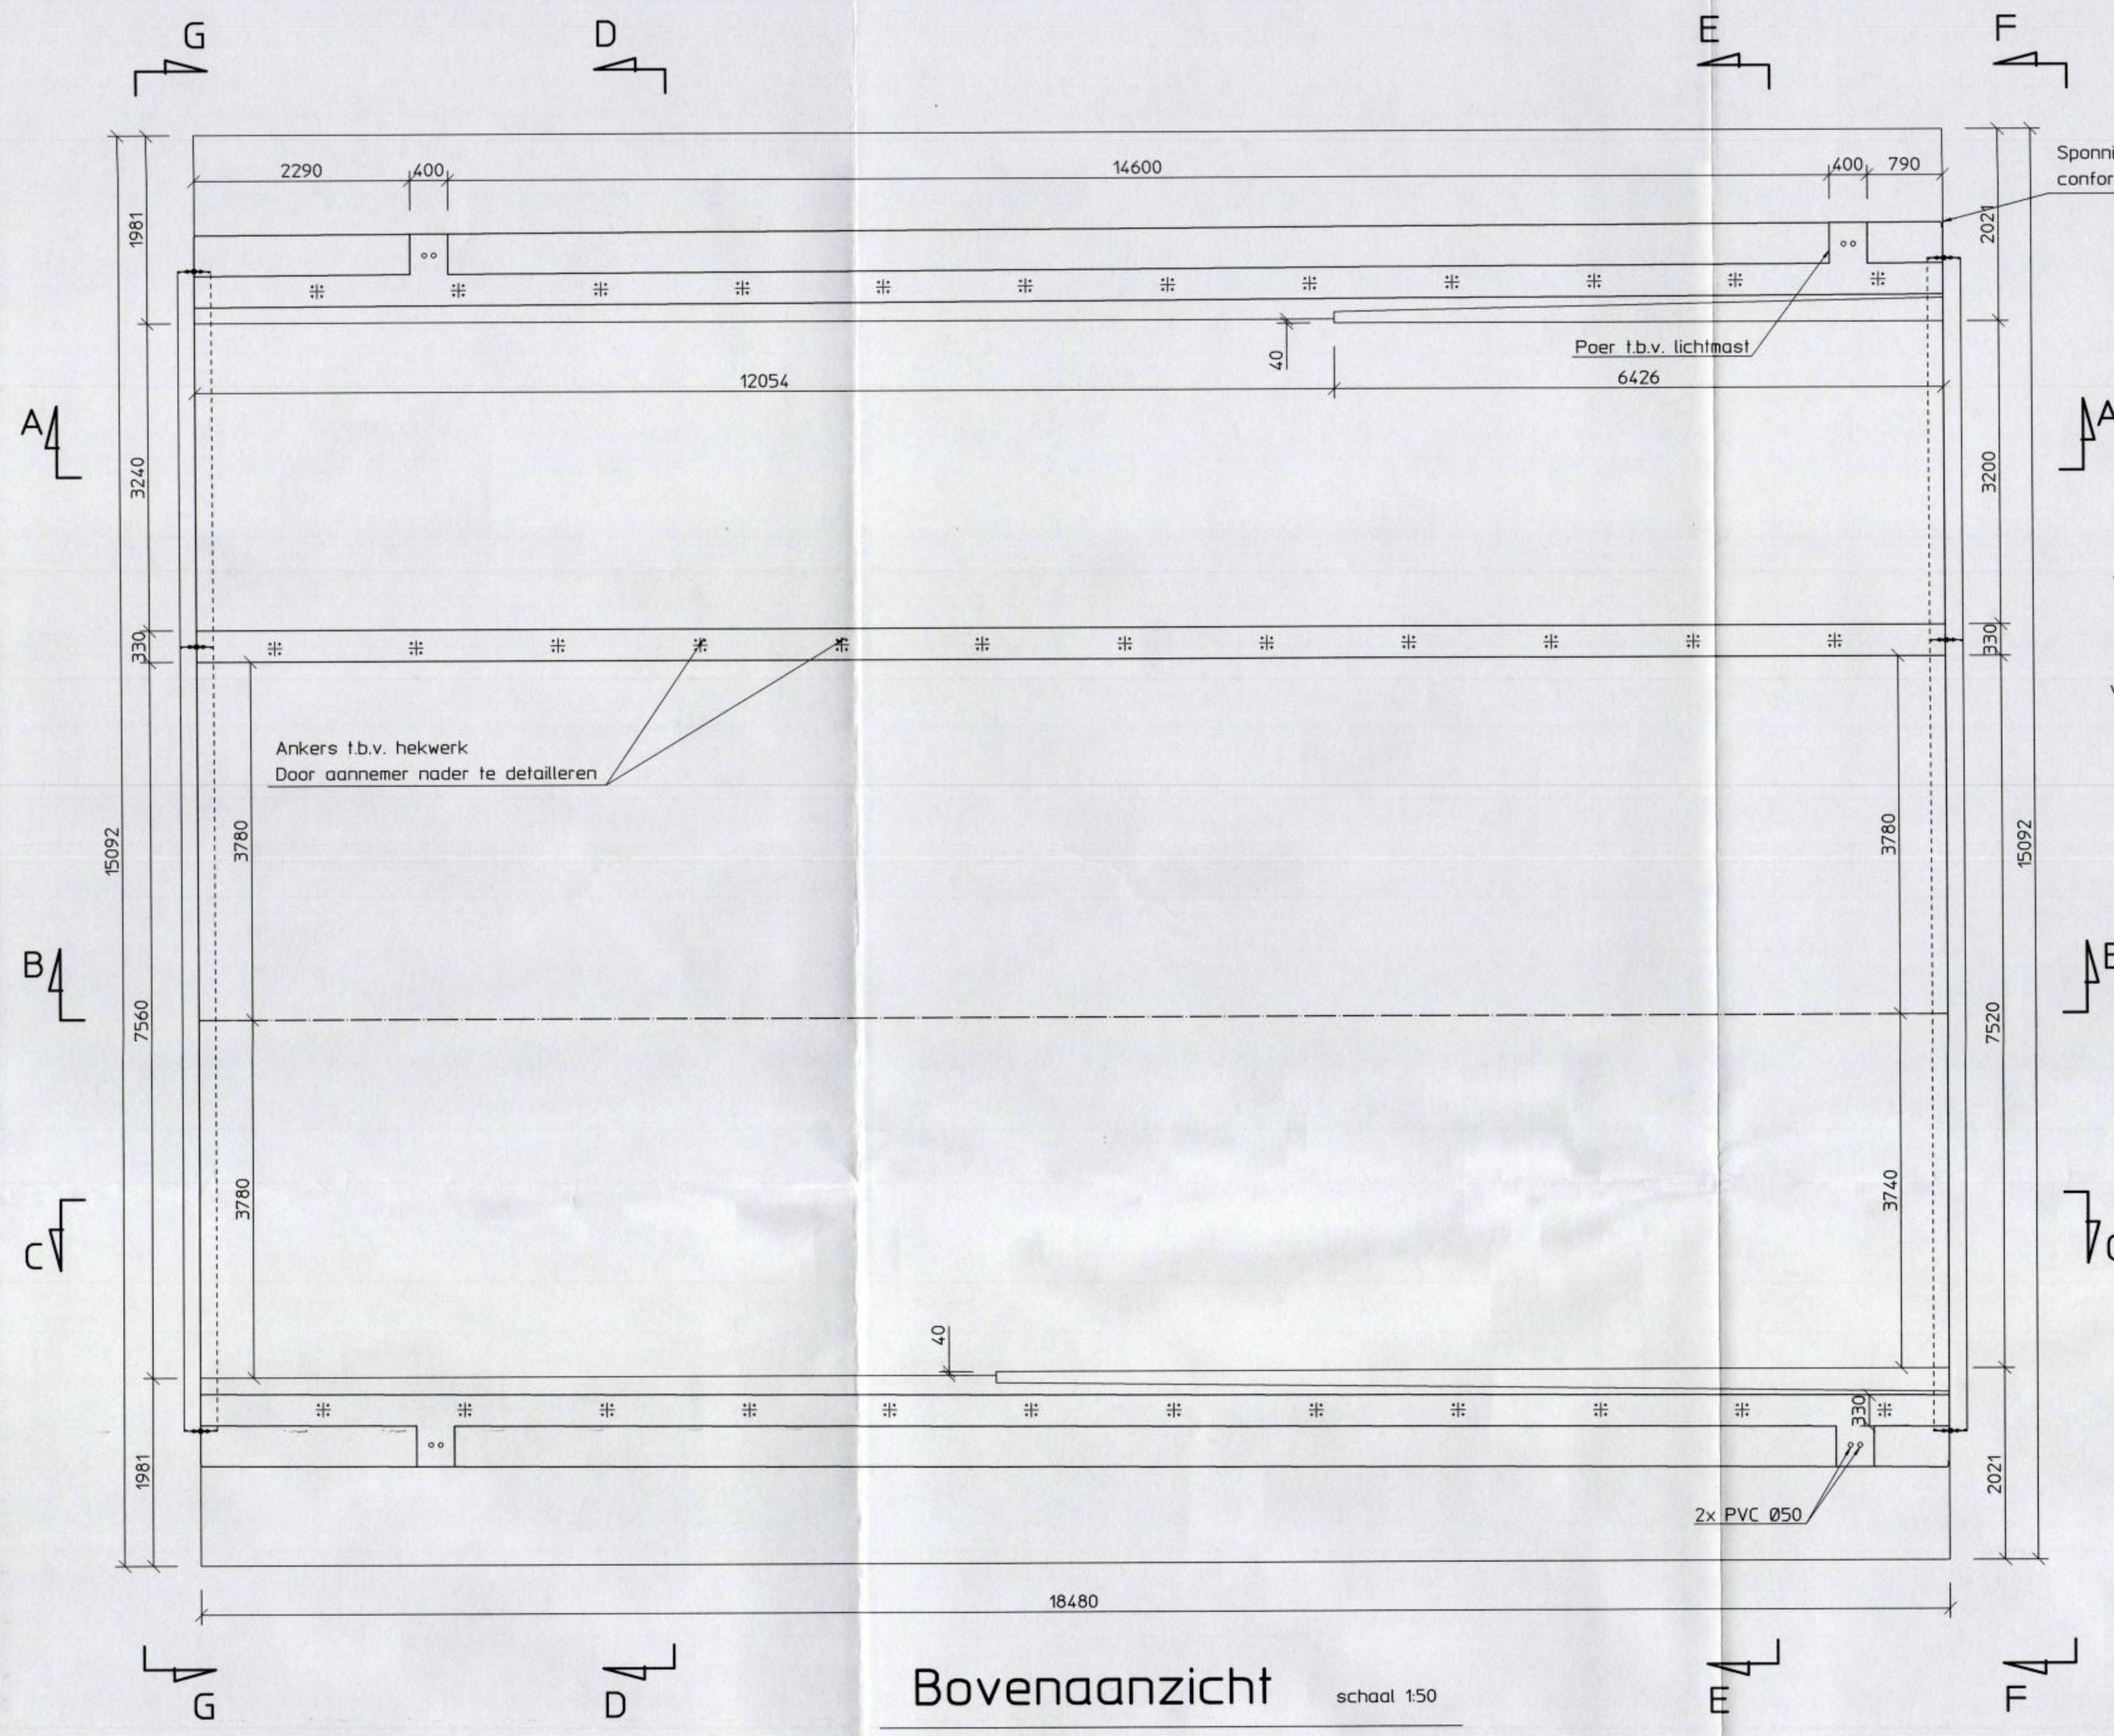


Bovenaanzicht schaal 150

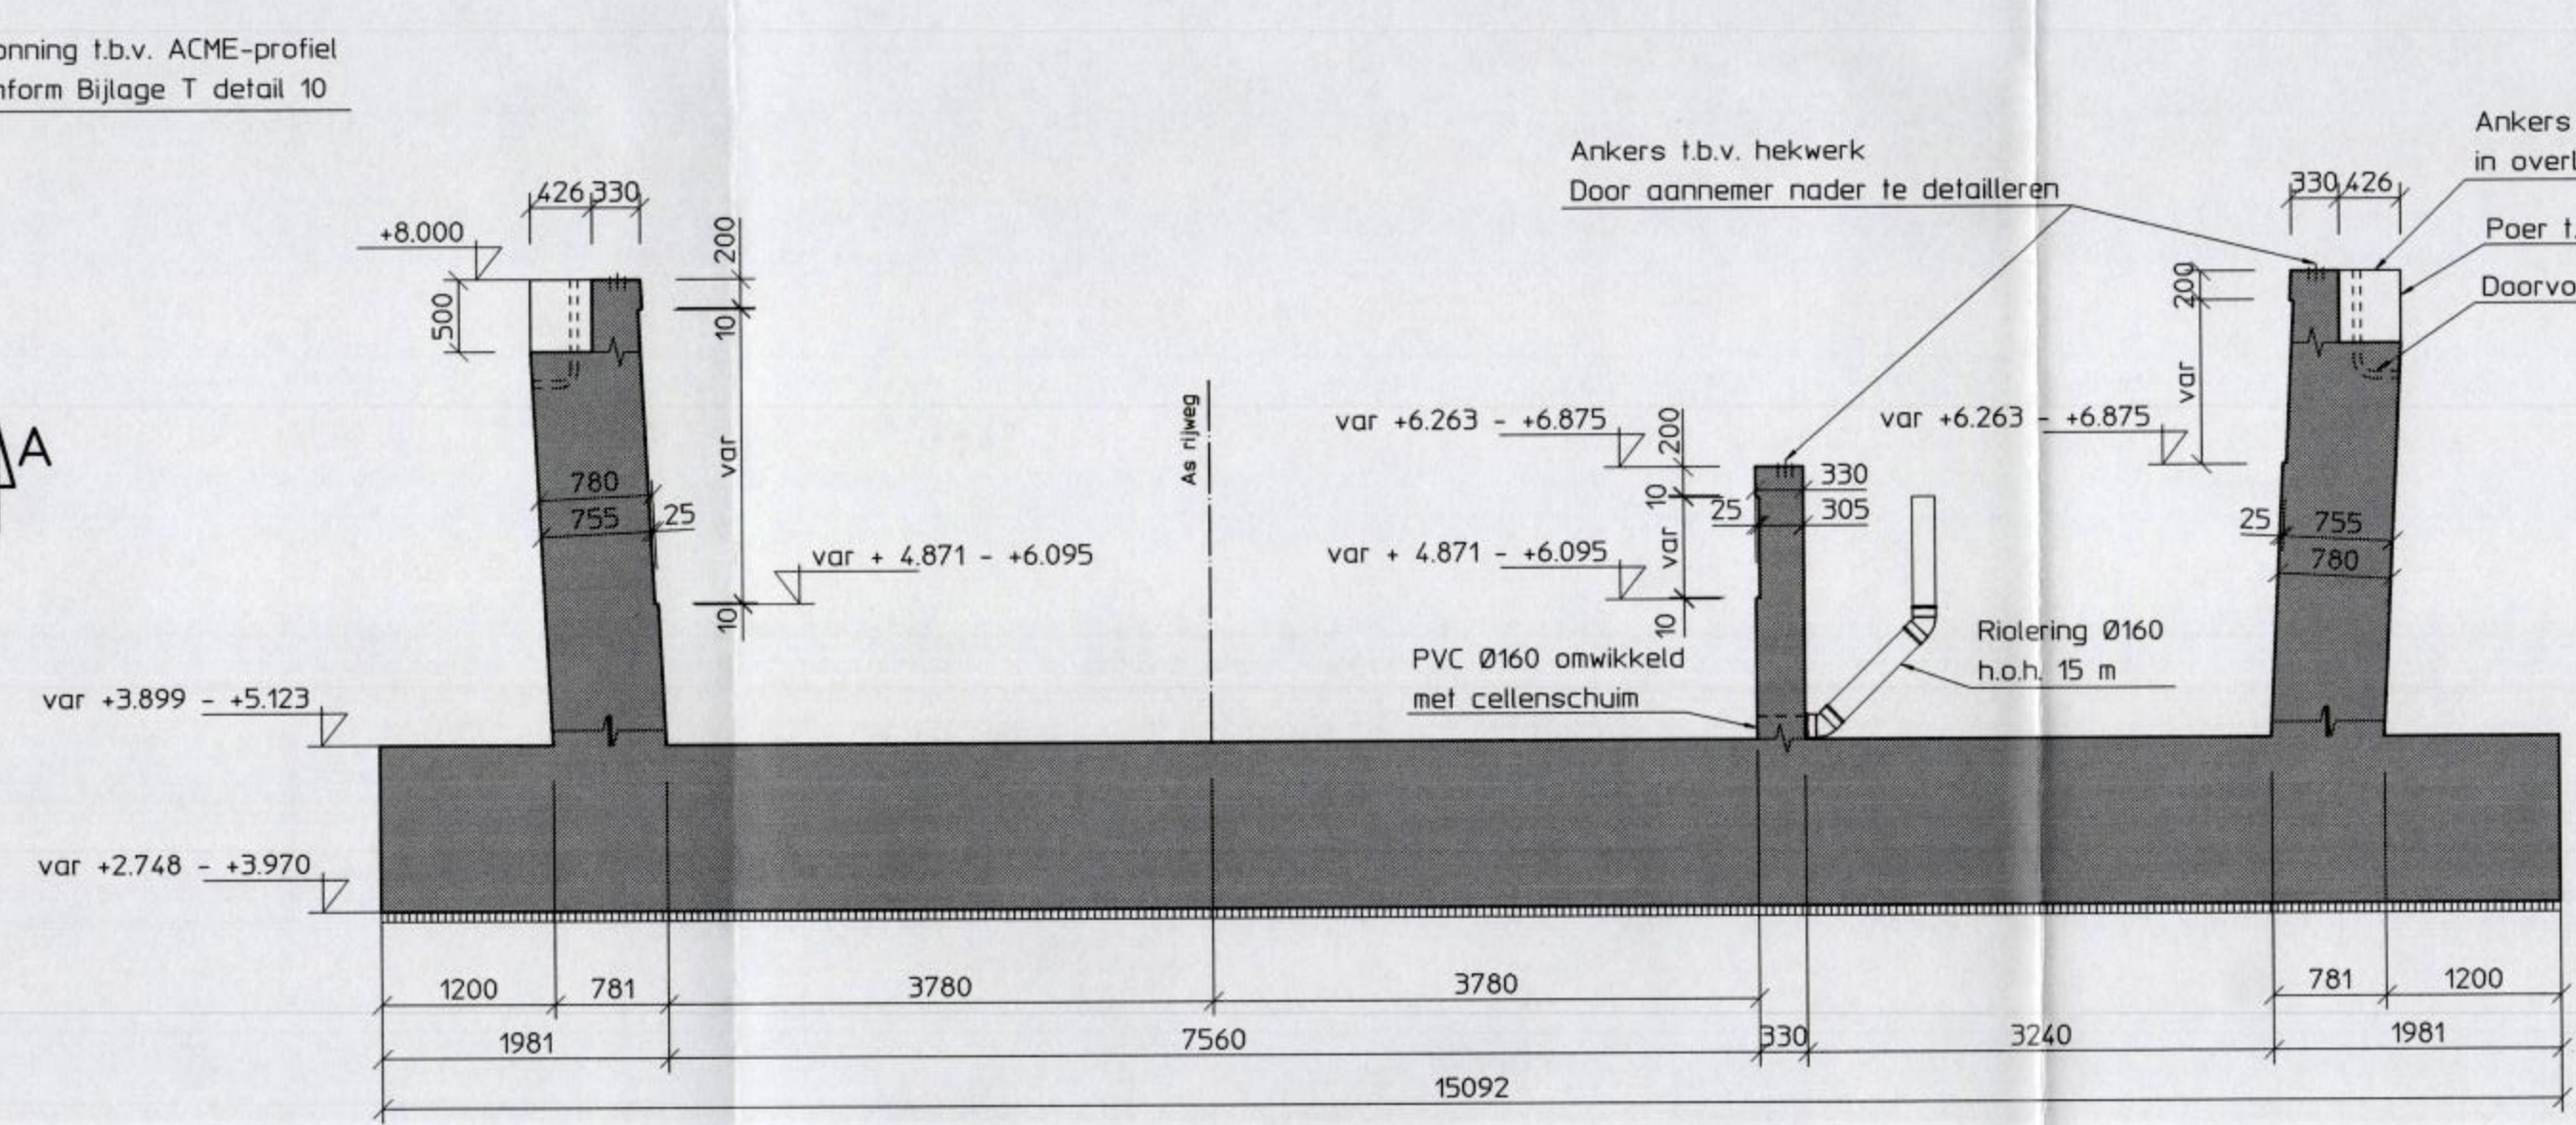


Doorsnede D schaal 150

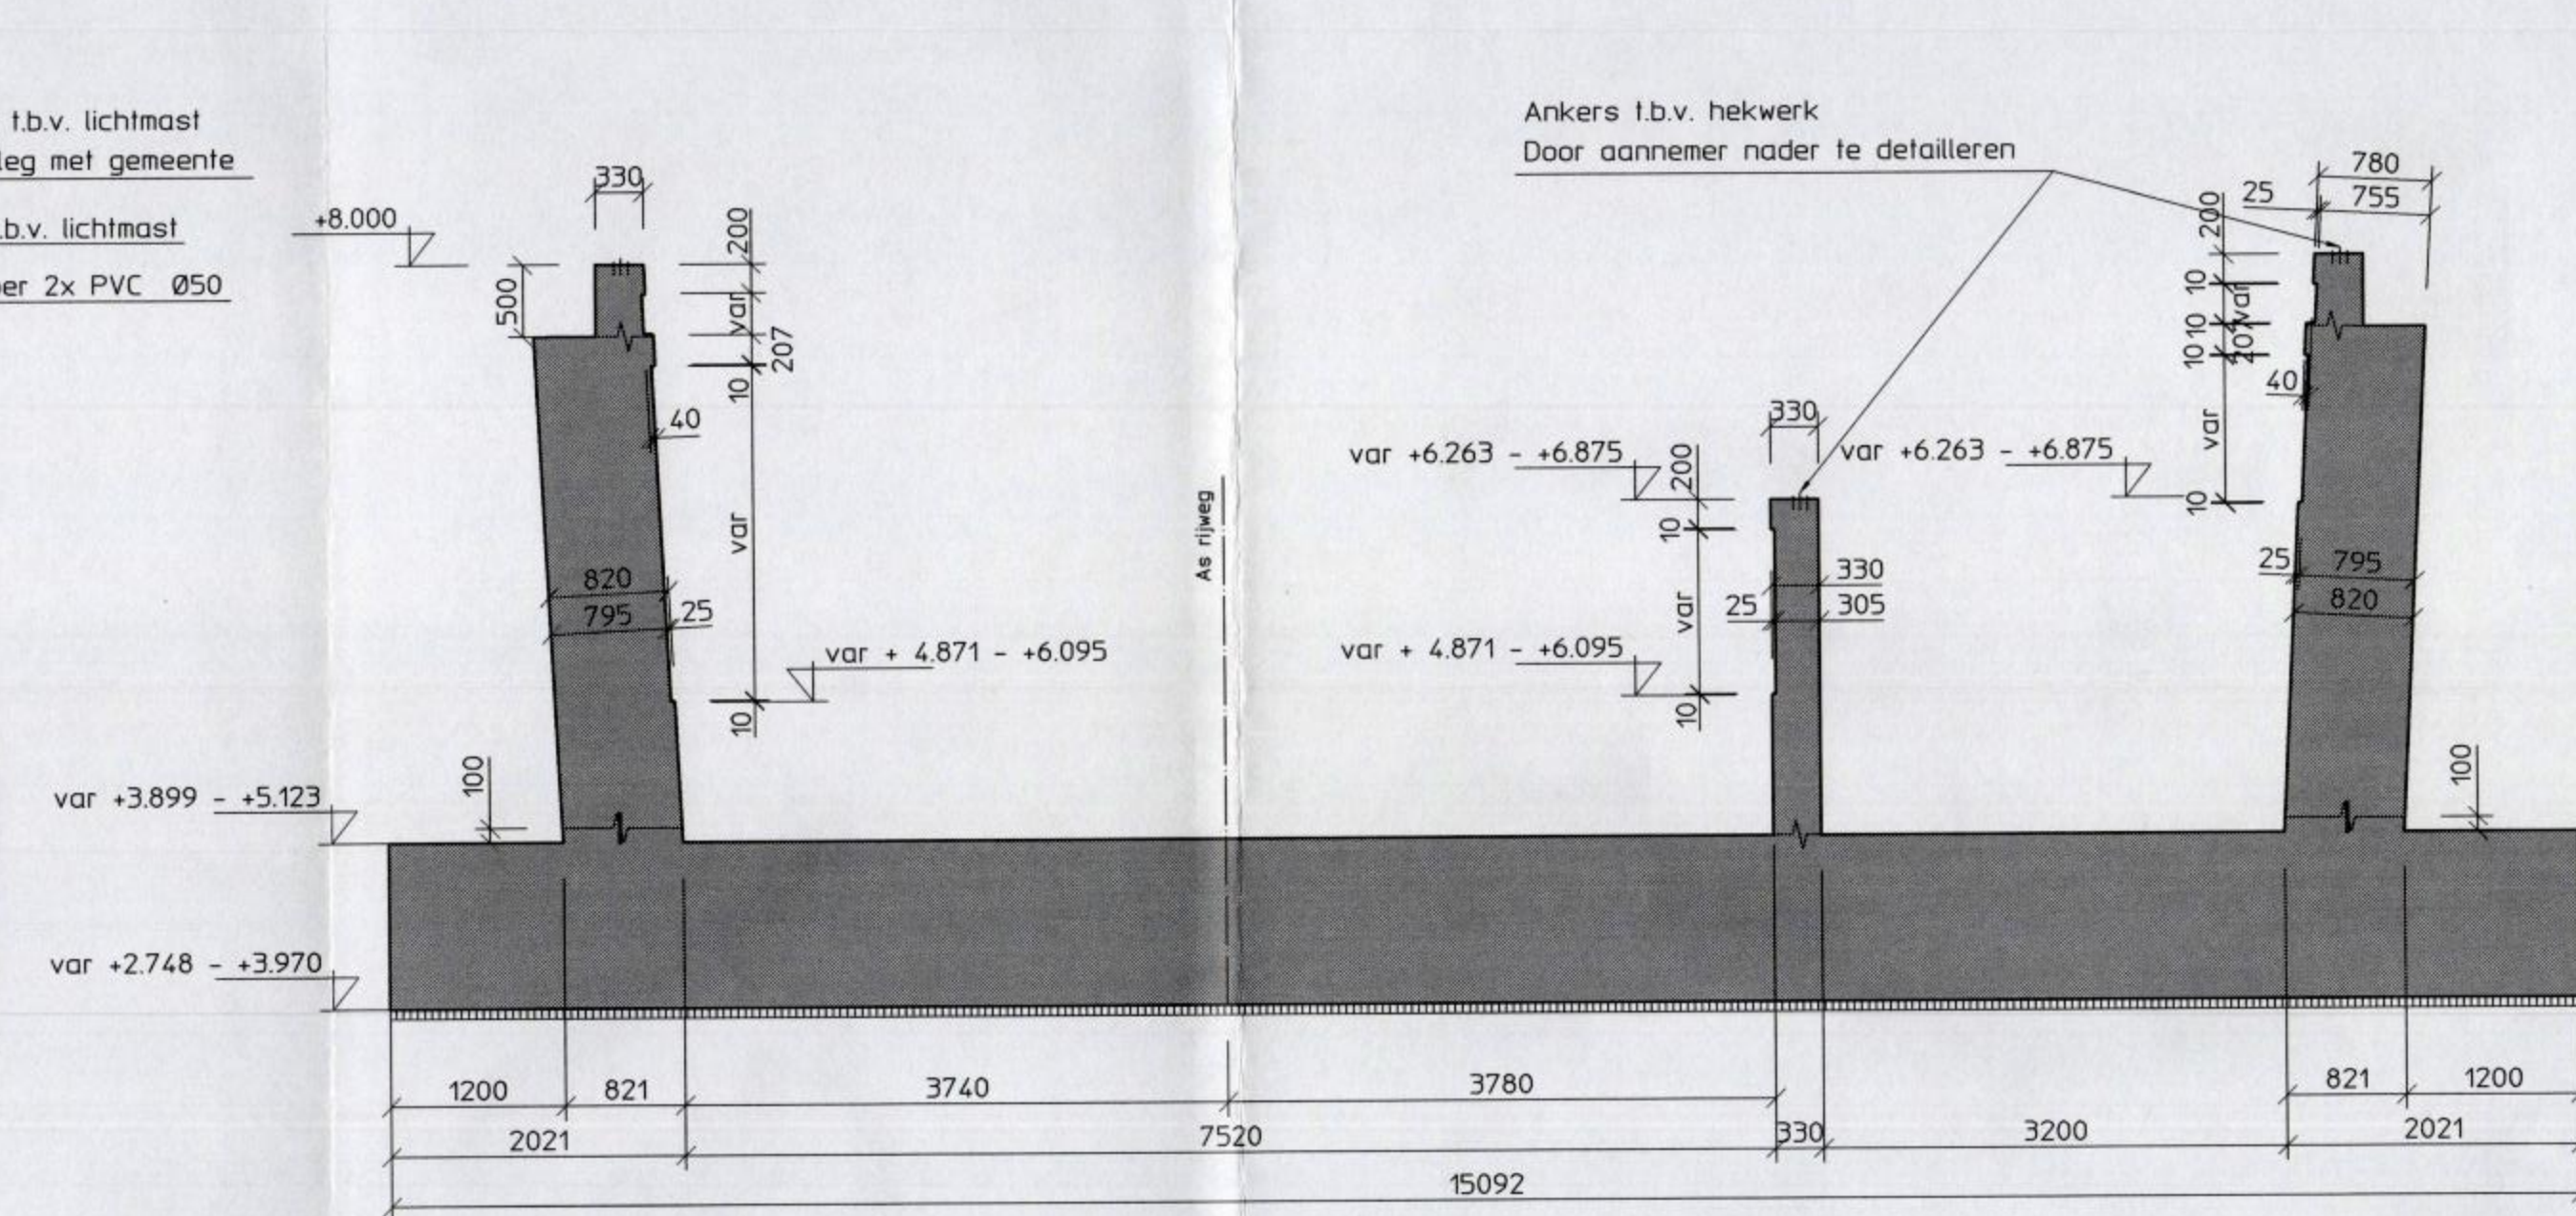


Doorsnede E schaal 150

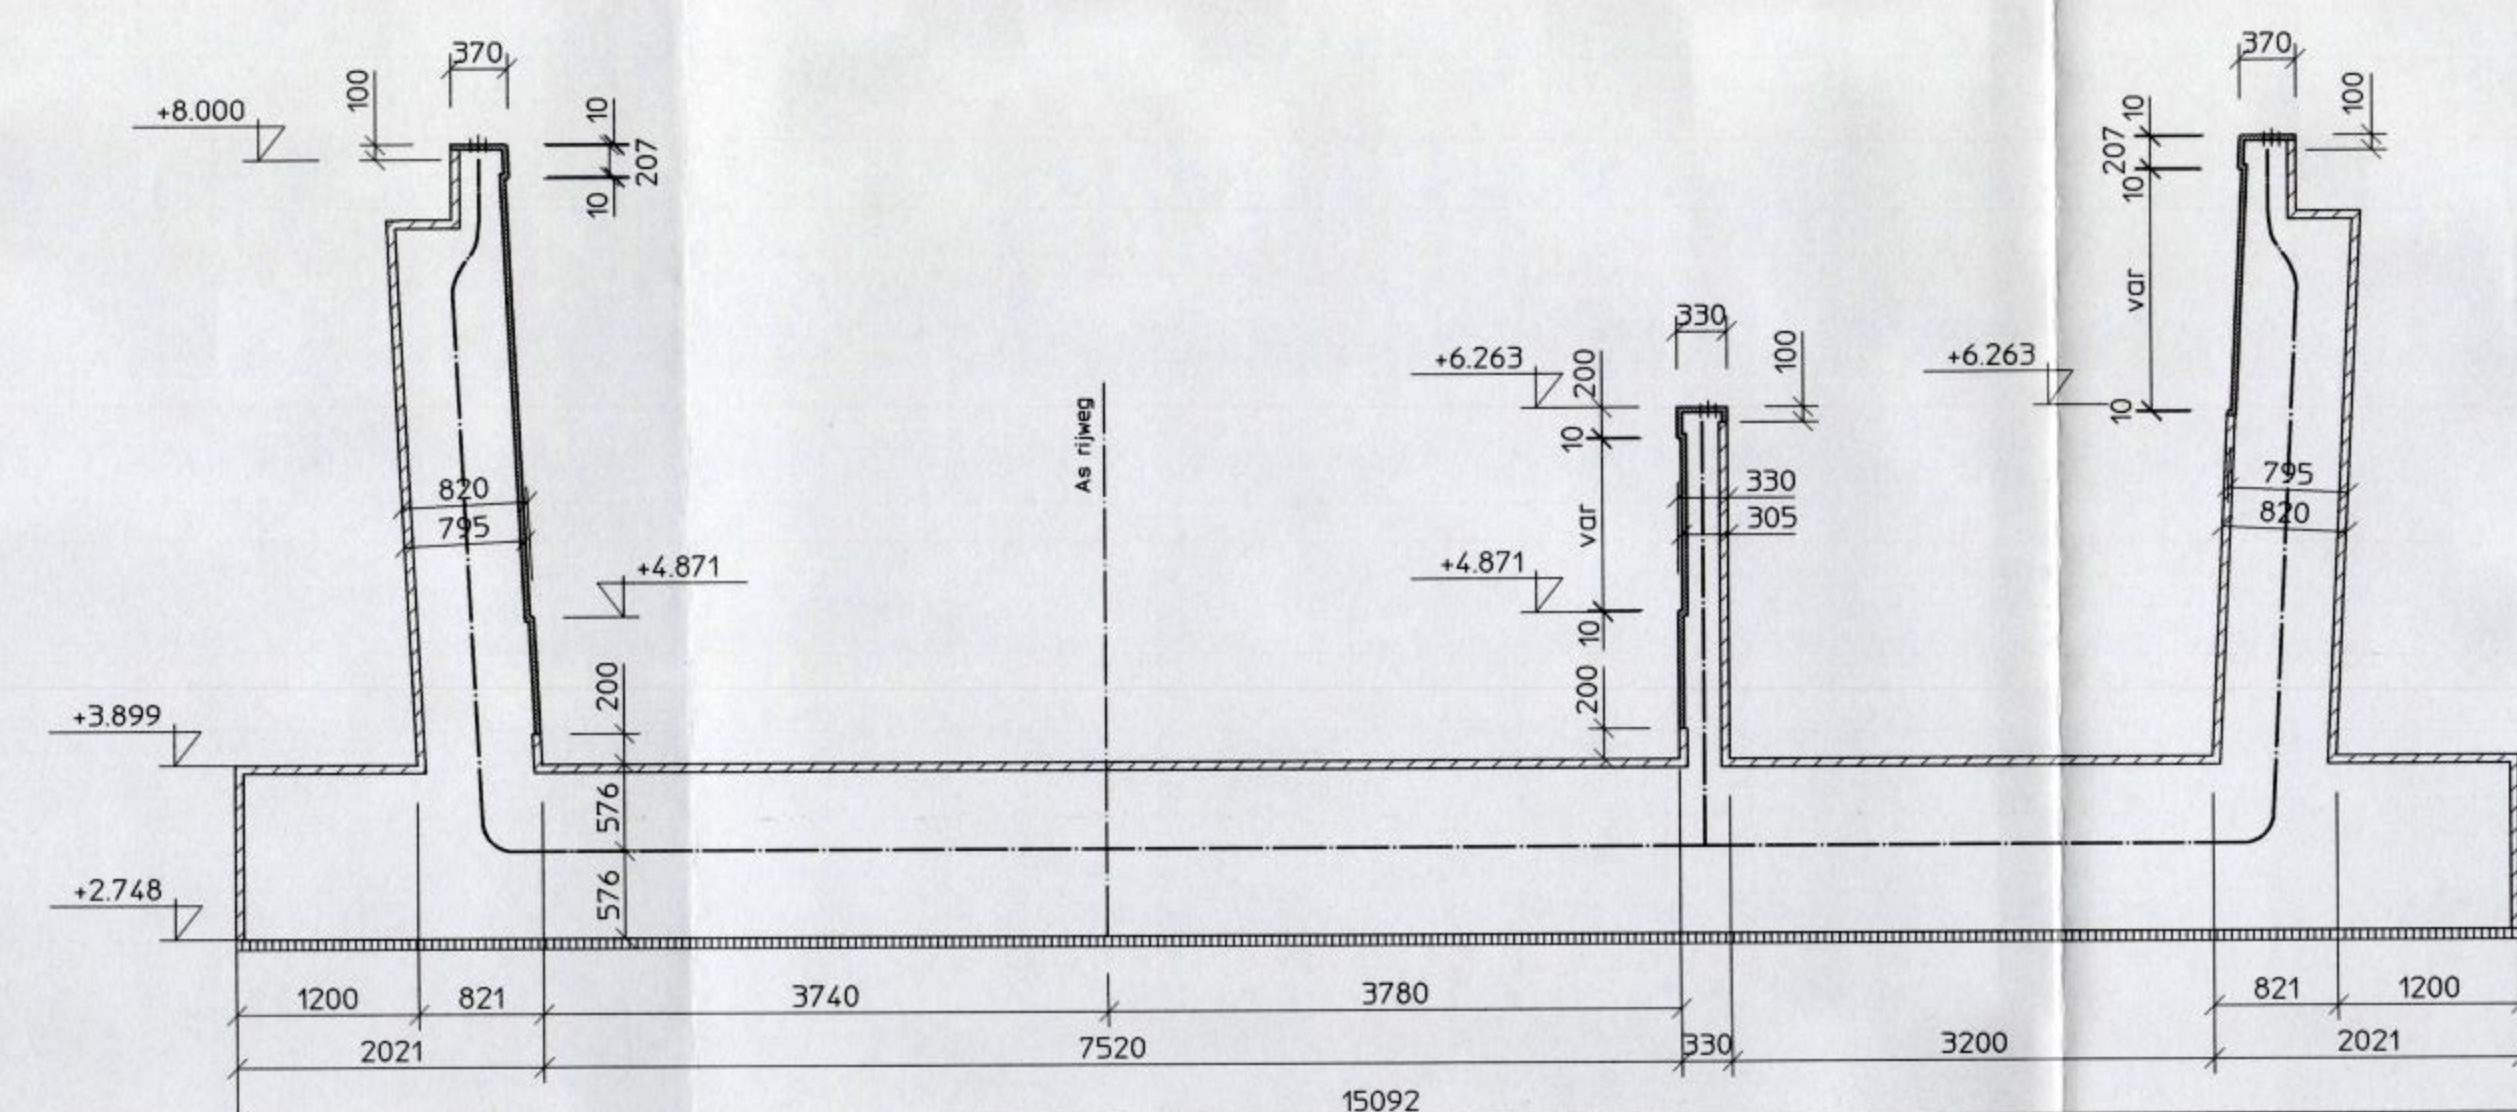


Aanzicht F schaal 150

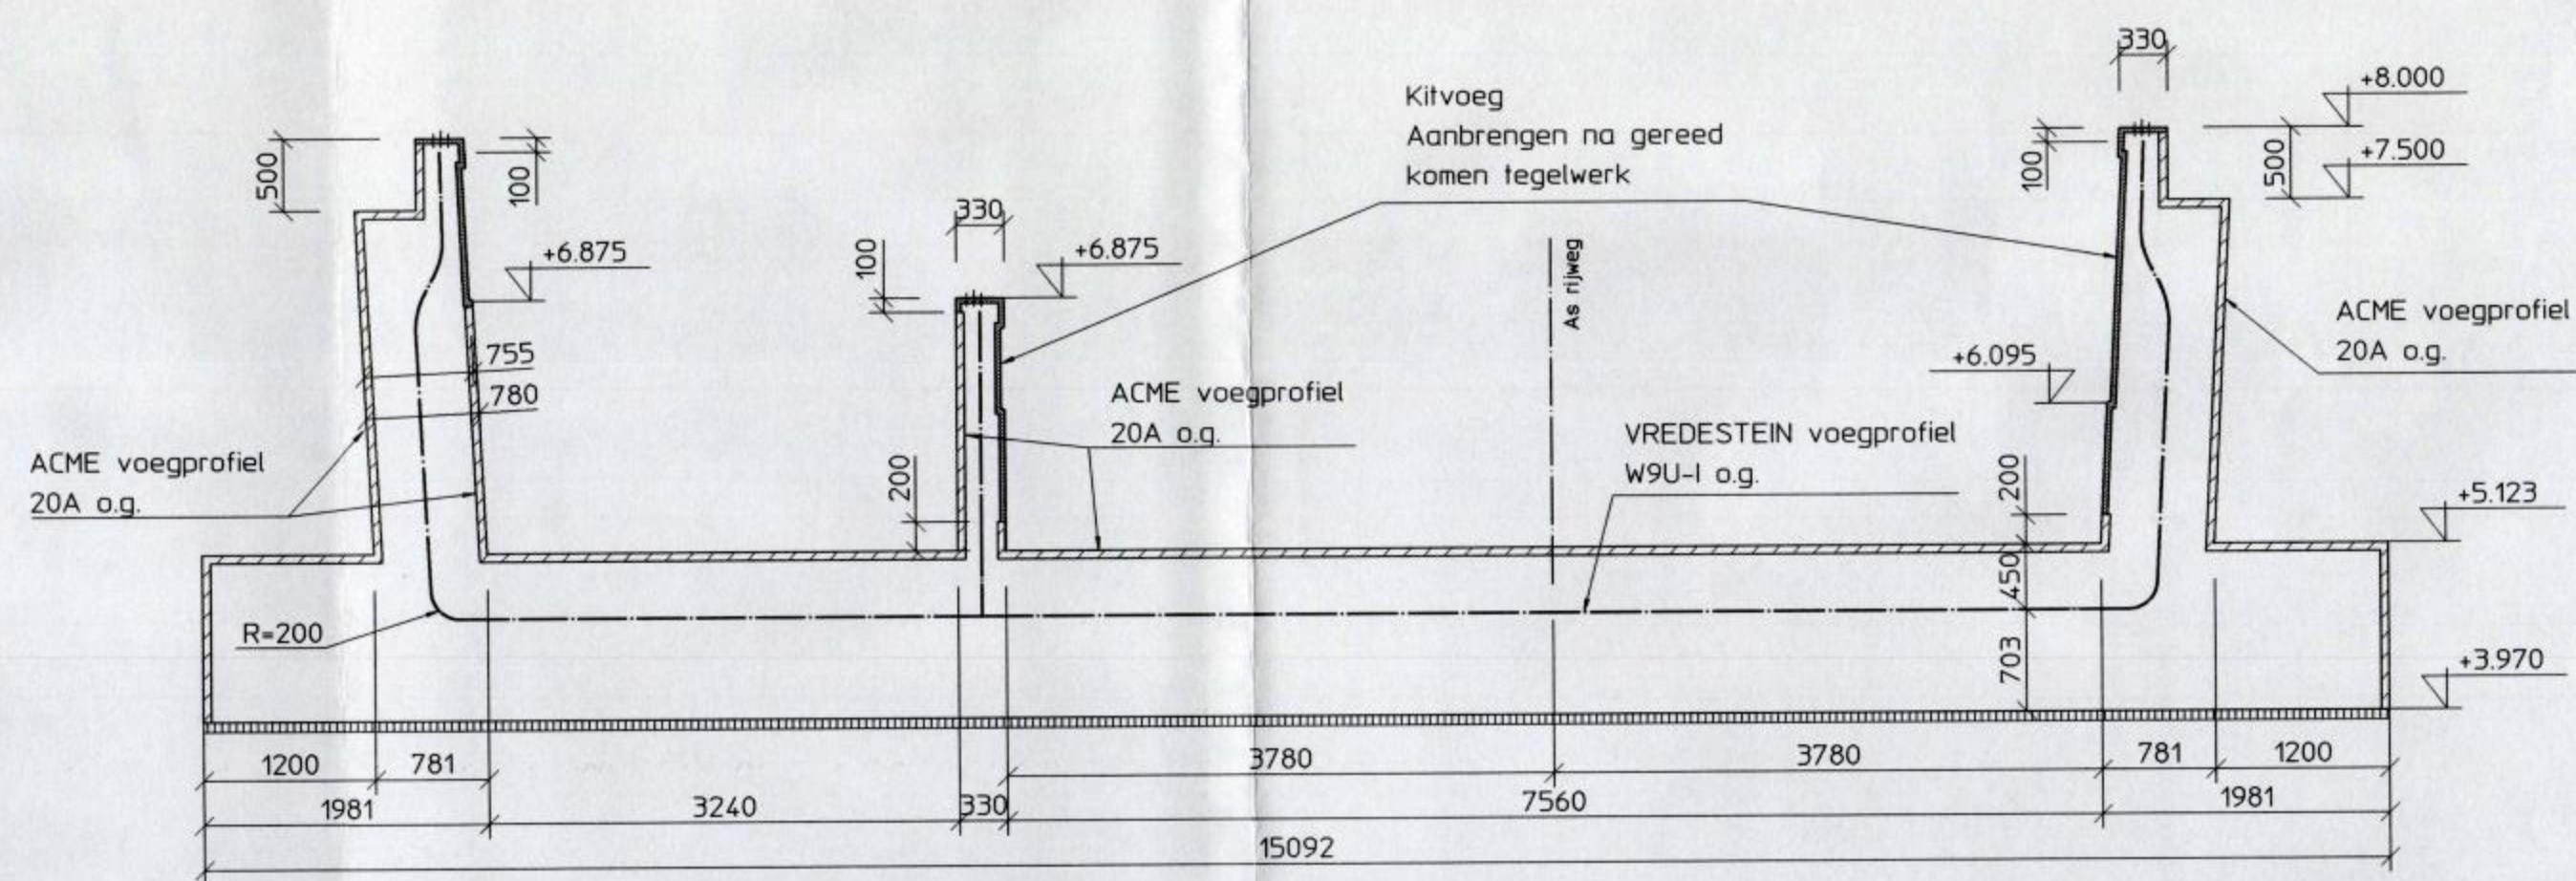


Aanzicht G schaal 150

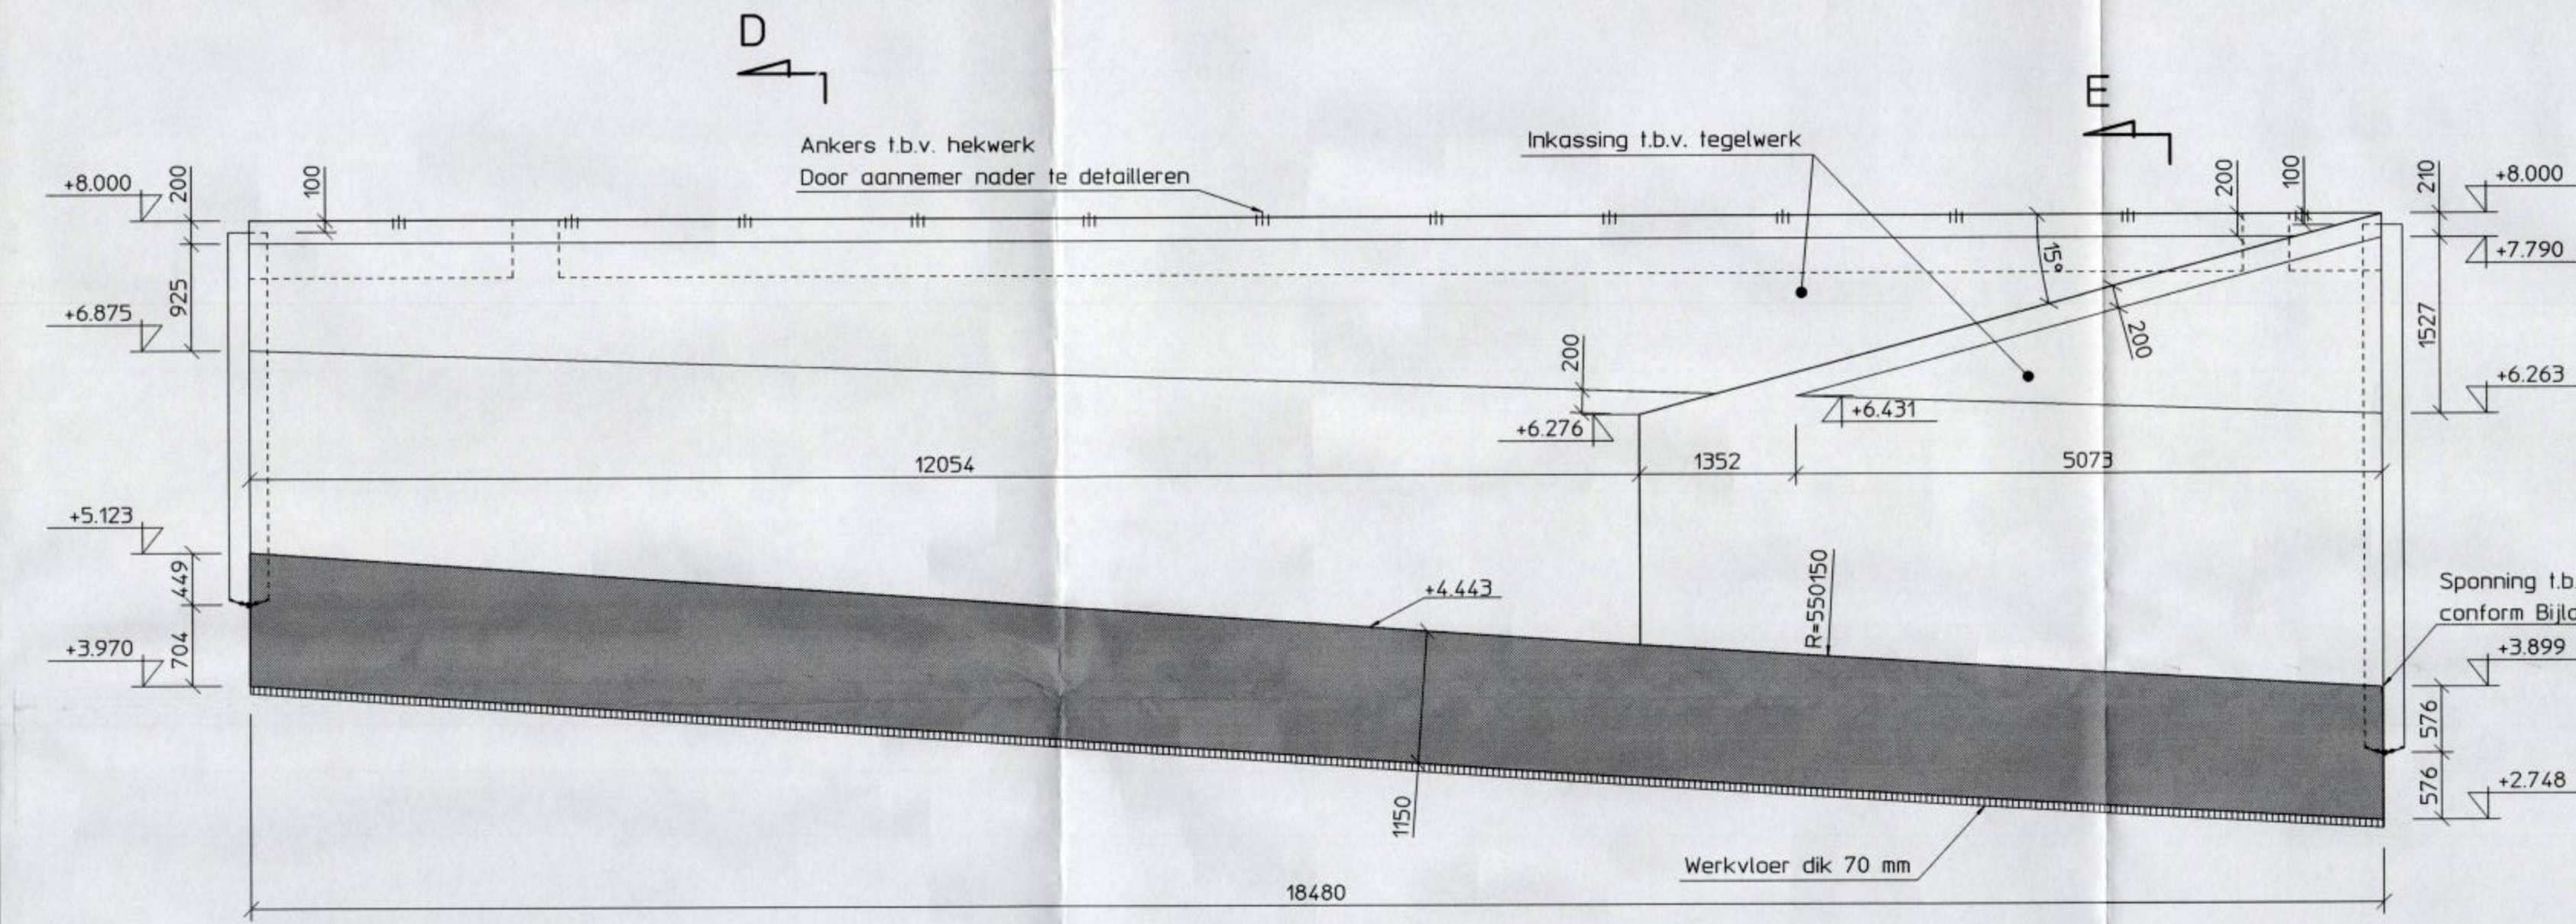


Doorsnede A schaal 150

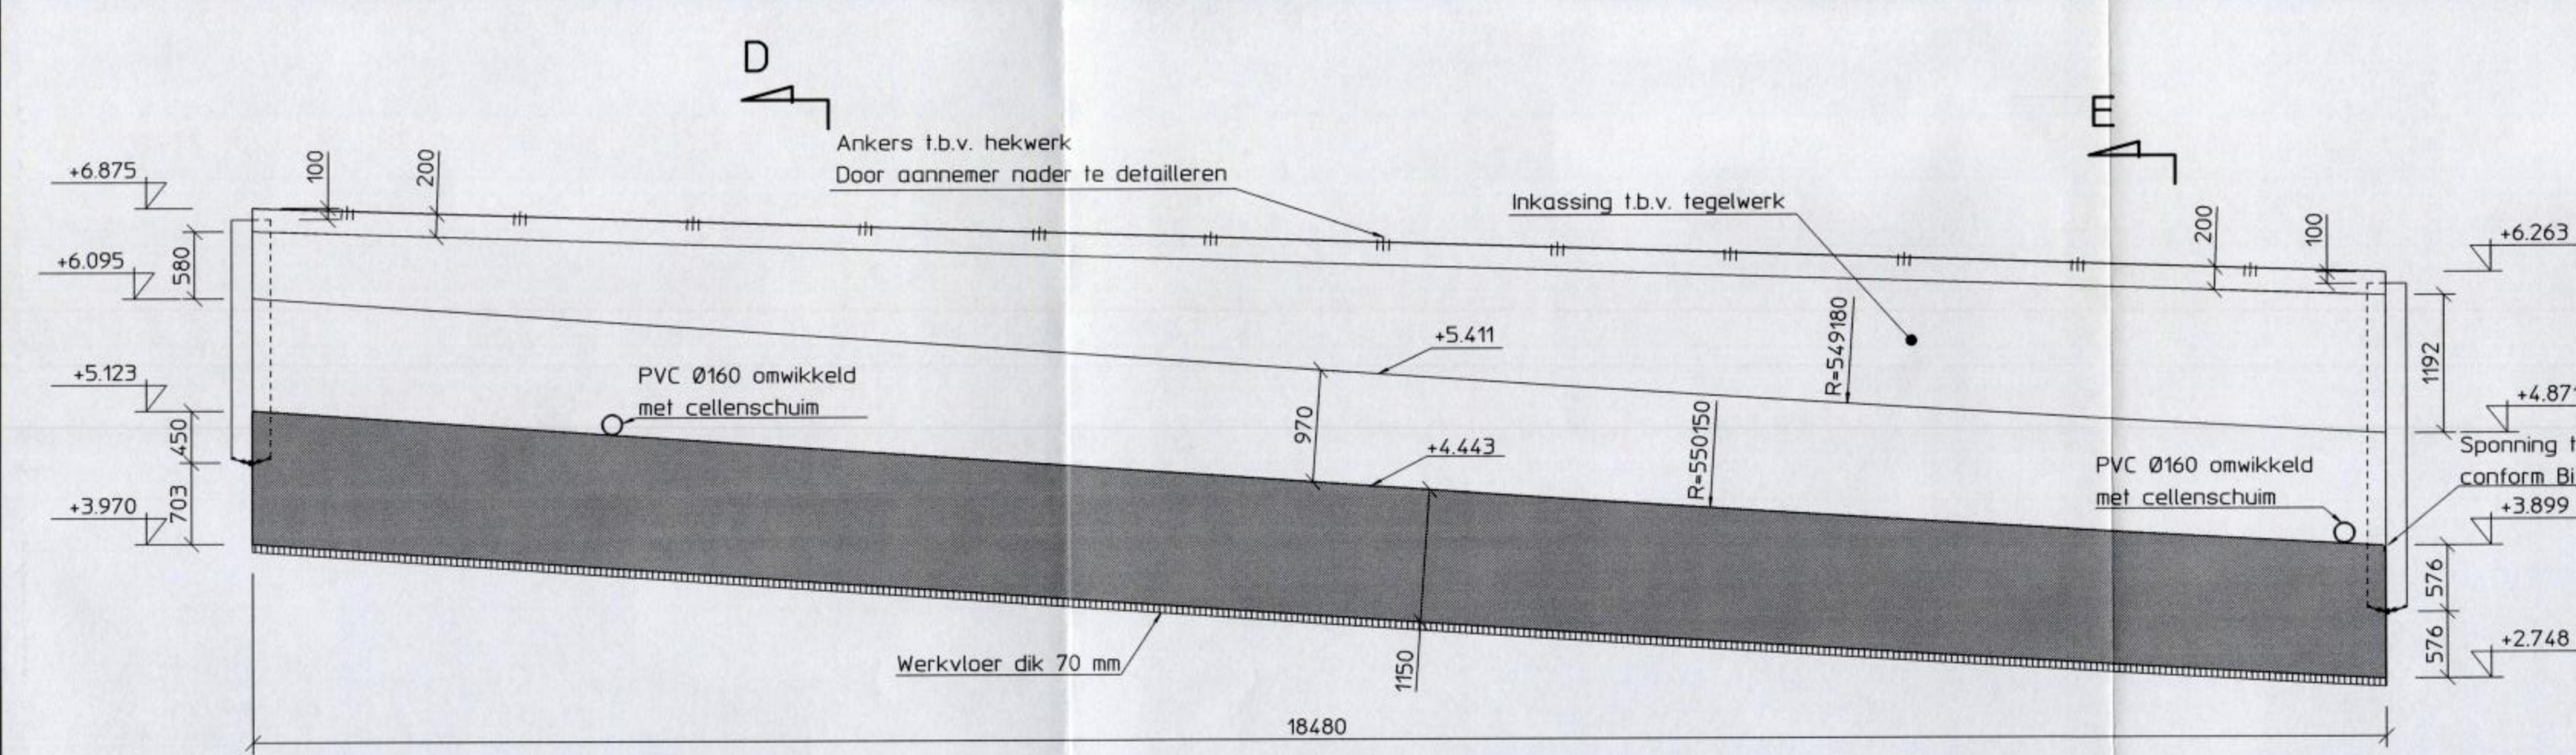

Doorsnede B schaal 150

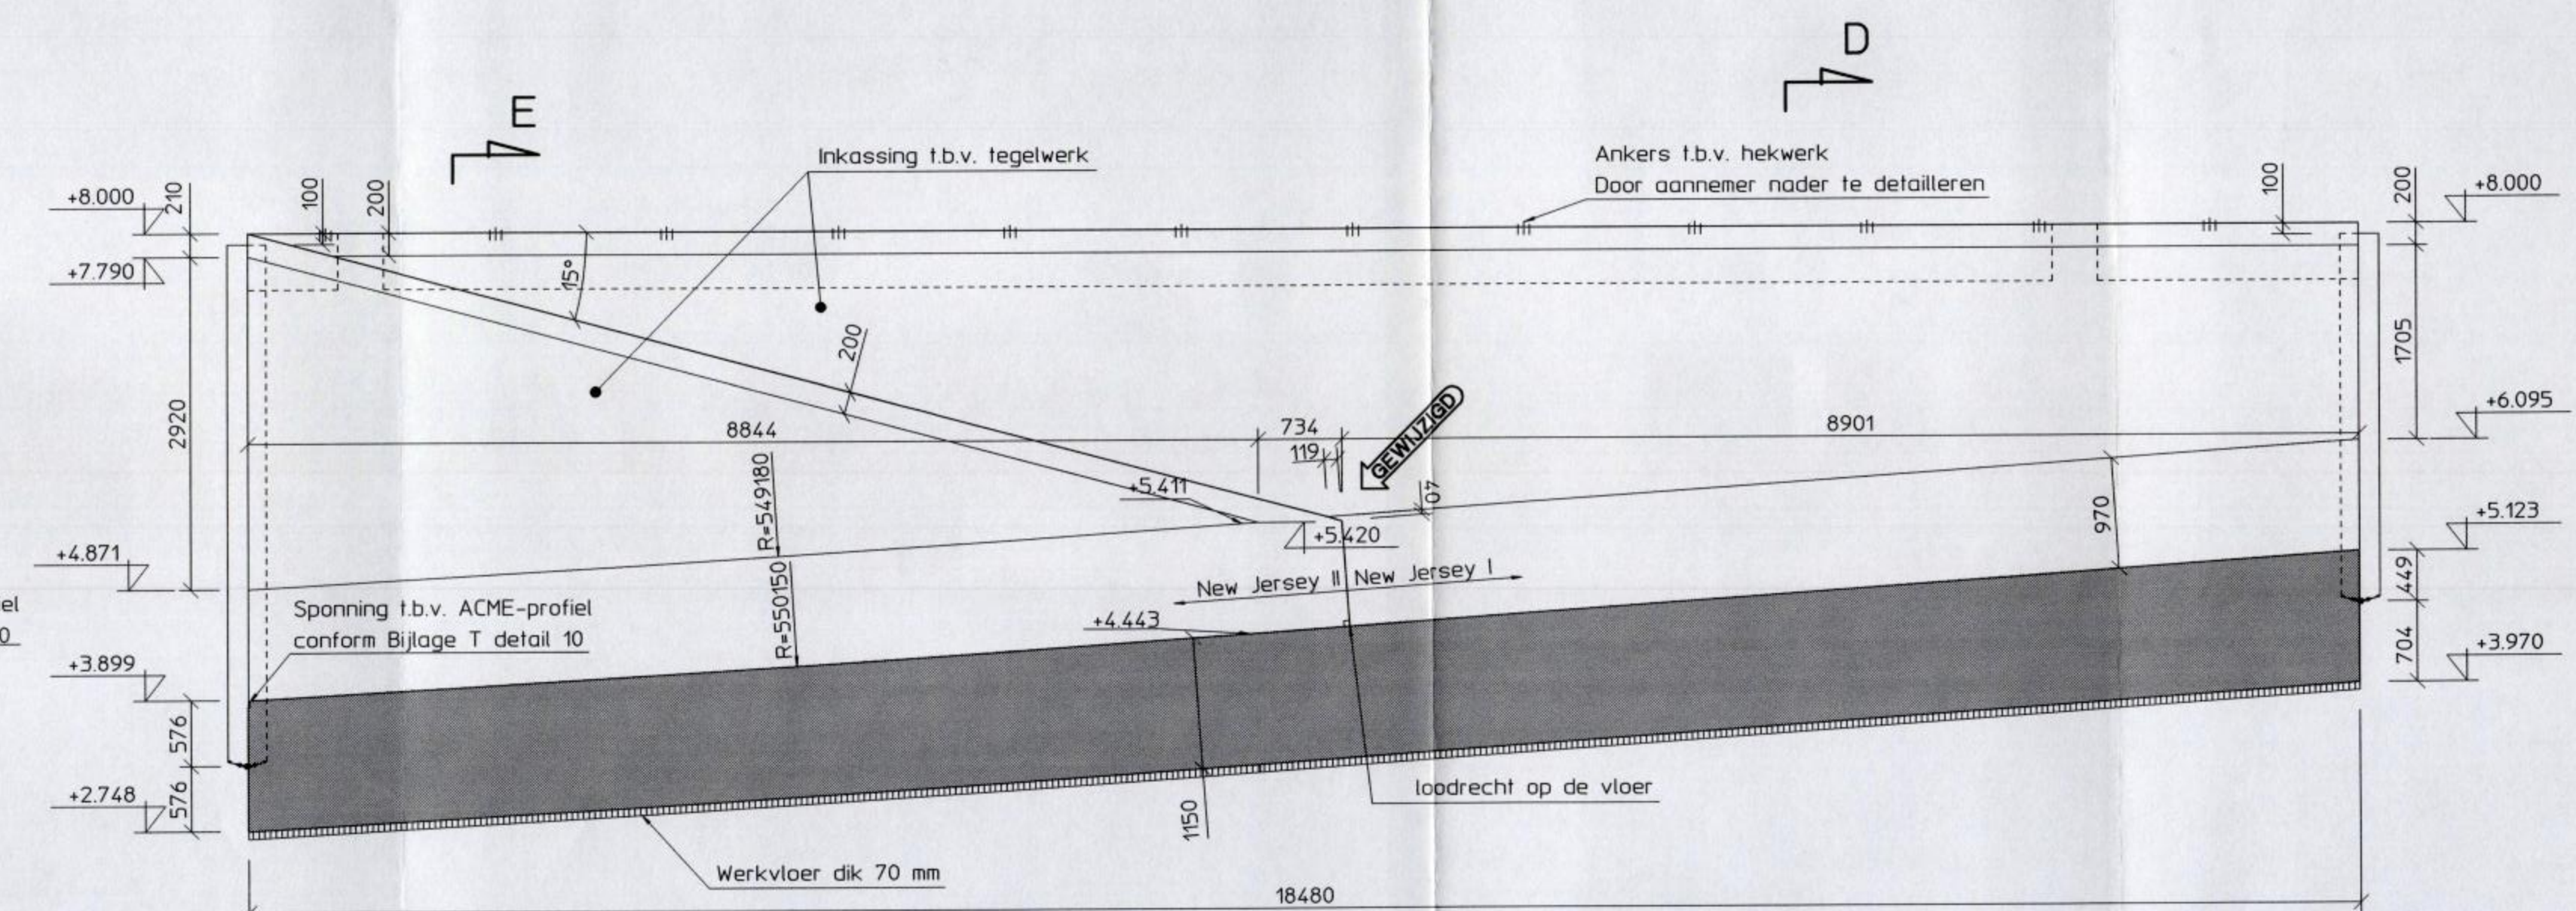

Doorsnede C schaal 150

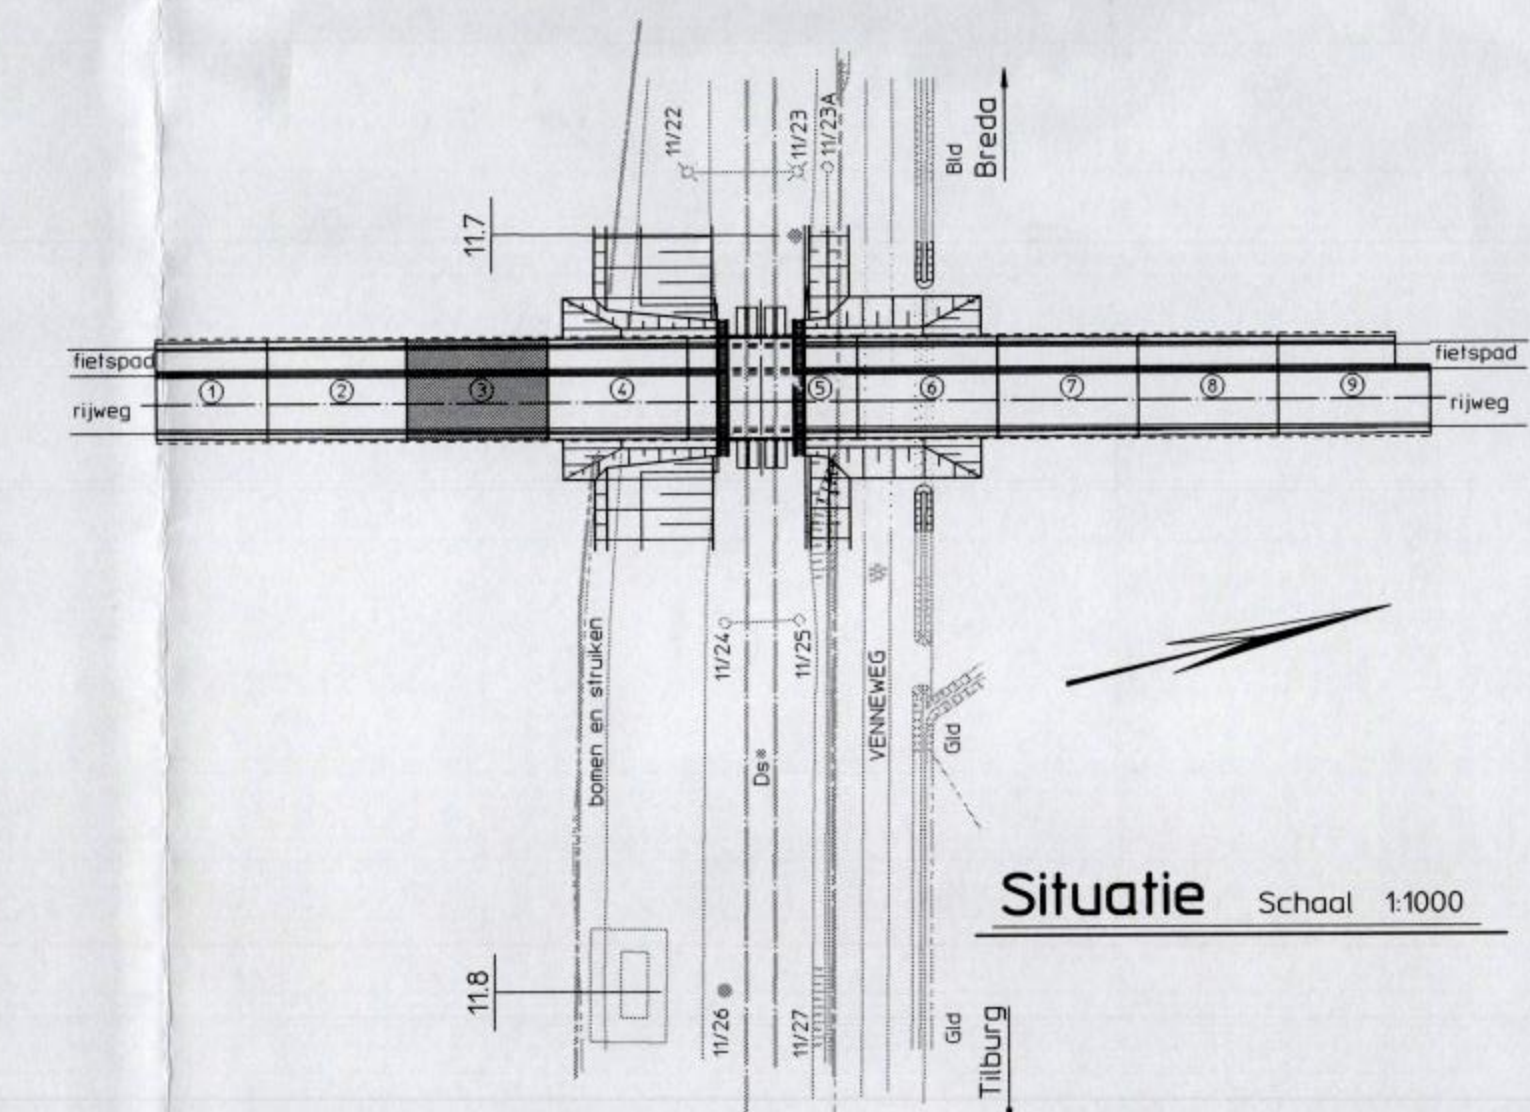

Situatie schaal 1:1000

- maatvoering in mm		- hoogtemaatvoering in m t.o.v. N.A.P.	
(Status: REVISIE d.d. 17-12-1999 14:05:05)			
naam	par	datum	
getekend	M.W. Gritter	17-12-99	
projectleider	C.P. Vink		
projectnr	3362706	var	10
locatie	V08B/09-50	Brn C	aanpak
toestand	AO	New Jersey	
schaal	150		
420	123	11.720	713
3362706	30	M	
Holland Railconsult			