
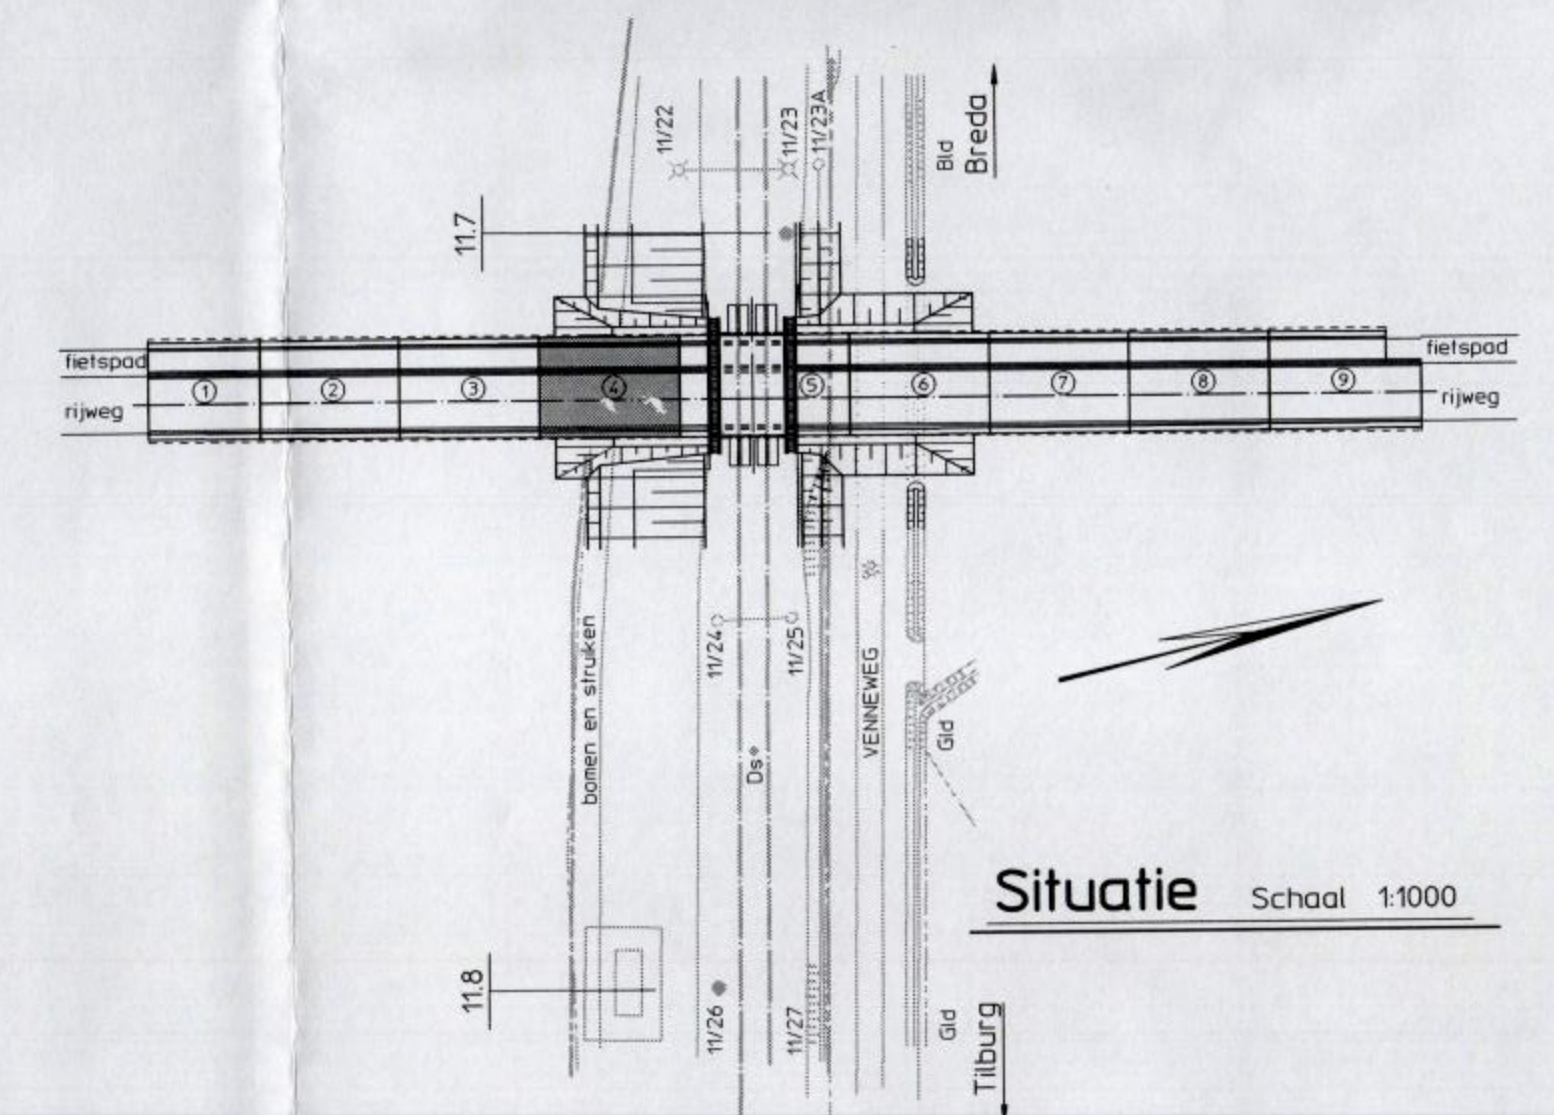
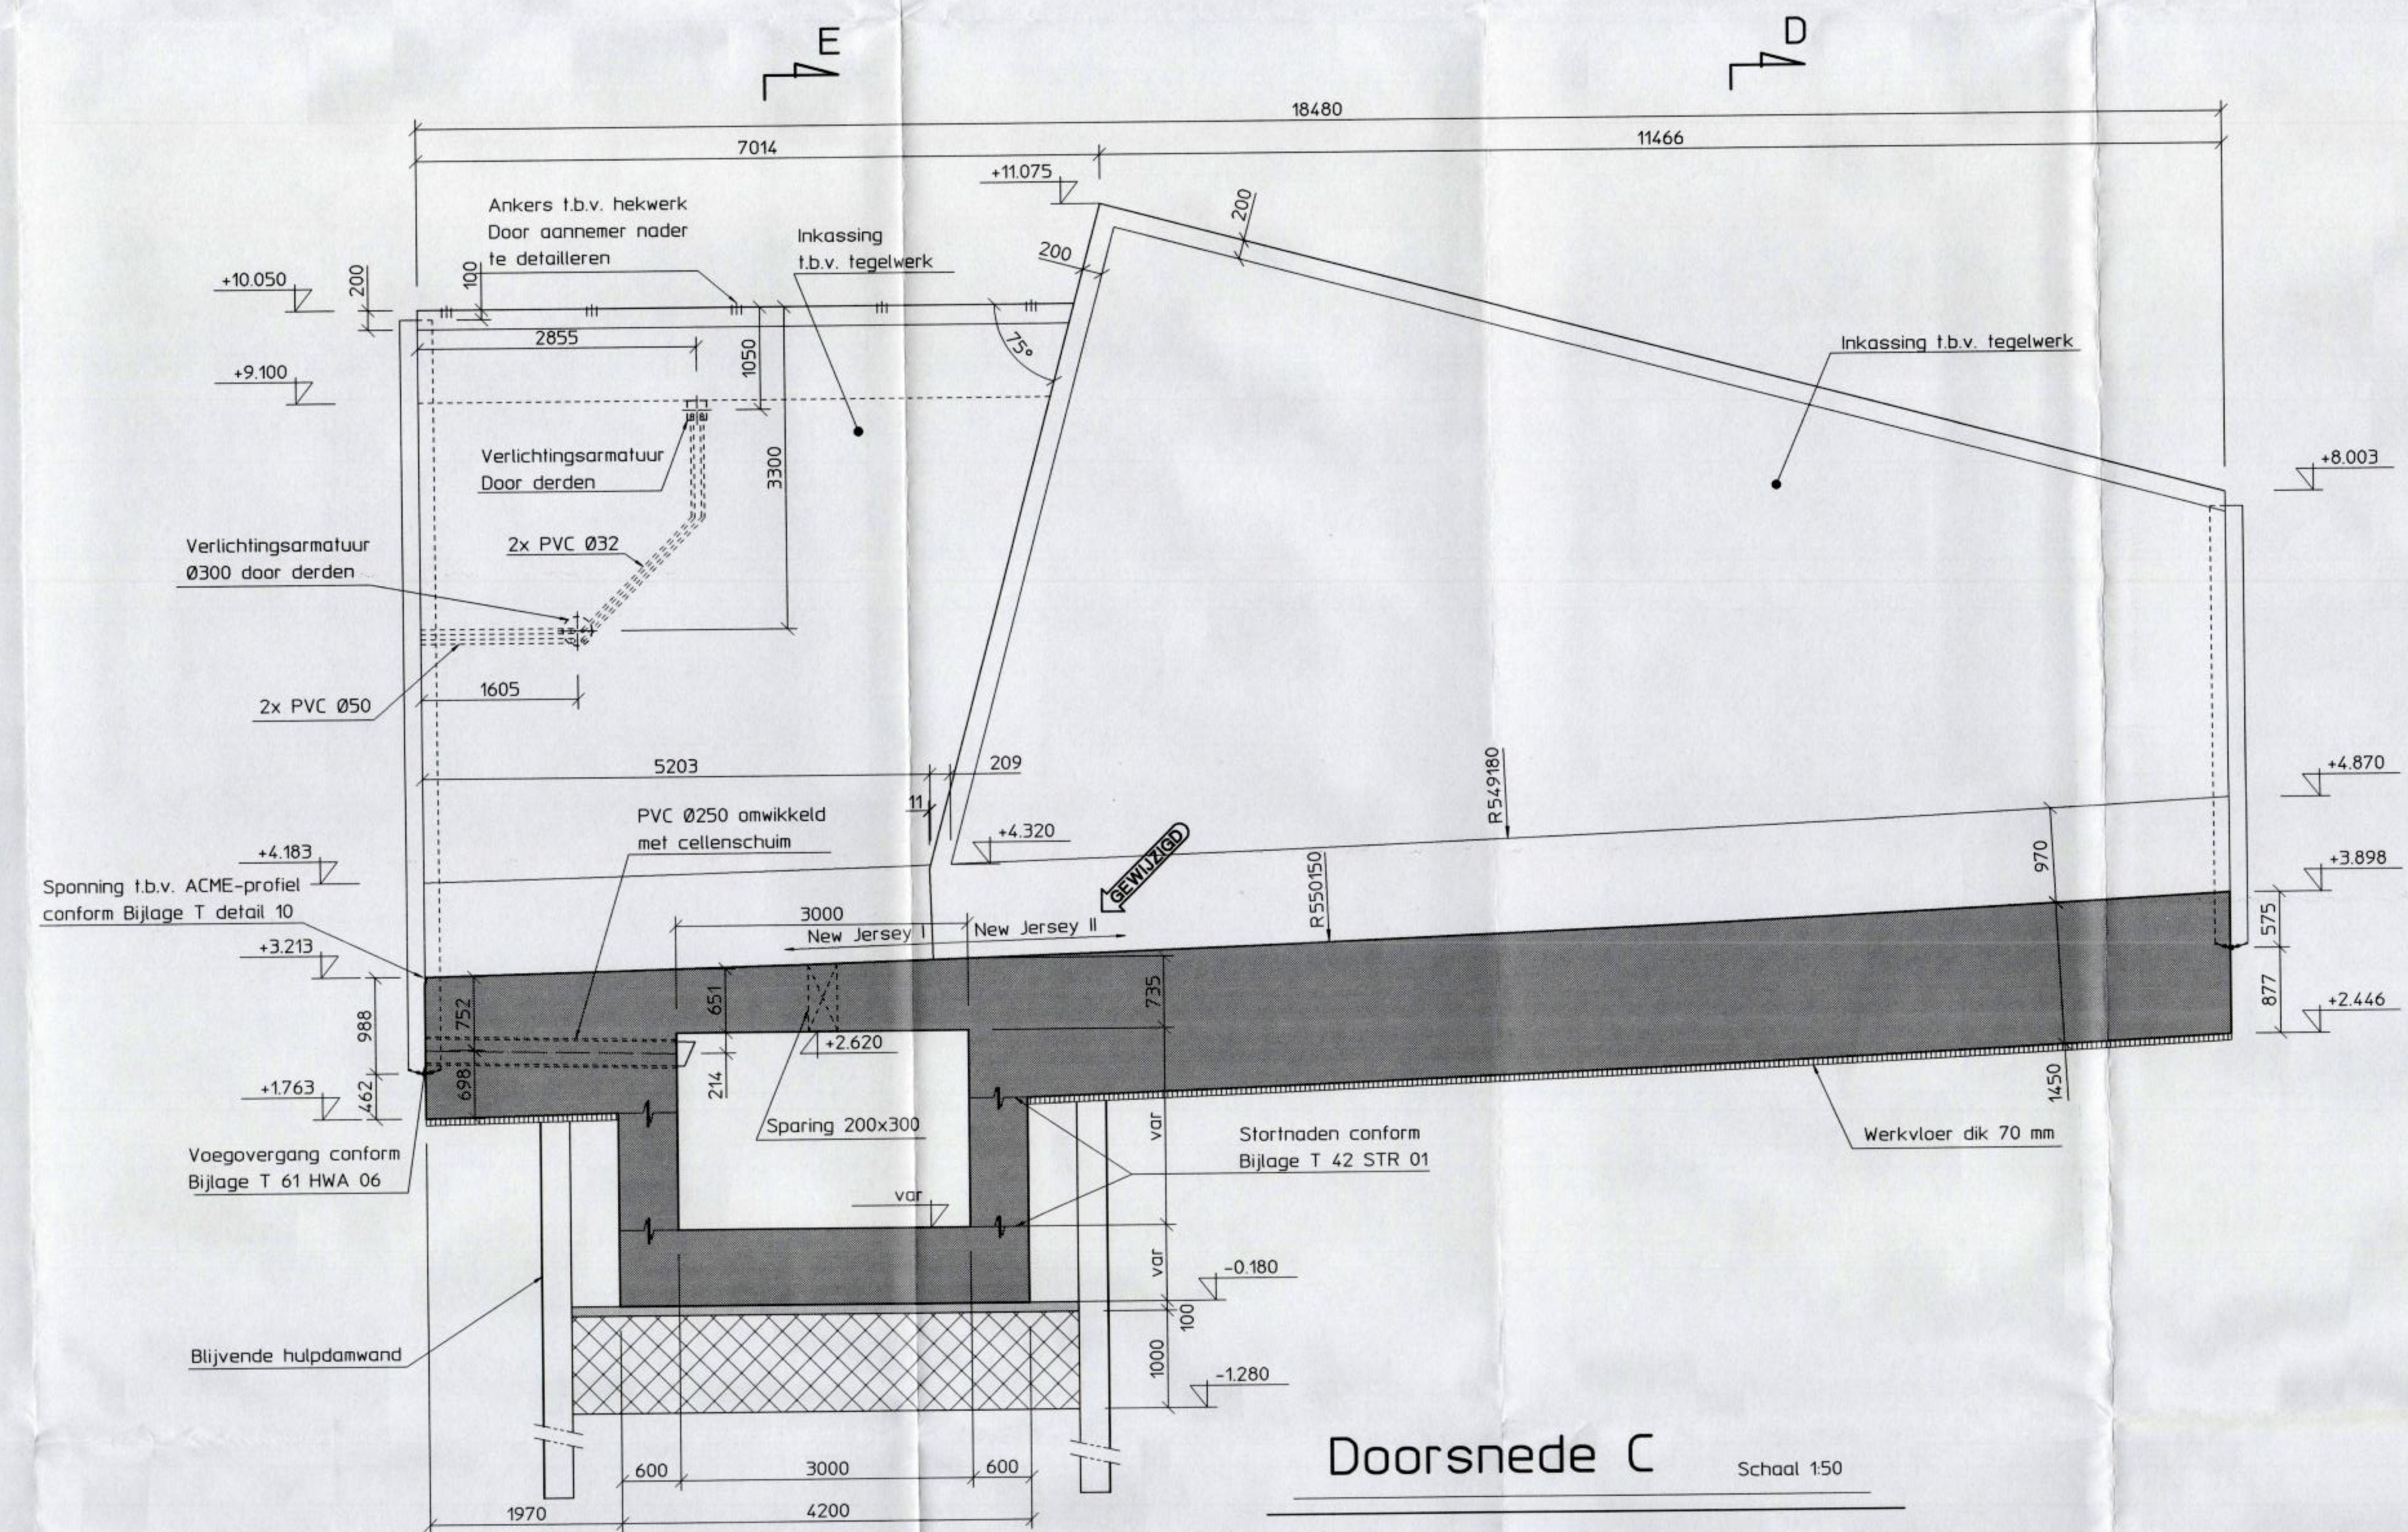
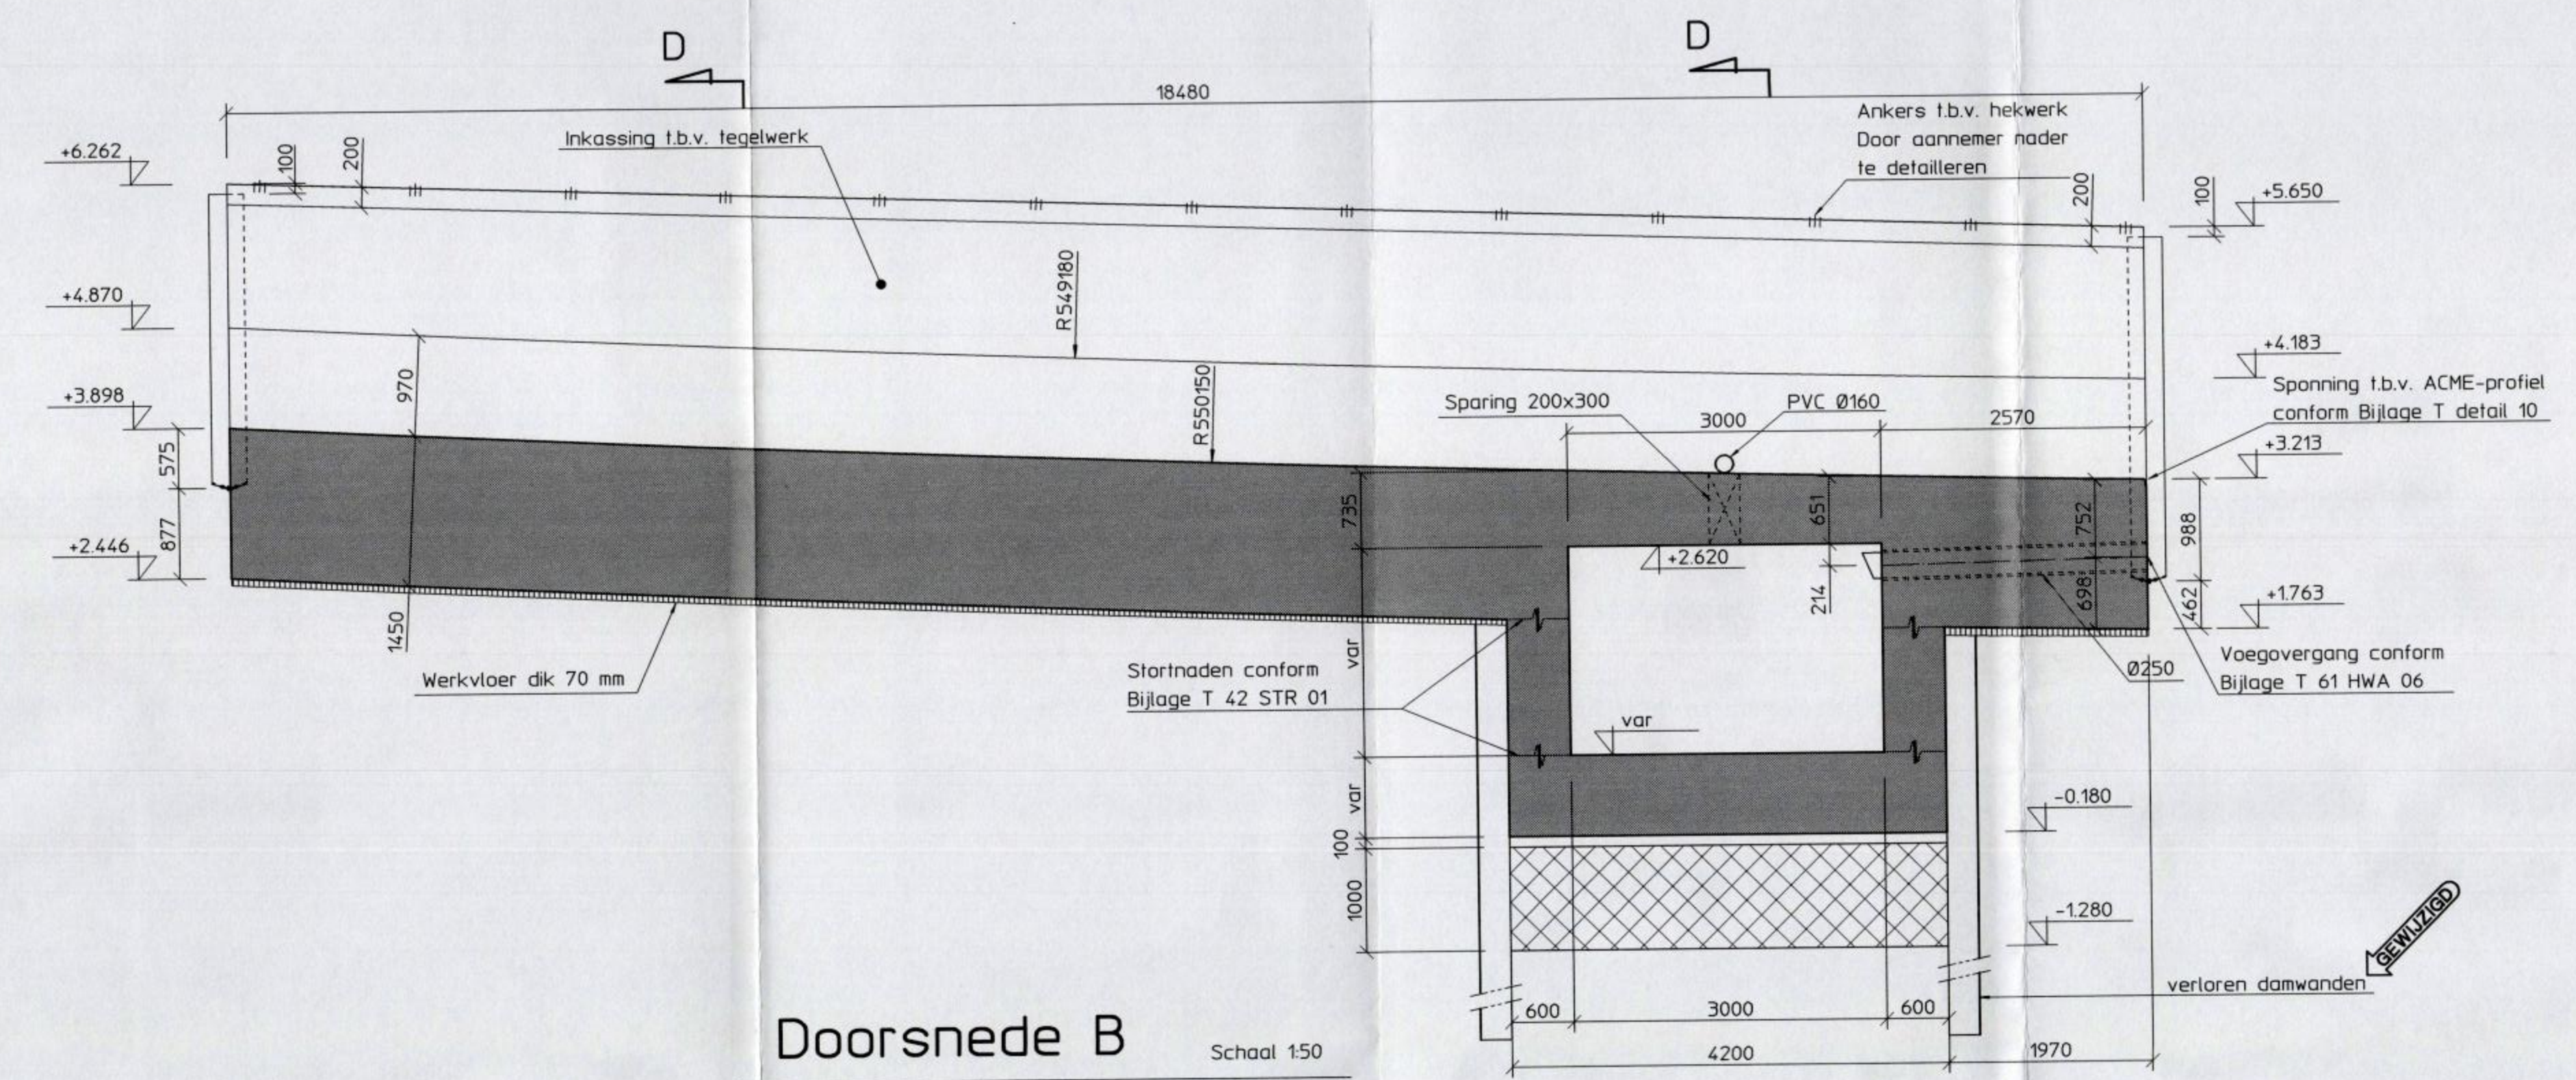
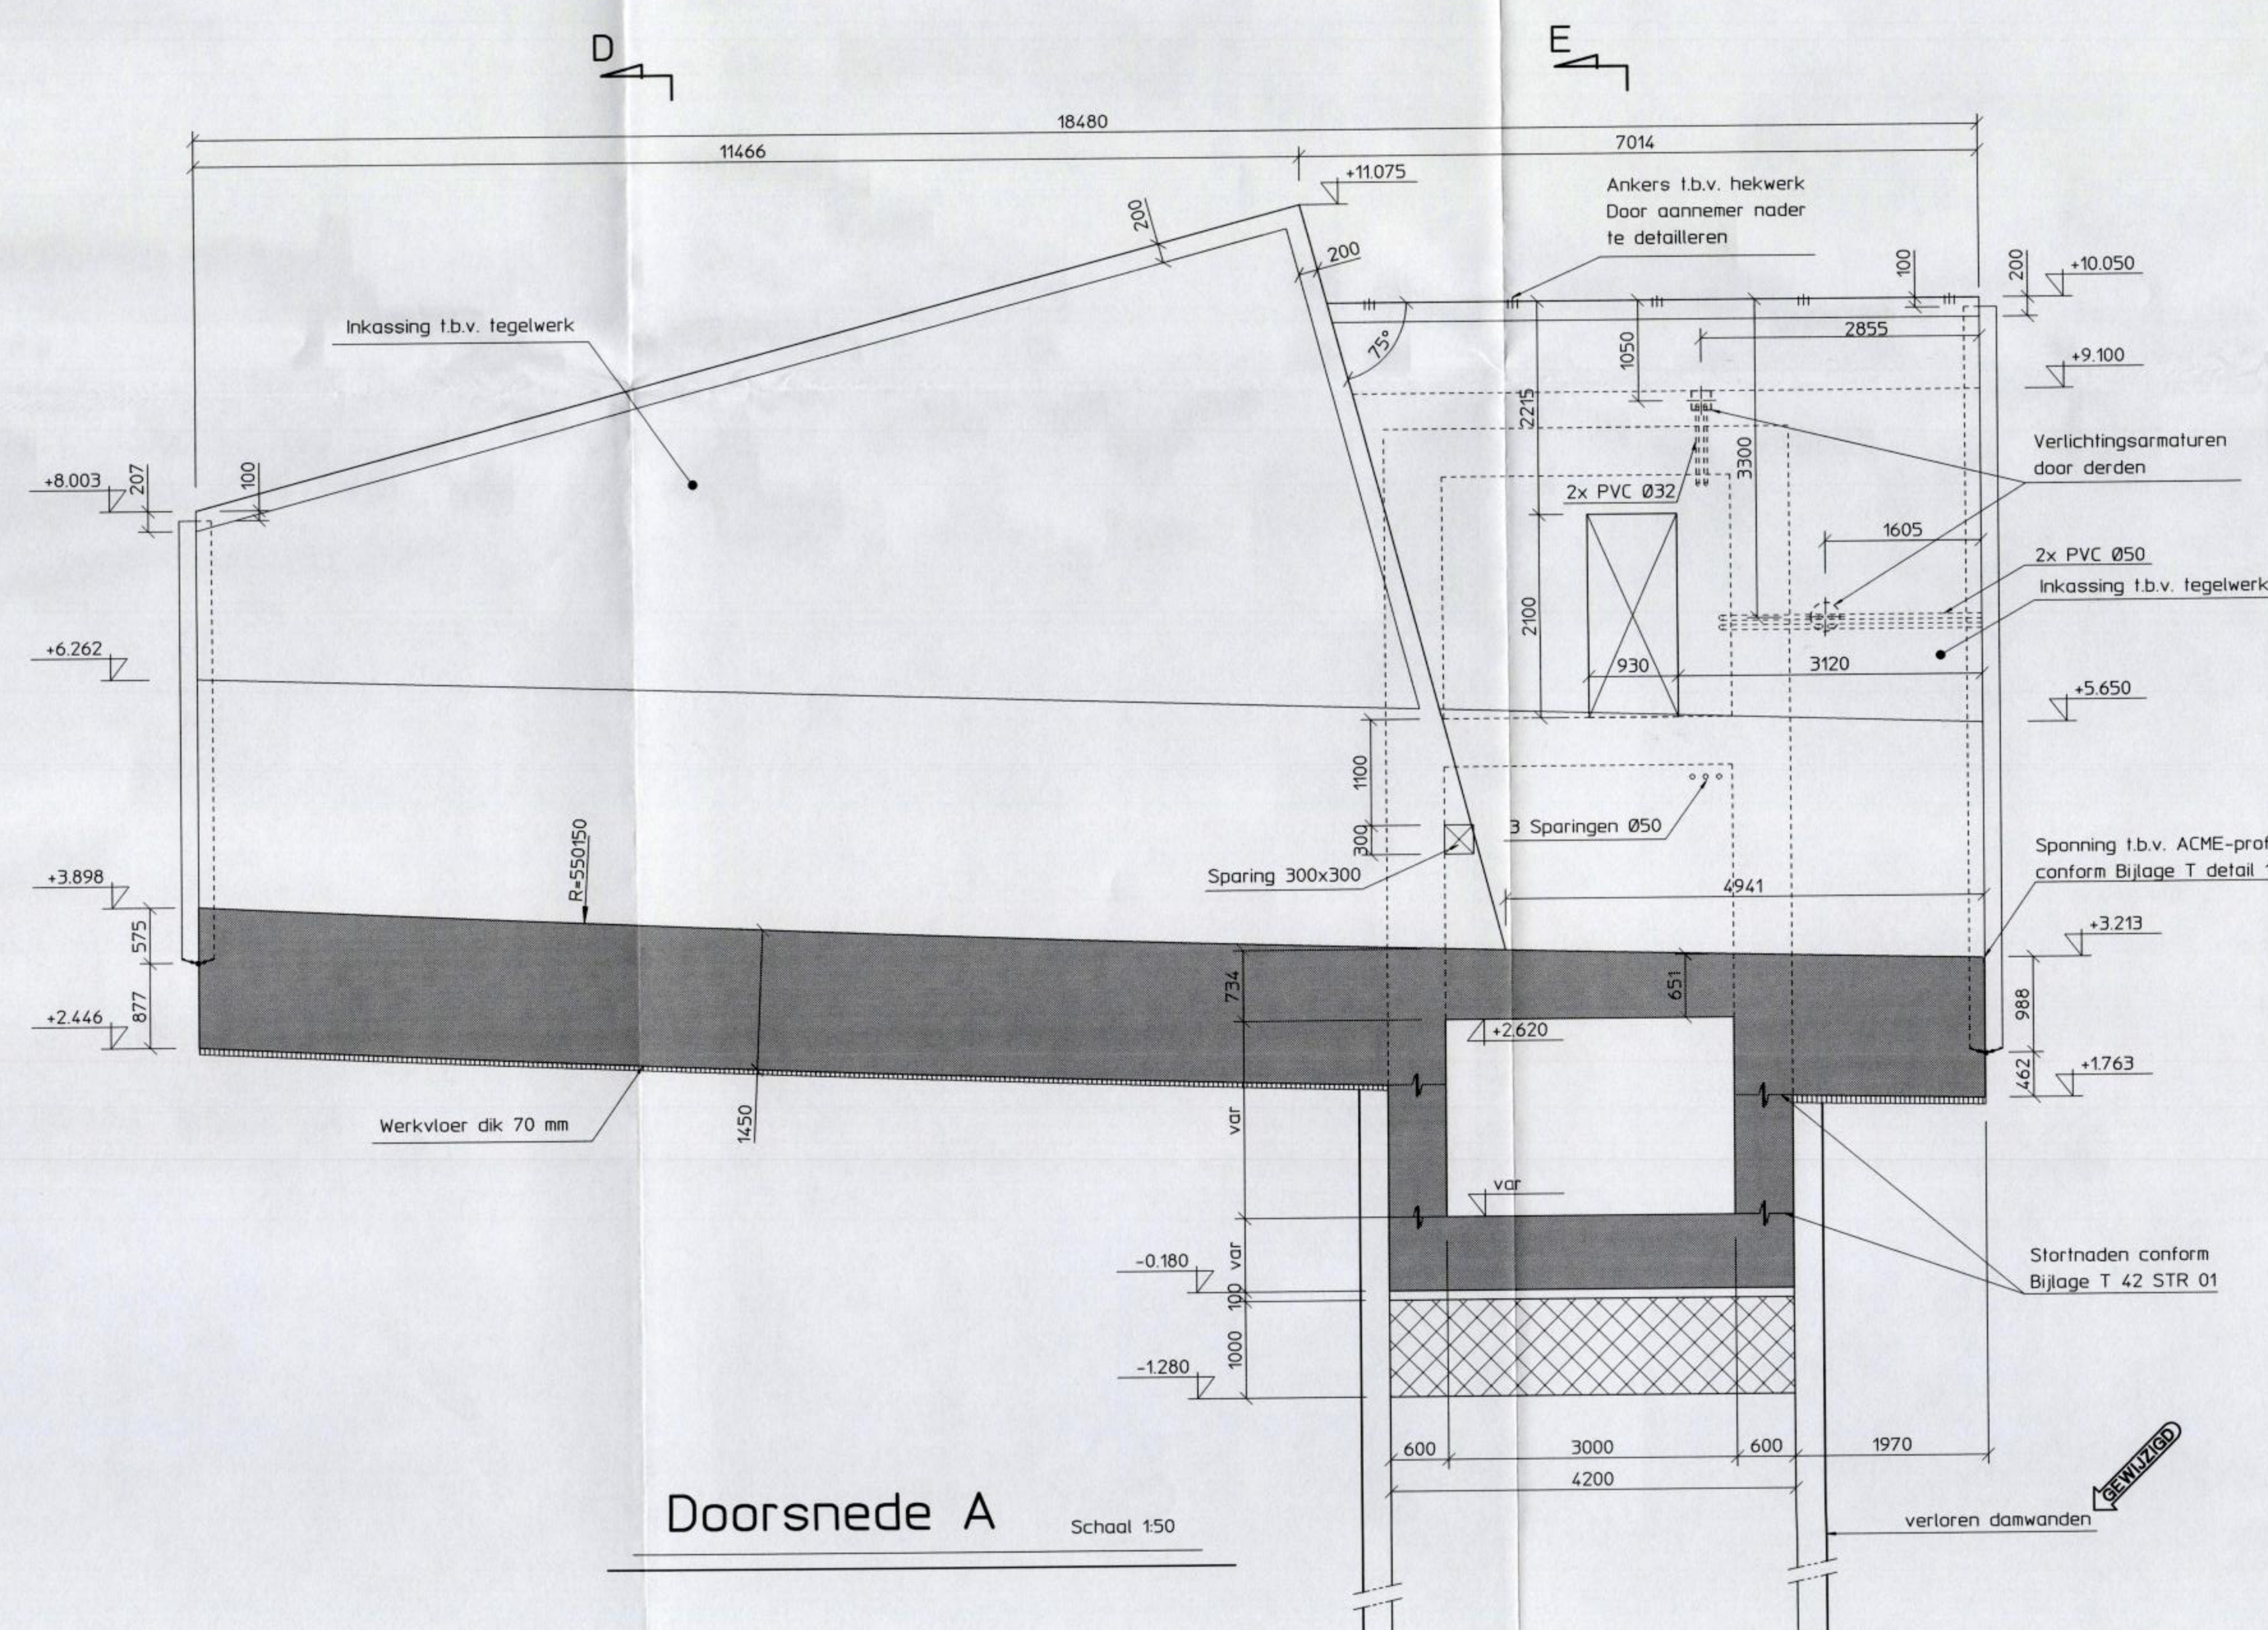


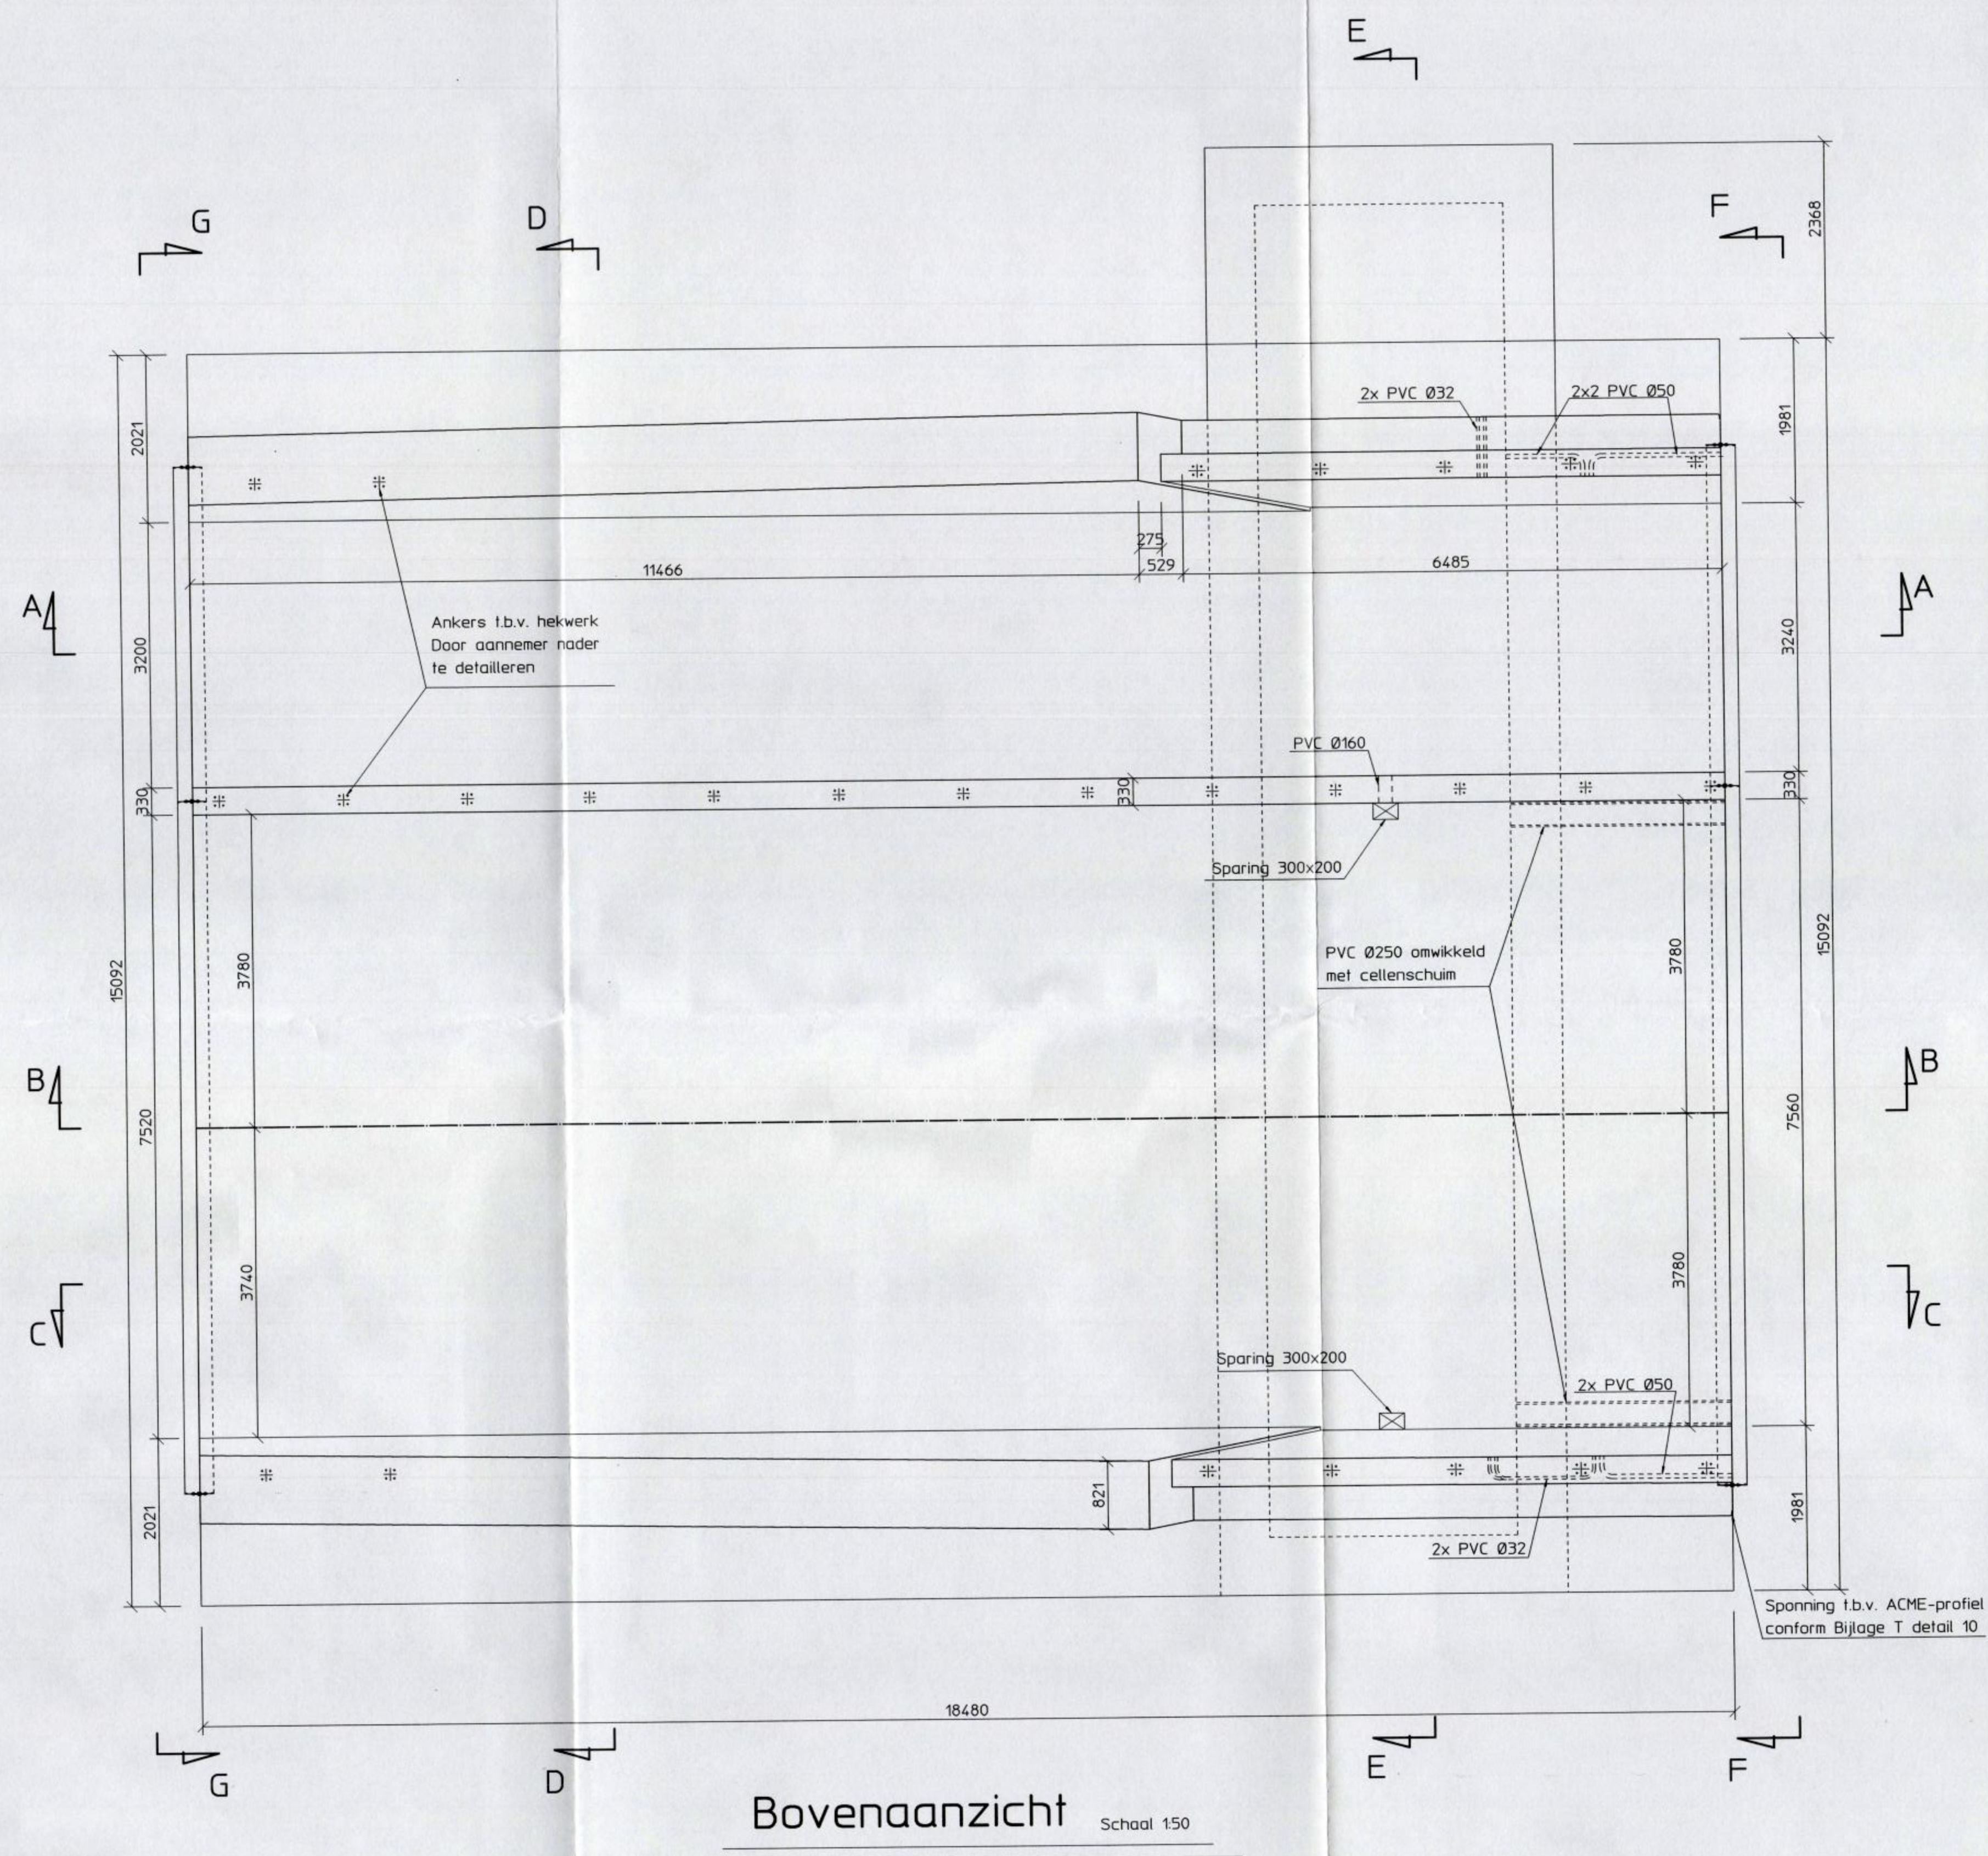

- maatvoering in mm
 - hoogtemaatvoering in m t.o.v. N.A.P.
 - voor doorsneden D t/m I zie blad 3362706 41 M

(Status: REVISE d.d. 17-12-1999 14:23:01)

naam	par	datum	Maatvoering maat 4
getekend H.W. Griffler		17-12-99	Blad 1
projectant C.F. Vink			
projectnr 3362706	versie 1.0		
besteknr V408K09450			
functiokaad AD			
schied zie tek			
420	123	11.720	713
3362706	40	M	

NS Railinfrabeheer Regio Zuid
 Gilze Rijen
 Onderdoorgang Europalaan

VA CT PG 82
 Postbus 2893
 3000 GK Utrecht
 Telefoon 030 - 235 89 58
 Telefax 030 - 235 72 29

Holland Railconsult

postinfo: hnl0_dwg/c1/ct123kso11720/pa3362706/ac14140_a H.W. Griffler P CT A85G T 1-Mar-1999 12:23:12