




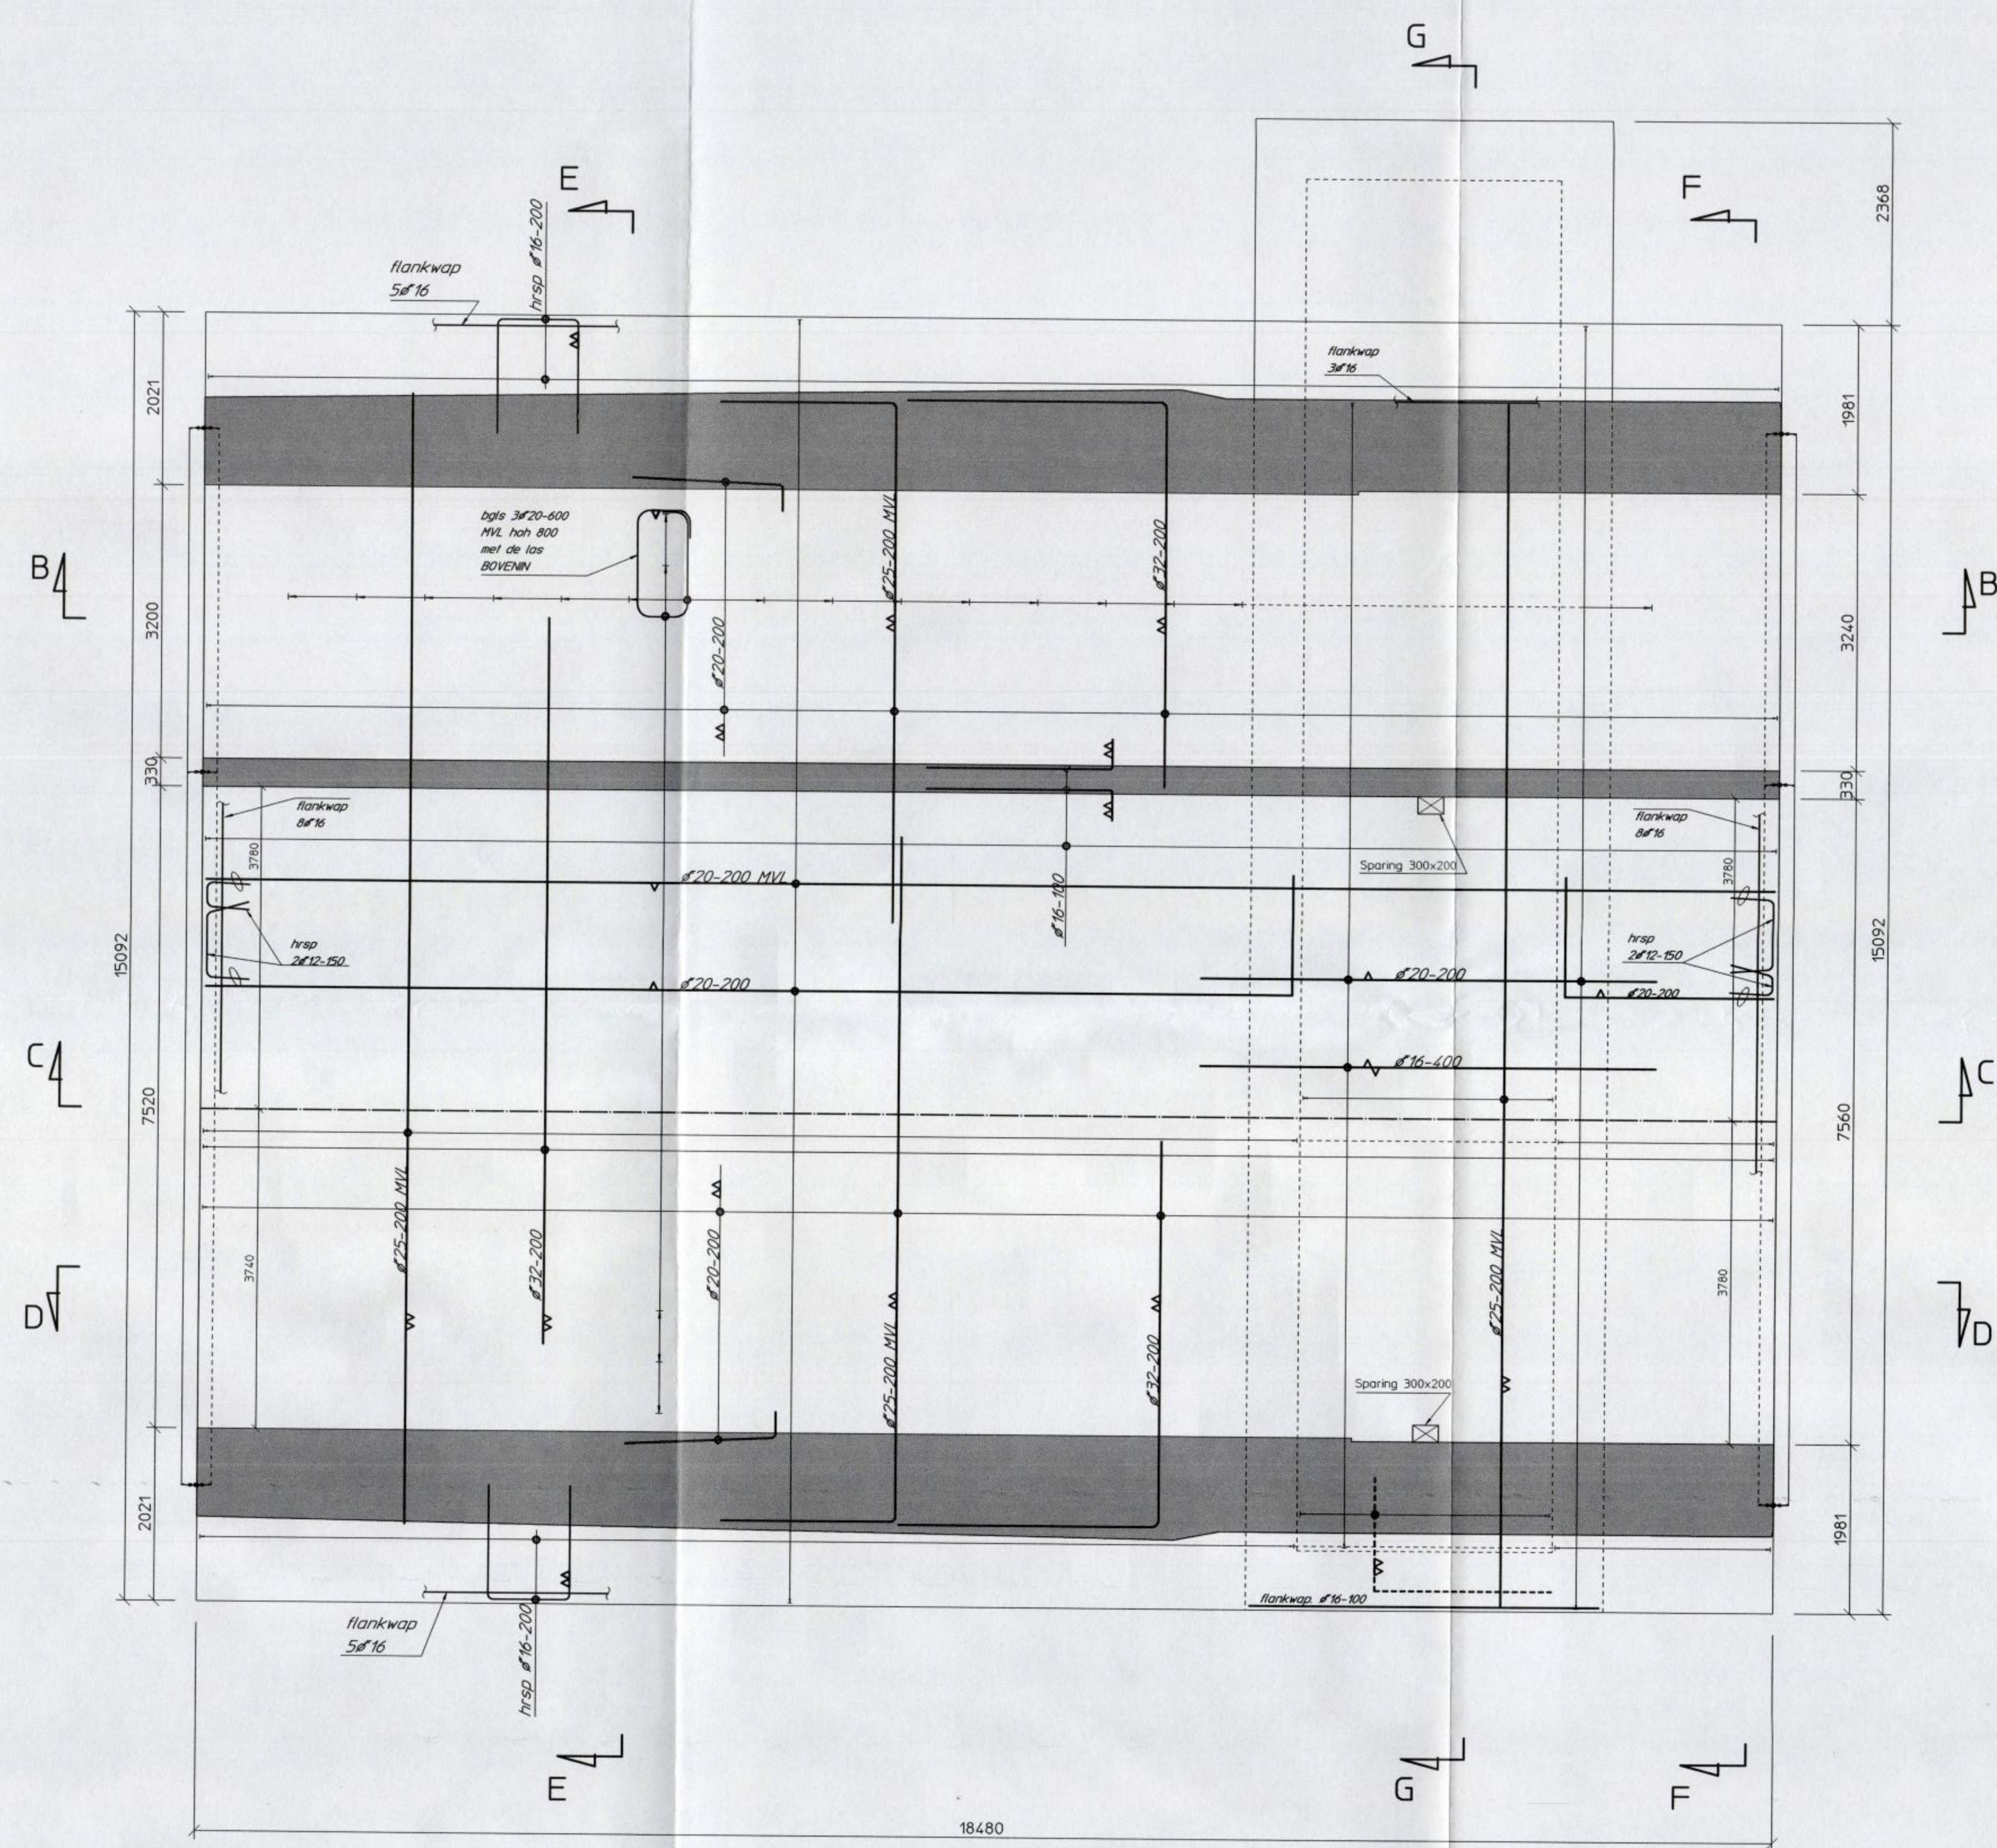


Doorsnede A-A Schaal 150

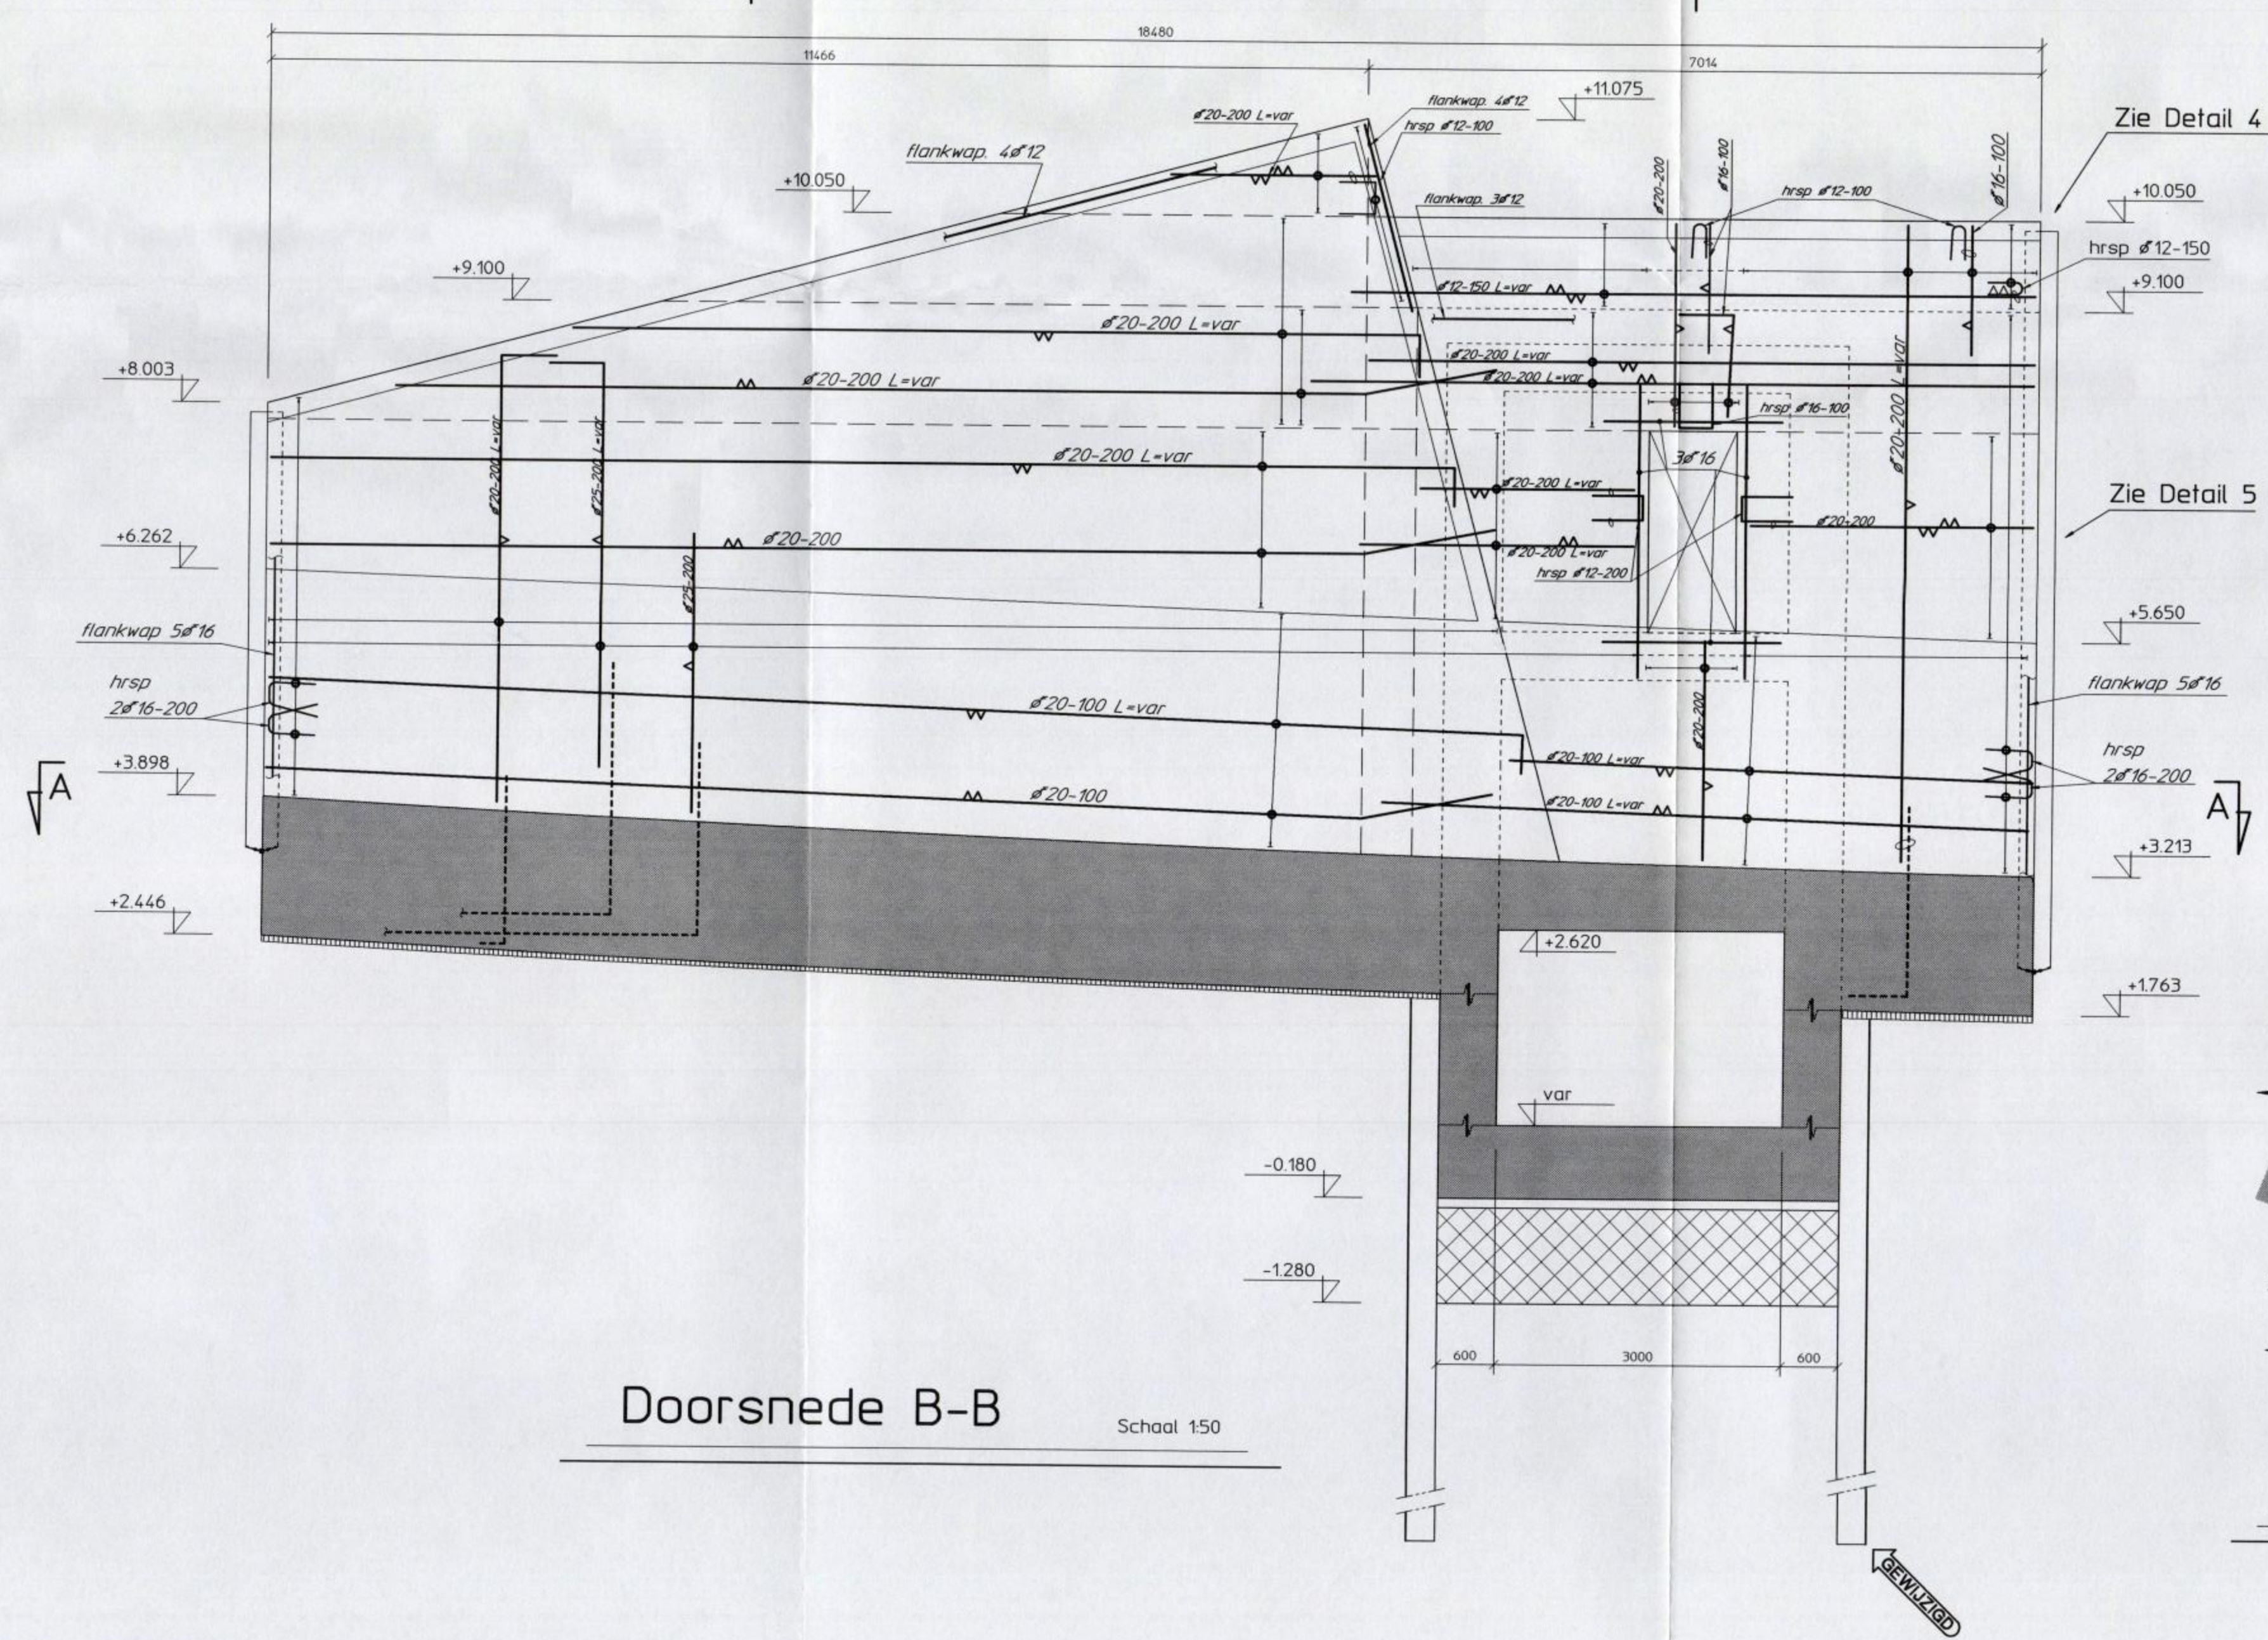


Doorsnede B-B Schaal 150

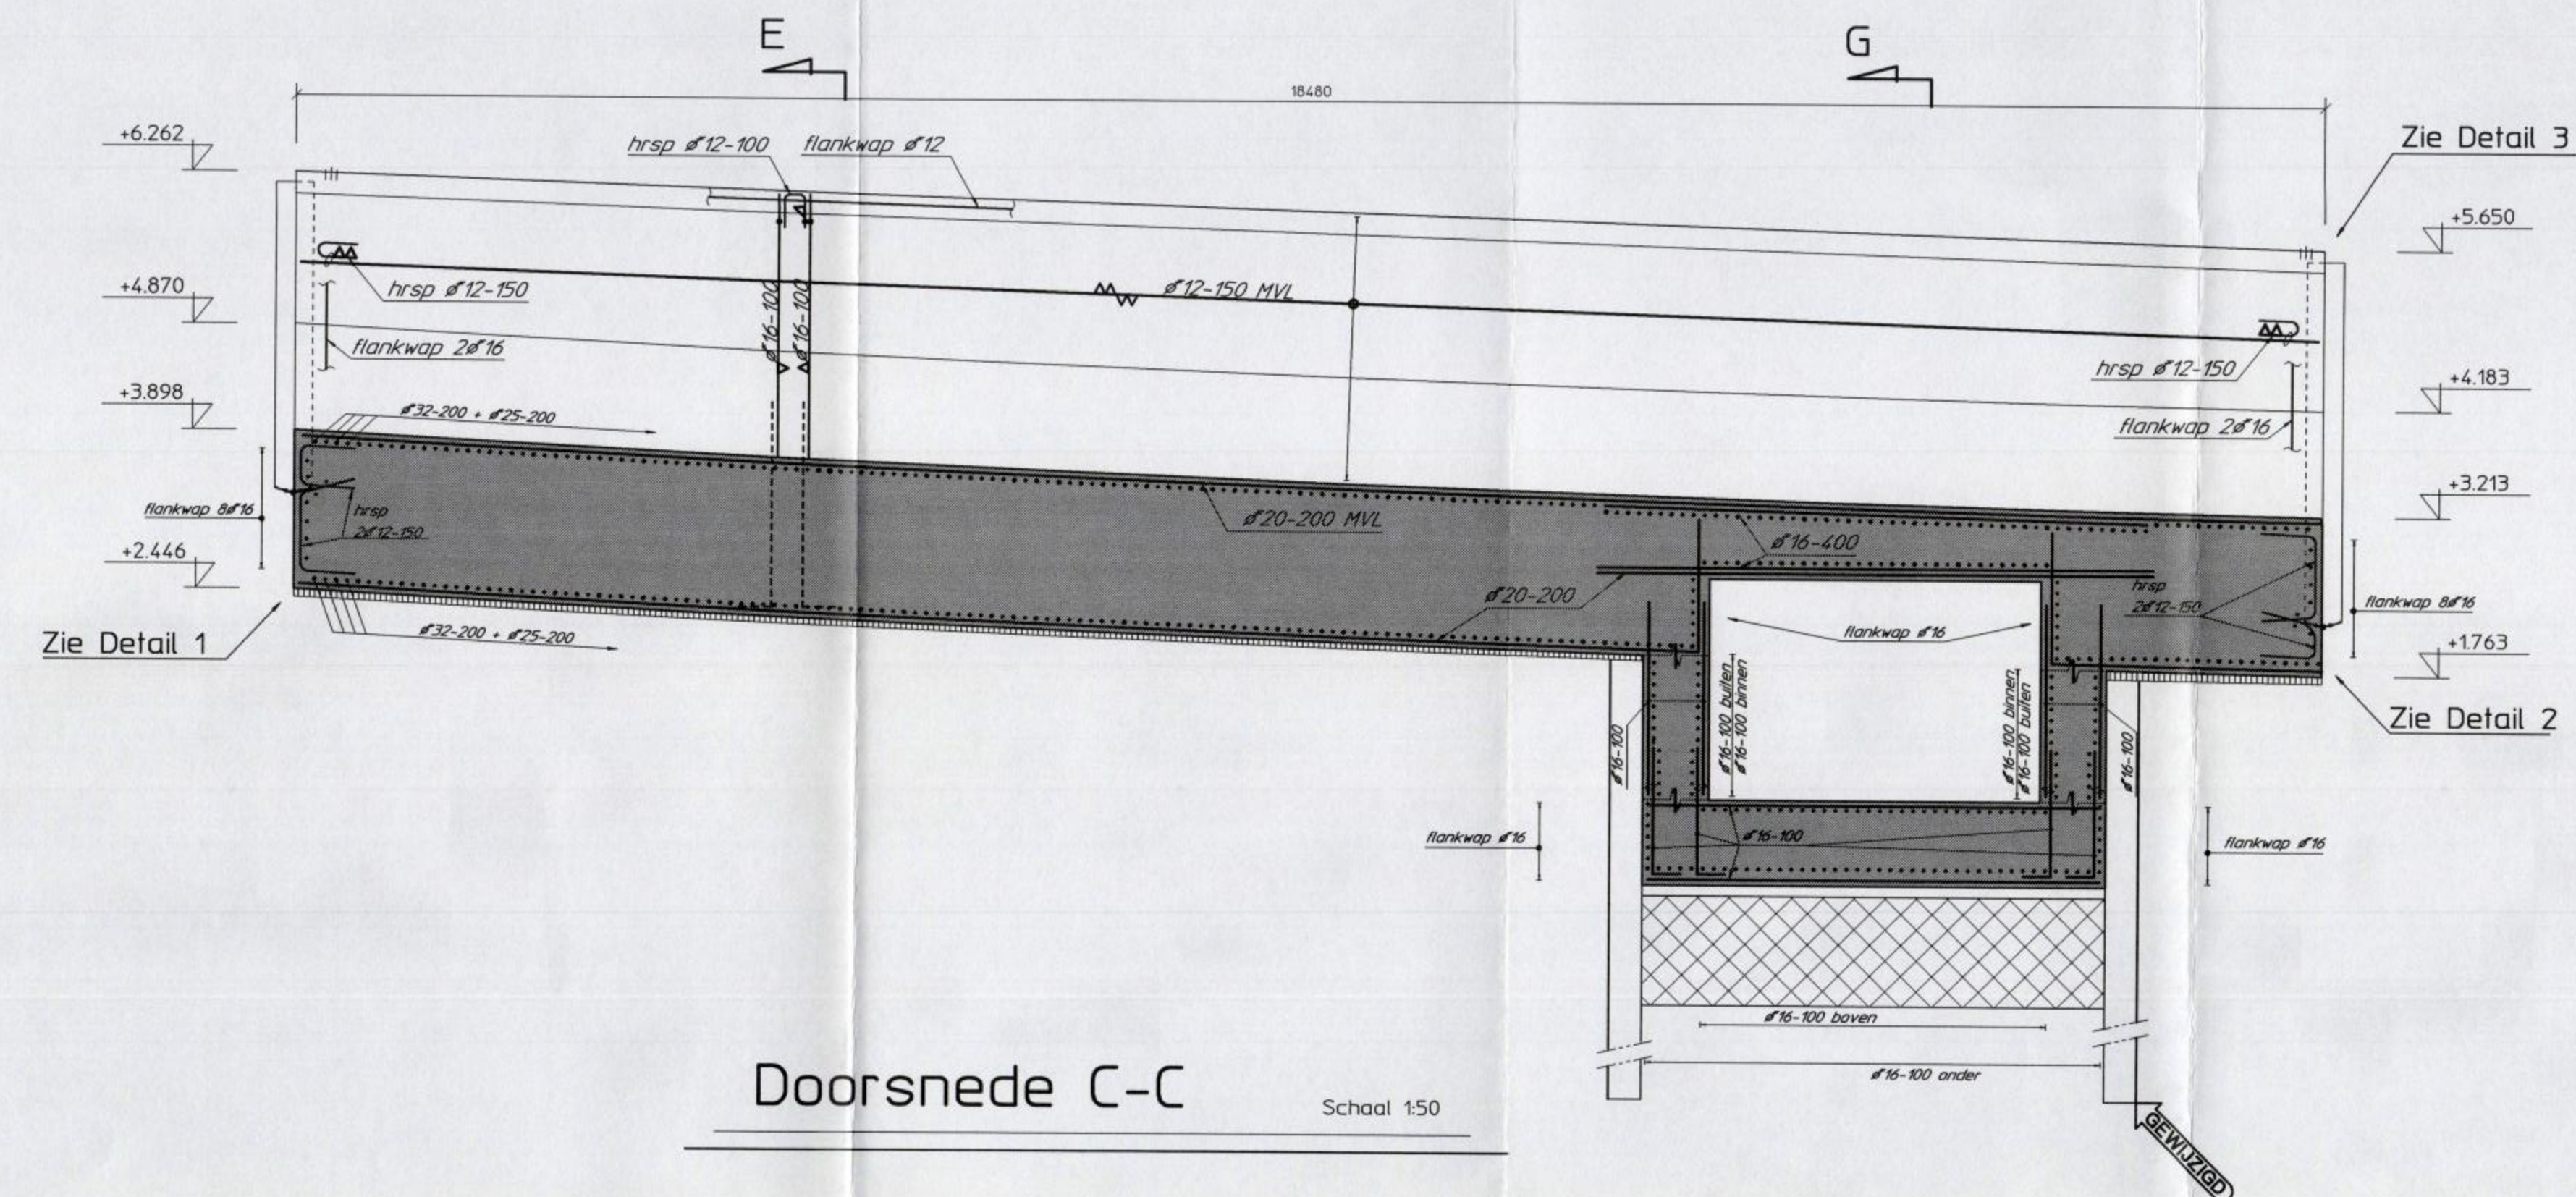


Doorsnede C-C Schaal 150

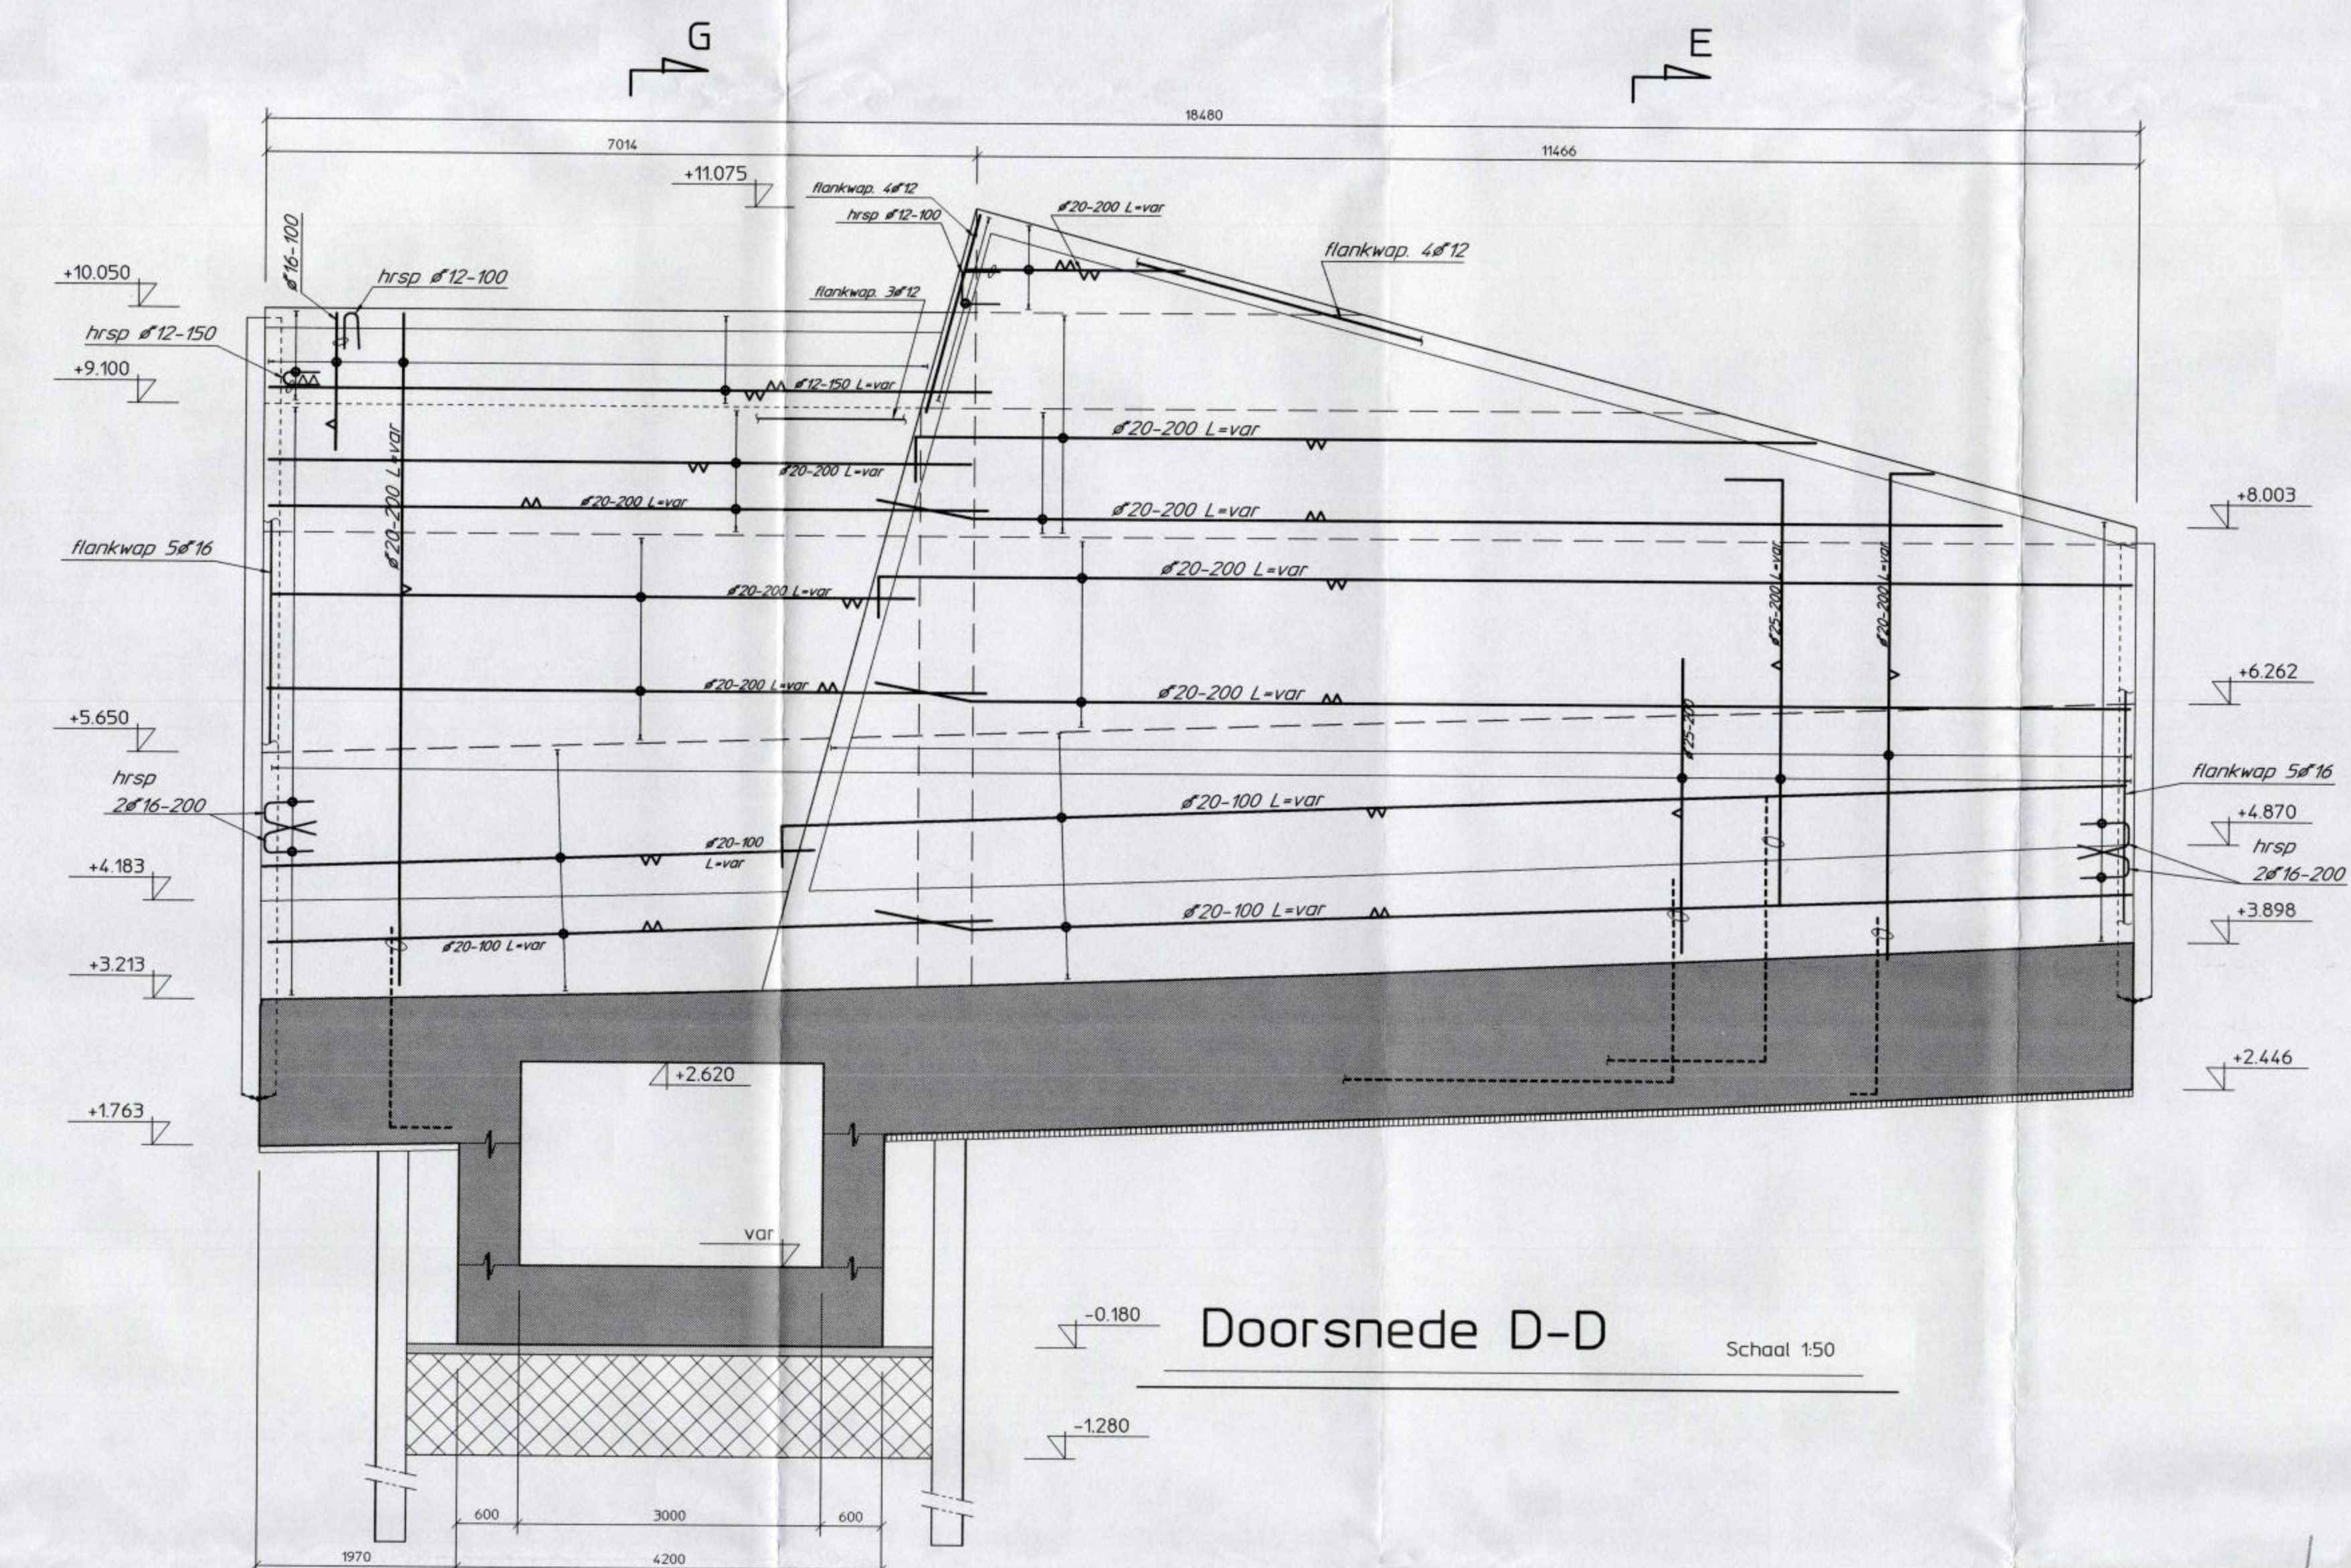


Doorsnede D-D Schaal 150

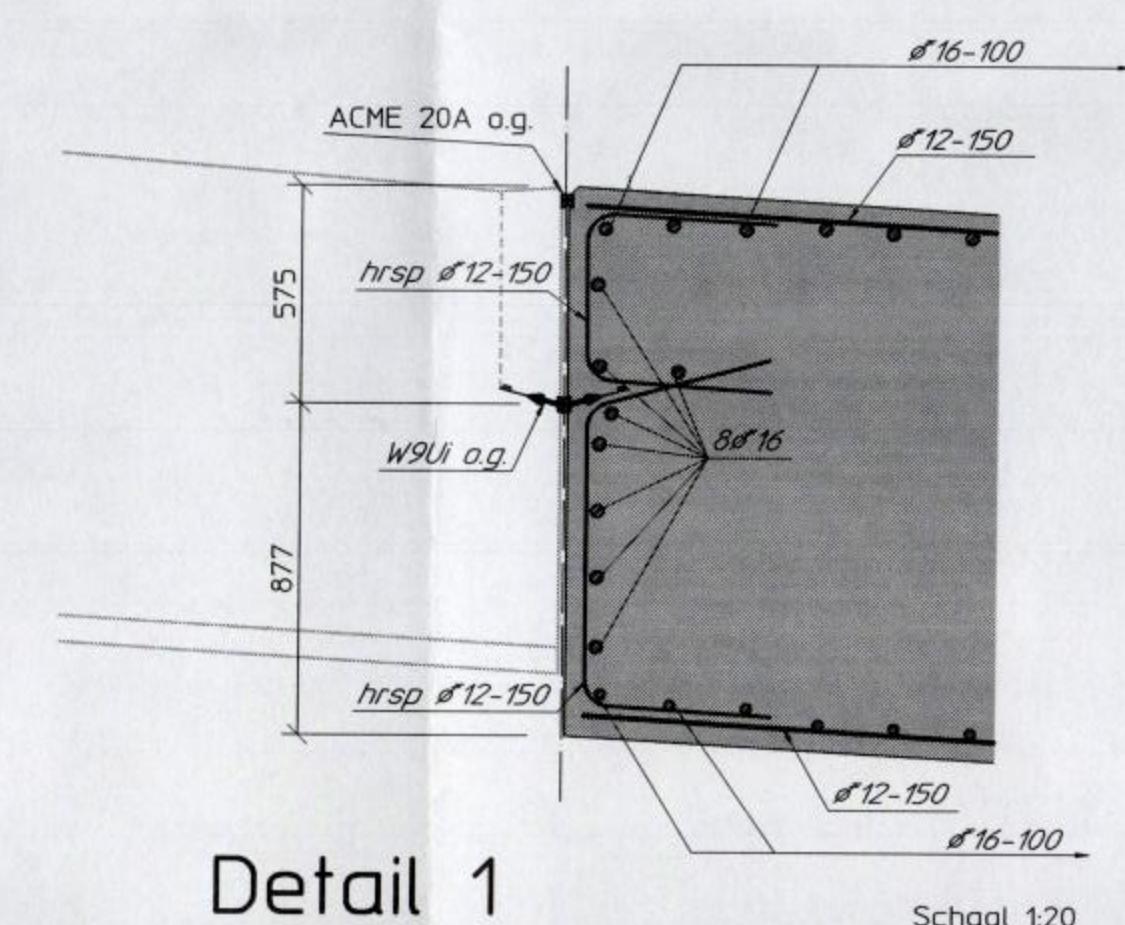


Detail 1 Schaal 120

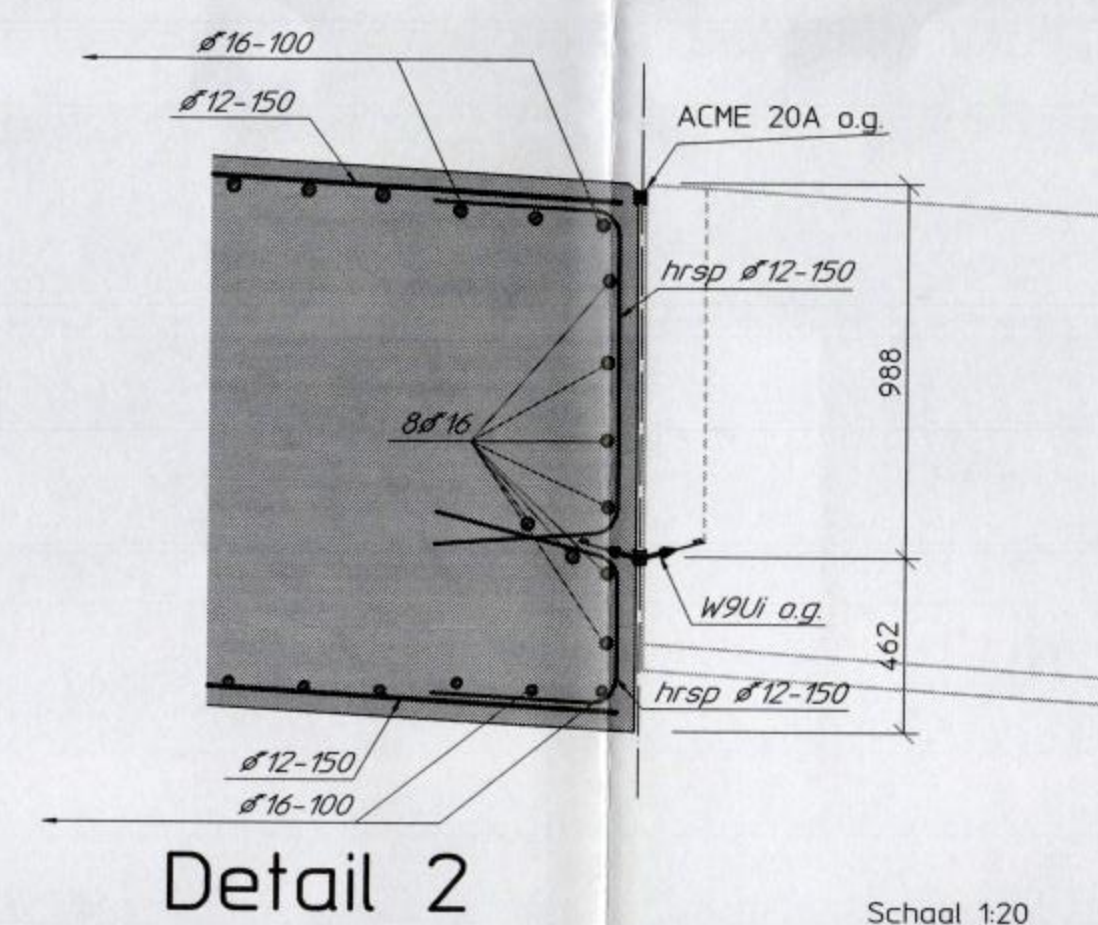


Detail 2 Schaal 120

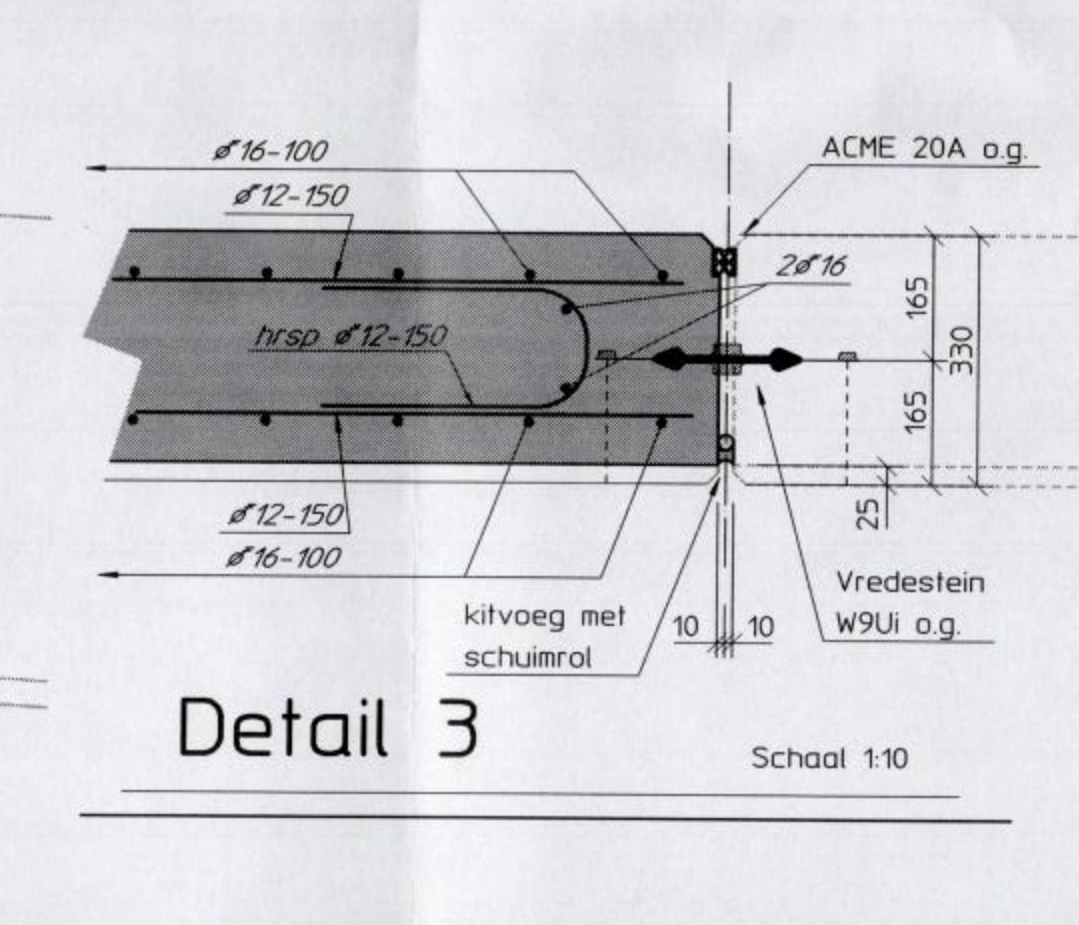


Detail 3 Schaal 110

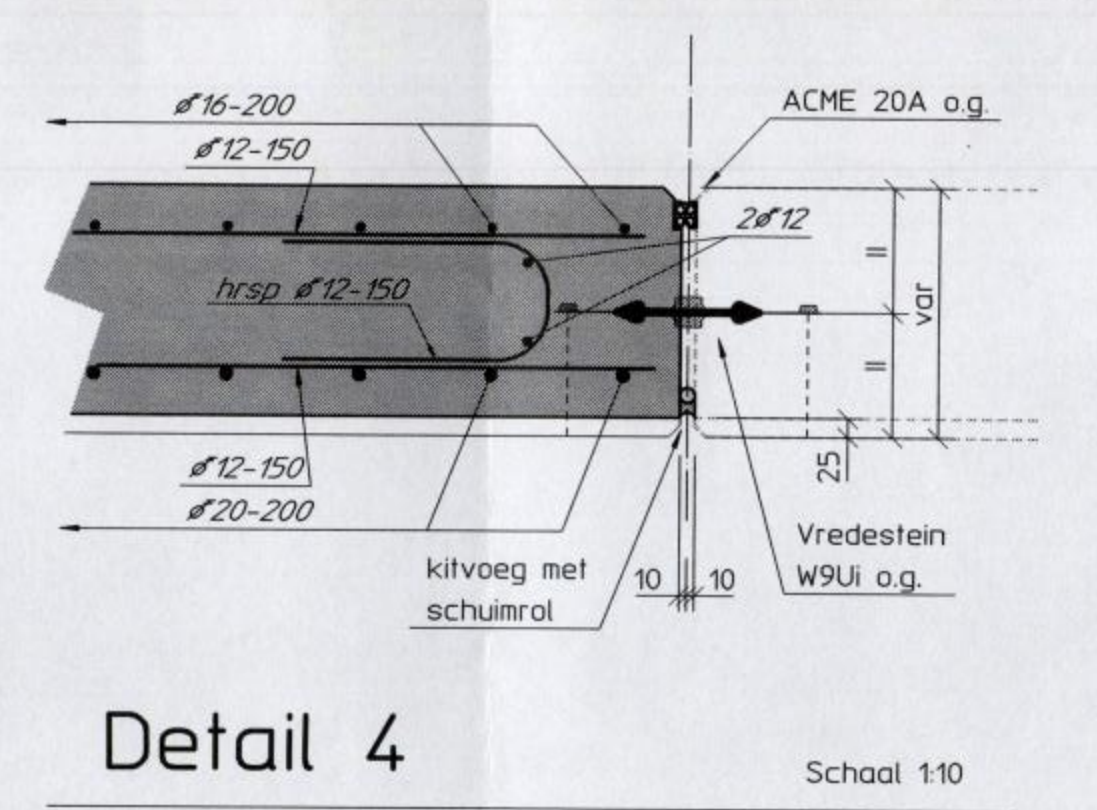

Detail 4 Schaal 110

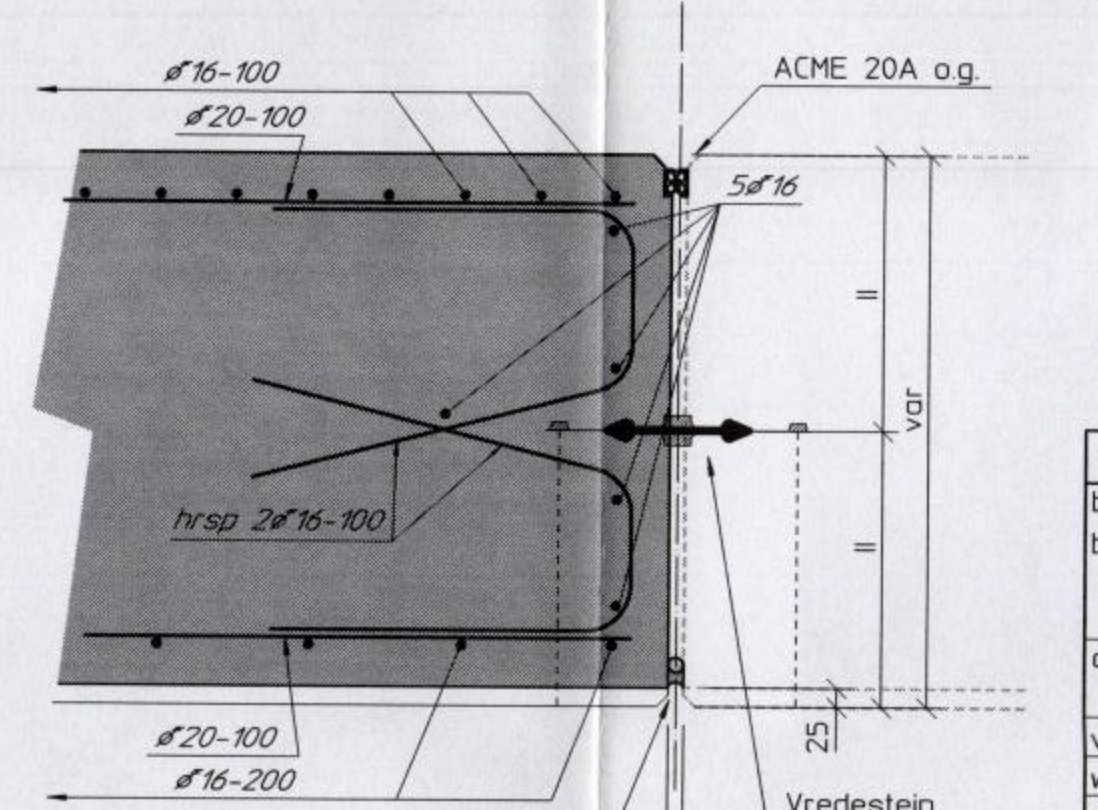

Detail 5 Schaal 110

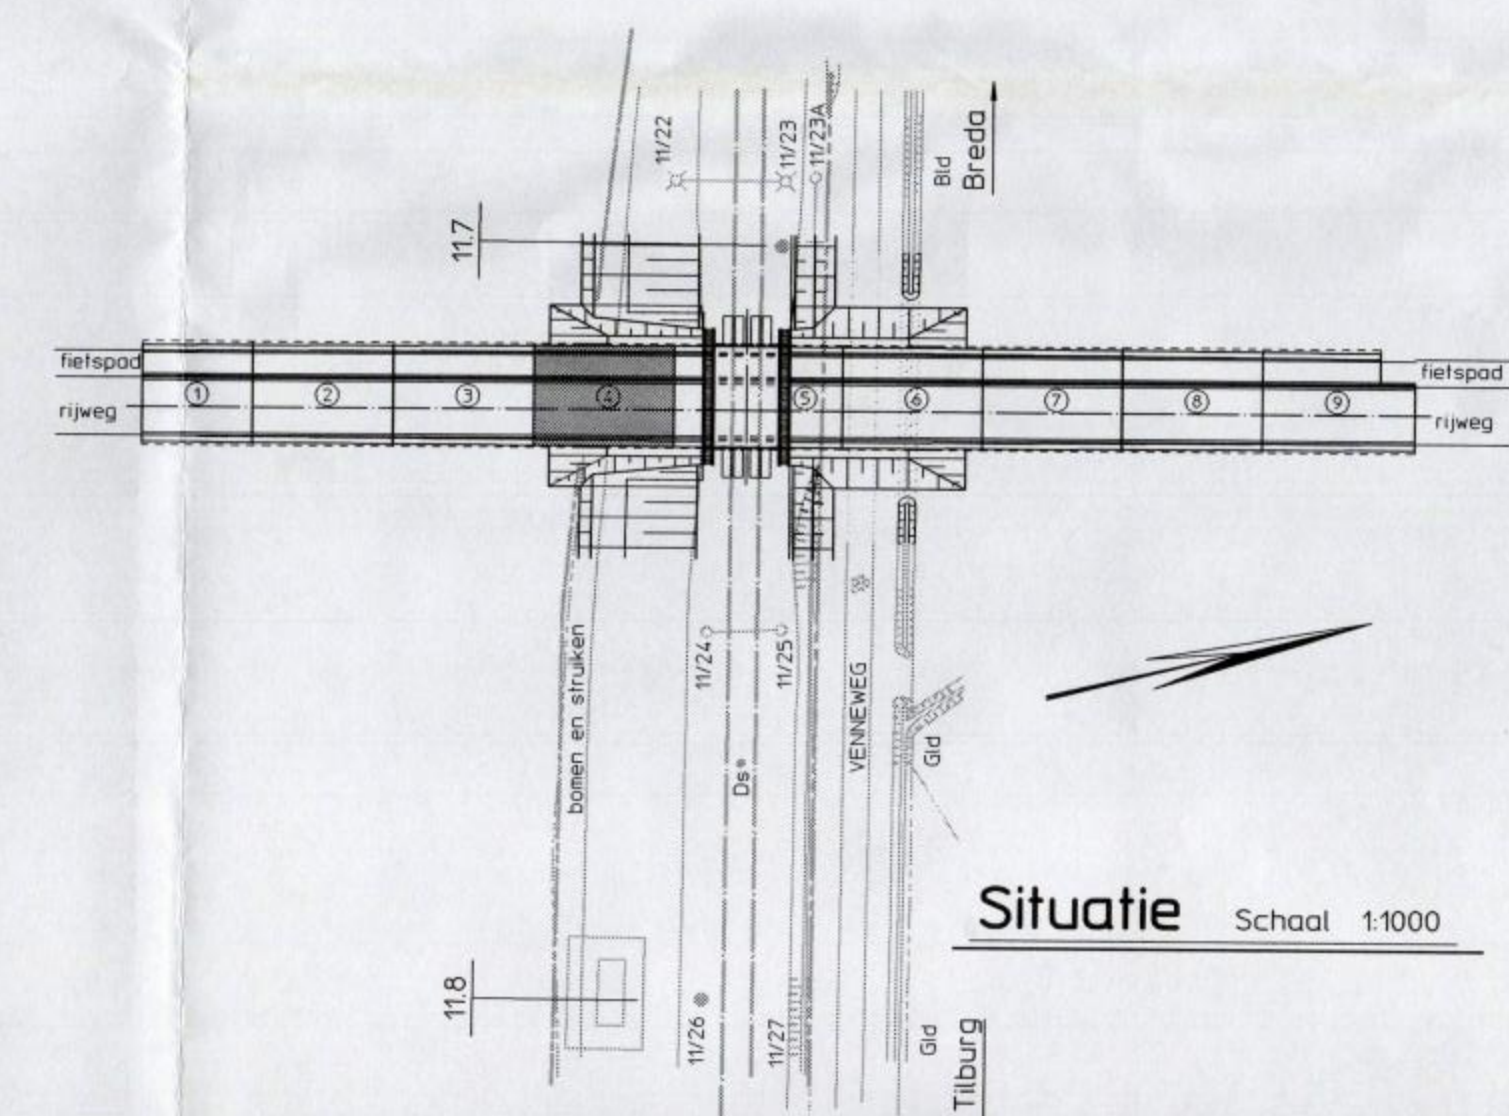

Situatie Schaal 11000

Legenda

- maatvoering in mm
- hoogtemaatvoering in m t.o.v. N.A.P.
- voor doorsneden E-E, F-F en G-G zie blad 3362706 41 W
- voor maatvoering zie tek. 3362706 40 M & 41 M
- MVL = met versprengende las
- var. = variabel

Status: REVISIE d.d. 17-12-1999 14:28:37

getekend	naam	par.	datum
T. Brand	T. Brand		17-12-99
projecteer	naam	par.	datum
C.F. Vink	C.F. Vink		
projectnr	naam	par.	datum
3362706	3362706		1.0
besteller	naam	par.	datum
V408K09450	V408K09450		
formaat	naam	par.	datum
A0	A0		
schaal	naam	par.	datum
zie tek.	zie tek.		

420 123 11.720 713 3362706 40 W

VA CT PG 82 Postbus 2855 3500 GR Utrecht Telefoon 030 - 275 89 58 Telefax 030 - 275 72 29

Holland Railconsult