




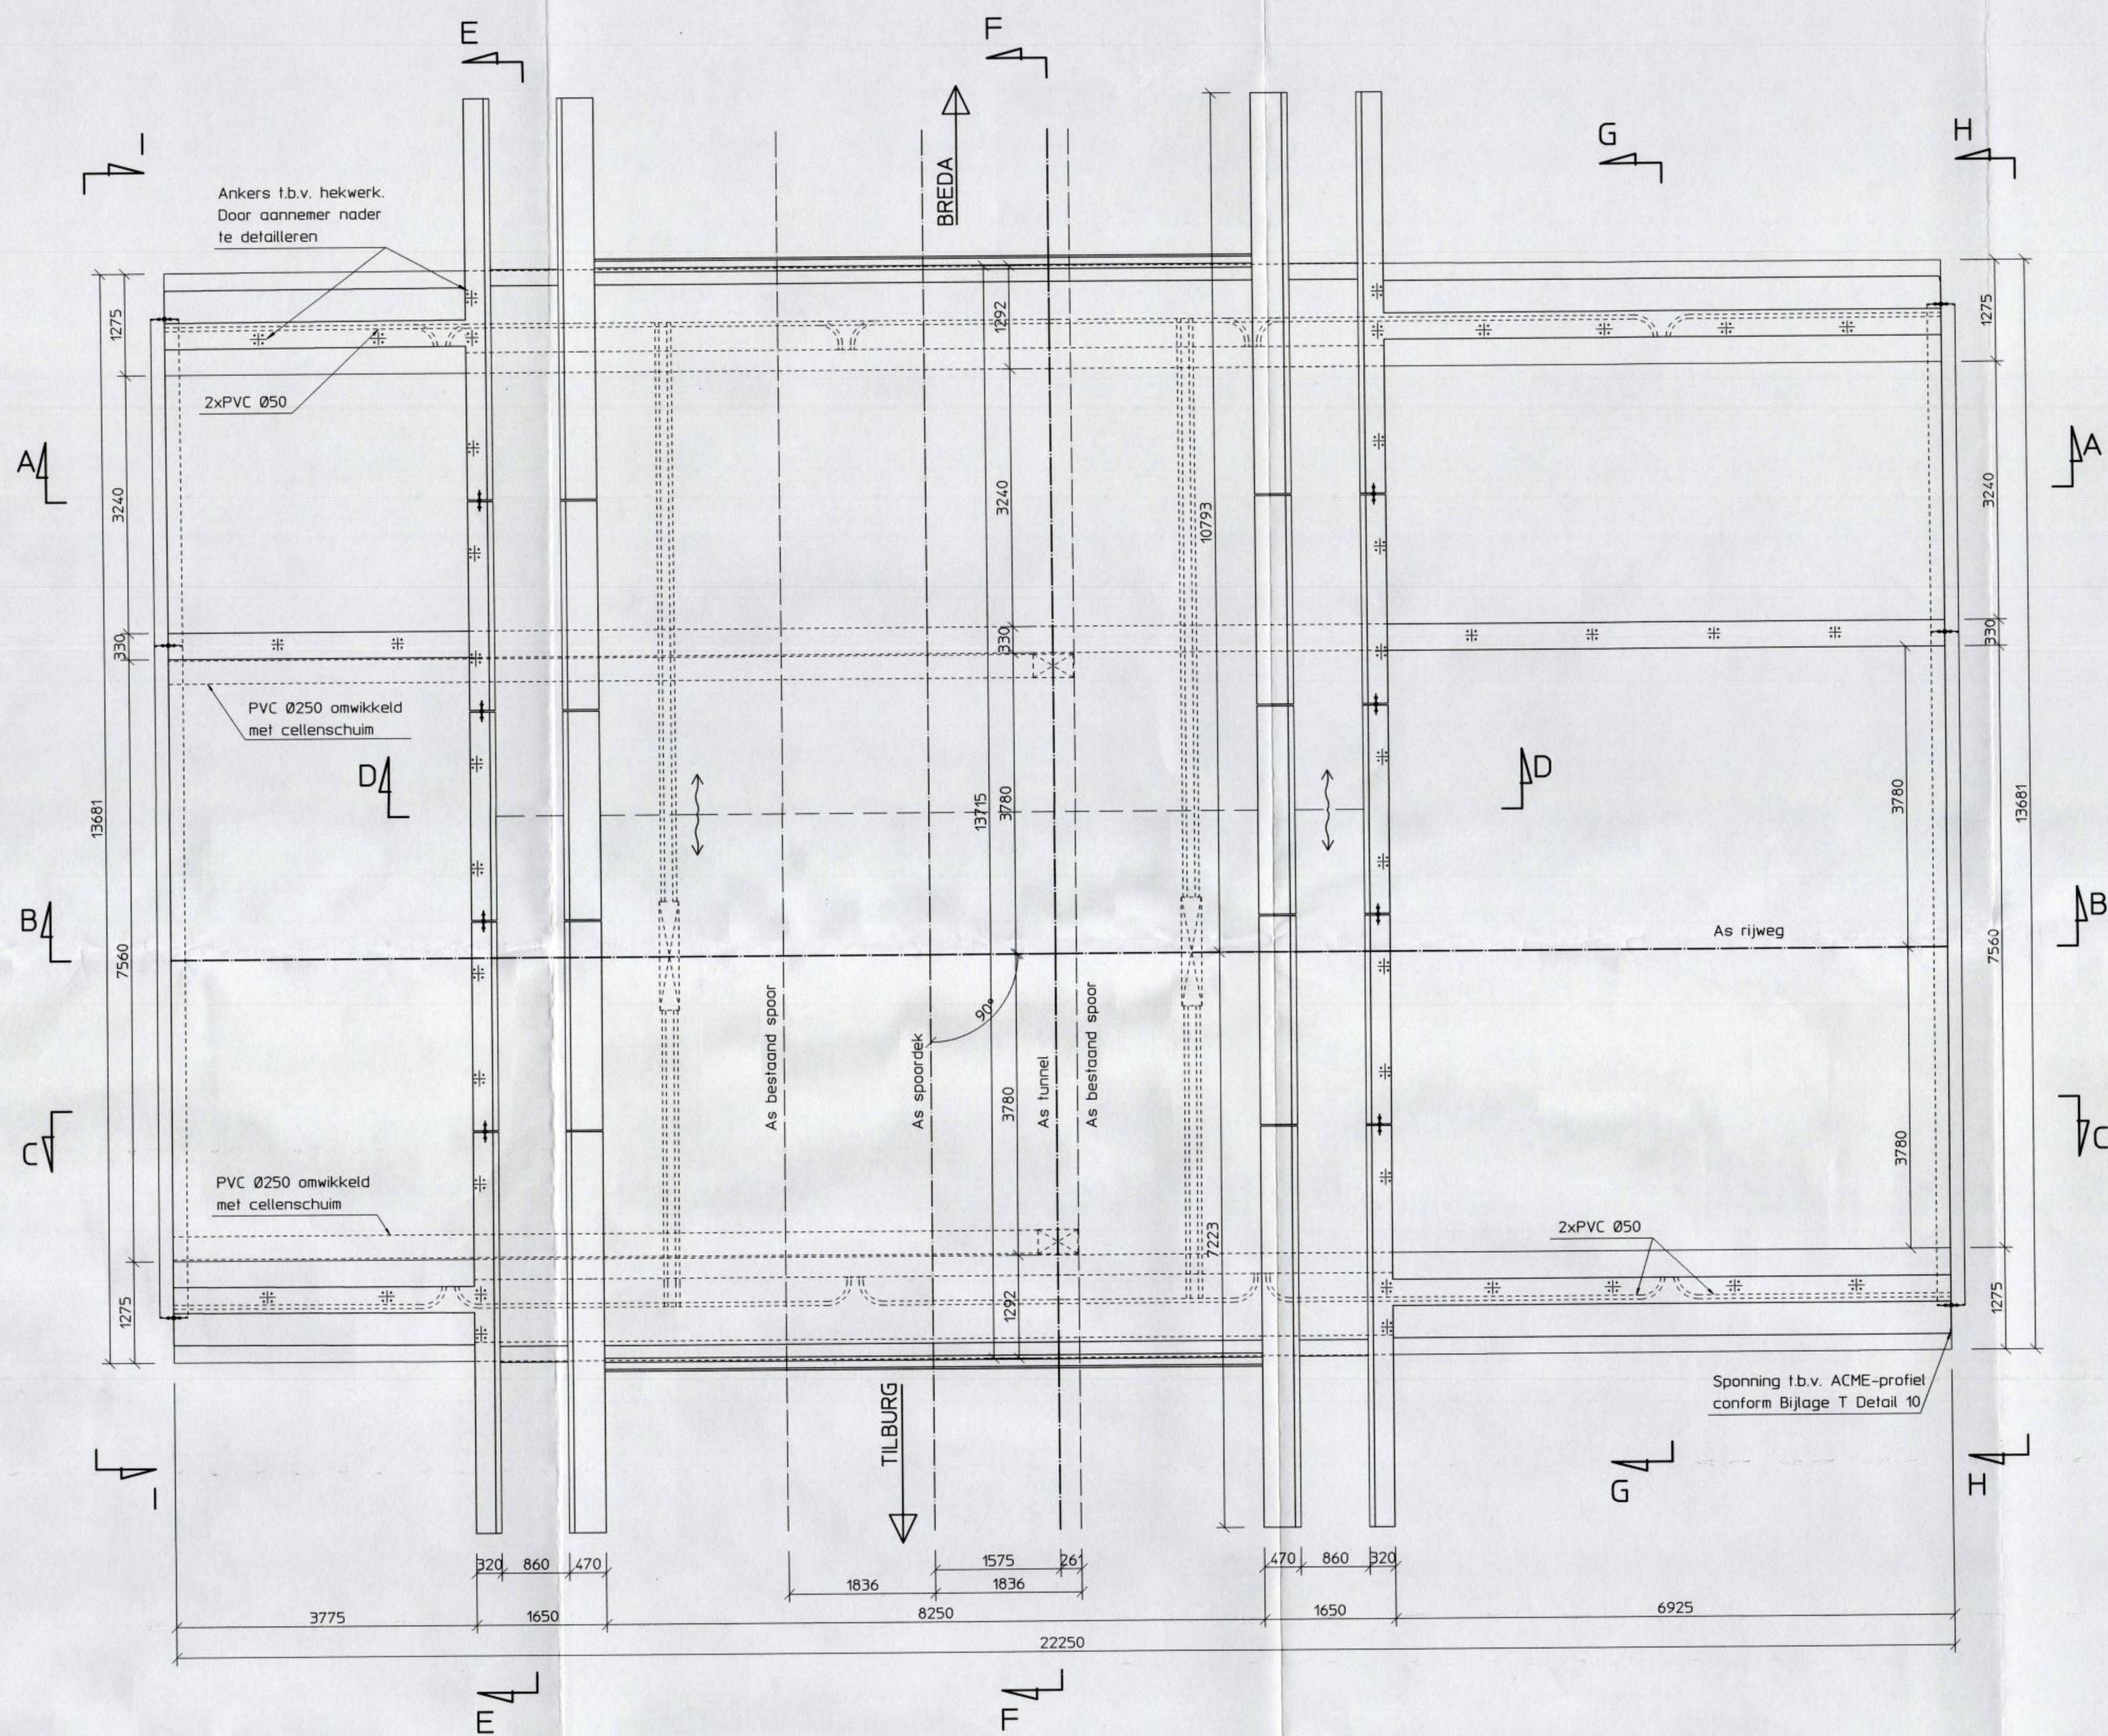


Bovenaanzicht

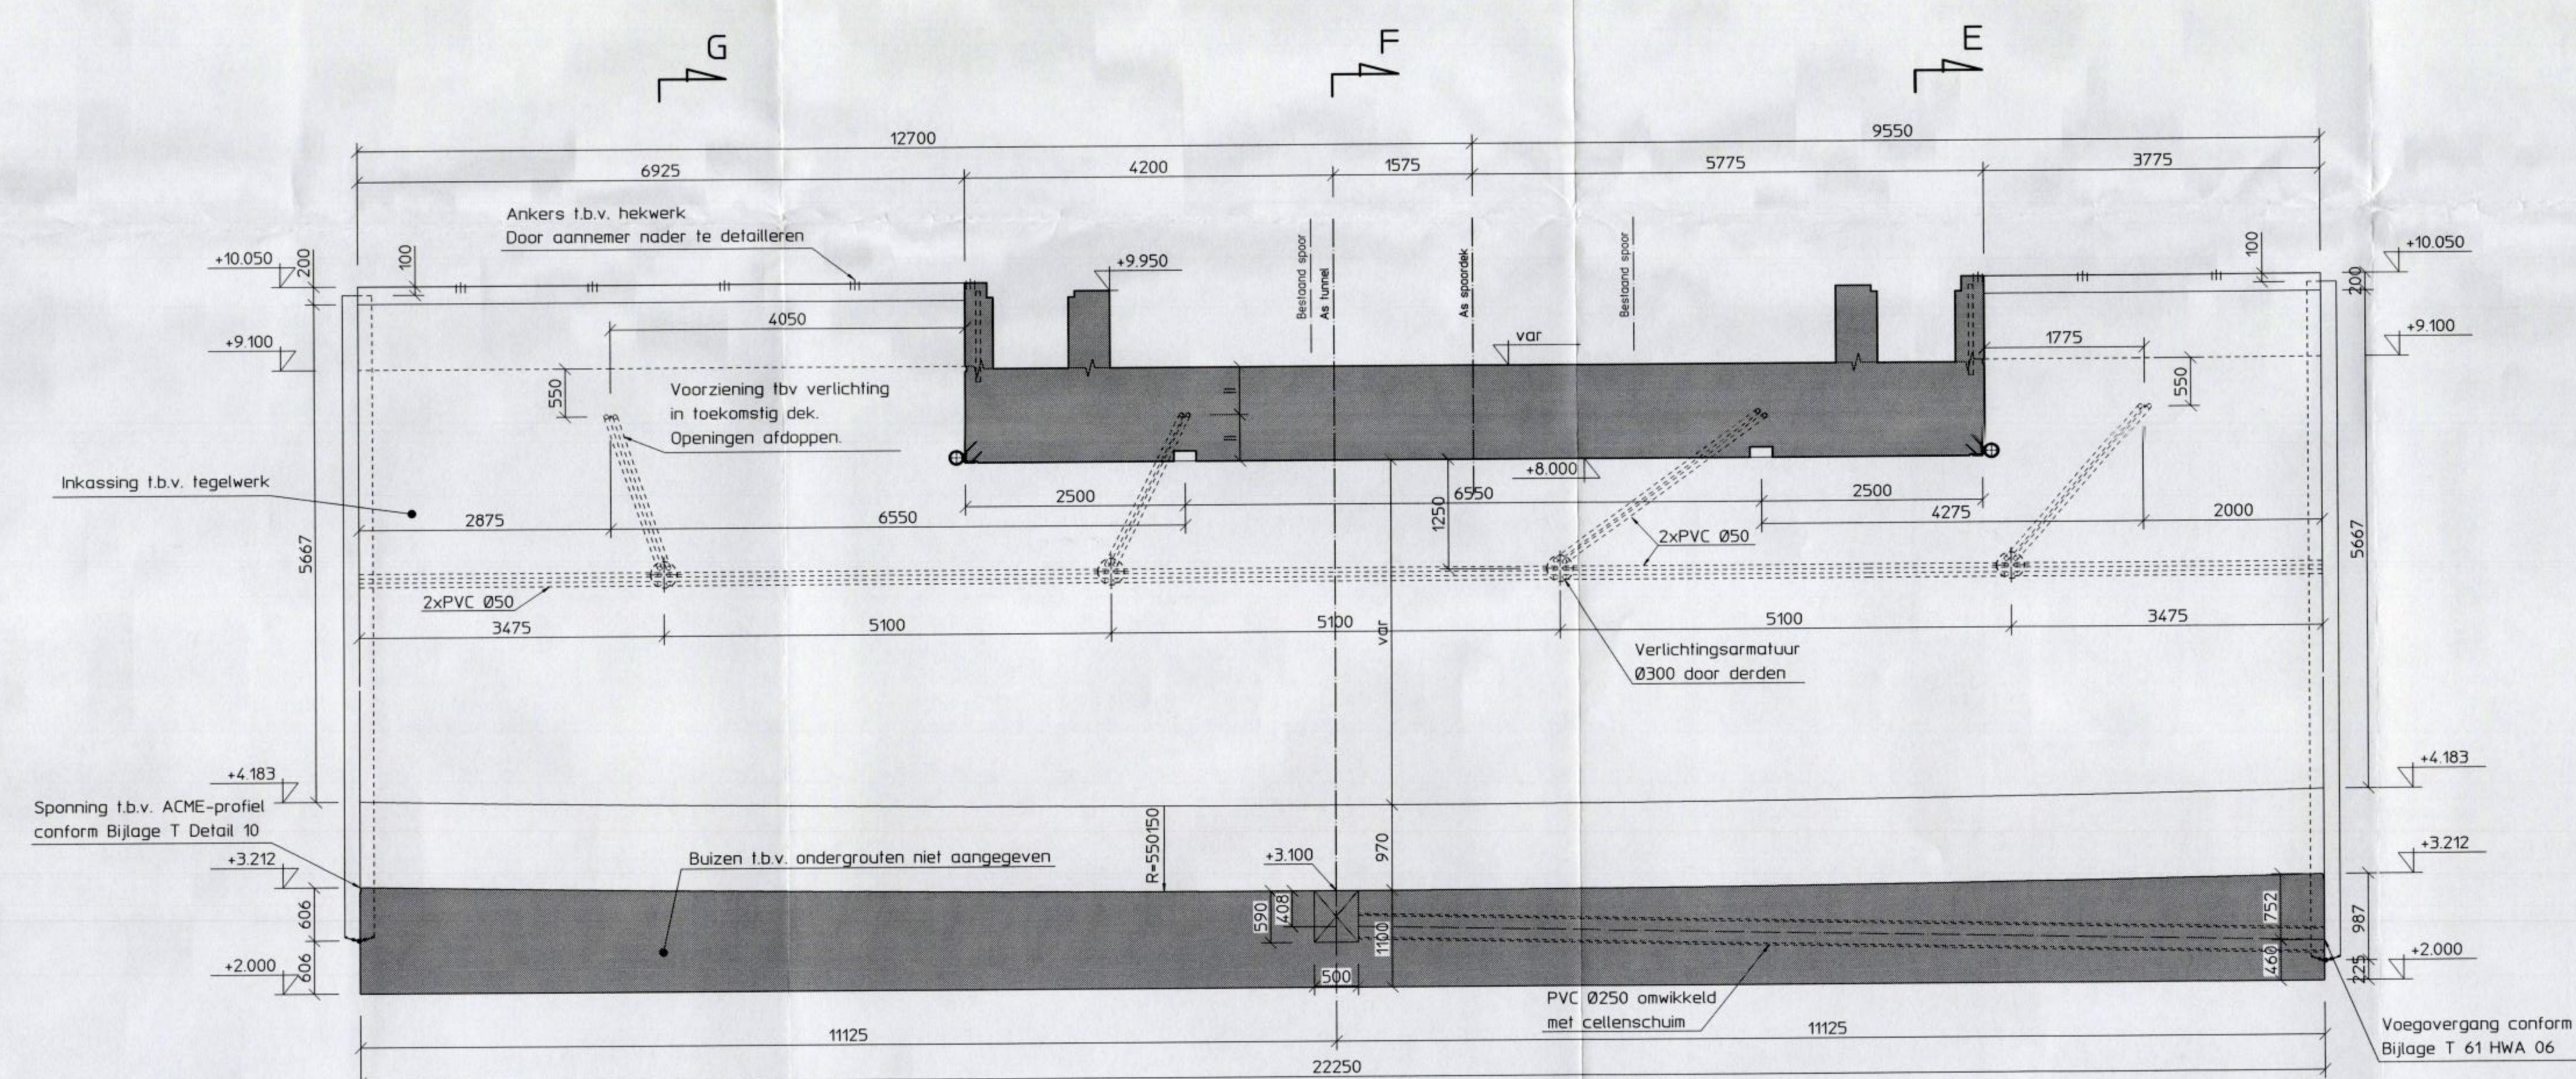


Doorsnede C

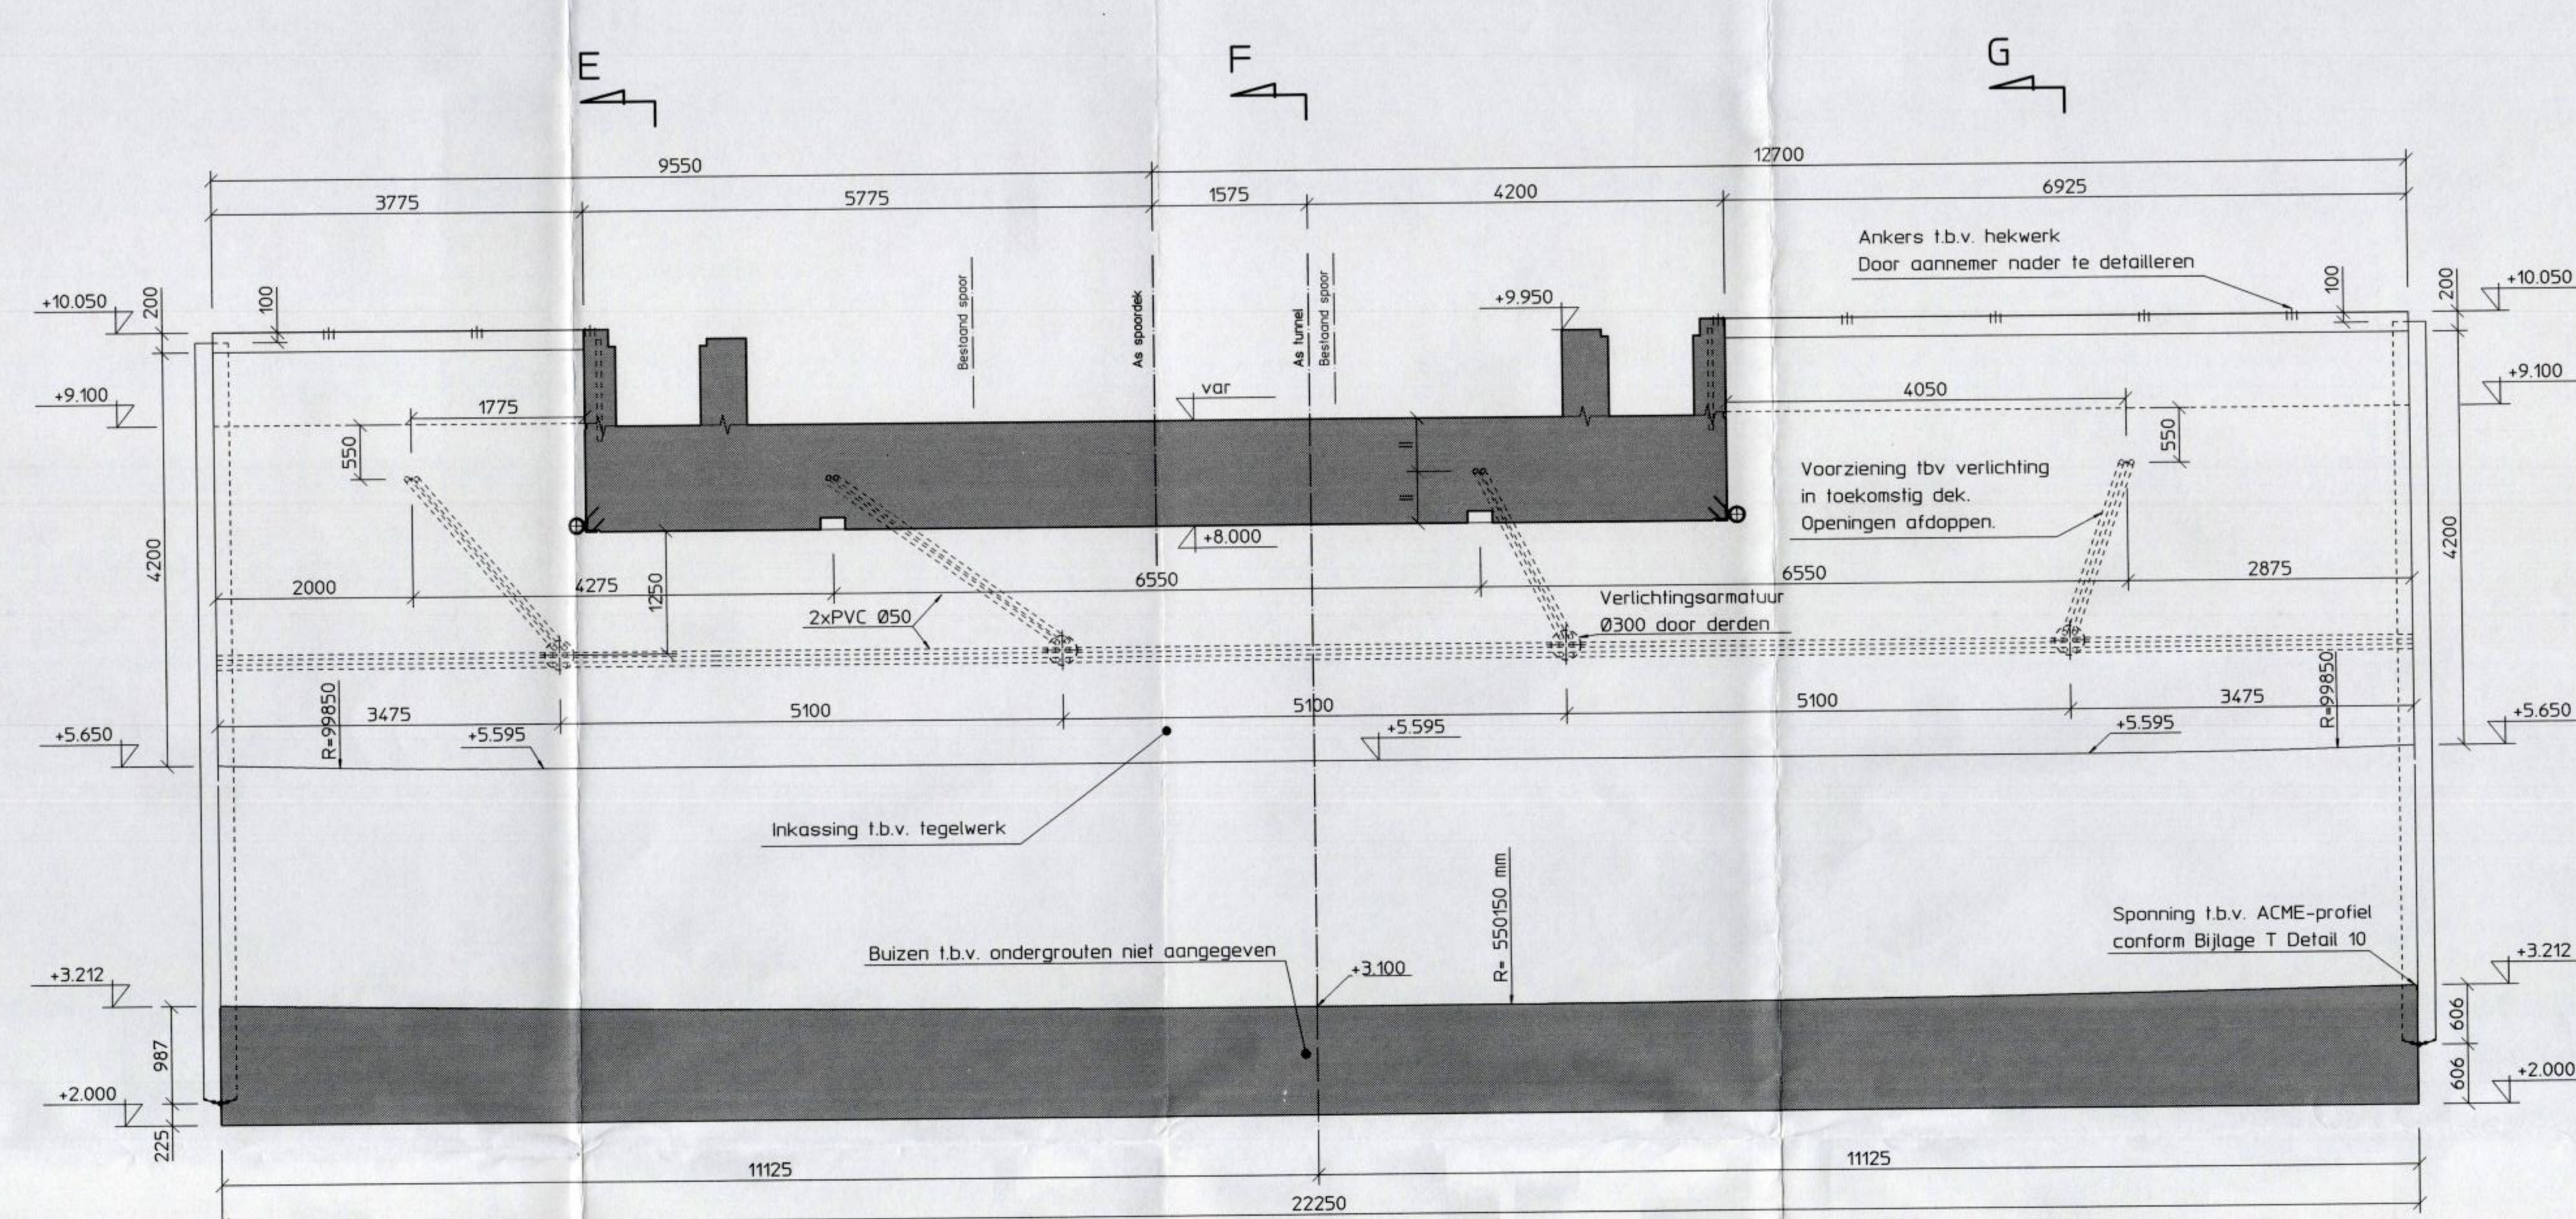

Doorsnede A

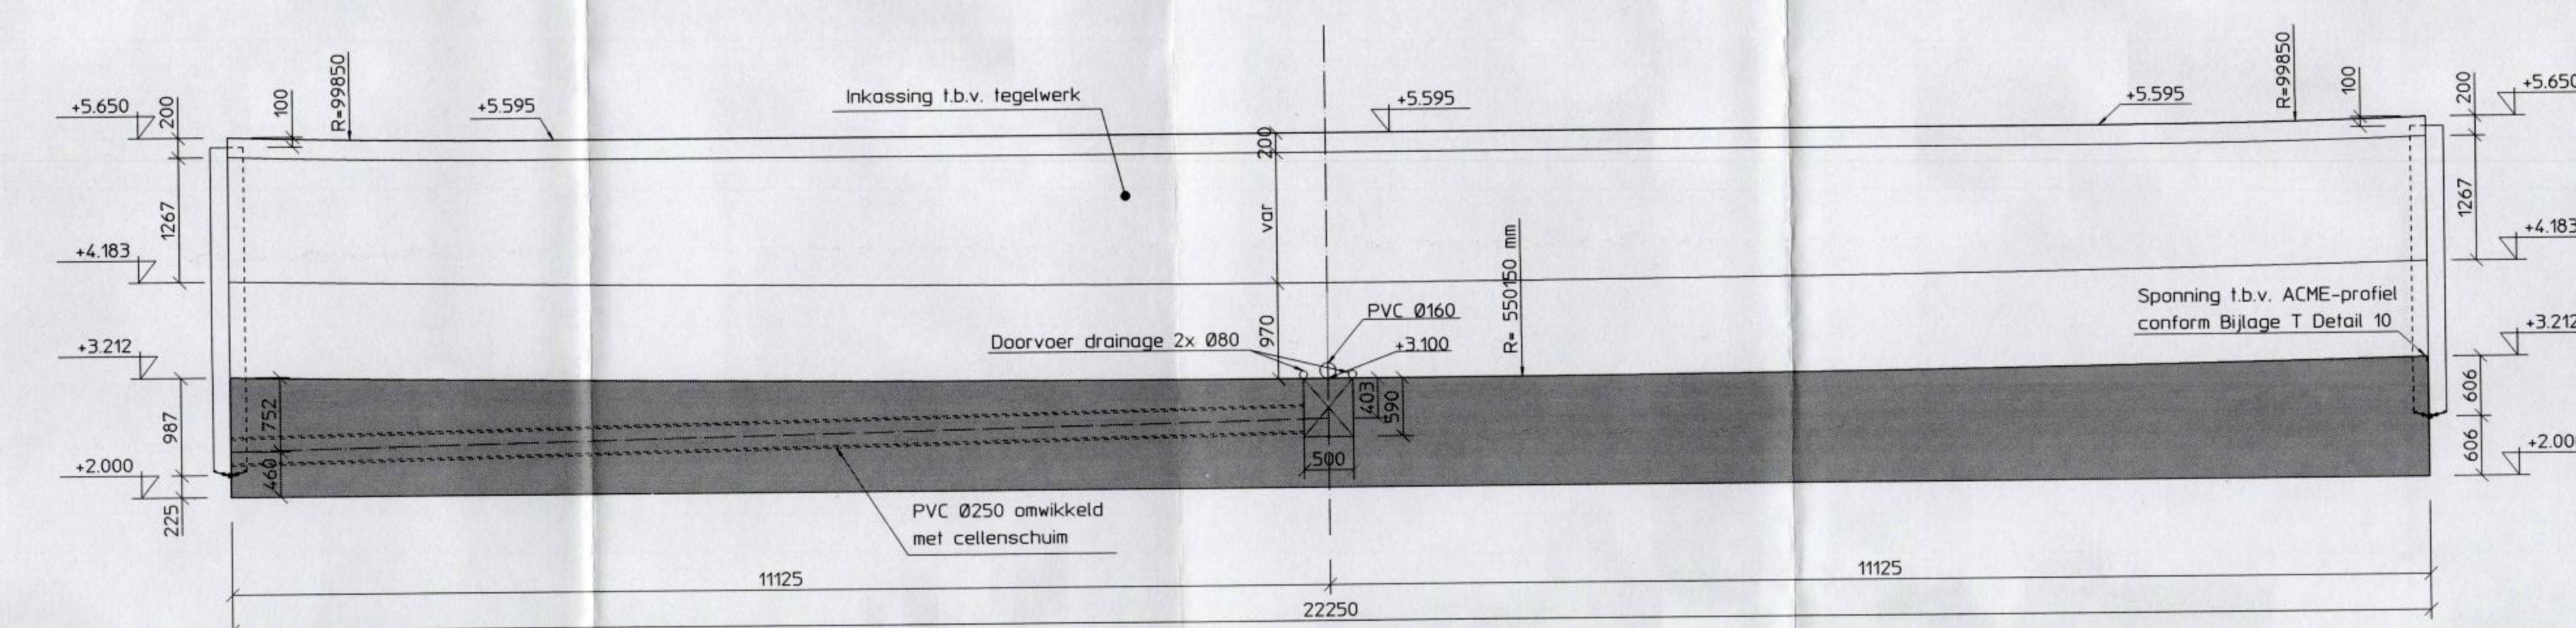

Doorsnede B

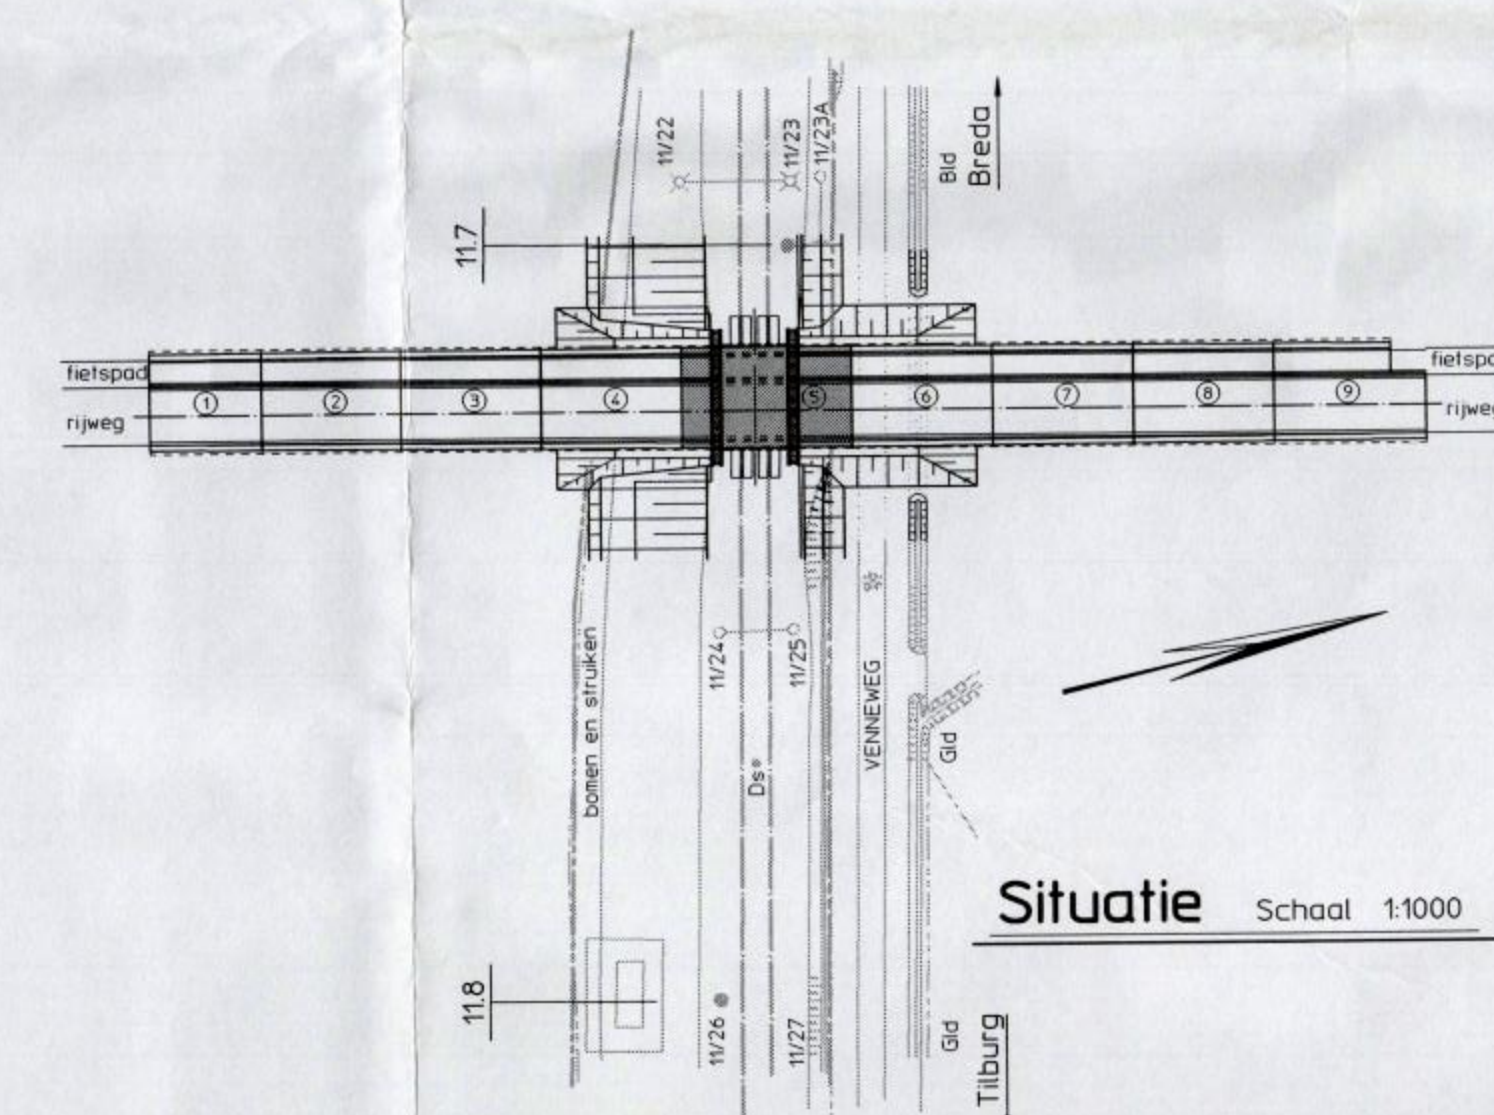

Situatie

- maatvoering in mm
- haagtemaatvoering in m t.o.v. N.A.P.
- voor doorsneden D t/m I zie tek. 3362706 51 M
(Status: REVISIE d.d. 17-12-1999 14:39:50)

naam	par	datum
getekend H.W. Griffler		17-12-99
projectleider J.P. de Boeck		
projectnr 3362706	versie 1.0	
bestelnr V00809450		
tekening AD		
echtheid zie tek.		

420 123 11.720 713 3362706 50 M

Holland Railconsult