



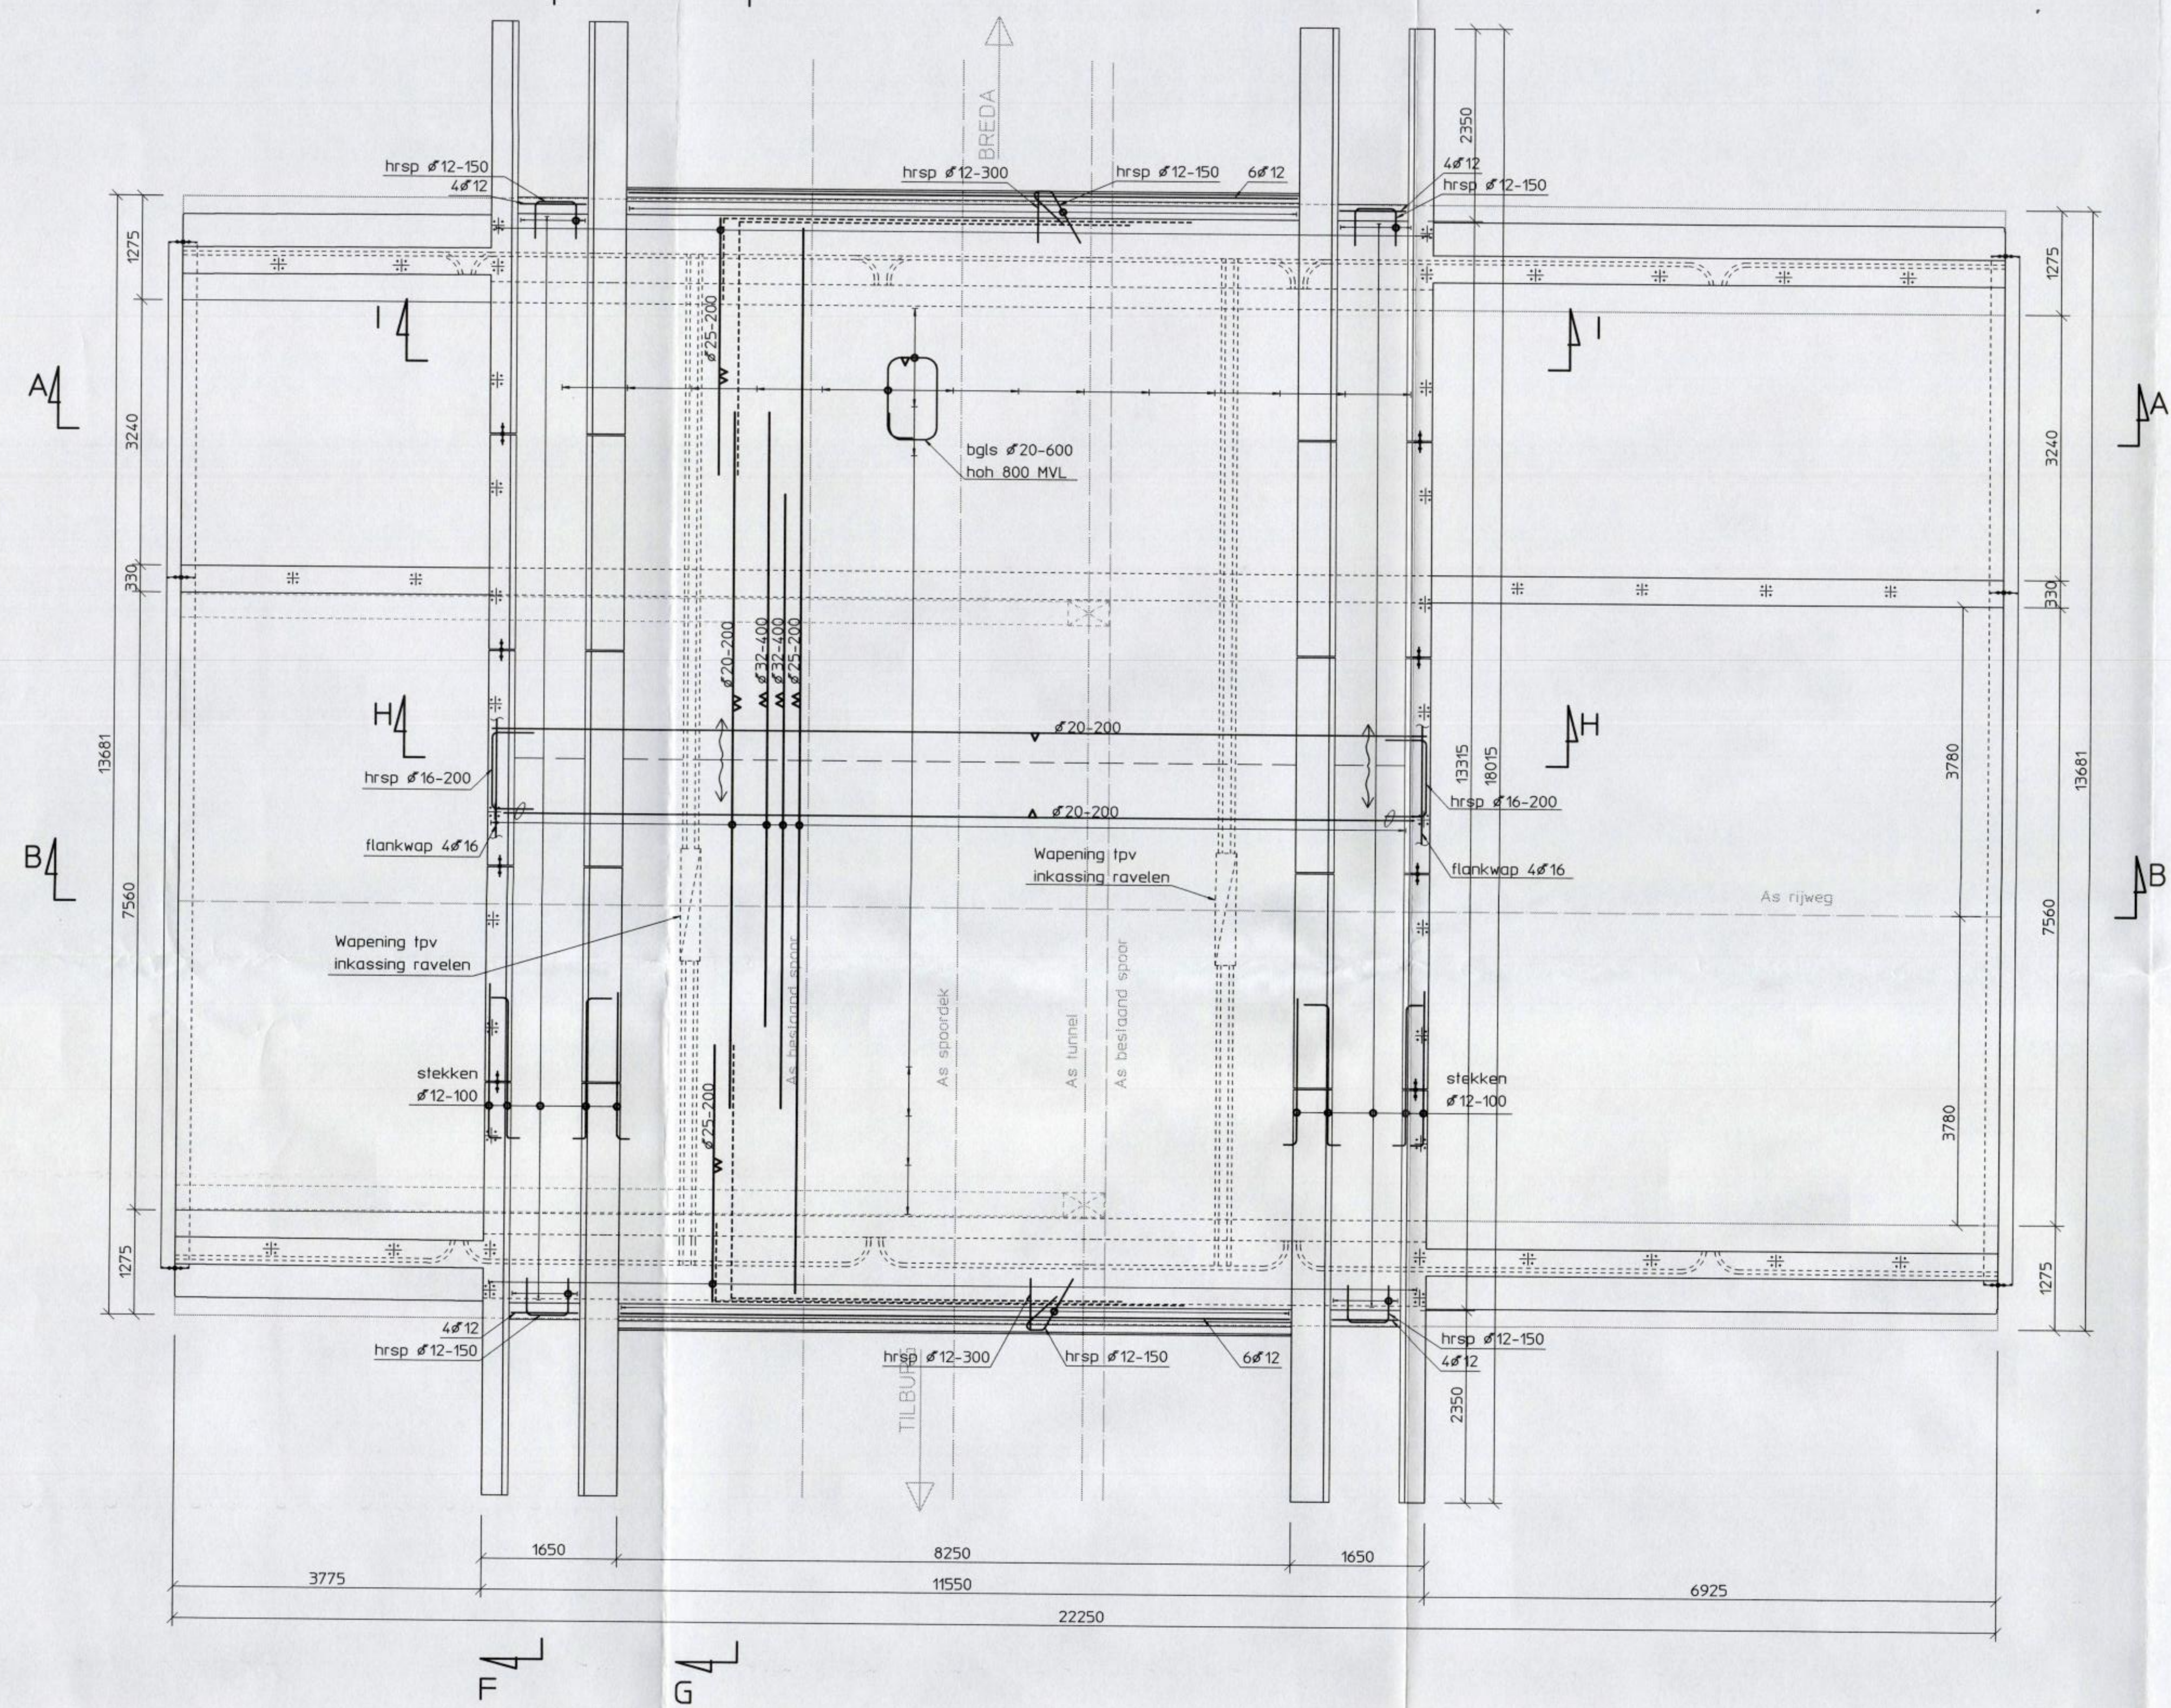


Bovenaanzicht

Schaal 150

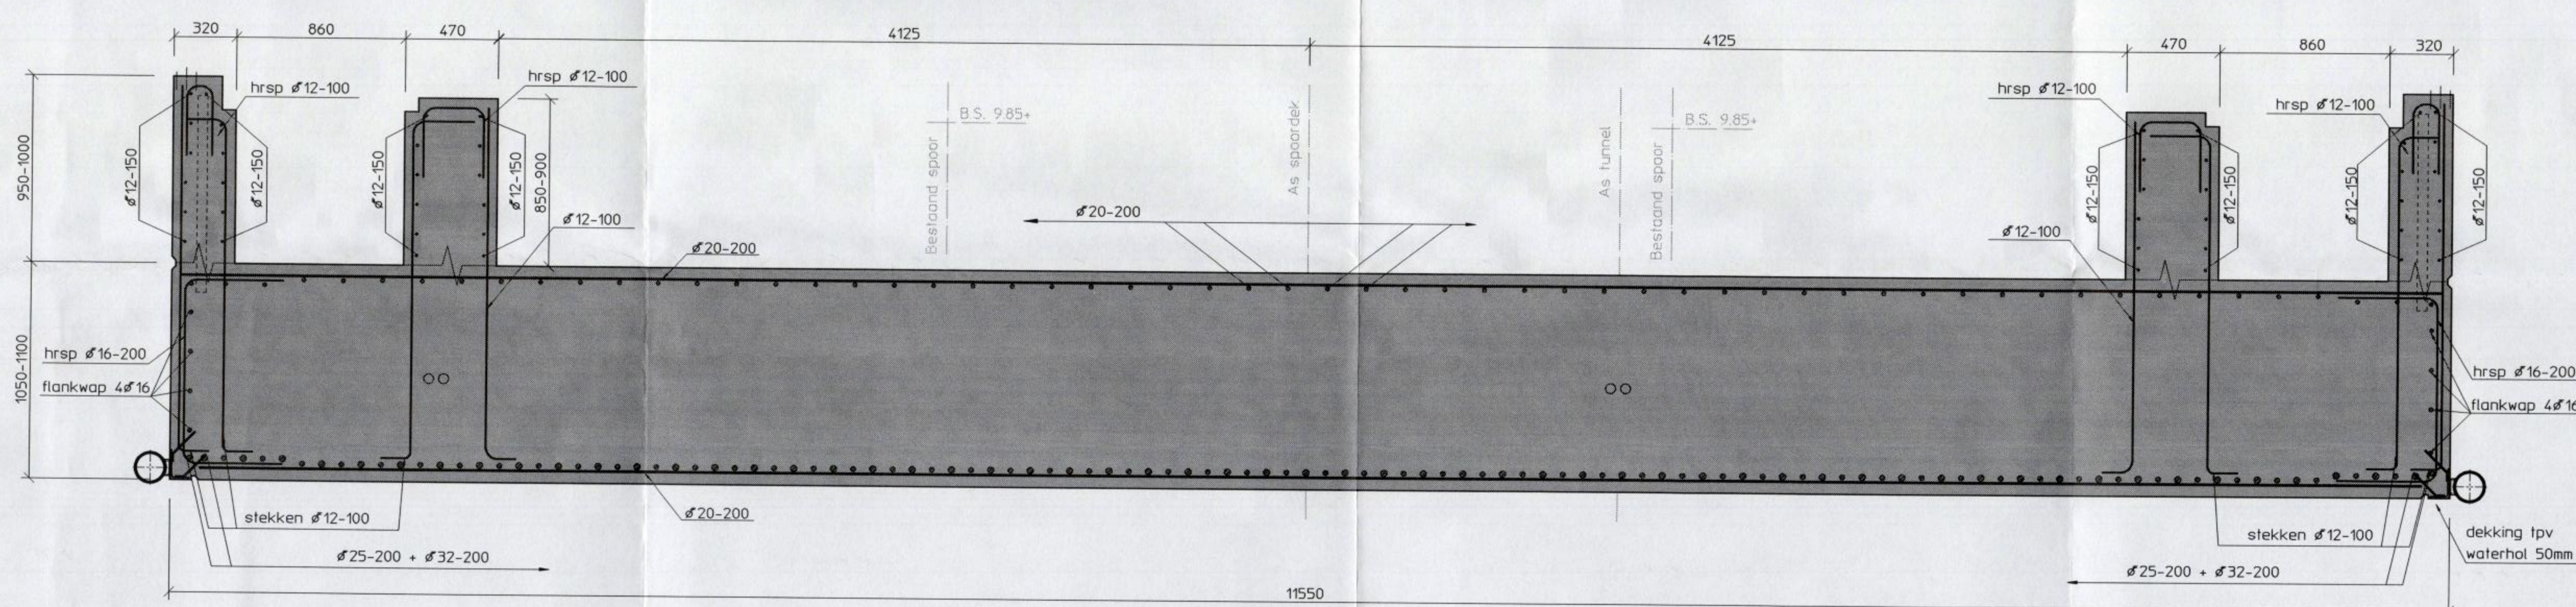


Doorsnede H

Schaal 120

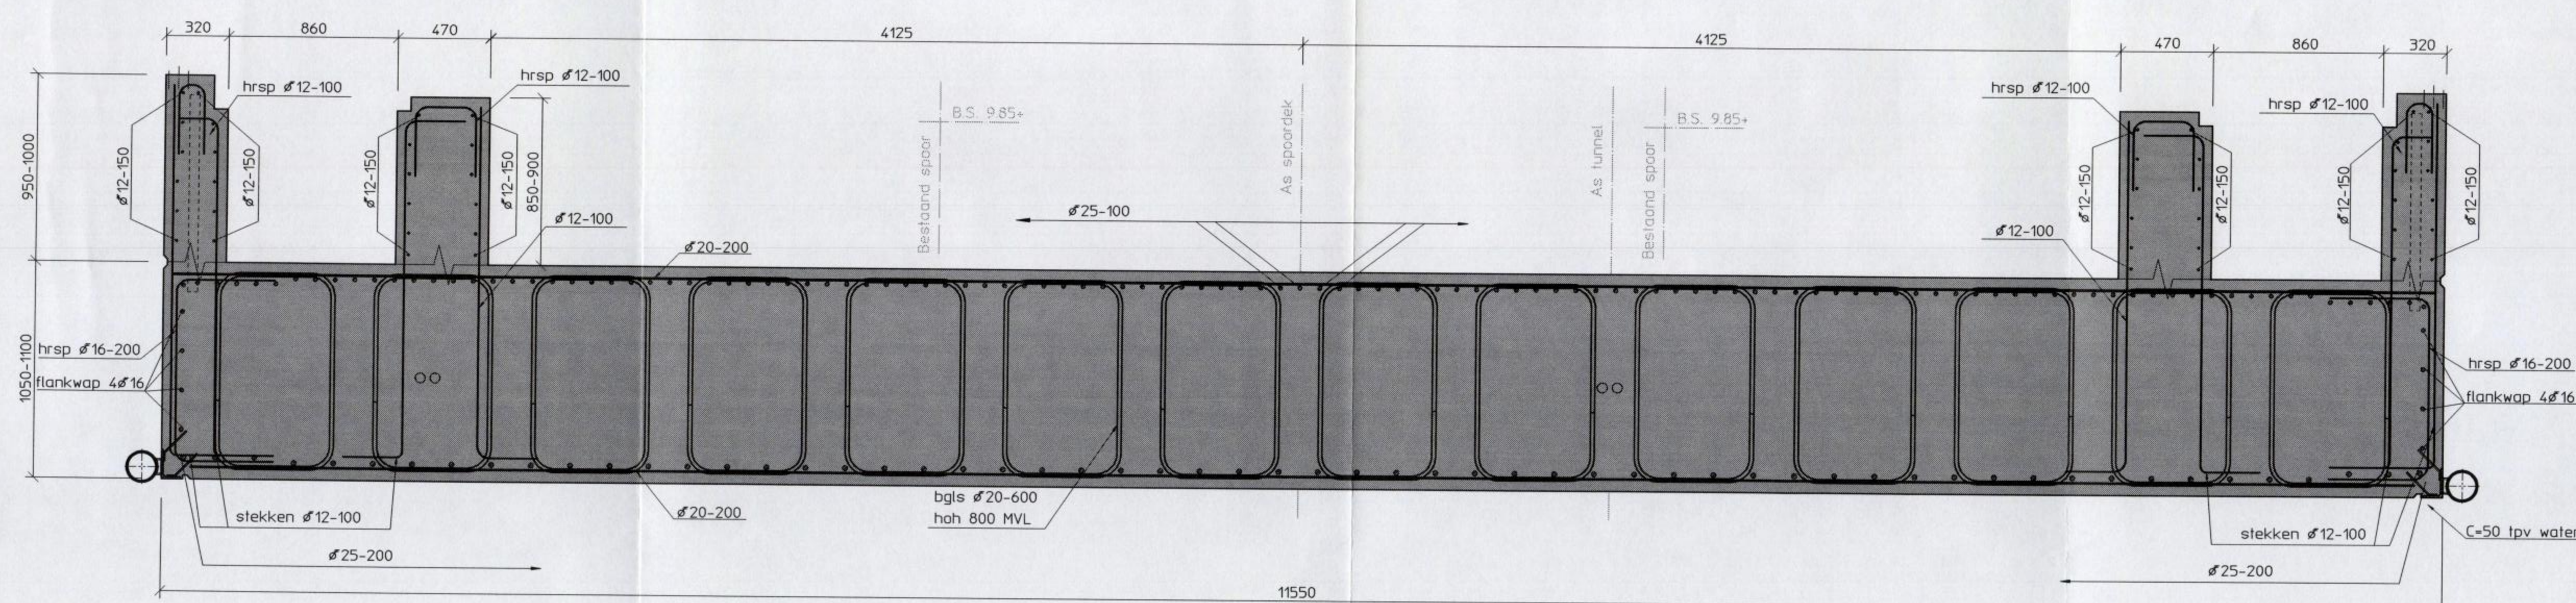

Doorsnede I


Schaal 120

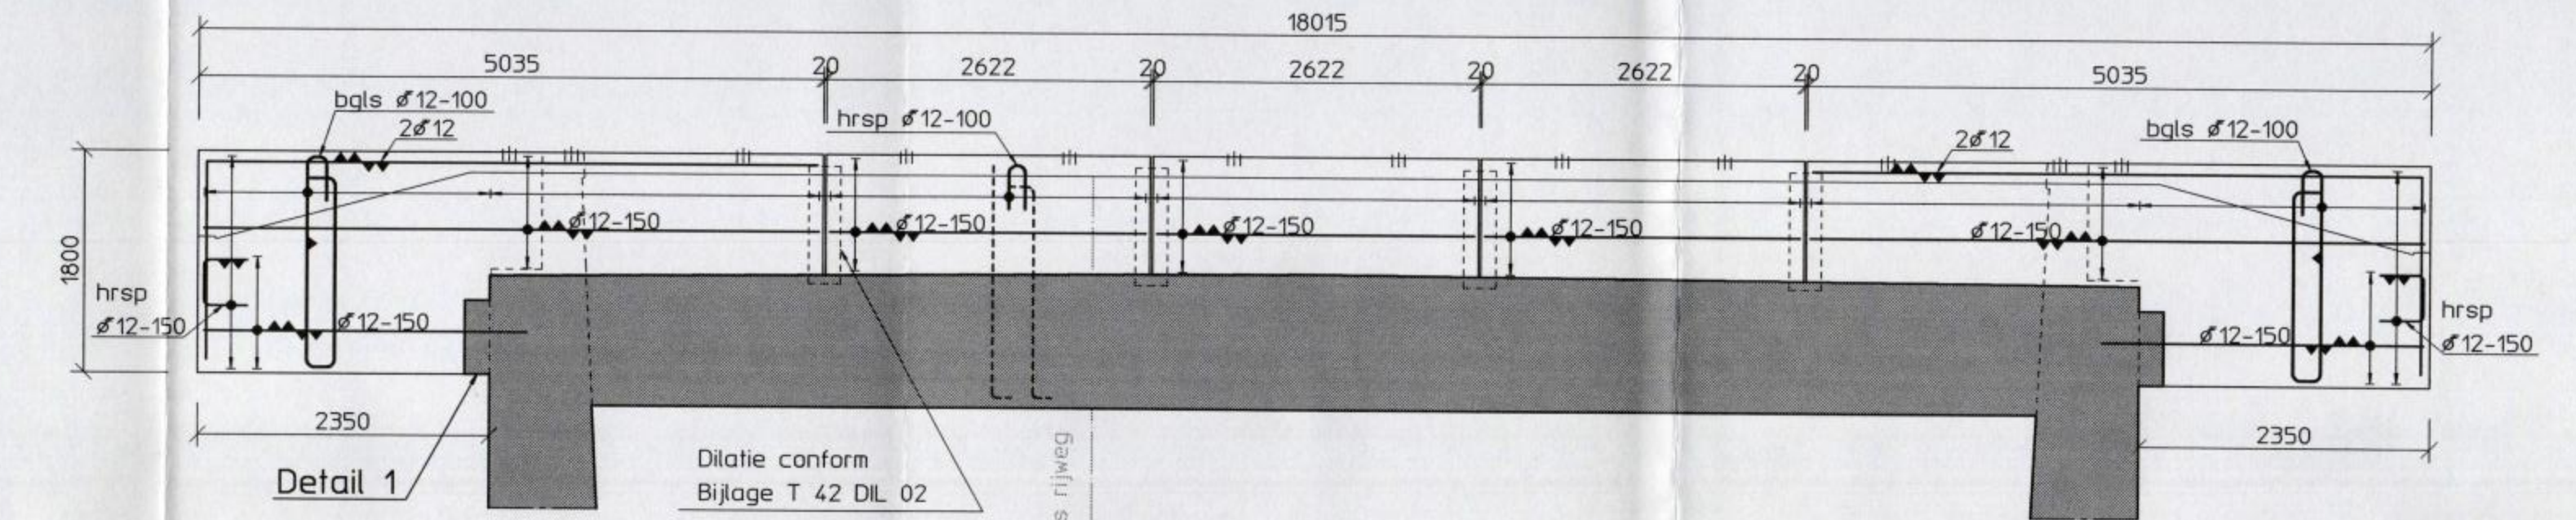

Doorsnede F

Schaal 150


2x uitvoeren

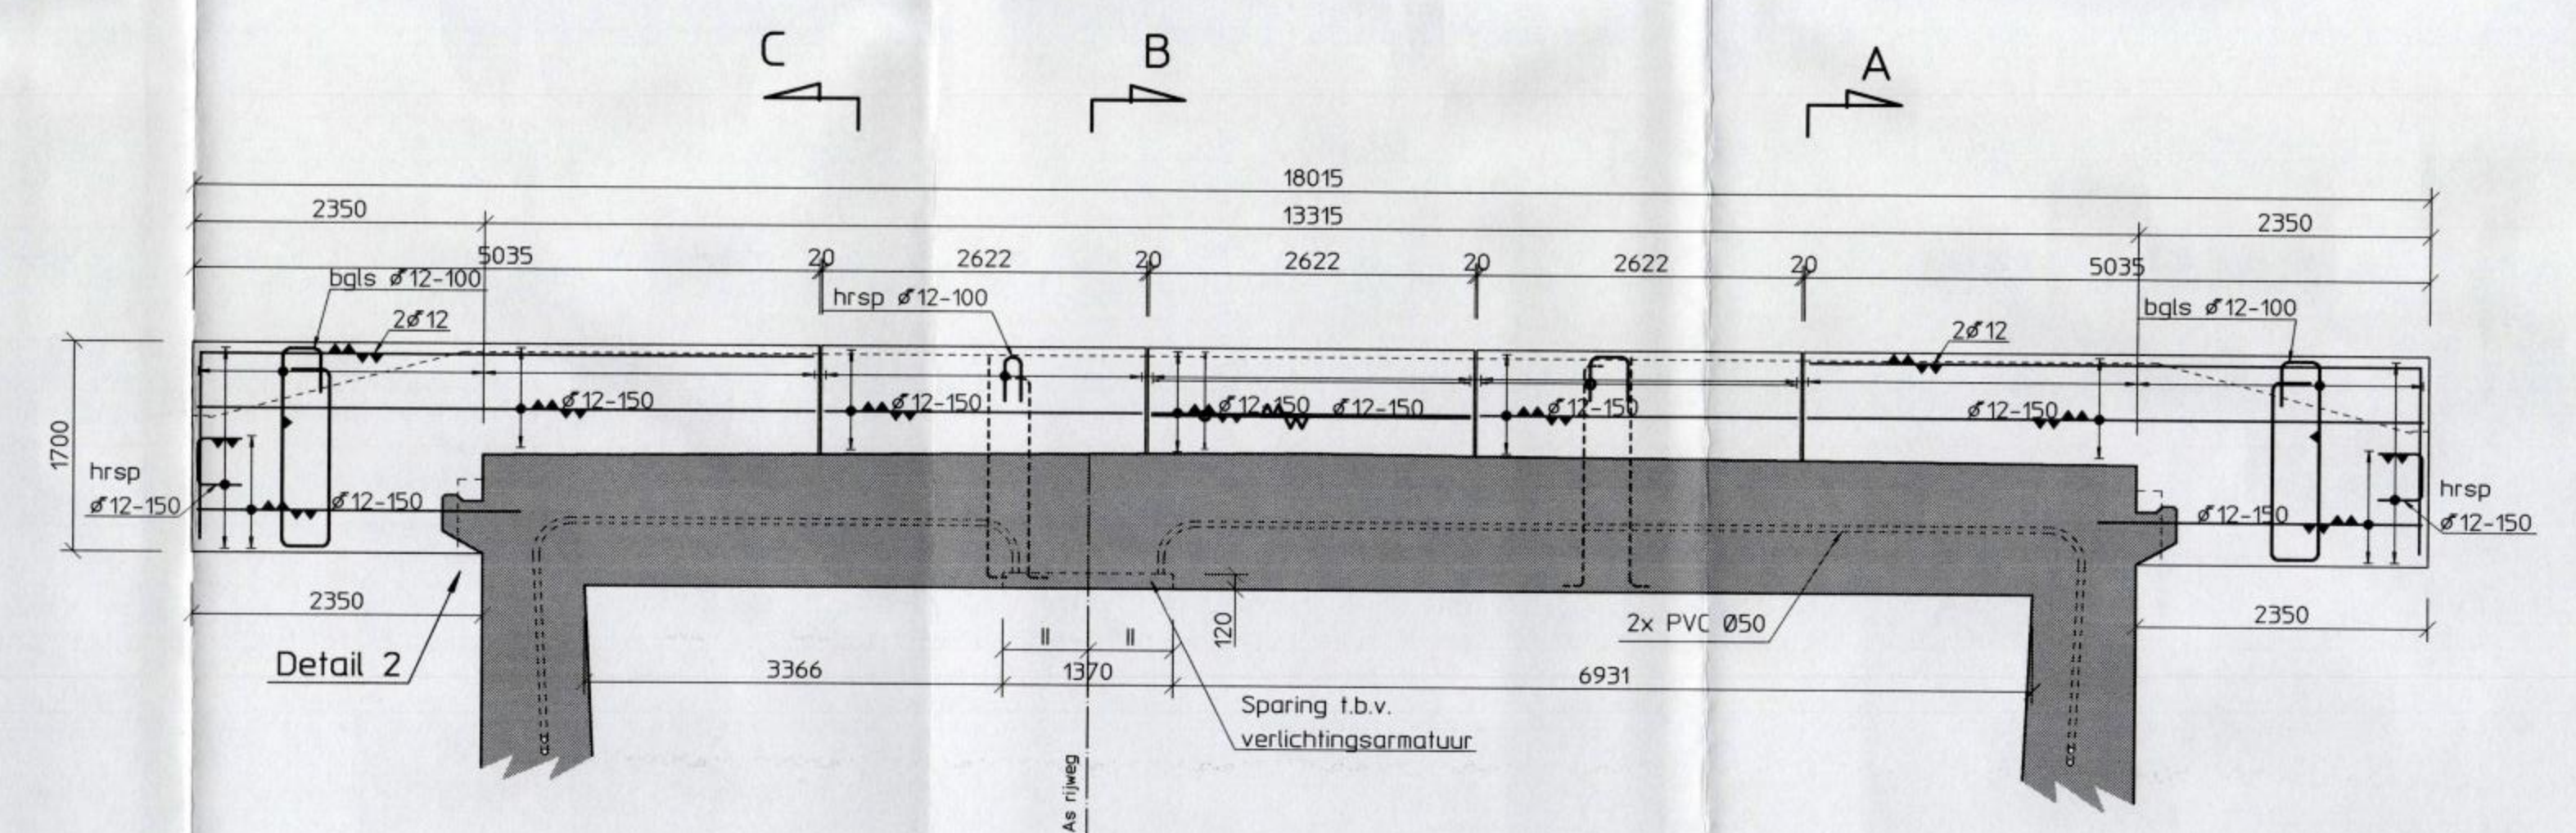

Doorsnede G


Schaal 150

2x uitvoeren

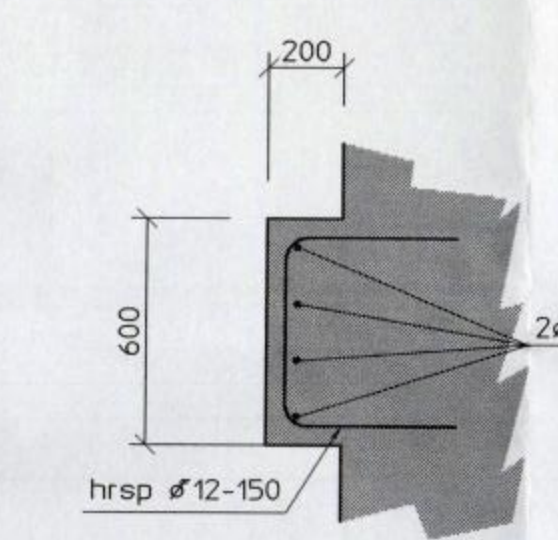

Detail 1

Schaal 120

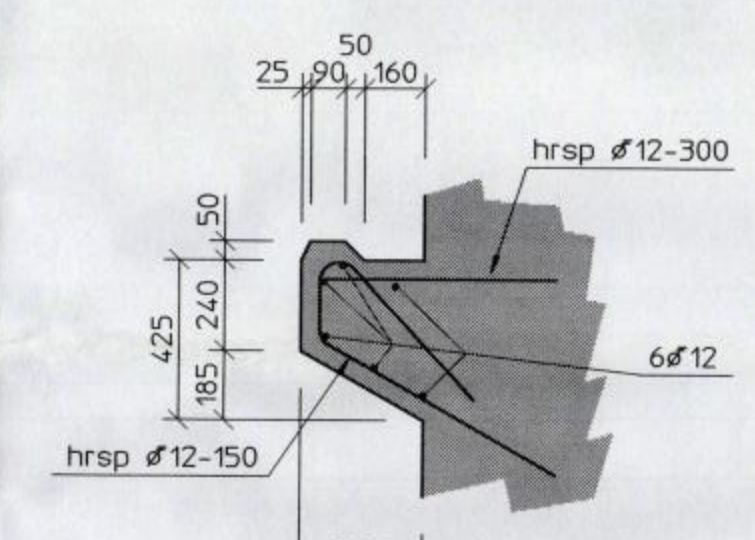

Detail 2

Schaal 120

betondekkingstabel		
betonstaal	- FeB 500 HWL en/of HR NEN 6008	
beton	- sterkteklasse B 35	
	- milieuklasse 3 (vloer) / 5b (wanden+dek)	
	- cement CEM III/B LH	
constructie		
betondekking in mm		
	controleerbaar	oncontroleerbaar
vloer	50	55
wand	50	55
dek	50	55
op- en aanstorten	35	40

verankeringslengten	
ø10	
ø12	270
ø14	
ø16	420
ø20	570
ø25	760
ø28	
ø32	1280
ø40	

- LEGENDA
- Maatvoering in mm
 - Peltmaten in m t.o.v. N.A.P.
 - Voor wapening vloer en wanden zie tek. 3362706 50 W
 - Voor maatvoering zie tek. 3362706 50 M en 51 M
 - HWL = met verspringende las

(Status: REVISIE d.d. 17-12-1999 14:50:40)

getekend	maak	par.	datum	Wapening Moot 5 Blad 2
HW Gijther	JP de Boeck		17-12-99	
projectleider	CF Vink			
projectnr.	3362706	versie	1.0	
besteknr.	V408K09450			
formaat	A0			
schaal	zie tek.			
420	123	11.720	713	3362706 51 W

VA CT PG 82
Postbus 2855
3500 DR Utrecht
Telefoon 030 - 235 89 58
Telefax 030 - 235 72 29
2001010: me0_dwg/c1/c123/m011720/p3362706/06736/51.w. HW Gijther F CT A000 T 26-Feb-1999 16:10:09

Holland Railconsult