




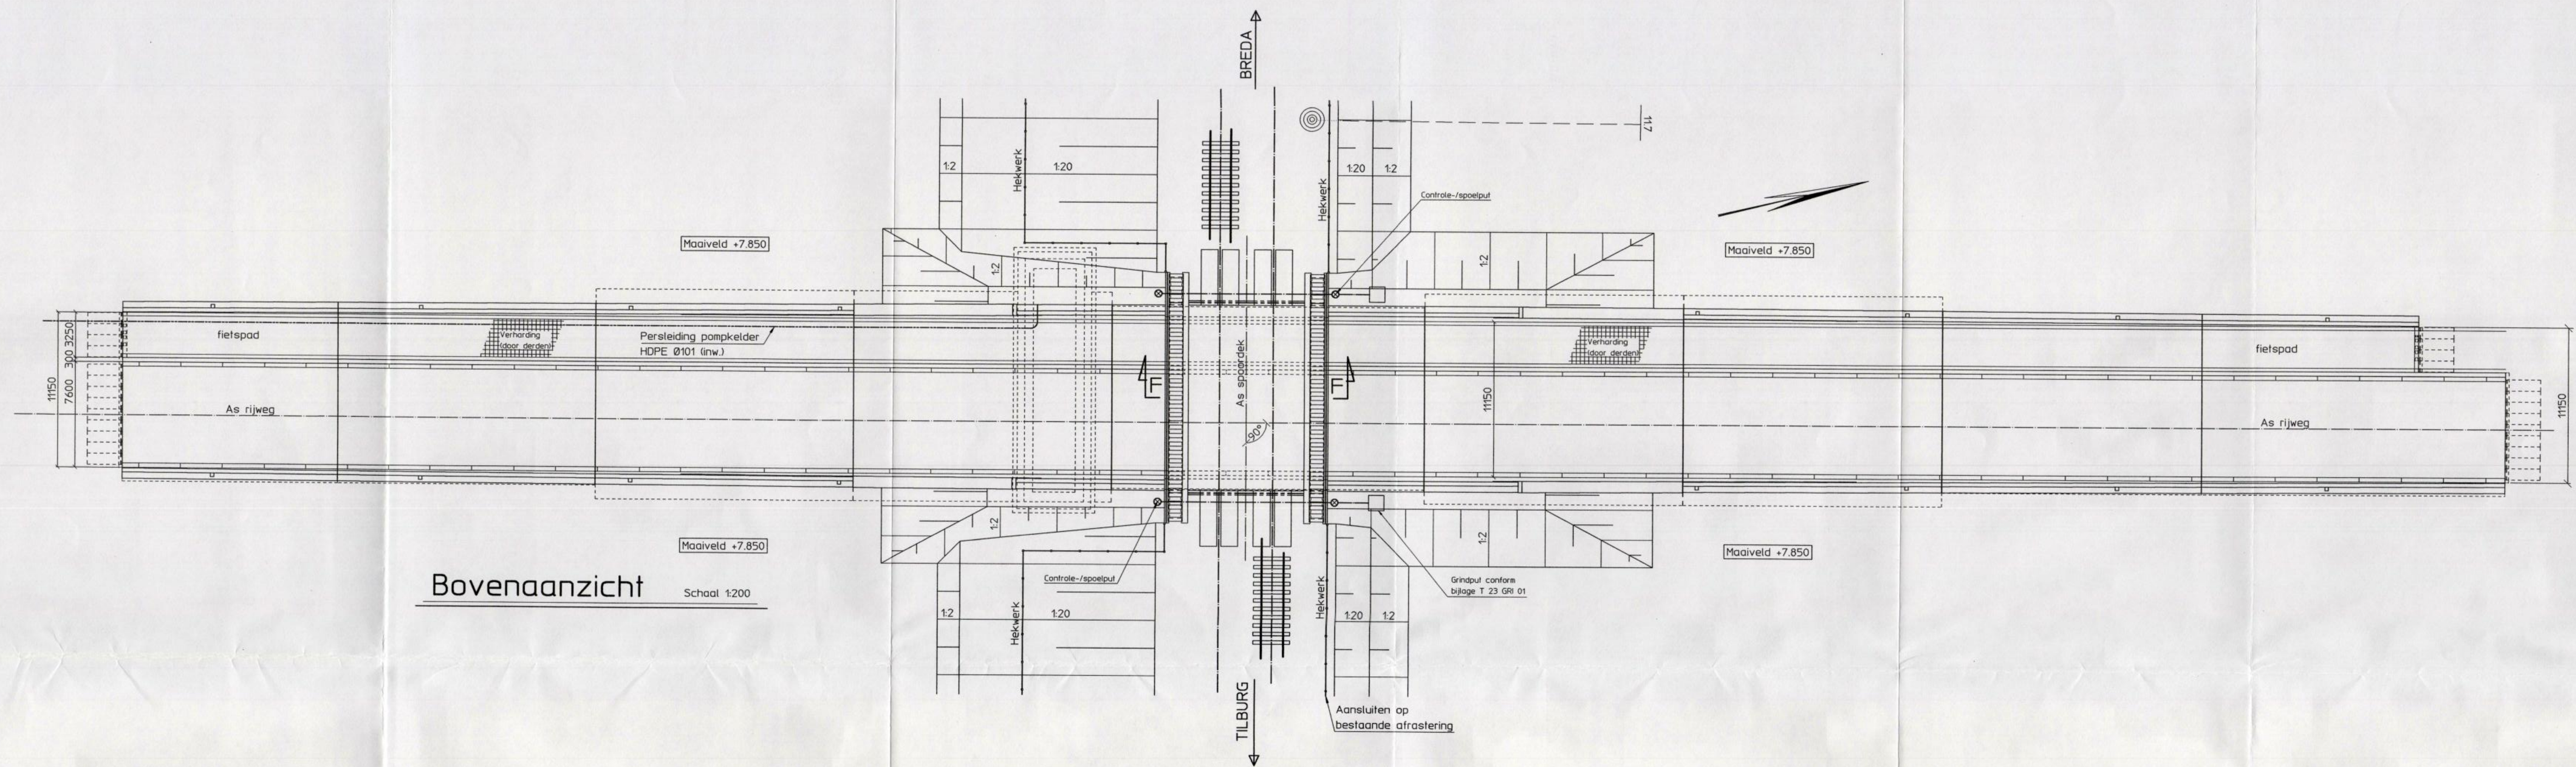


Bovenaanzicht  
Schaal 1:200

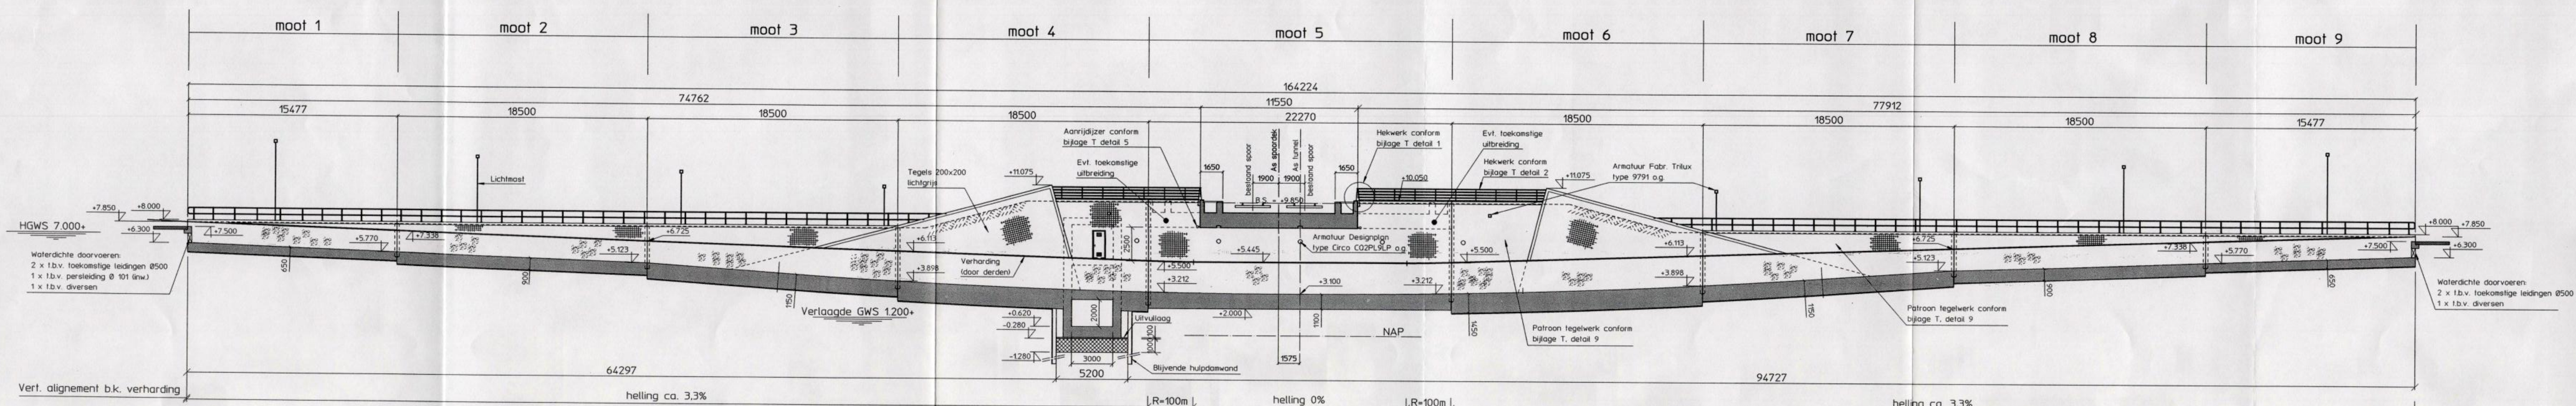

Langsdoorsnede fietspad  
Schaal 1:200

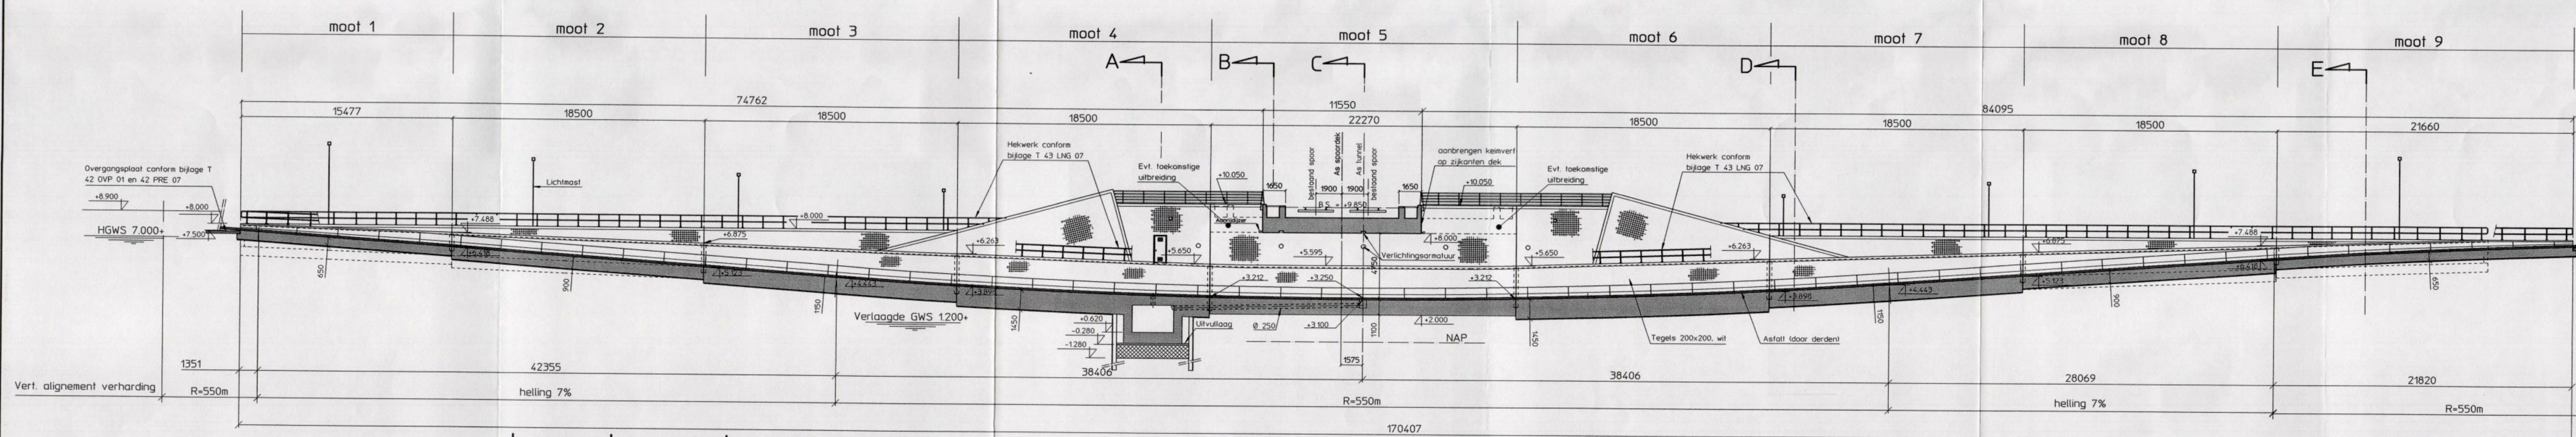

Langsdoorsnede weg  
Schaal 1:200

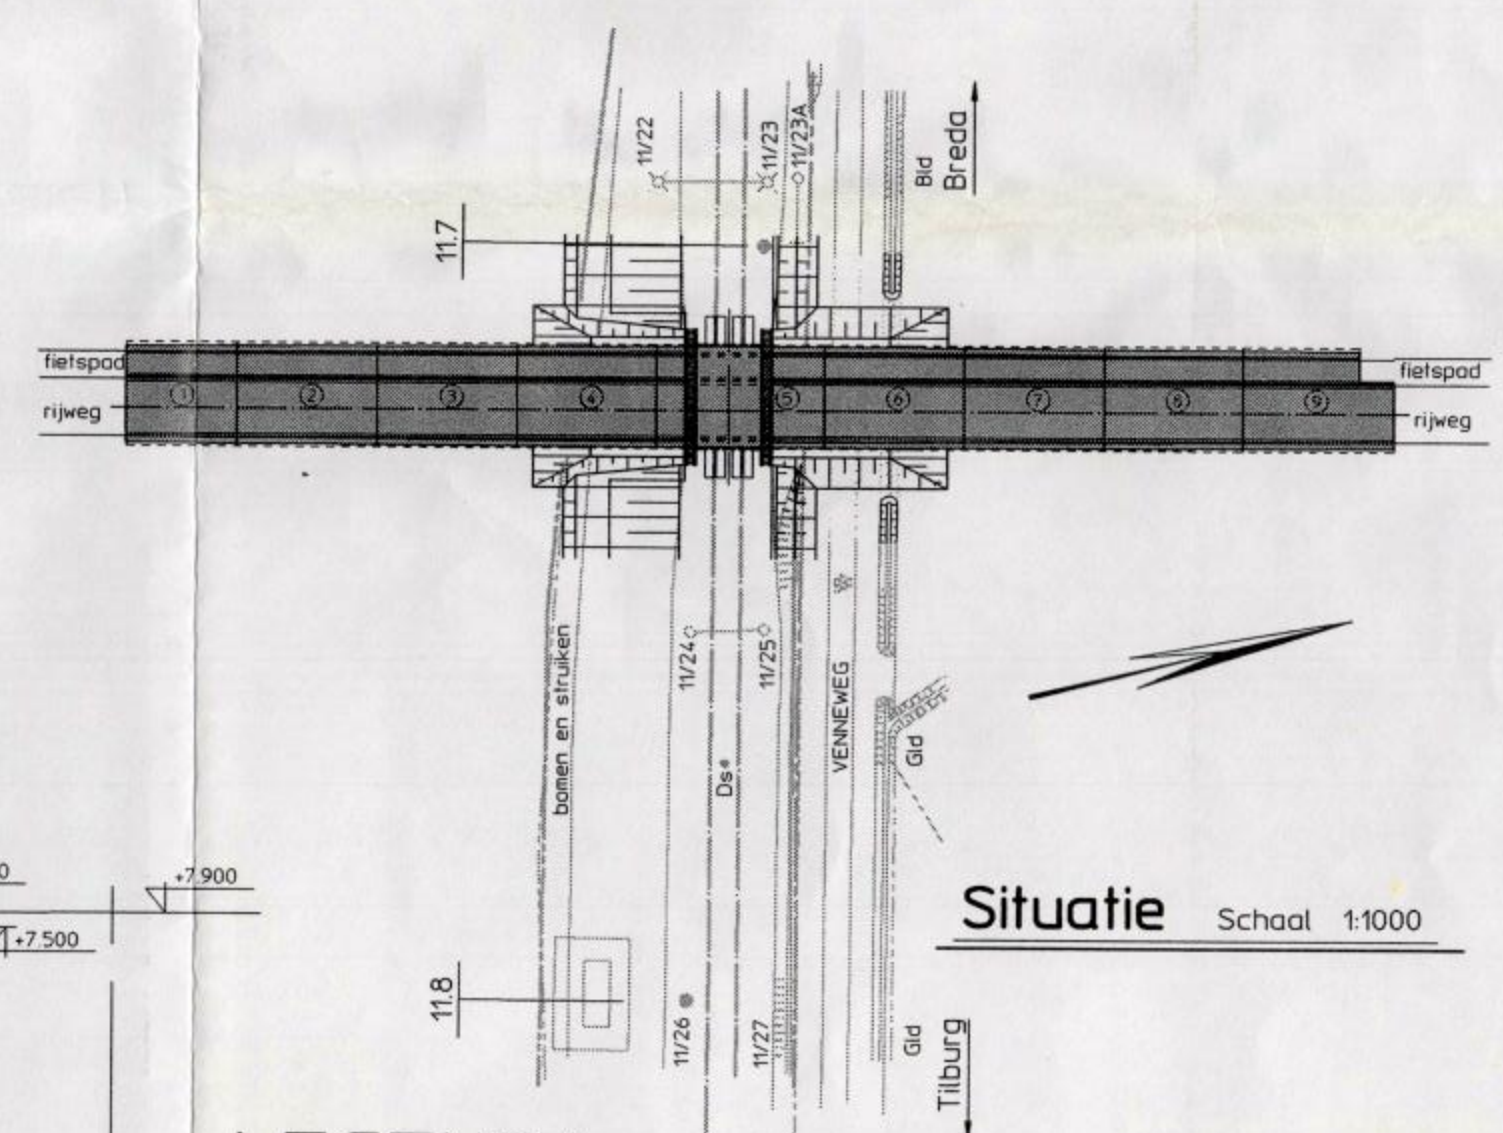

Situatie  
Schaal 1:1000

## LEGENDA

Maten in millimeters, tenzij anders aangegeven  
Hoogtematen in meters t.o.v. NAP, tenzij anders aangegeven

- : gewapend beton
- : prefab beton
- : onderwaterbeton

Ontwerpsnelheid: V = 160 km/h  
Voor doorsnede A 1/m F & details zie blad B-2

Status: REVISIE d.d. 13-04-2000 09:11:03

| getekend     | naam         | par.   | datum    | Bestekstekening                 |
|--------------|--------------|--------|----------|---------------------------------|
| V. Winkelaar | V. Winkelaar |        | 25-11-98 | Bovenaanzicht + langsdoorsneden |
| projectie    | CF. Vink     | versie | 1.0      | NS Railinfrabeheer Regio Zuid   |
| projectie    | 3362704      |        |          | Gilze Rijen                     |
| bestek       | V08B09450    |        |          | Onderdoorgang Europaal          |
| formaat      | A0           |        |          |                                 |
| schaal       | div.         |        |          |                                 |

420 123 11.720 713 3362704 B-1

VA CT PG B2  
Postbus 2805  
3500 GW Utrecht  
Telefoon 030 - 235 89 58  
Telefax 030 - 235 72 29

Holland Railconsult

plafond /me0\_dwg/ct/c123/kn011720/pa3362704/loc714/p\_1\_revisie backp c1.3 13-04-2000 09:23:13