

Gilze - Rijen
Onderdoorgang Europalaan
Besteknr. V40 BK 09450

Bijlage T:

Diverse details


Bijlage T: Inhoudsopgave

Projectgebonden details:


- Detail 1: Leuning type 1
- Detail 2: Leuning type 2
- Detail 3: New Jersey-profiel
- Detail 4: Aanrijdijzer en waterhol
- Detail 5: Huismerk NS met jaartal, klein model
- Detail 6: Doorvoer t.b.v. drainagebuis
- Detail 7: Uitvoering omranding tegelwerk
- Detail 8: Tegelwerk in spiegels en t.p.v. voegen
- Detail 9: Patroon tegelwerk
- Detail 10: Dilatatievoeg tunnelwand

Algemene standaarddetails:


- 23 DRA 01: Drainage kunstwerk t.p.v. de overgangsplaten
- 23 GRI 01: Grindkoffer, inhoud circa 1 m³
- 23 ISP 01: Inspectieput
- 42 DIL 02: Voegafdichting kabelkoker
- 42 OVP 01: Overgangsplaat t.b.v. wegverkeer
- 42 PRE 02: Kabelovergangsplaat bij kunstwerk met doorgaand ballastbed
- 42 PRE 04: Overgangsplaat in het spoor
- 42 PRE 06: Voetpadplaten
- 42 PRE 07: Overgangsplaat t.b.v. wegverkeer
- 42 STR 01: Stortnaad vloer/wand
- 43 LNG 07: Leuning type 3
- 43 STA 01: Stalen ladder en handgrepen t.b.v. toegang waterberging
- 43 STA 02: Stalen deur
- 61 HWA 06: Voegovergang hemelwaterafvoer type 2

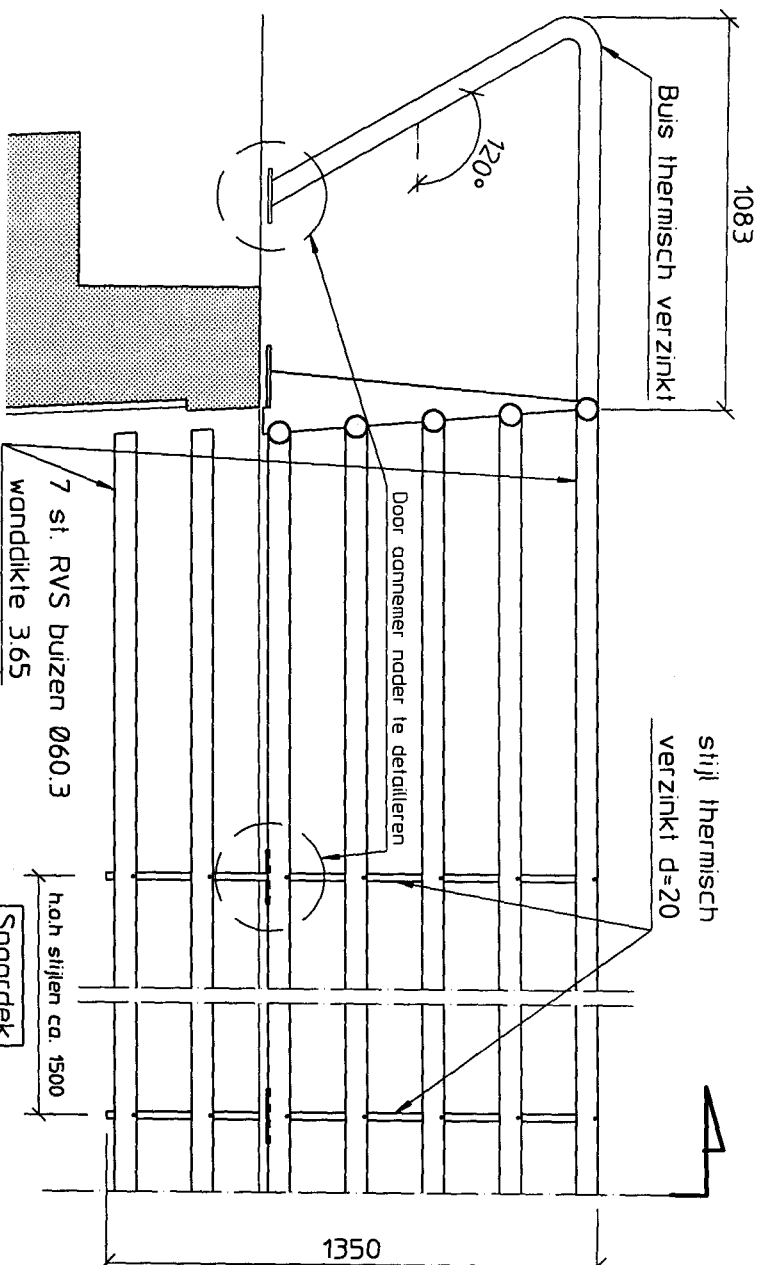

Aanzicht hek

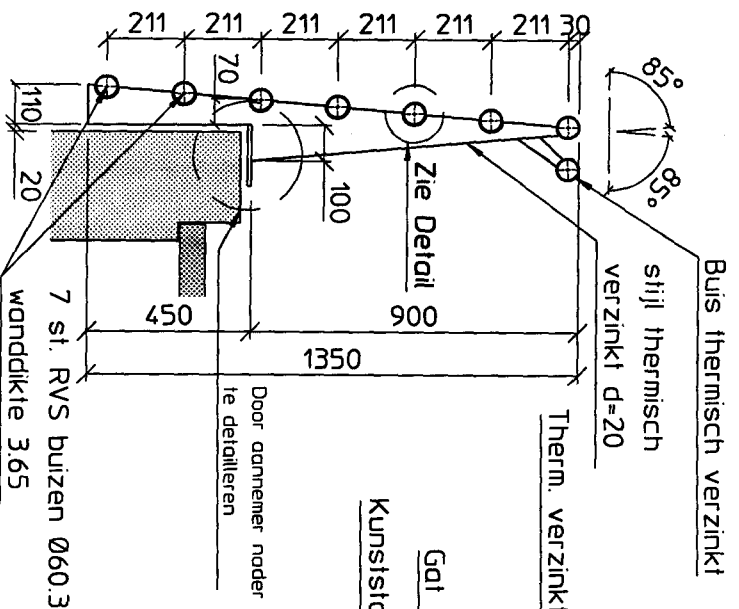


Detail

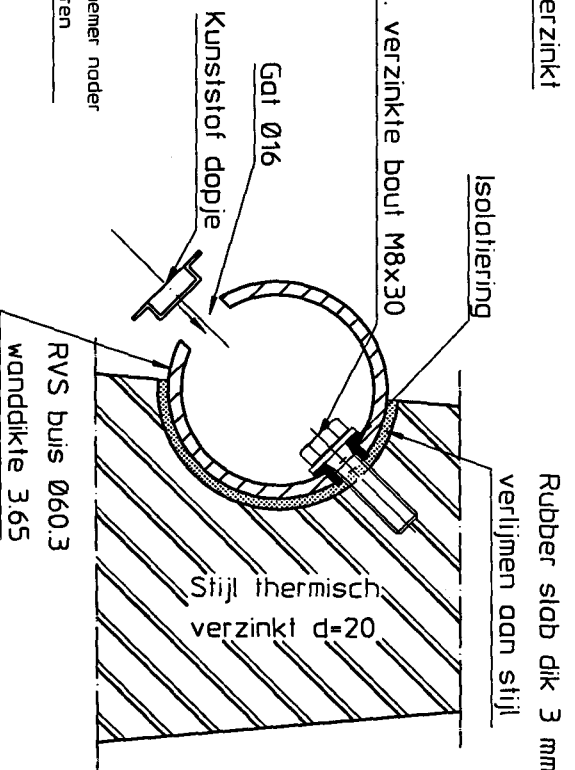



Doorsnede hek

naam/paraf	datum	Leuning type 1	
getekend V. Winkelaar	280998		
gecontroleerd P. Scholten	25-11-91		
goedgekeurd H. SCHURMAN	01.12.98		



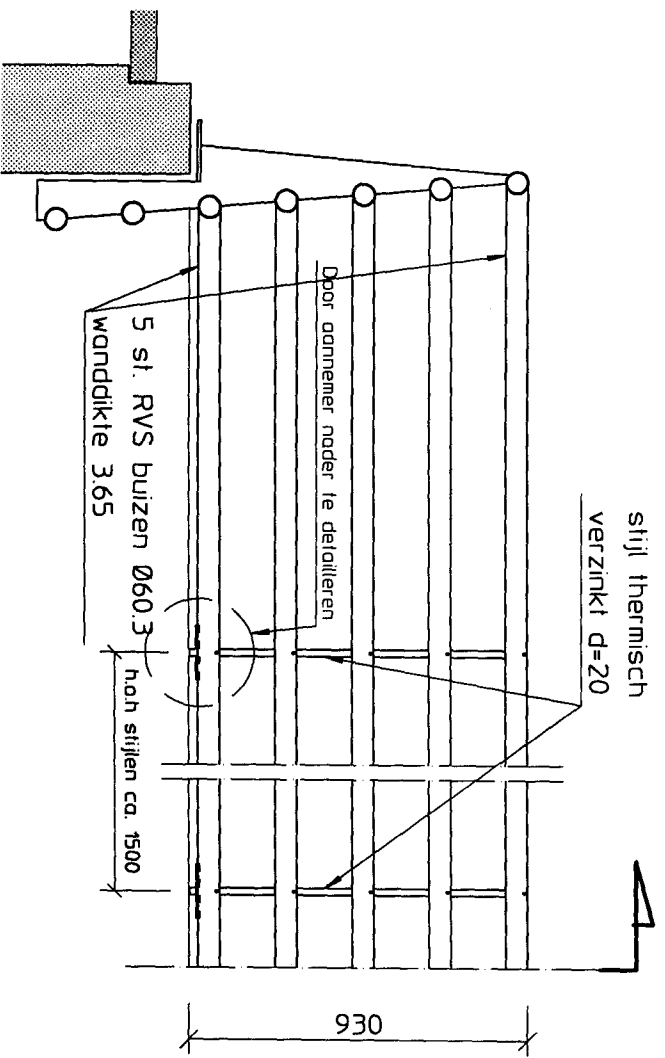

Aanzicht hek

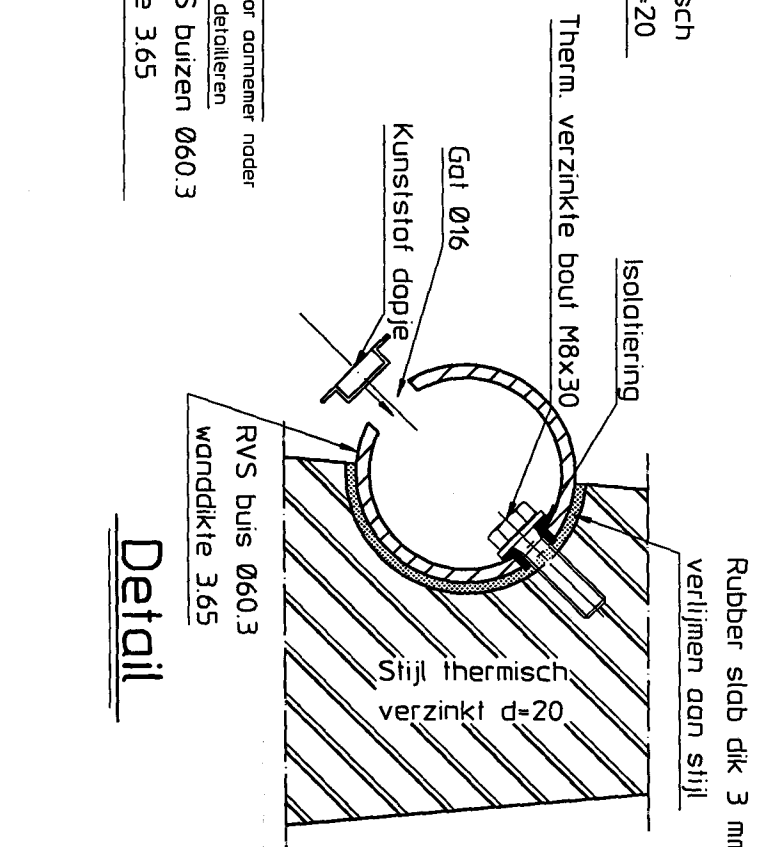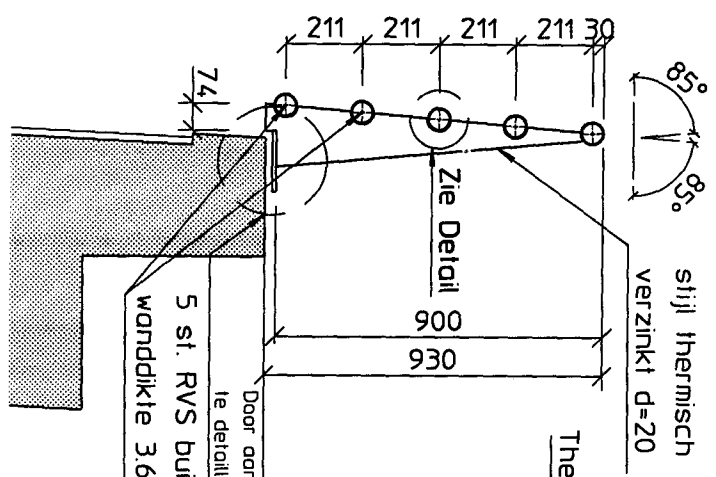


Detail

Doorsnede hek


naam/paraaf	datum
V. Winkelaar	290998
gecontroleerd P. Scholten	25-11-91
goedgekeurd H. SCHURMAN	1. sch. 20-12-98

Leuning type 2

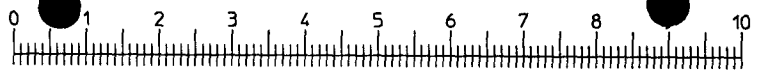


geleidend	nodm/portaal	datum
V. Winkelhaar	08/10/98	
gecontroleerd	P. Scholten	25-11-98
goedgekeurd	HOOFD TECHNIEK H. SCHURMAN	01-12-98
New-Jersey profiel		
formaat	A4	
schaal	div.	
uitgave	A	


- opmerkingen:
- Langswaapening in het New Jersey-profiel $\phi 12-80$
 - Elementen t.p.v. tunnelerende hebben verloopende hoogte

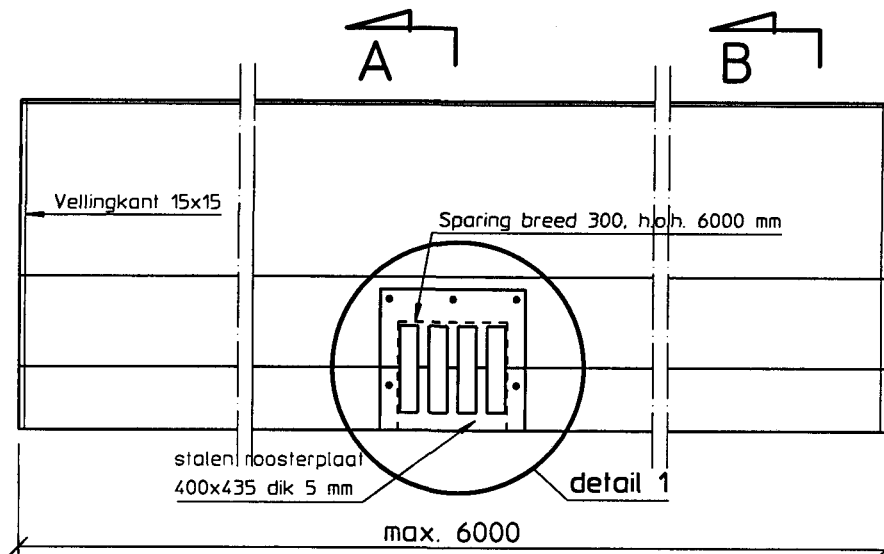


Aanzicht New-Jersey

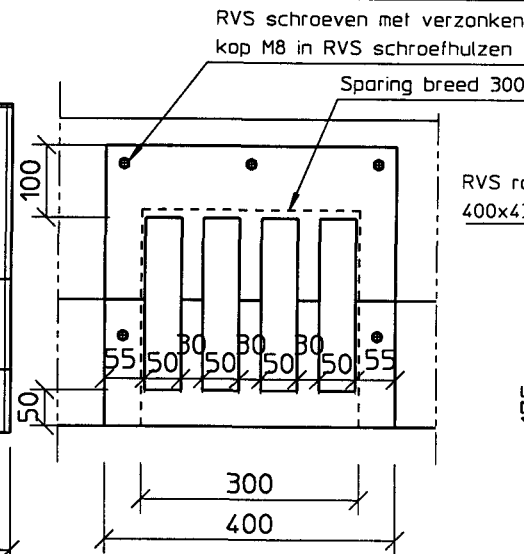

Detail 1

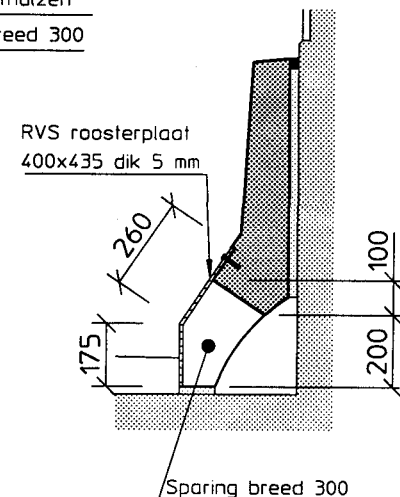


Doorsnede A


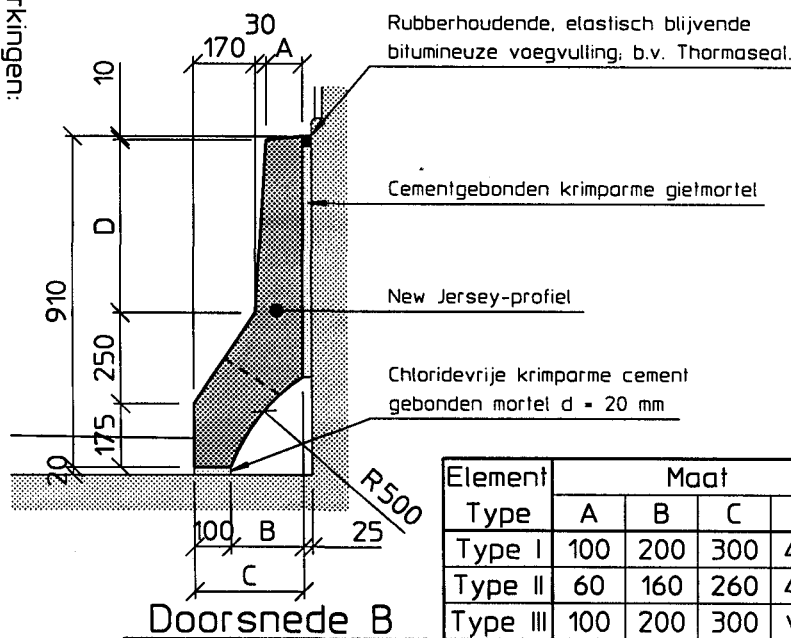


Doorsnede B

Element Type	Maat			
	A	B	C	D
Type I	100	200	300	475
Type II	60	160	260	475
Type III	100	200	300	var

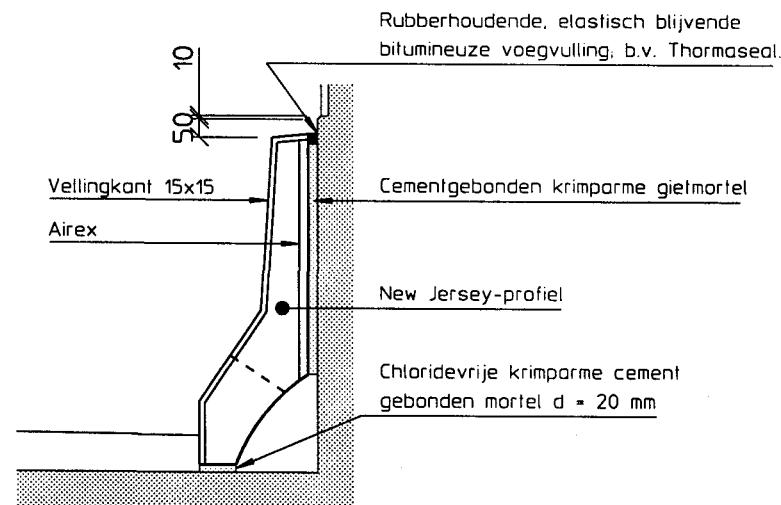

Doorsnede t.p.v. voeg

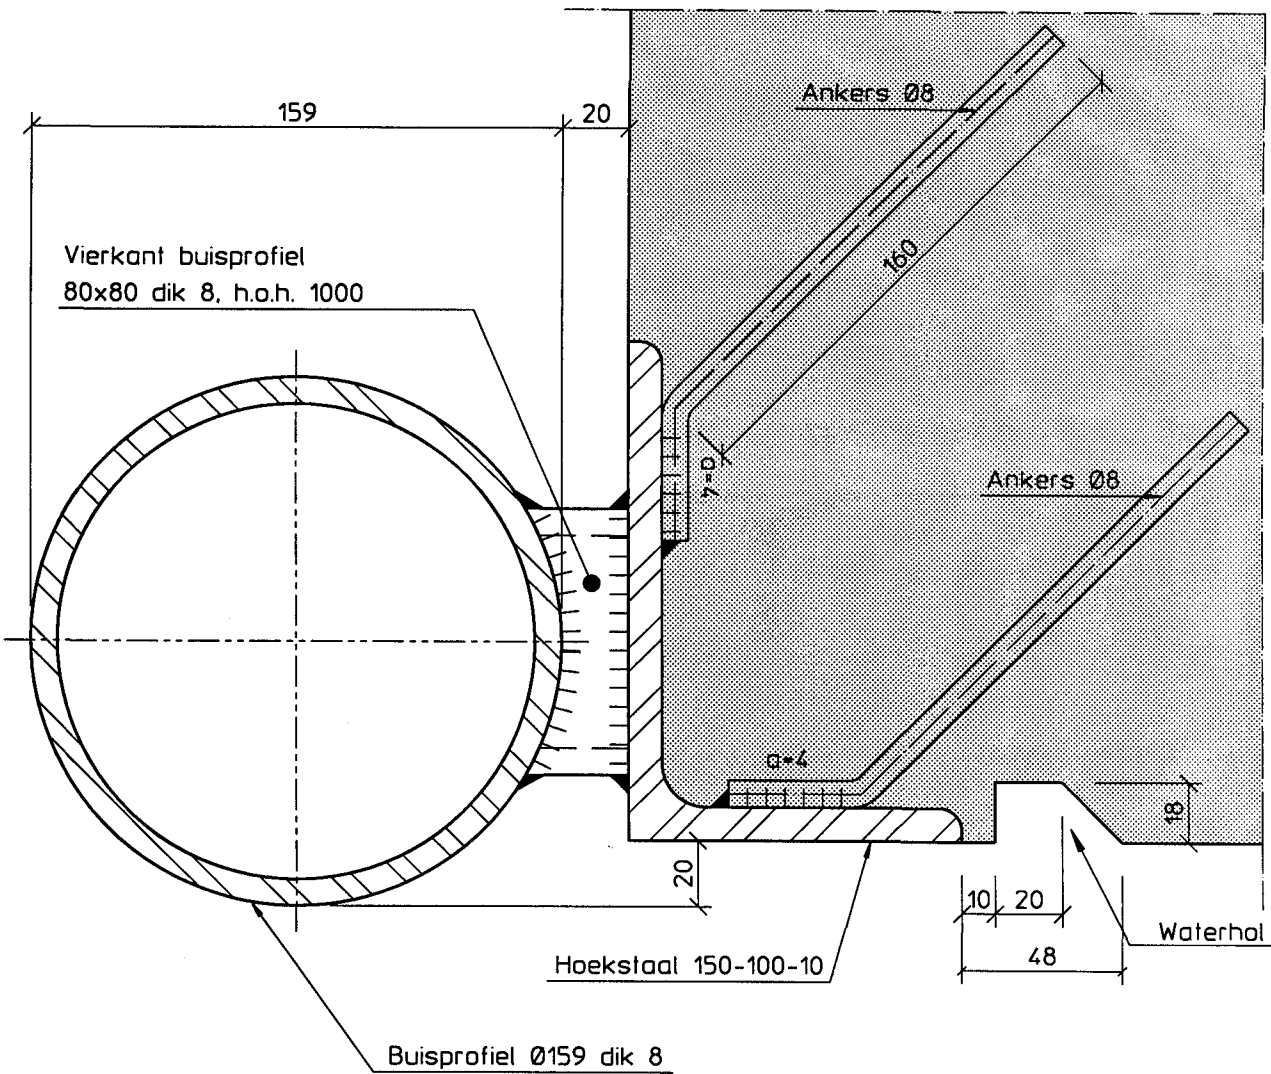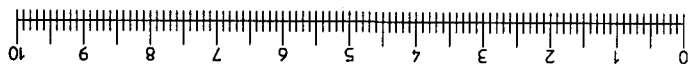

aanrijdijzer: - thermisch verzinkt kwaliteit S 235 JR

Conservering:

aanrijdijzer: Th. verzinkt

ankers : Th. verzinkt

ankers: - 2 rijen Ø8 mm S 235 JR

Hoeveelheden:


ankers : 5 stuks/m¹

- onwikkelde lengte 220 mm

- ankers vastlassen h.o.h. 400 mm (a=4mm)

- de ankerrijen verspringend t.o.v. elkaar

naam/porroef	datum	Aanrijdijzer en waterhol		formaat	A4
getekend	R.C. van Diepen			schaal	1:2
gecontroleerd	P. Scholten	25-4-91		uitgave	
goedgekeurd	HOOFD TECHNIEK	1-5-91			
	H. SCHURMAN	10-12-91			

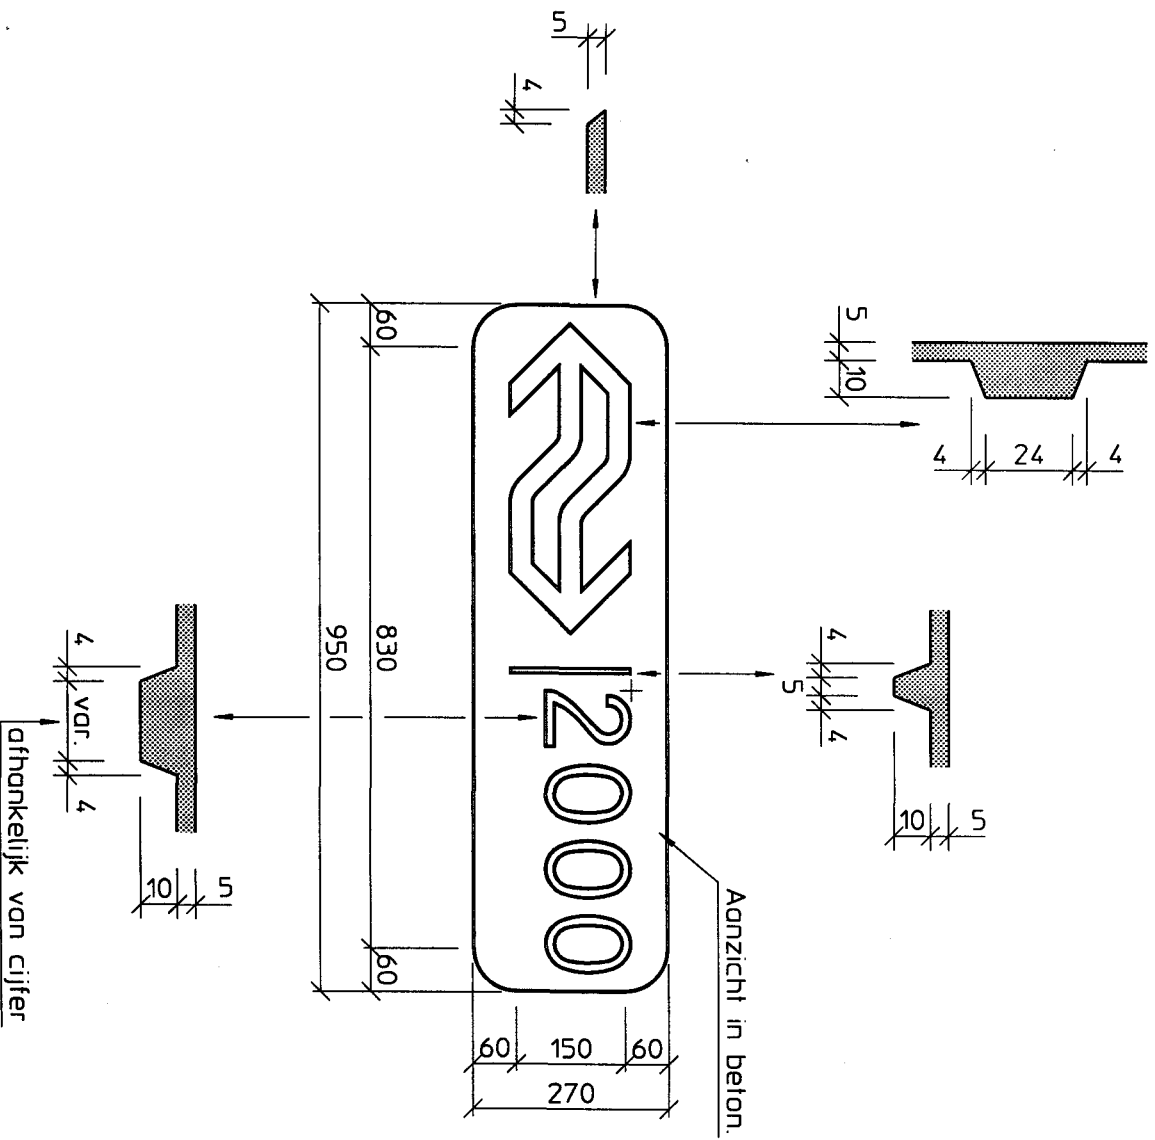

Huismerk N.S. met jaartal uitvoeren in
rubbermalbekisting

Maten in mm


Tekening. schaal 1 : 1 op aanvraag leverbaar

	naam/paraaf	datum	Huismerk N.S. met jaartal		formaat	A4
getekend	R.C. van Diepen		Klein model		schaal	
gecontroleerd	P. Scholten	25-11-11			uitgave	
goedgekeurd	HOOED TECHNIEK H. SCHUURMAN	04-12-98				



Vakafdeling Civiele Techniek

Detail 5


Holland Railconsult

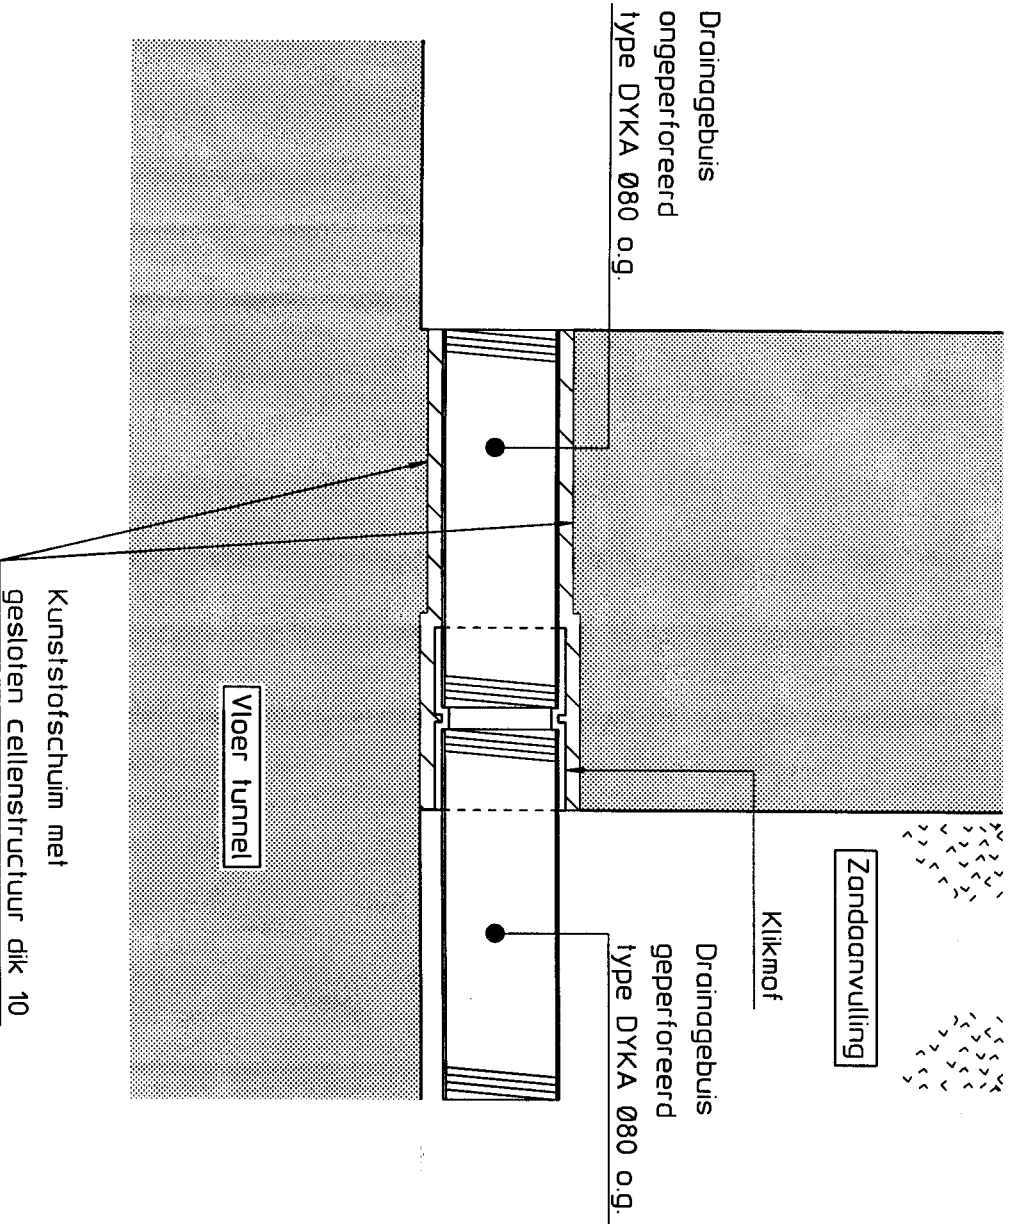


	naam/paraaf	datum	Doorvoer t.b.v. drainagebuis				formaat	A4
getekend	R.C. van Diepen						schaal	
gecontroleerd	P. Scholten	25-11-98					uitgave	
goedgekeurd	HOOFD TECHNIEK H. SCHURMAN	9.5.98 01.12.98						

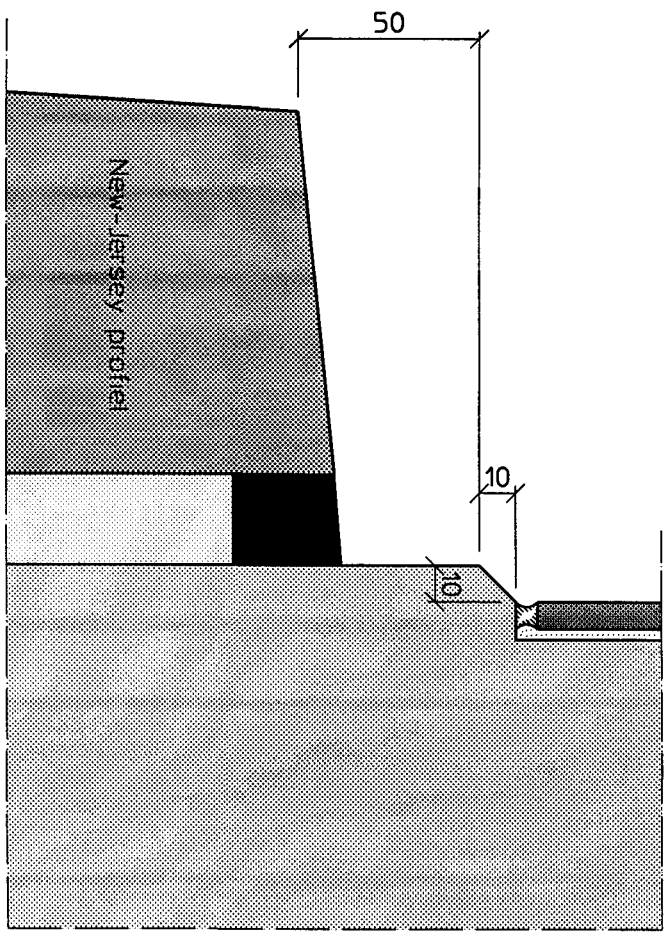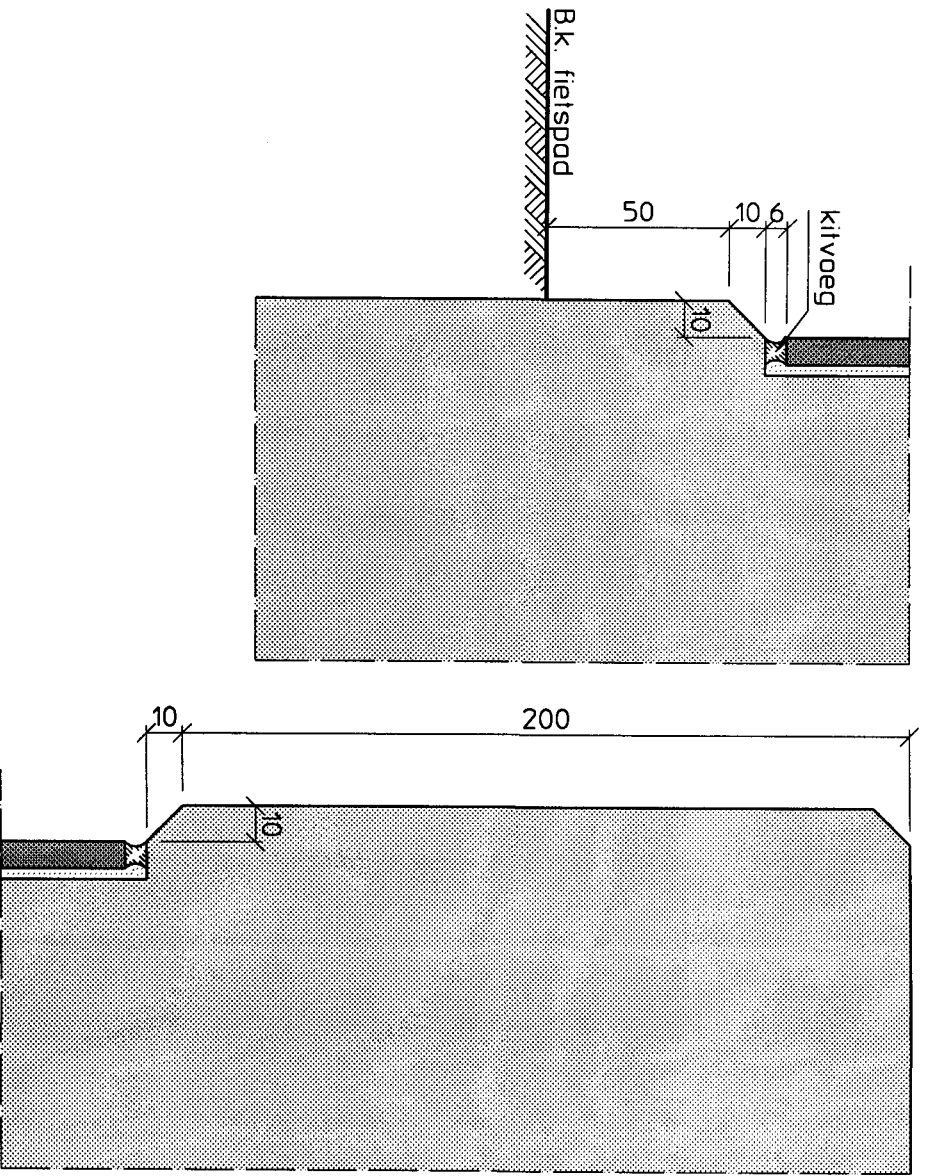

	naam/paraaf	datum	Uitvoering omranding tegelwerk			
getekend	V. Winkelbaar	30-11-98				
gecontroleerd	P. Scholten	30-11-98				
goedgekeurd	HOOFD TECHNIEK H. SCHURMAN	12.12.98				
			formaat	A4		
			school			
			uitgave			
			1			

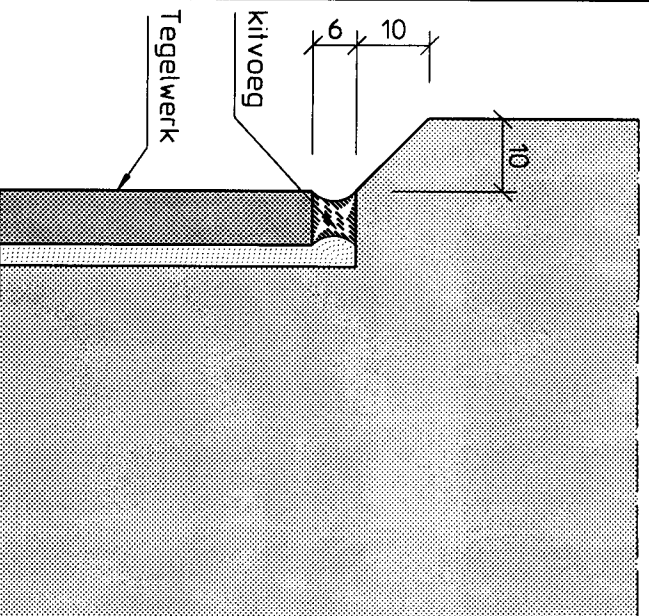


Doorsnede spiegels

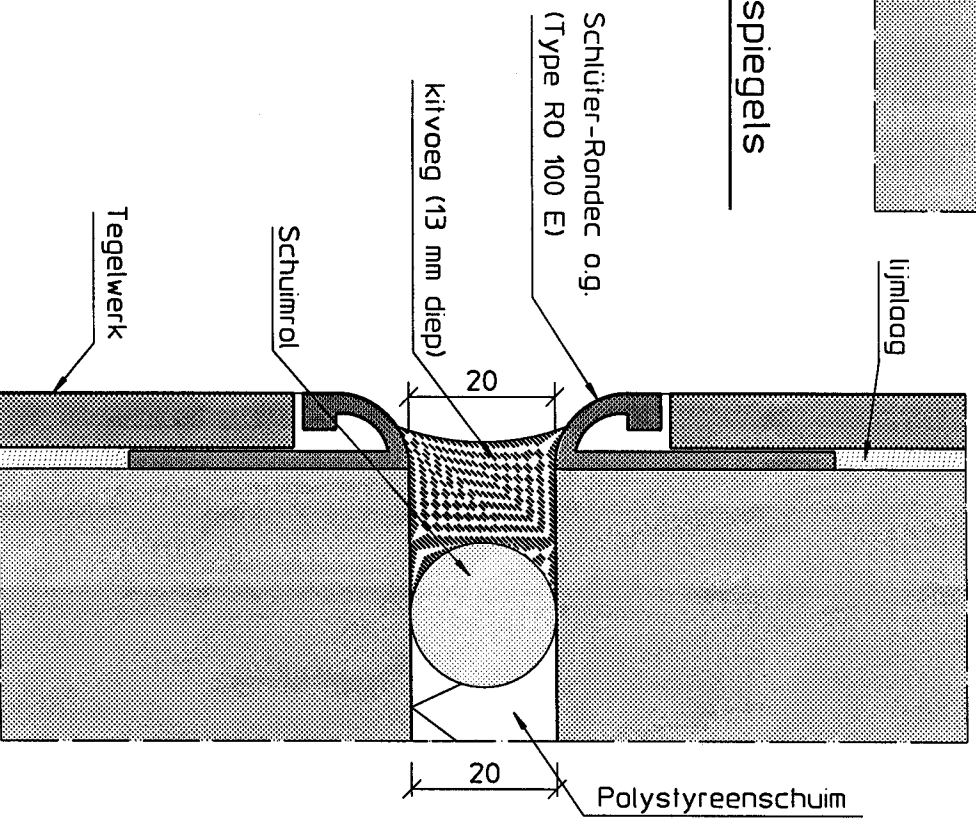


Doorsnede voegen

naam/paraaf	datum	formaat	A4
V. Winkelaar	25-11-98	schaal	
gecontroleerd	P. Scholten	uitgave	1
goedgekeurd	HOOED TECHNIEK		
	H. SCHURMAN		


Tegelwerk in spiegels
en t.p.v. voegen

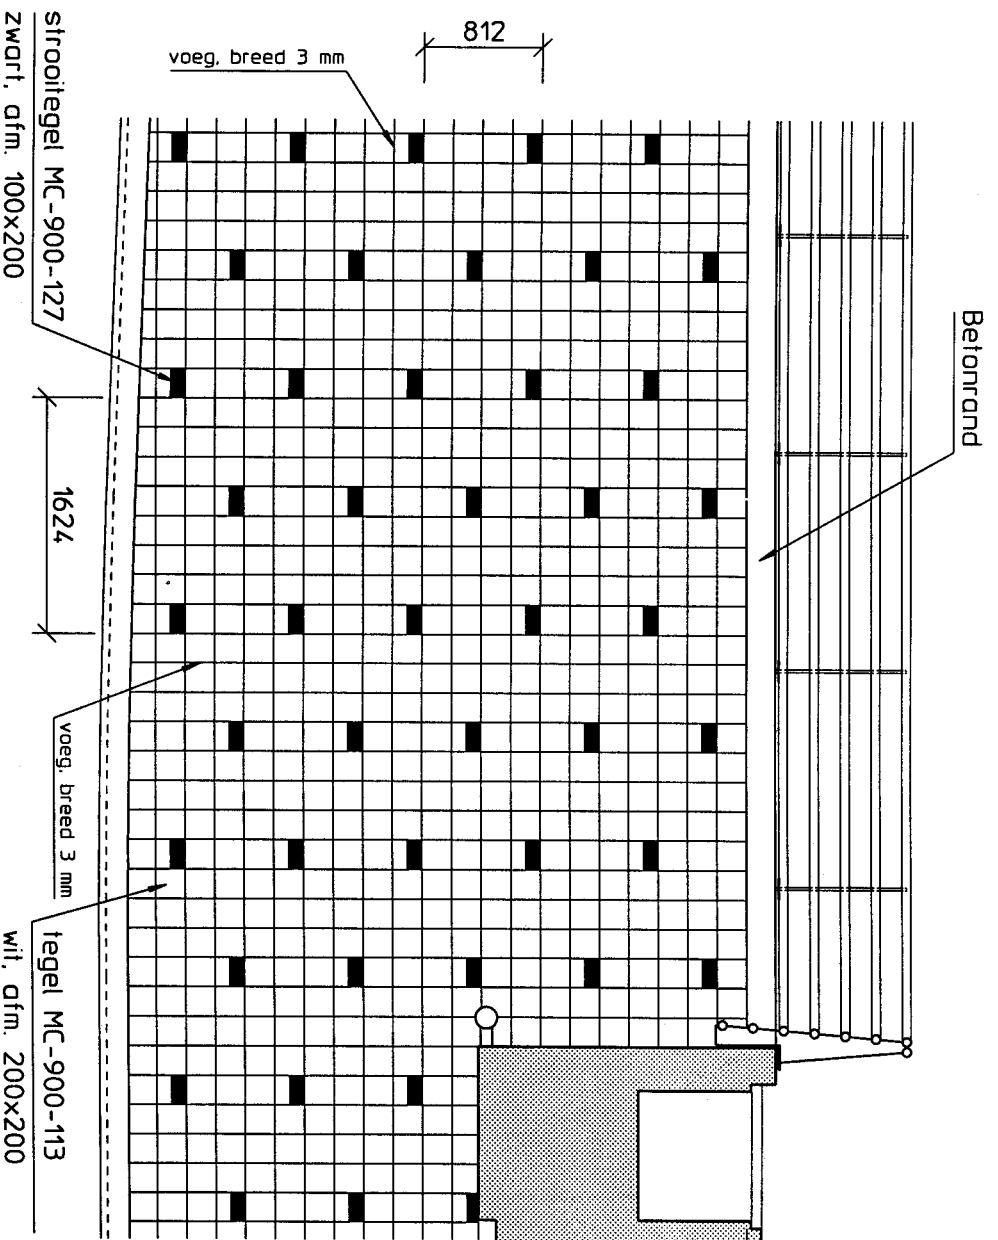

	naam/parooaf	datum	Patroon tegelwerk				formaat	A4
getekend	V. Winkelaar	23-09-'98					school	150
gecontroleerd	P. Scholten	25-11-98					uitgave	
goedgekeurd	HOOFD TECHNIEK H. SCHUURMAN	1.5.98						

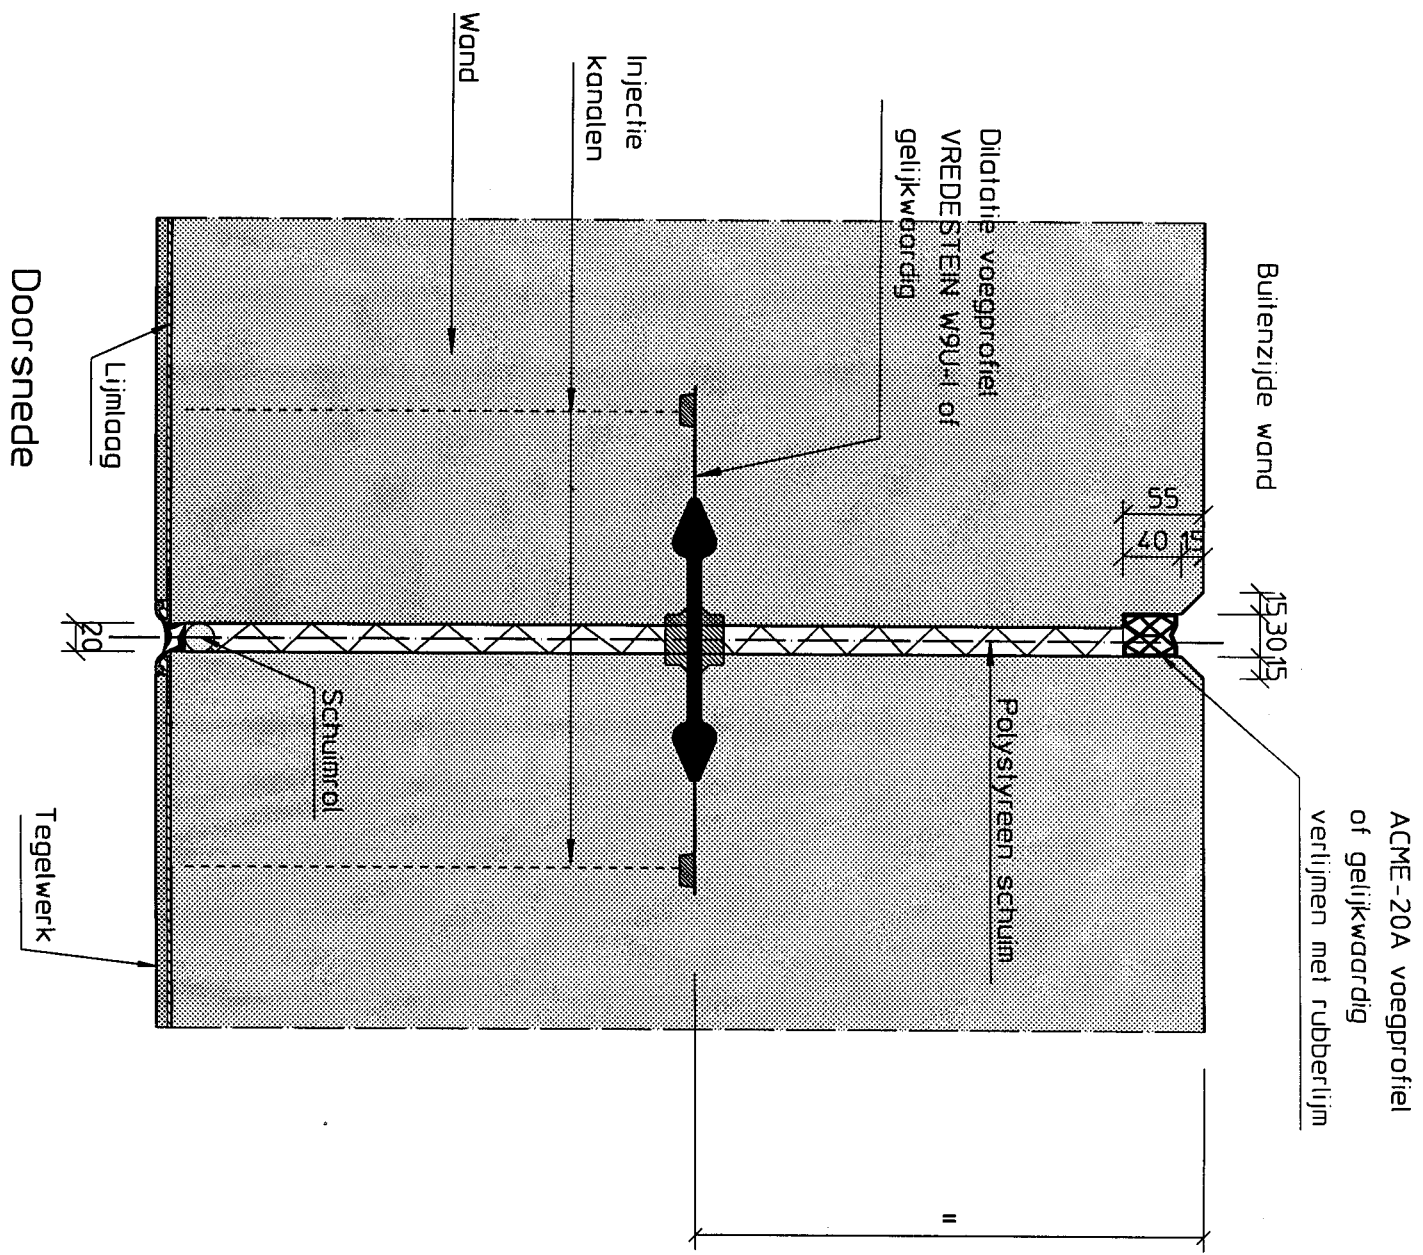

	naam/parooi	datum	Dilatatievoeg tunnelwand				formaat	A4
getekend	V. Winkelaar	30-11-98					schoon	
gecontroleerd	P. Scholten	30-11-98					uitgave	
goedgekeurd	HOOFD TECHNIEK H. SCHURMAN	02-12-98					A	

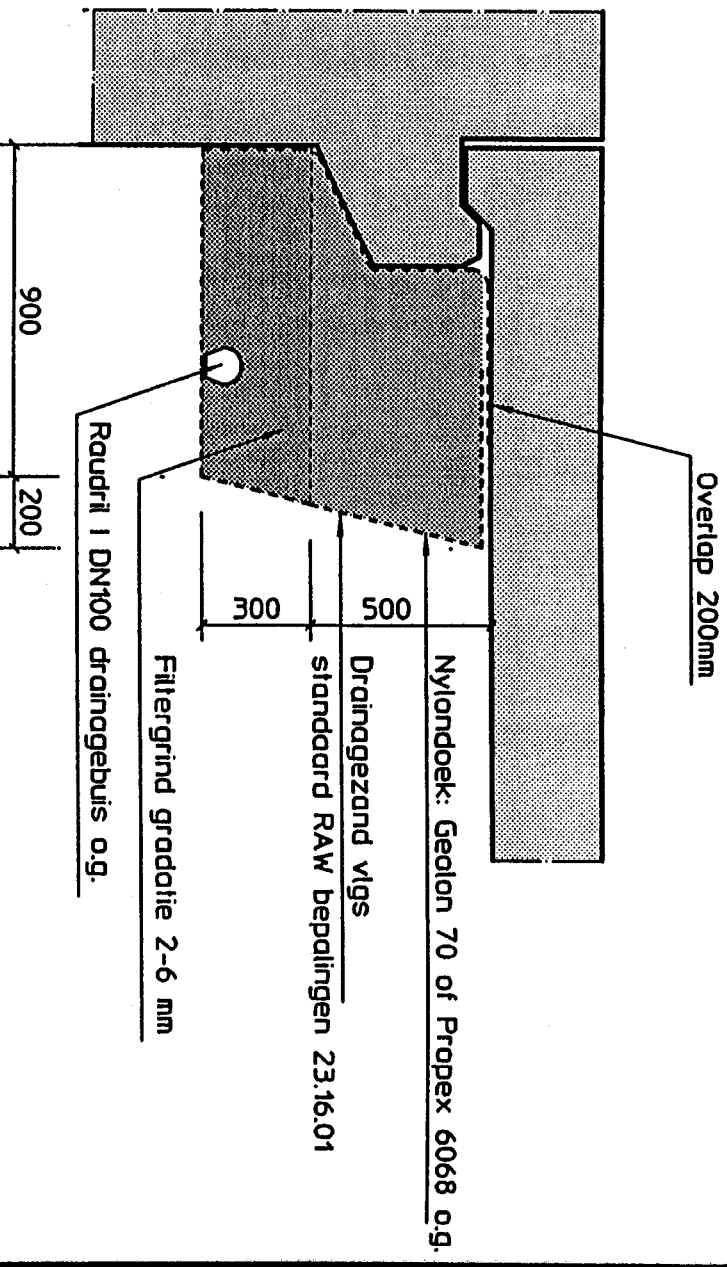

DOORSNEDE

Hoeveelheid bouwstoffen per mt:

- Nylandoek: ca. 3.3 m²/m¹
- Drainagezand: ca. 0.4 m³
- filtergrind: ca. 0.3 m³
- 1 m RAUDRIL 1 DN100 drainagebuis

	naam/portaal	datum	Drainage kunstwerk tpv de overgangsplaten			
geleend	H.J. BOSMAN	01-08-96				
geconroleerd	H. SCHURMAN	03-08-96				
goedgekeurd	HOOFD TECHNIEK GMH. TONM.	<i>AN 18/96</i>				
			formaat	A4		
			schaal	1:20		
			uitgave			

Holland Railconsult


Vakafdeling Civiele Techniek

Standaarddetail

23

DRA

01

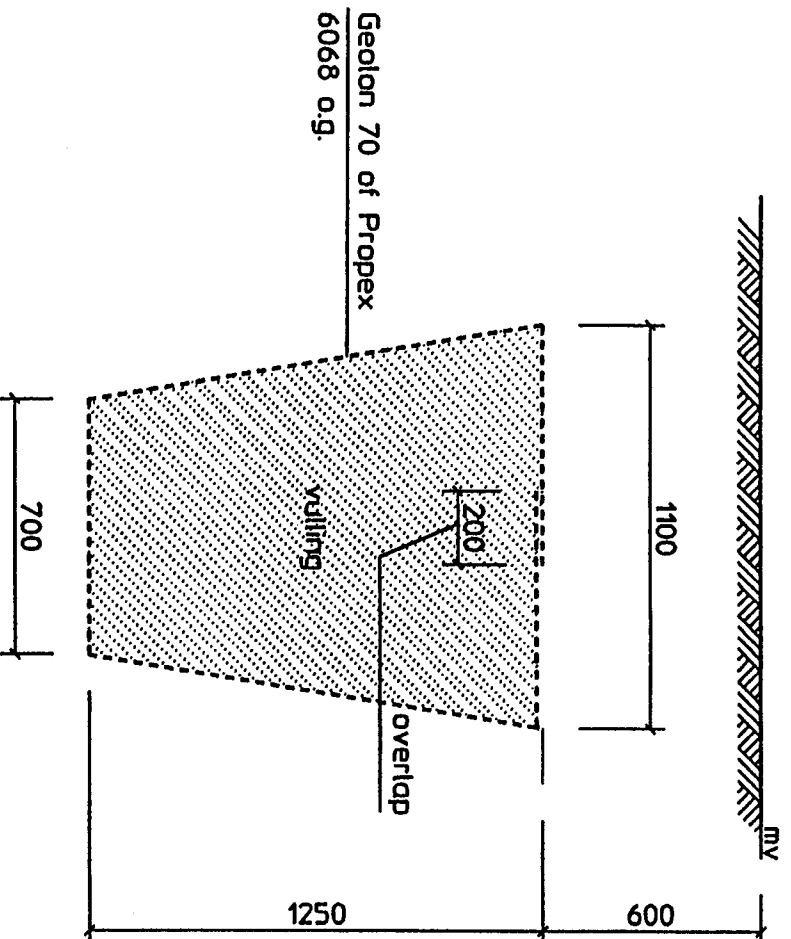

nylondoek: - Geolon 70 of Propex 6068 o.g.

vulling: - Grind nominaal 32 mm
(ca. 1 m³)

uitmonding van de aanvoerleiding
aan de bovenzijde van grindkoffer


	naam/paraf	datum	Grindkoffer inhoud ca 1m ³		(formaat)	A4
getekend	H.J. BOSMAN	01-08-96			schaal	1:20
gecontroleerd	H. SCHURMAN	01-08-96			uitgave	
geedgekeurd	HOOFD TECHNEK	01-08-96				
	GML TOUW.	01-08-96				

Holland Railconsult

Vakafdeling Civiele Techniek			
Standaarddetail	23	GRI	01

Overgangsplaten conform
42/PRE/04

Drainage conform
23/DRA/01

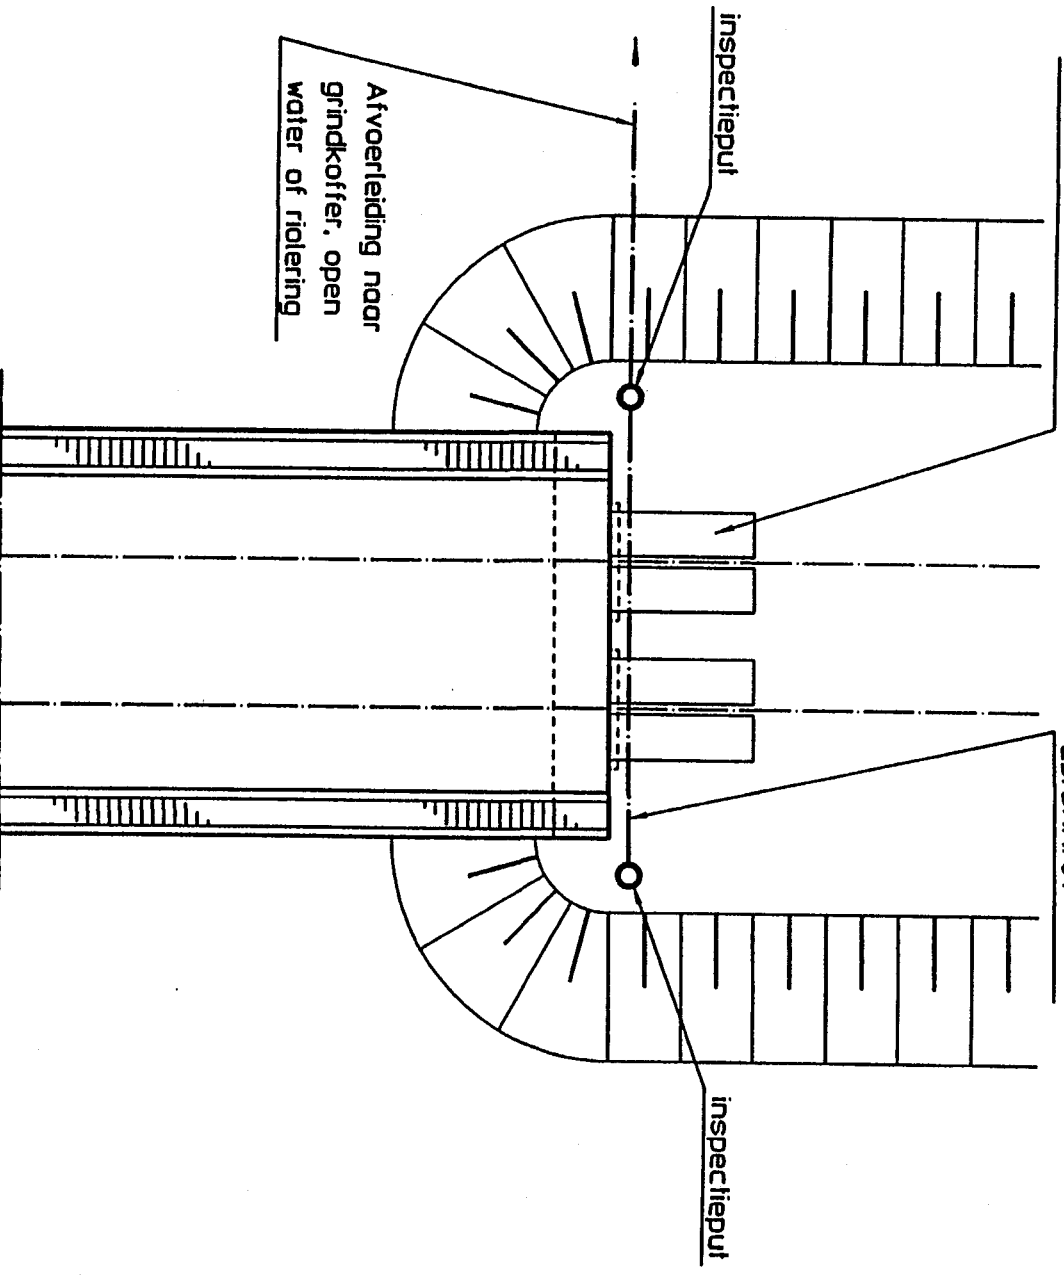

Bovenaanzicht

Inspectieput:


- put: -inwendige middellijn 600 mm
- fabr. Dyka of gelijkwaardig.
- put voorzien van een vlakke bodem met stroomprofiel en de benodigde aansluitingen.
- puthoogte ca. 2000 mm.
- b.k. put is 0.50m.- B.S.

deksel: put aan de bovenzijde voorzien van een betonnen opzetrand met gelijkzereen putdeksel, fabr TBS type 313 of gelijkwaardig.


	naam/paraaf	datum	Inspectieput		formaat	A4
geleidend	H.L. BOSMAN	01-08-96			school	120
gecontroleerd	H. SCHURMAN	01-08-96			uitgave	
goedgekeurd	HOOFD TECHNIEK G.M. TOOM	01/08/96				

Holland Railconsult

Vakafdeling Civiele Techniek			
Standaarddetail	23	ISP	01

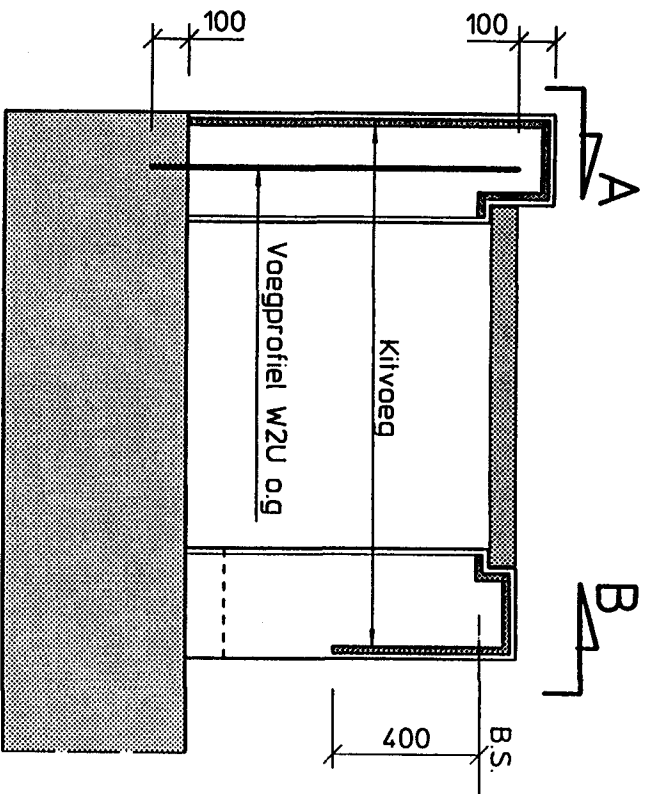


Doorsnede

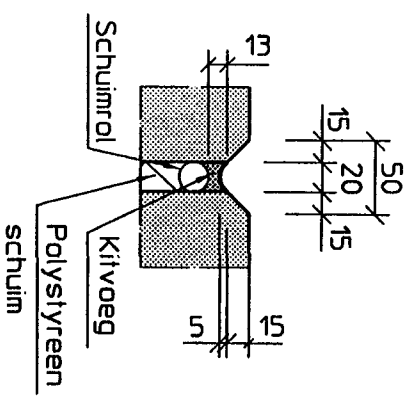


Detail kitvoeg

Voegprofiel W2U o.g

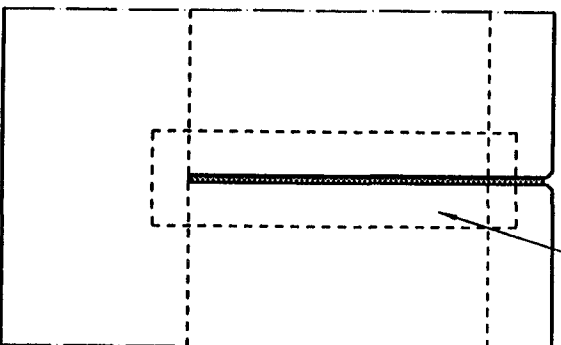

Aanzicht A

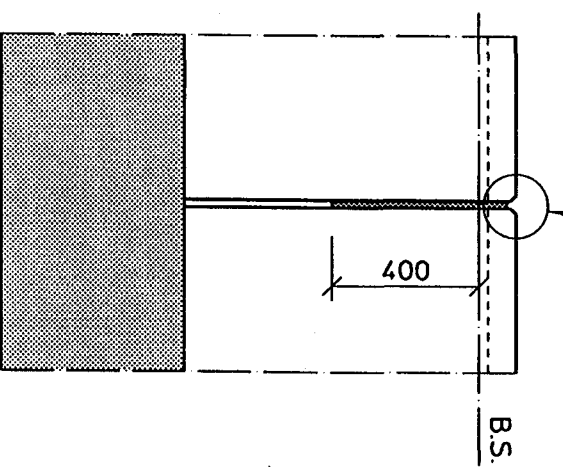

Aanzicht B

	naam/paraf	datum	Voegafdichting kabelkoker		
getekend	H.J. BOSMAN	Nov '97			
gecontroleerd	H. SCHURMAN	Nov '97			
goedgekeurd	HOOFD TECHNIEK J.H. JONKER	<i>[Signature]</i>			
			Vakafdeling Civiele Techniek		
			formaat	A4	
			schaal	1:20	
			uitgave		
			A		


Holland Railconsult

Standaarddetail	4.2	DIL	02
-----------------	-----	-----	----


naam/paraaf	datum
H.J. BOSMAN	Nov '97
H. SCHURMAN	Nov '97
gecontroleerd	
gecontroleerd	
goedgekeurd	
J.H. JONKER.	

Overgangsplaat t.b.v. wegverkeer

formaat	A4
schaal	DIV
uitgave	
A	

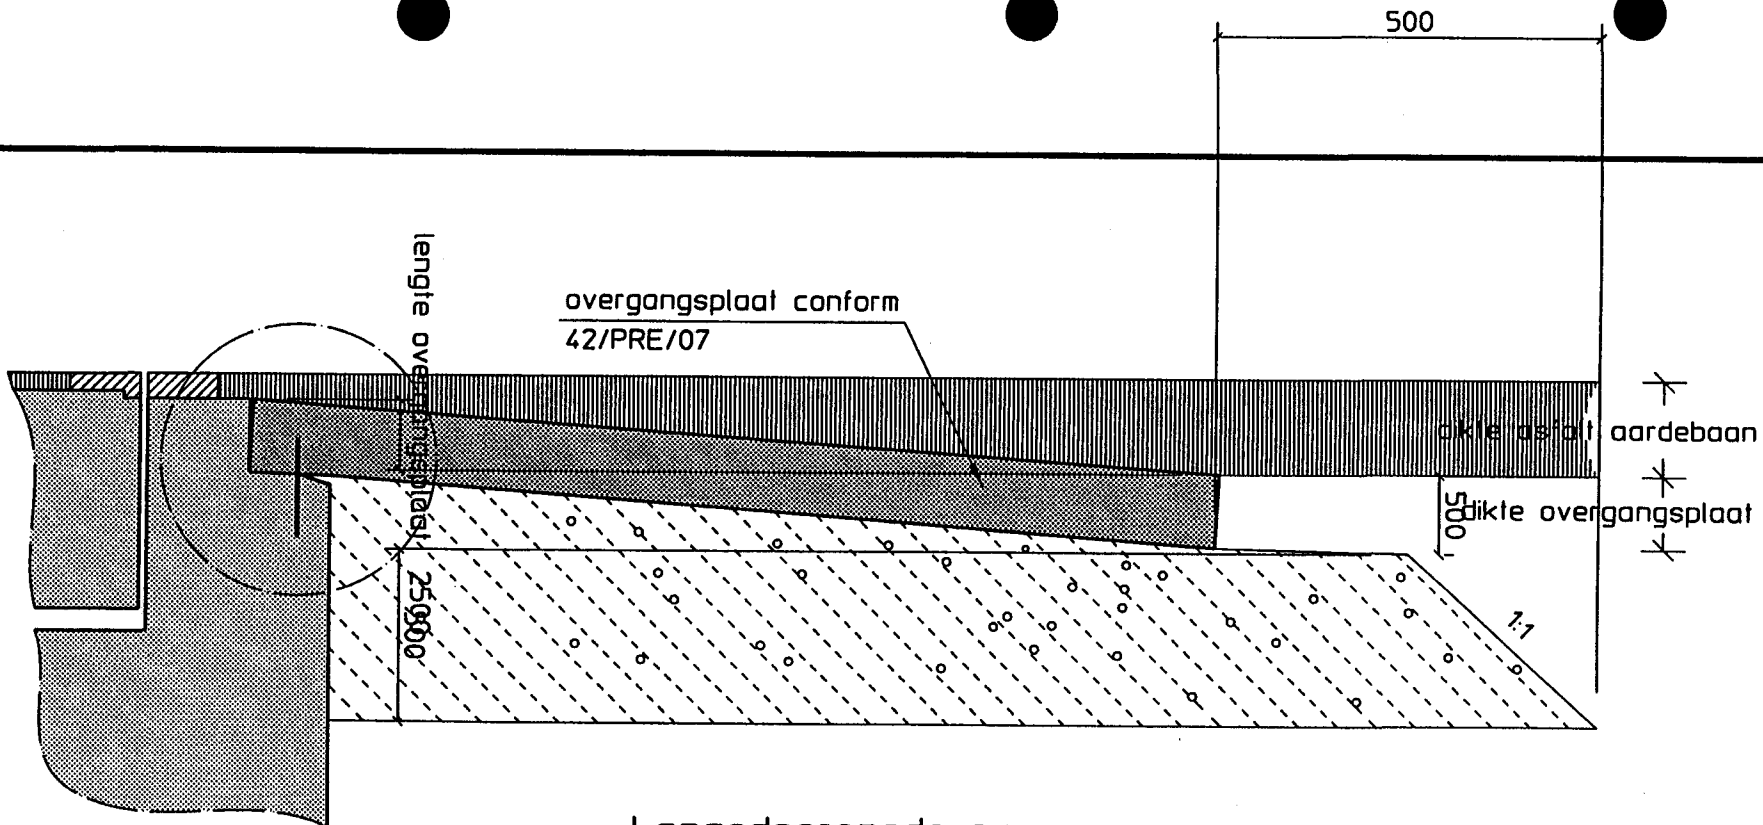

Langsdoorsnede Schaal 1:20

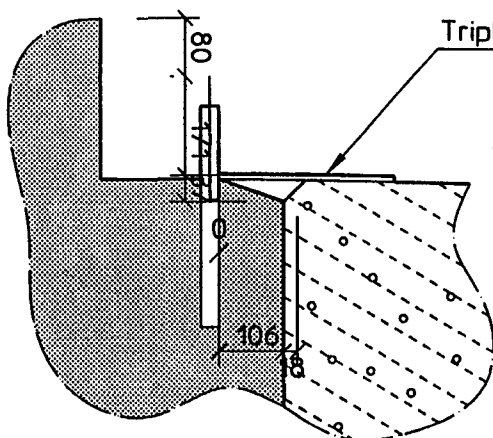


Triplex dik 4 mm incl. plakfolie dik 0.3 mm


Detail oplegging overgangsplaat Schaal 1:10

Hoeveelheden:
Gestabiliseerd zand: 1.75 m3/m1


Verklaring		Maten in mm
- RVS doek AISI 304 (1.4301), ø25 hoh 800 mm Over een lengte van 130 mm omwikkelen Met densoband		- Voegovergang
- Triplex dik 4 mm incl. plakfolie dik 0.3 mm		- Asfaltconstructie
- Overgangsplaat		- Gestabiliseerd zand 175 kg cement/m3

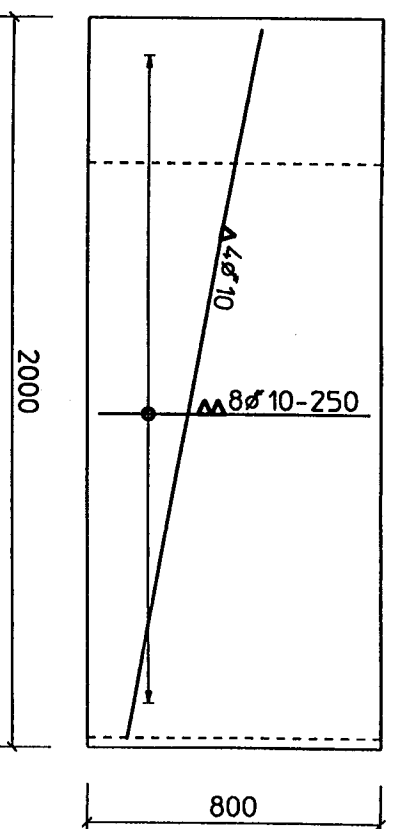

Bovenaanzicht

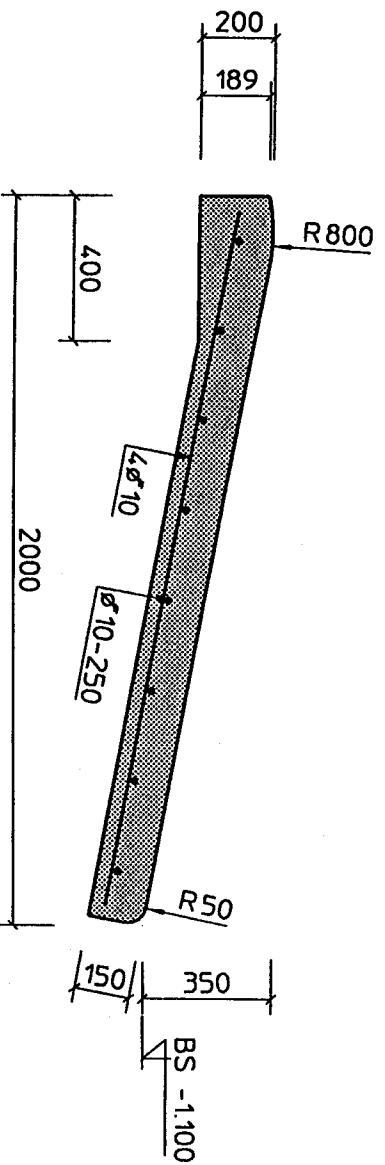

Langsdoorsnede

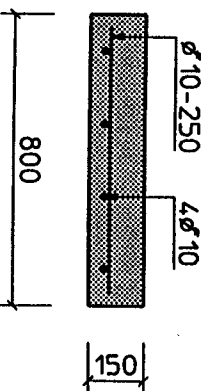

Dwarsdoorsnede

betonslaai: - FeB 500 NEN 6008
beton: - sterkteklasse B 25
- milieuklasse 5b
- cementsoort: CEM I
- dekking 30 mm

Hoeveelheden:
beton: 0.25 m³
betonslaai: 8.8 kg

naam/por:naam	datum	Kabelovergangsplaat bij kunstwerk met doorgaand ballastbed			
geleidend	H.J. BOSMAN	Nov '97			
gecontroleerd	H. SCHUURMAN	Nov '97			
goedgekeurd	HOOFD TECHNIEK J.H. JONKER				



Holland Railconsult

Vakafdeling Civiele Techniek			
Standaarddetail	42	PRE	02

Overgangsplaat in het spoor


naam/paraf	datum
H.J. BOSMAN	Nov '97
H. SCHURMAN	Nov '97
gecontroleerd	
goedgekeurd	
HOOFD TECHNIEK	
J.H. JONKER	


formaat	schaal	uitgave
A4	1:20	

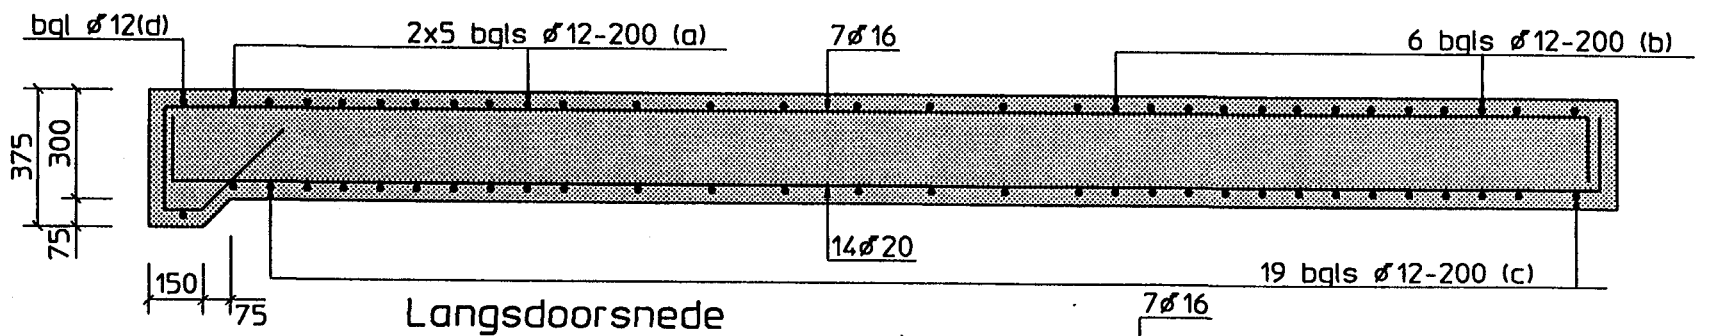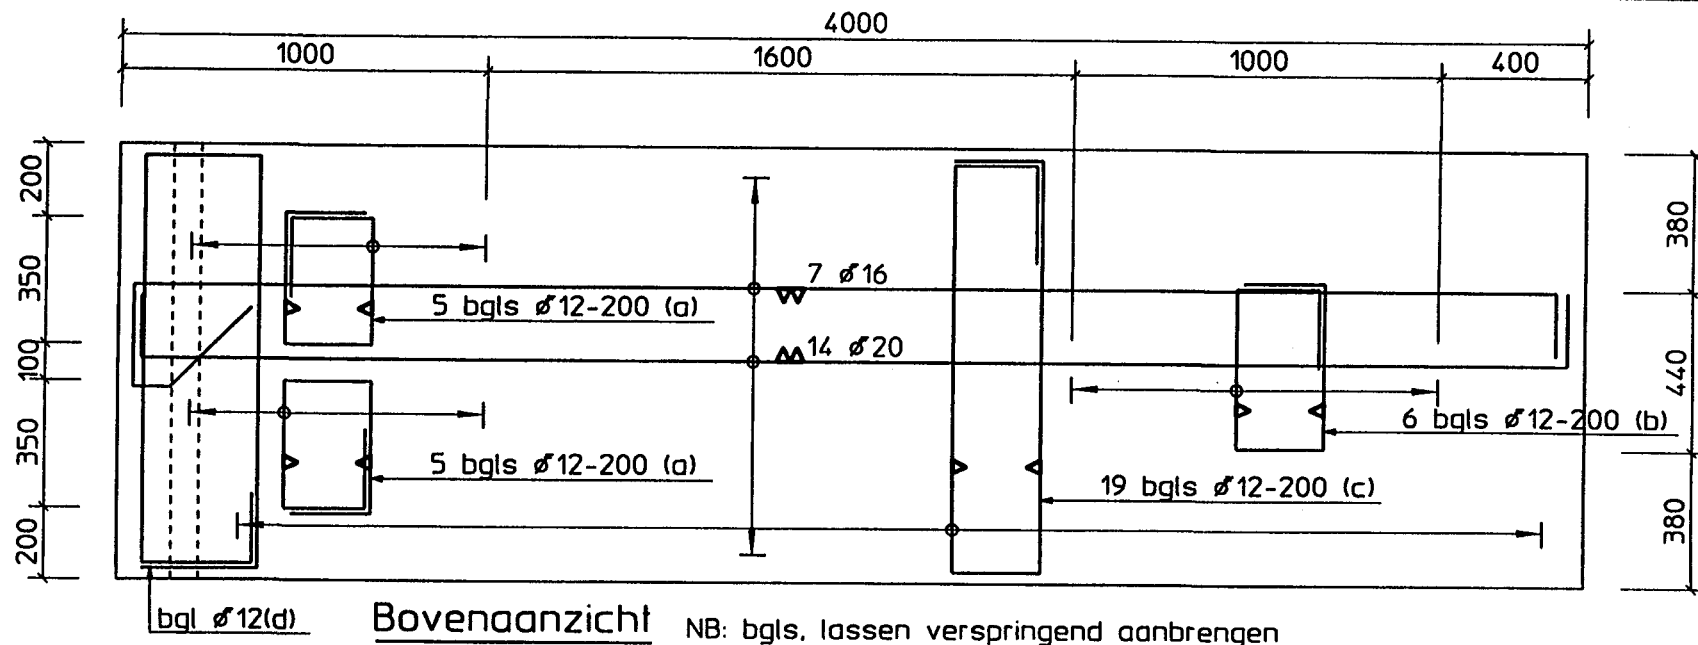


- betonstaal: - FeB 500 HWL/HK NEN 6008
 beton: - sterkteklasse B 35
 - milieuklasse Sb
 - Hoogovencement CEM I of CEM III
 - dekking 35 mm

Hoeveelheden:
 beton: 1.5 m³
 betonstaal: 280 kg

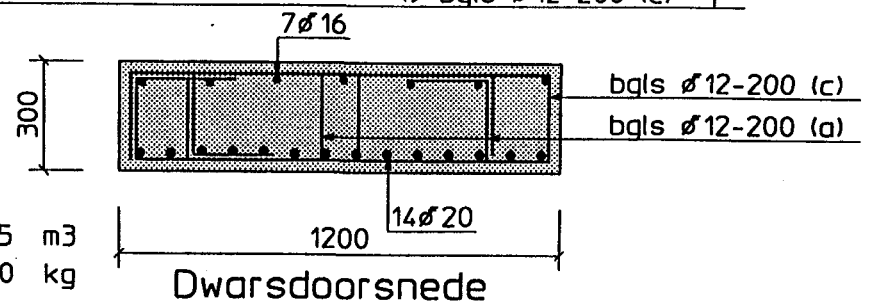


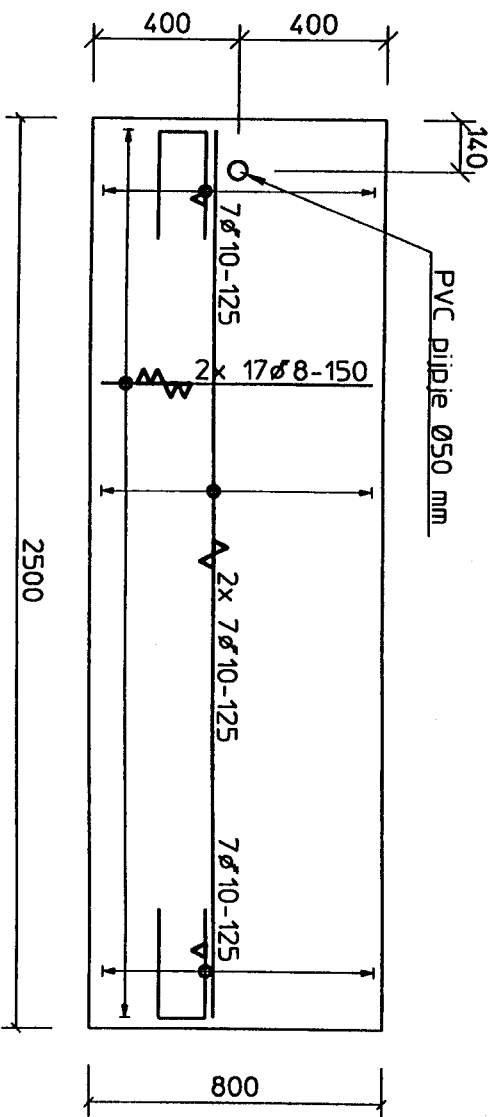

Bovenaanzicht

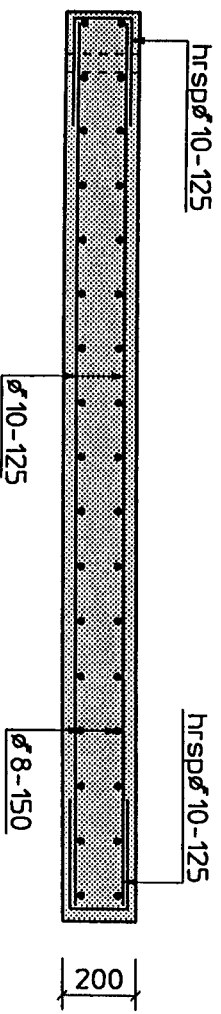

Langsdoorsnede

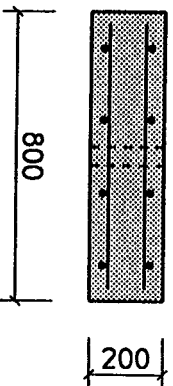


Dwarsdoorsnede


Betonstaal: - FEB 500 HWL of HK /NEN 6008
 Beton: - sterkteklasse B 35
 - milieuklasse 3
 - cementsoort: CEM I
 - dekking 35 mm

Hoeveelheden:
 beton: 0,4 m³
 betonstaal: 43,0 kg

	naam/portaal	datum	Overgangsplaat t.b.v. wegverkeer			
geleend	J. HAARSSMA	Nov '97	formaat	A4		
gecontroleerd	H. SCHURMAN	Nov '97	schaal	1:20		
goedgekeurd	HOOFD TECHNIK J.H. JONKER.		uitgave			

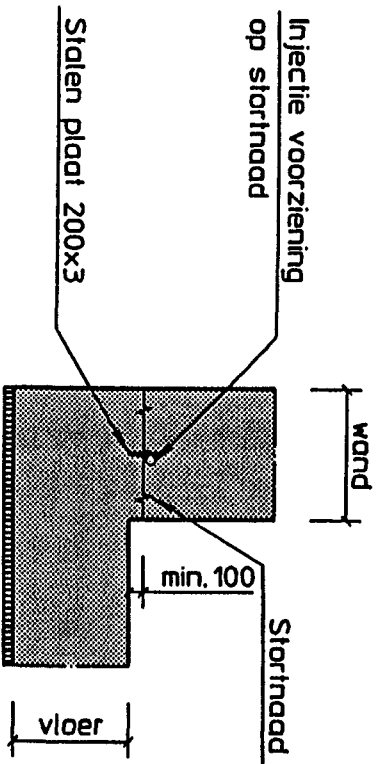

Doorsnede
Stortnaad vloer/wand

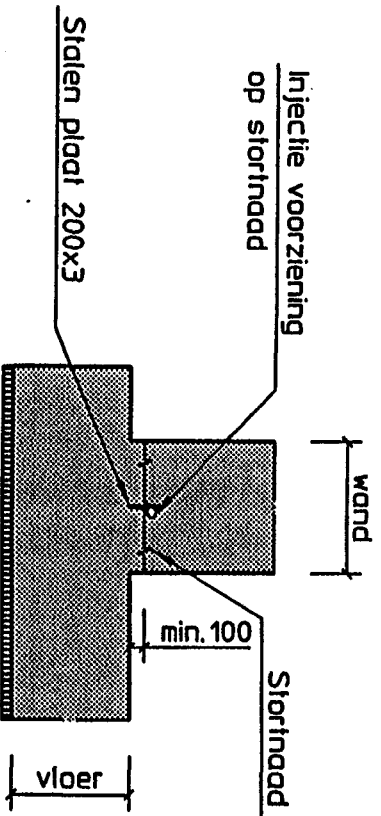

Doorsnede
Stortnaad vloer/wand

Conservering:

plaat: Th. verzinkt


Hoeveelheden:

plaat: 200x3 4.72 kg/m¹

	naam/paraaf	datum	Stortnaad vloer/wand		formaat	A4
geleend	H.J. BOSMAN	01-08-96			school	150
gecontroleerd	H. SCHURMAN	01-08-96			afgave	
goedgekeurd	HOOFD TECHNIEK J.H. JONKER					


Holland Railconsult

Vakafdeling Civiele Techniek			
Standaarddetail	42	STR	01

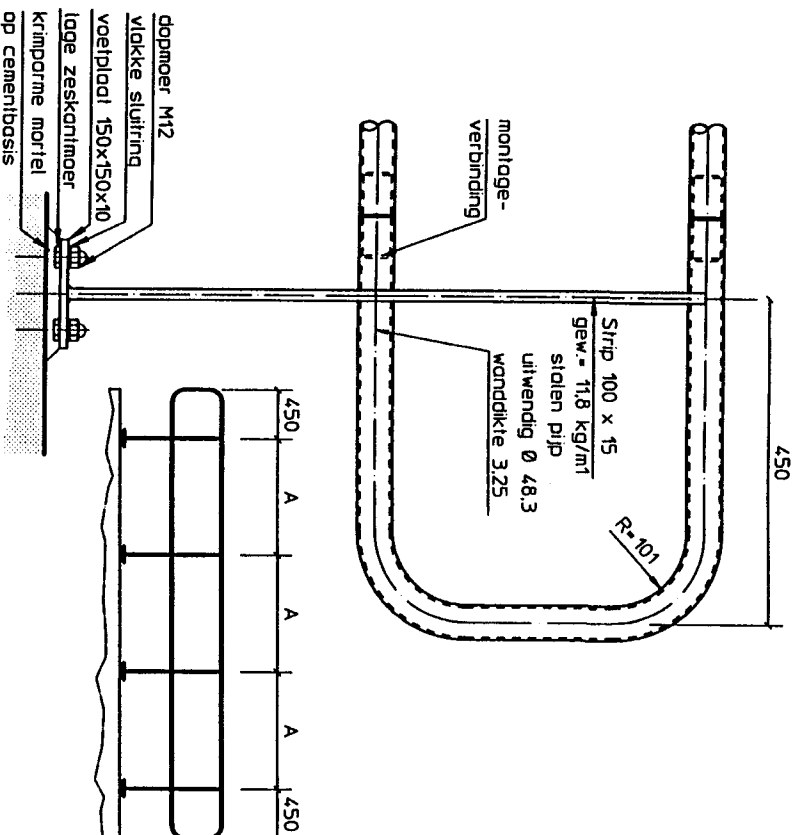

Aanzicht

Schaal 1:10

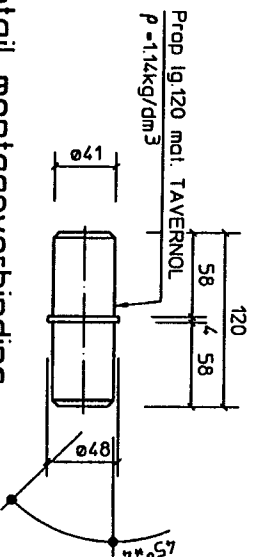

Detail montageverbinding

Schaal 1:5



(h.o.h. max. 5 m).

onderdeel	diam	kwaliteit	norm
anker	M12	klasse 70 A2	DIN 975
lage moer	M12	klasse 70 A2	DIN 4398
dopmoer	M12	klasse 70 A2	DIN 1587
sluitring	M12	AZ	DIN 125A

alle onderdelen
rvs kwaliteit AISI 304 (1.4301)

Doorsnede

Schaal 1:10

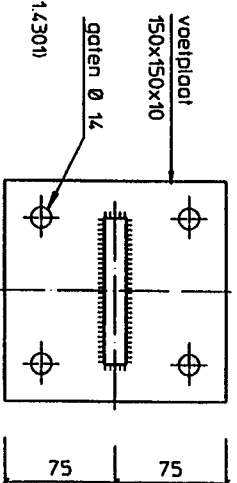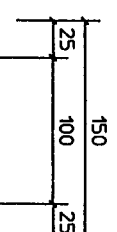

Voelpiaat

Schaal 1:5
Conservering:

regels: lh. verzinkt

stijl: lh. verzinkt

voelpiaat: lh. verzinkt

Hoevereligheden:

regels: 3,61 kg/m¹ / regel

stijl: 11,8 kg/m¹

voelpiaat: 1,8 kg/stuk

- Maatvoering in mm
- A = lengte tussen stijlen h.o.h. gemiddeld 1500 mm
- Leuning in- en uitwendig verzinken volgens NEN 1275 en NEN 1332, laagdikte 50-70 micrometer
- In alle pijpen de nodige gootjes boren i.b.v. het verzinken
- Alle lasverbindingen elektrisch lassen Δ o-a
- stalen pijp 3,61 kg/m¹


	naam/paraaf	datum	Leuning type 3		
geleend	H.J. BOSMAN	Nov '97			
gecontroleerd	H. SCHURMAN	Nov '97			
goedgekeurd	HOOFD TECHNIEK G.M.M. TOUW.	<i>SA</i>			
			formaat	A4	
			schaal	DIV	
			uitgave		
			A		

Holland Railconsult


Vakafdeling Civiele Techniek

Standaarddetail 43

LNG 07

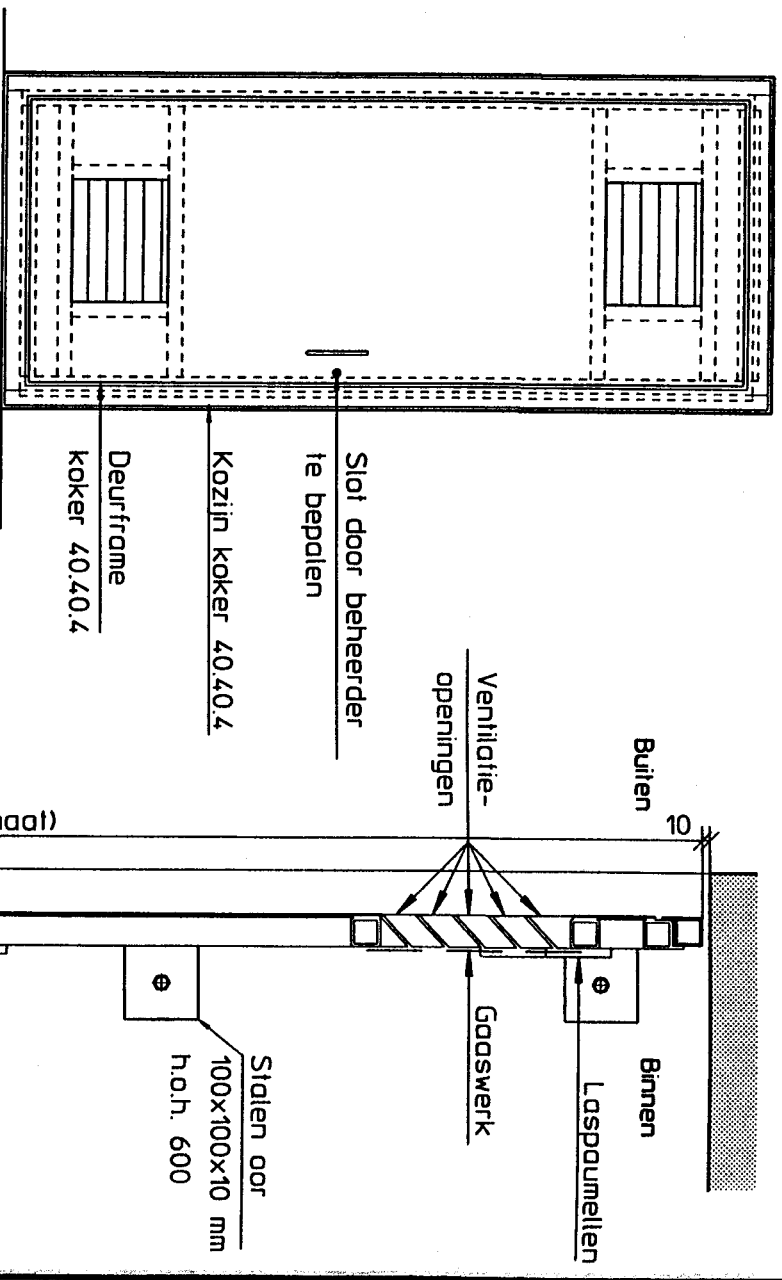


Aanzicht deur 1:20

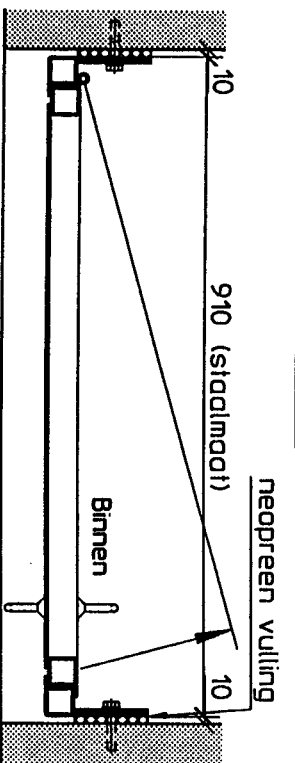

Doorsnede A-A 1:10


Conservering:
 Kokerprofiel: Th. verzinken
 Plaatstaal : Th. verzinken
 Stalen oor : Th. verzinken
 Hoeveelheden:
 Kokerprofiel: 75 kg
 Plaatstaal : 34 kg
 Stalen oren : 8 stuks

Opmerking: overige voorzieningen en bewerkingen van staalconstr. zie bestek

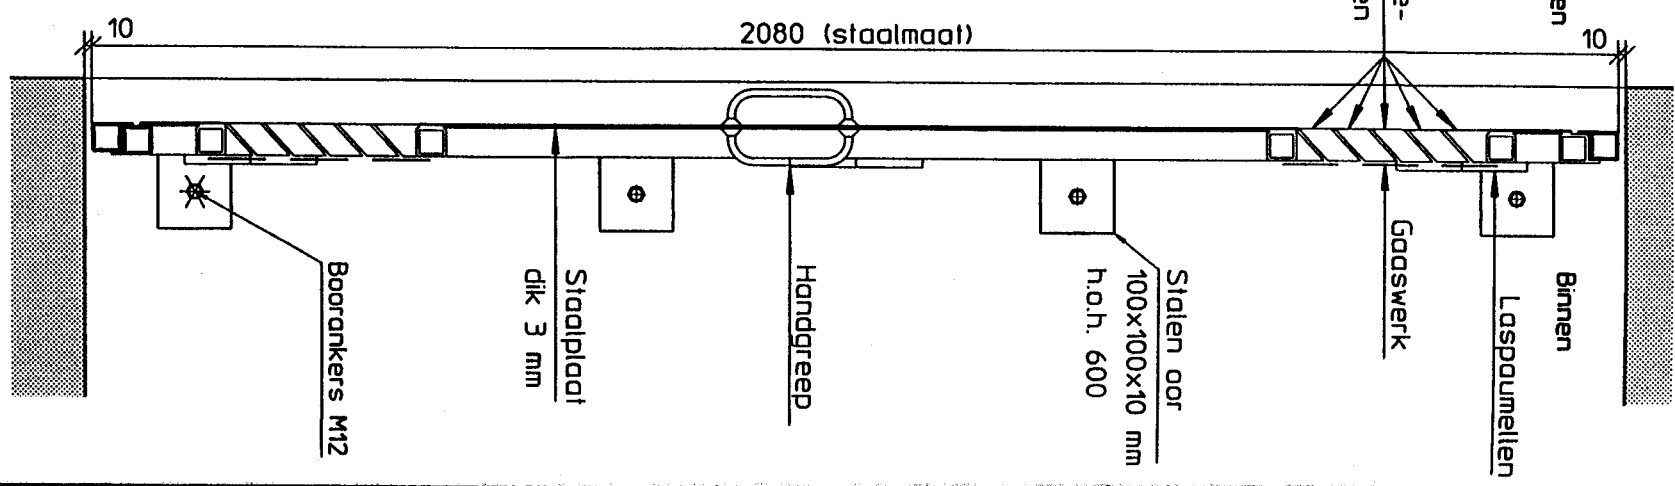

Doorsnede B-B 1:10

	naam/paraaf	datum	Stalen deur naar binnen draaiend		
getekend	J. HAARMA	Nov '97			
gecontroleerd	H. SCHUURMAN	Nov '97			
geedgekeurd	HOOFD TECHNIEK J.H. JONKER				
			Vakafdeling Civiele Techniek		
			Standaarddetail	43	STA 02

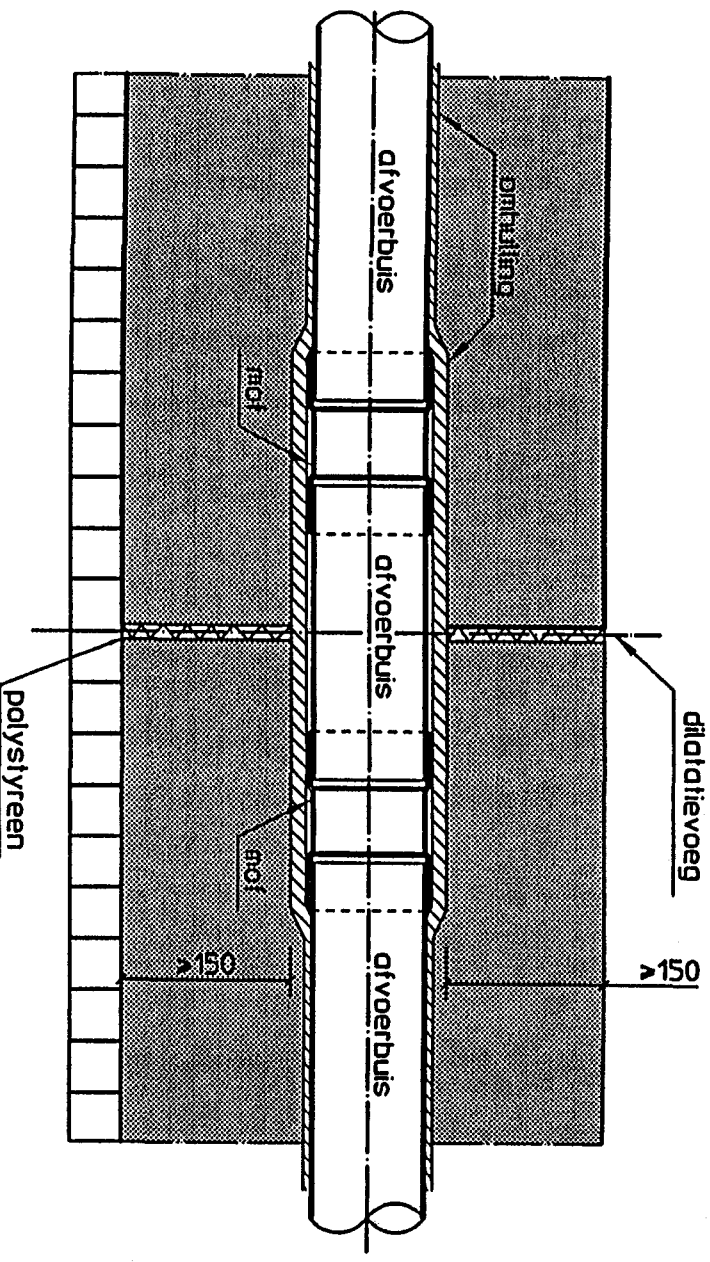

Langsdoorsnede

- afvoerbuis: - PVC buis
- manchel: - PVC moef
- omhulling - kunststofschuim met gesloten cellenstructuur
t.p.v. moffen: dikte 20 mm
- omhulling - kunststofschuim met gesloten cellenstructuur
t.p.v. PVC buis: dikte 10 mm
- voegvulling: - polystyreen

	naam/paraaf	datum	Voegovergang hemelwaterafvoer Type 2		formaat	A4
geleidend	H.J. BOSMAN	07-08-95			school	1:0
gecontroleerd	H. SCHURMAN	07-08-95			uitgave	
goedgekeurd	HOOFD TECHNIEK G.H.H. TOUW.	07-08-95				

Holland Railconsult

Vakafdeling Civiele Techniek

Standaarddetail

61

HWA

06