




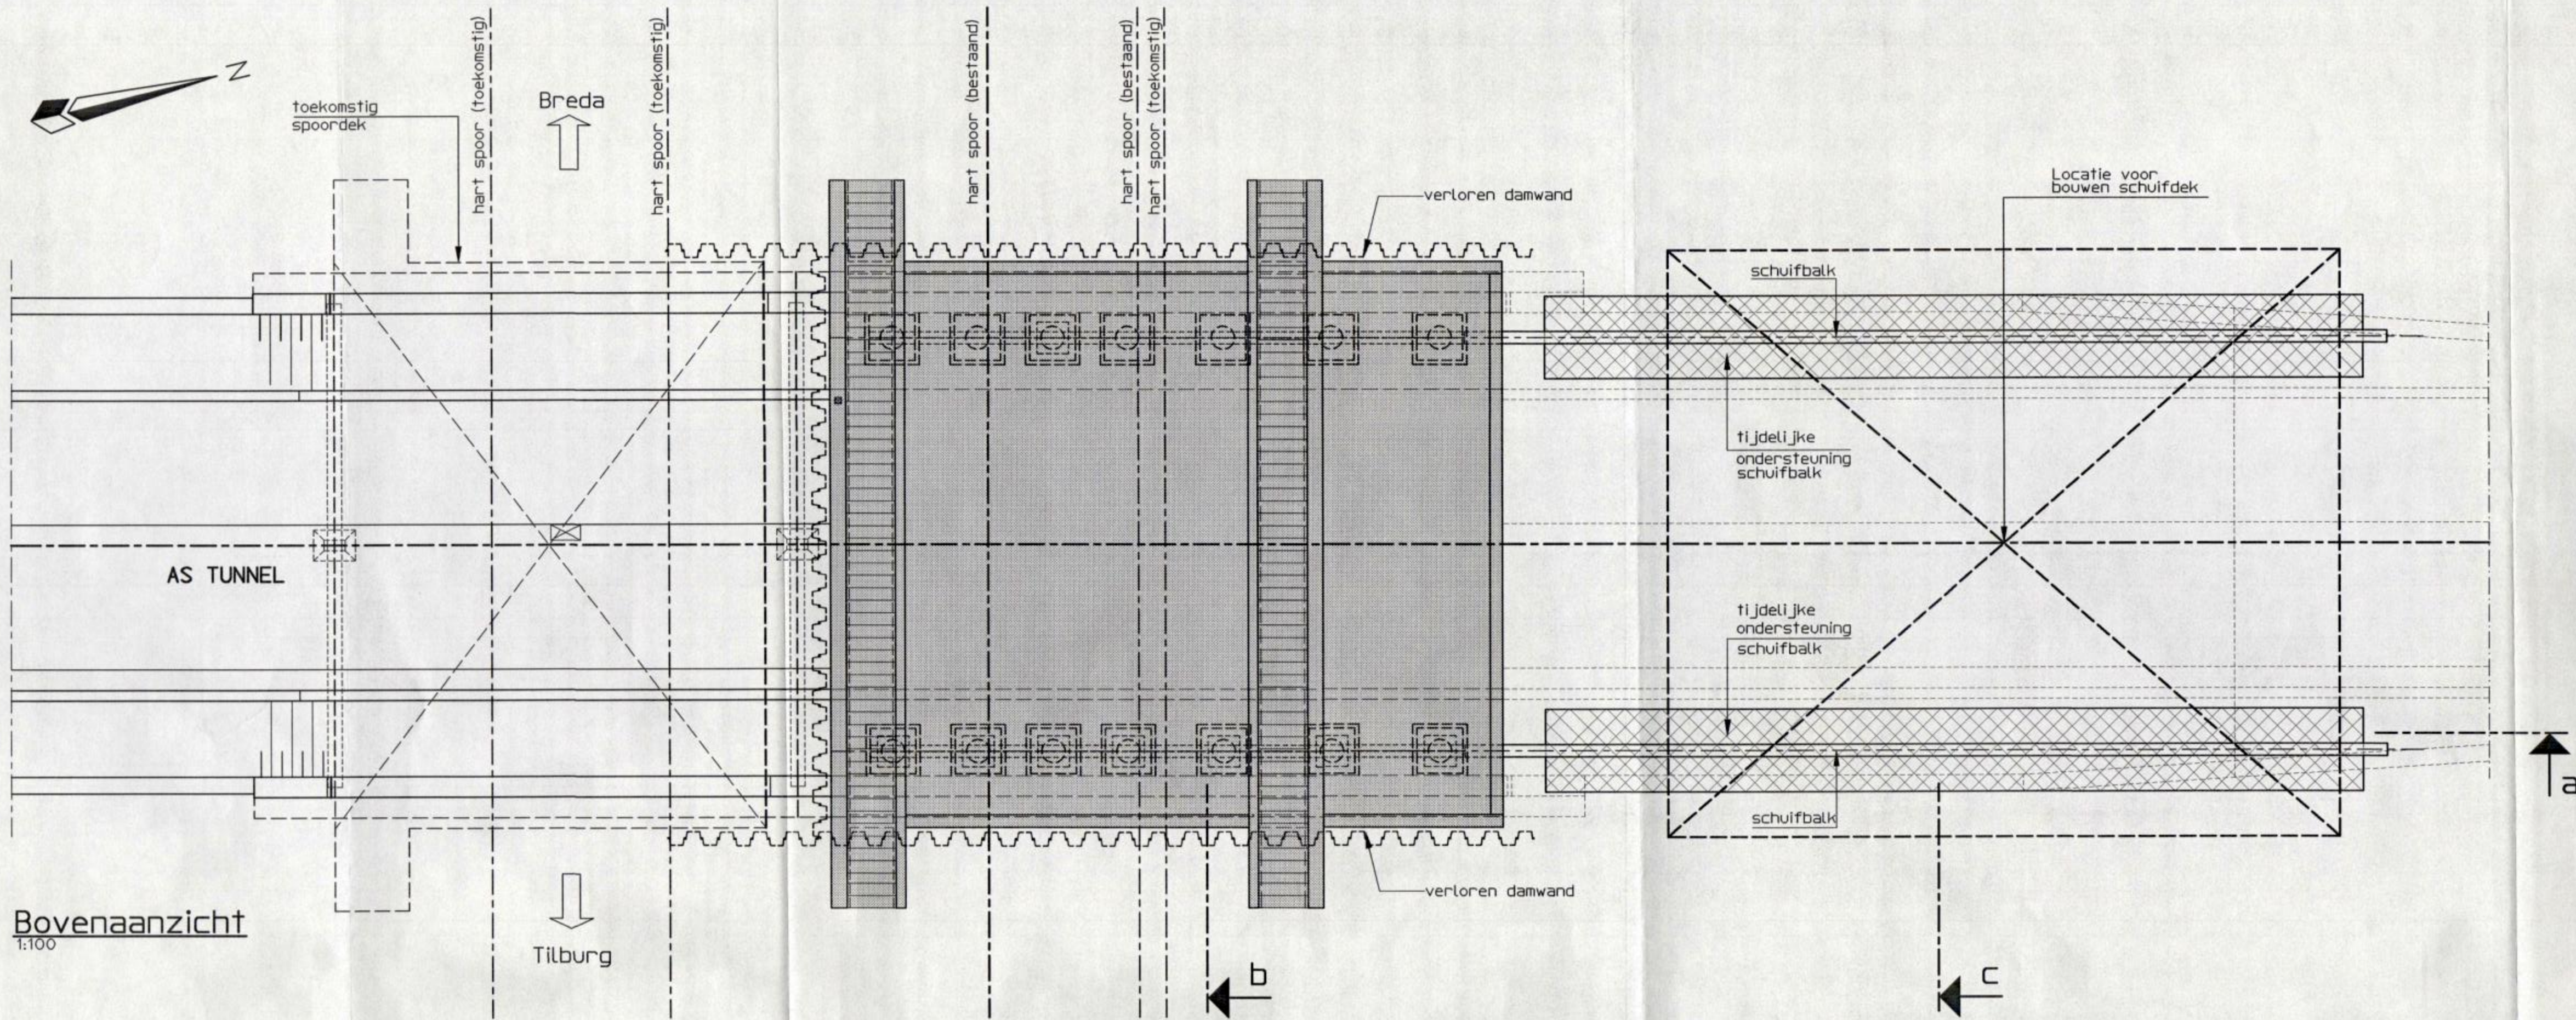


Bovenaanzicht
1:100

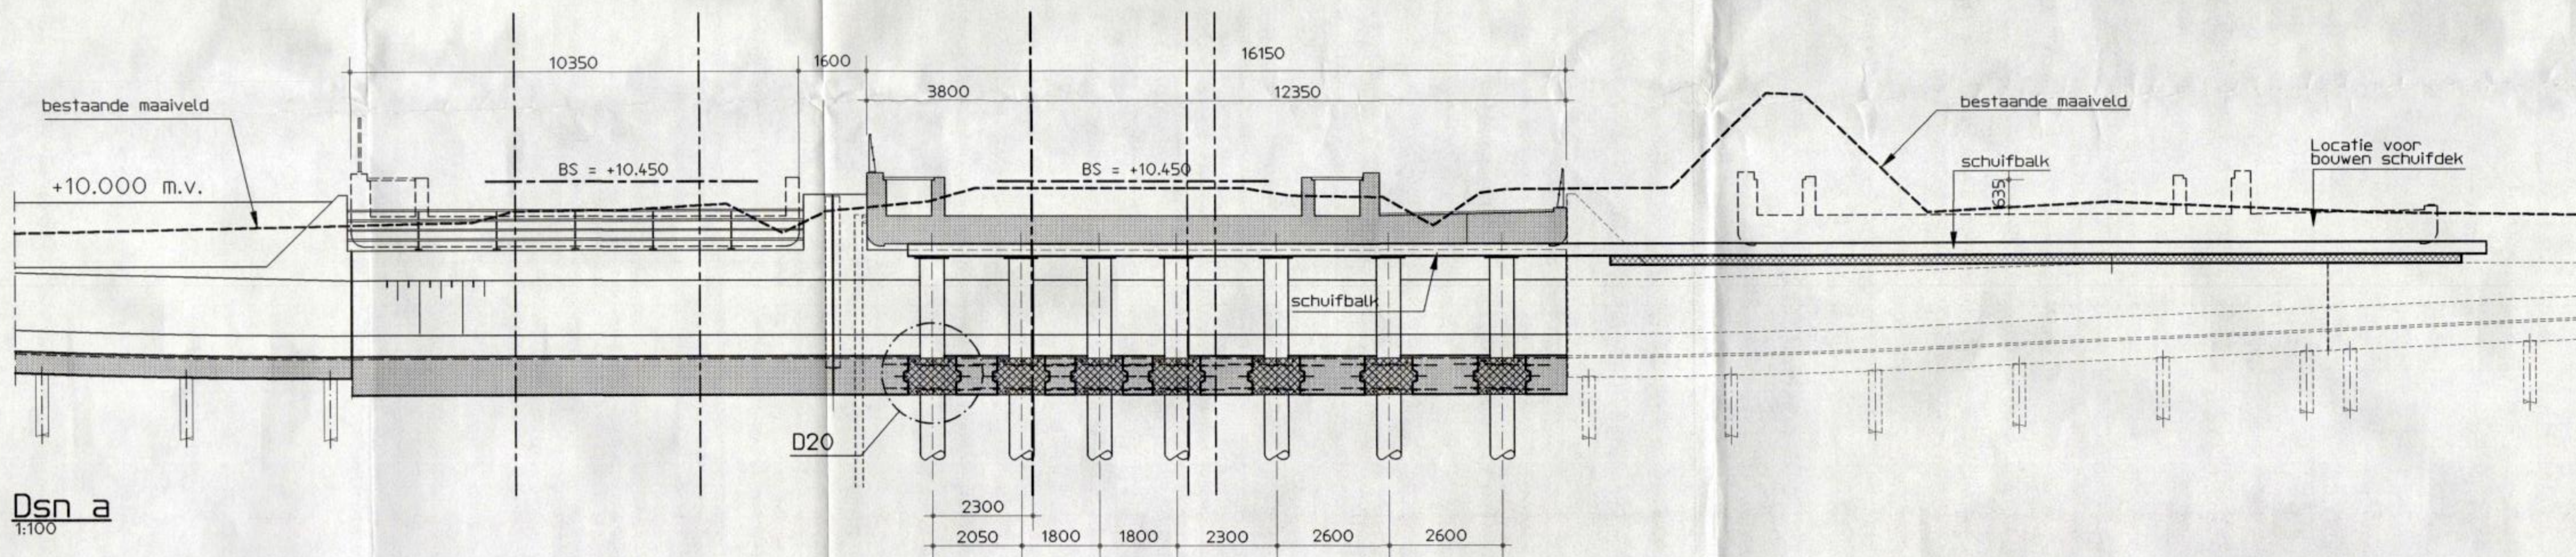

Dsn a
1:100

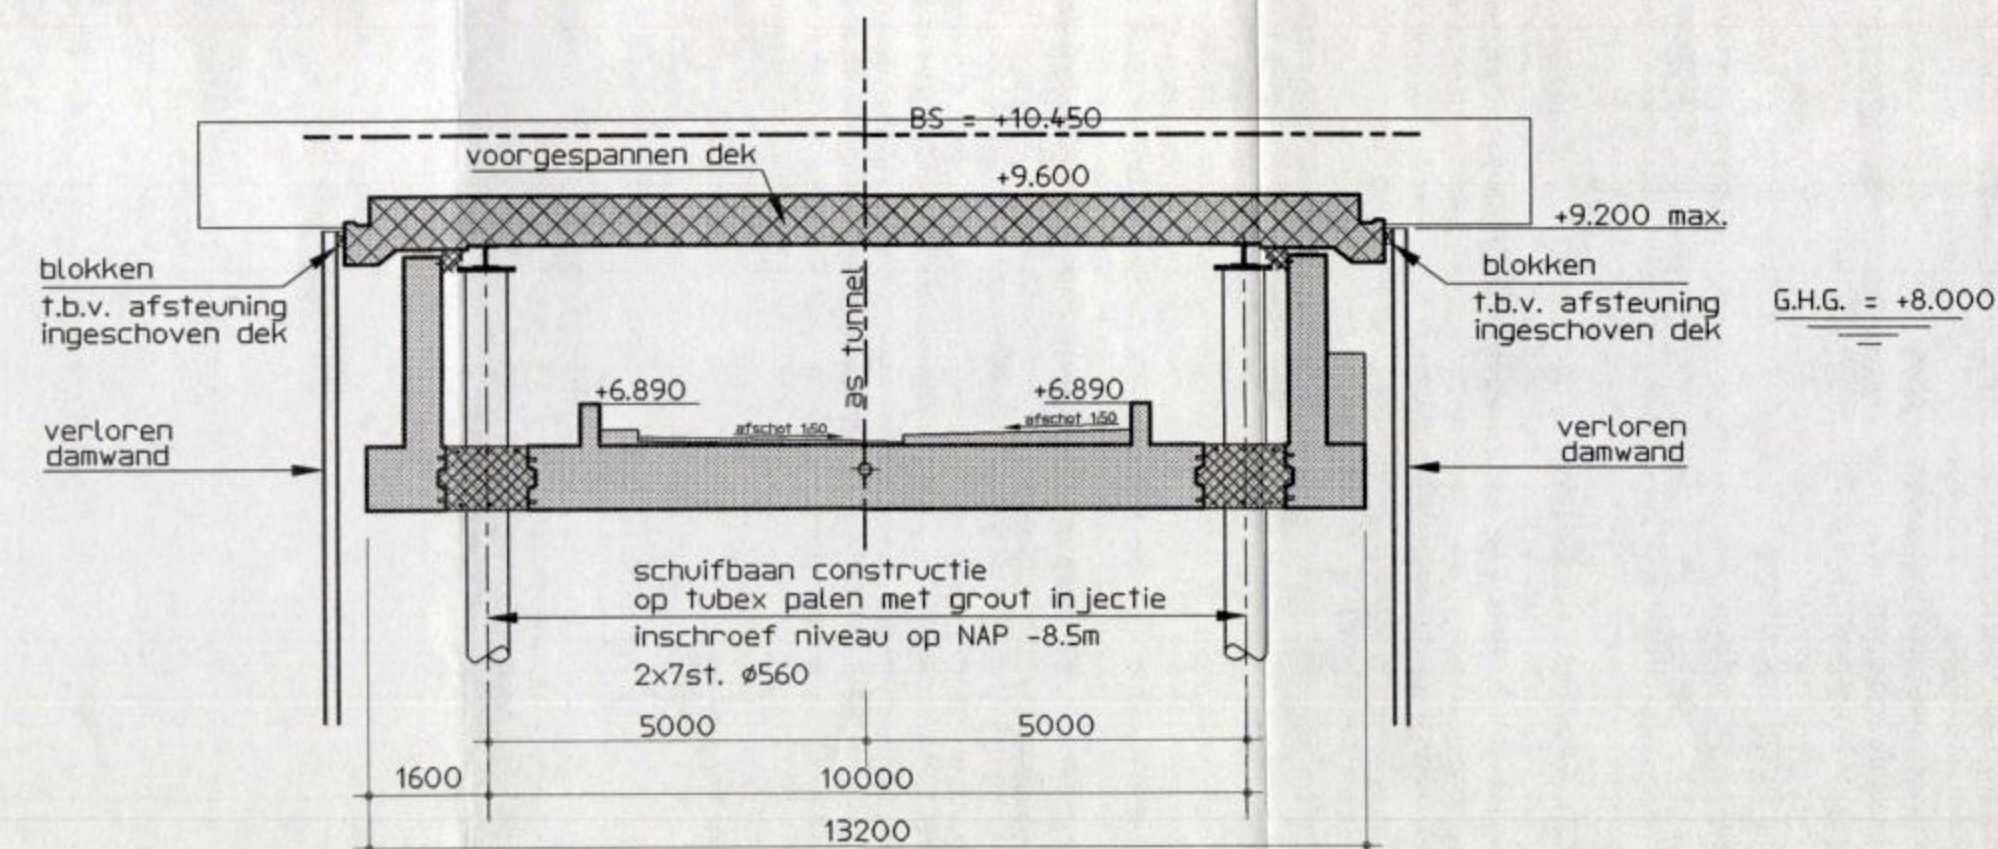


Dsn b
1:100

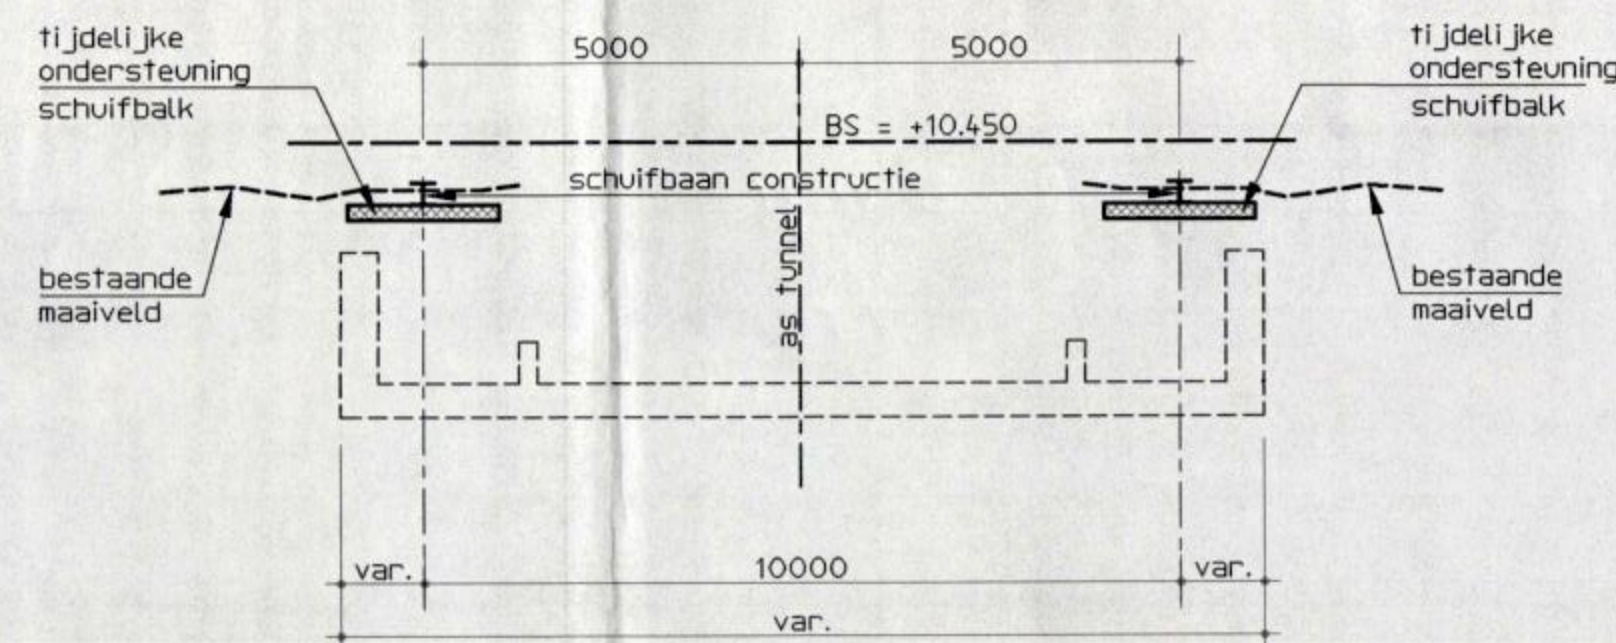

Dsn c
1:100

Voor tunnel alignment zie blad 300
Voor bovenaanzicht en doorsneden zie blad 301
Voor palenplan zie blad 302
Voor details zie blad 304 (Detailboek)

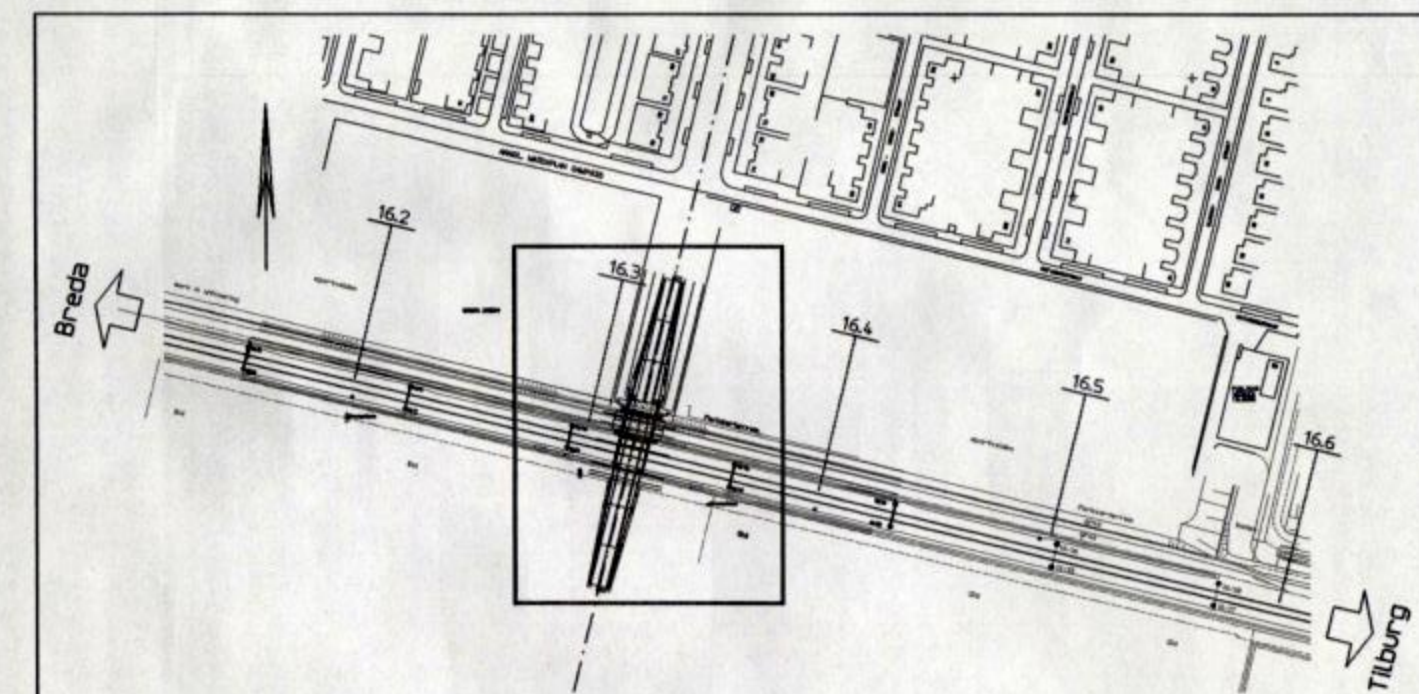

Opmerkingen
- alle maten in mm
- hoogtematen in m t.o.v. N.A.P.
- coördinaten t.o.v. Parijs stelsel

REVISIE TOEGEPAST

ARCADIS BOUW/INFRA

Berkenweg 7
Postbus 220, 3800 AE Amersfoort
Telefoon 033 460 44 00
Telefax 033 460 44 06

Project
Tilburg
o.d.g. Camphoef-Witbrant

Onderdeel
Bestek
Hulpconstructie

Codering derden :

Status :
Goedgekeurd :
F.J. Hovinga
Vrijgegeven :
J.W.M. Hagen
Schaal : 1:100
Formaat : A1

Tekeningnummer:
Tb 42/3/1 303

ARCADIS Bouw/Infra BV is ontstaan uit Articon, Grabowsky&Poort,
Heldemij Advies Bouw, Bureau Jongen, Starke Diekstra en Van der Mast