




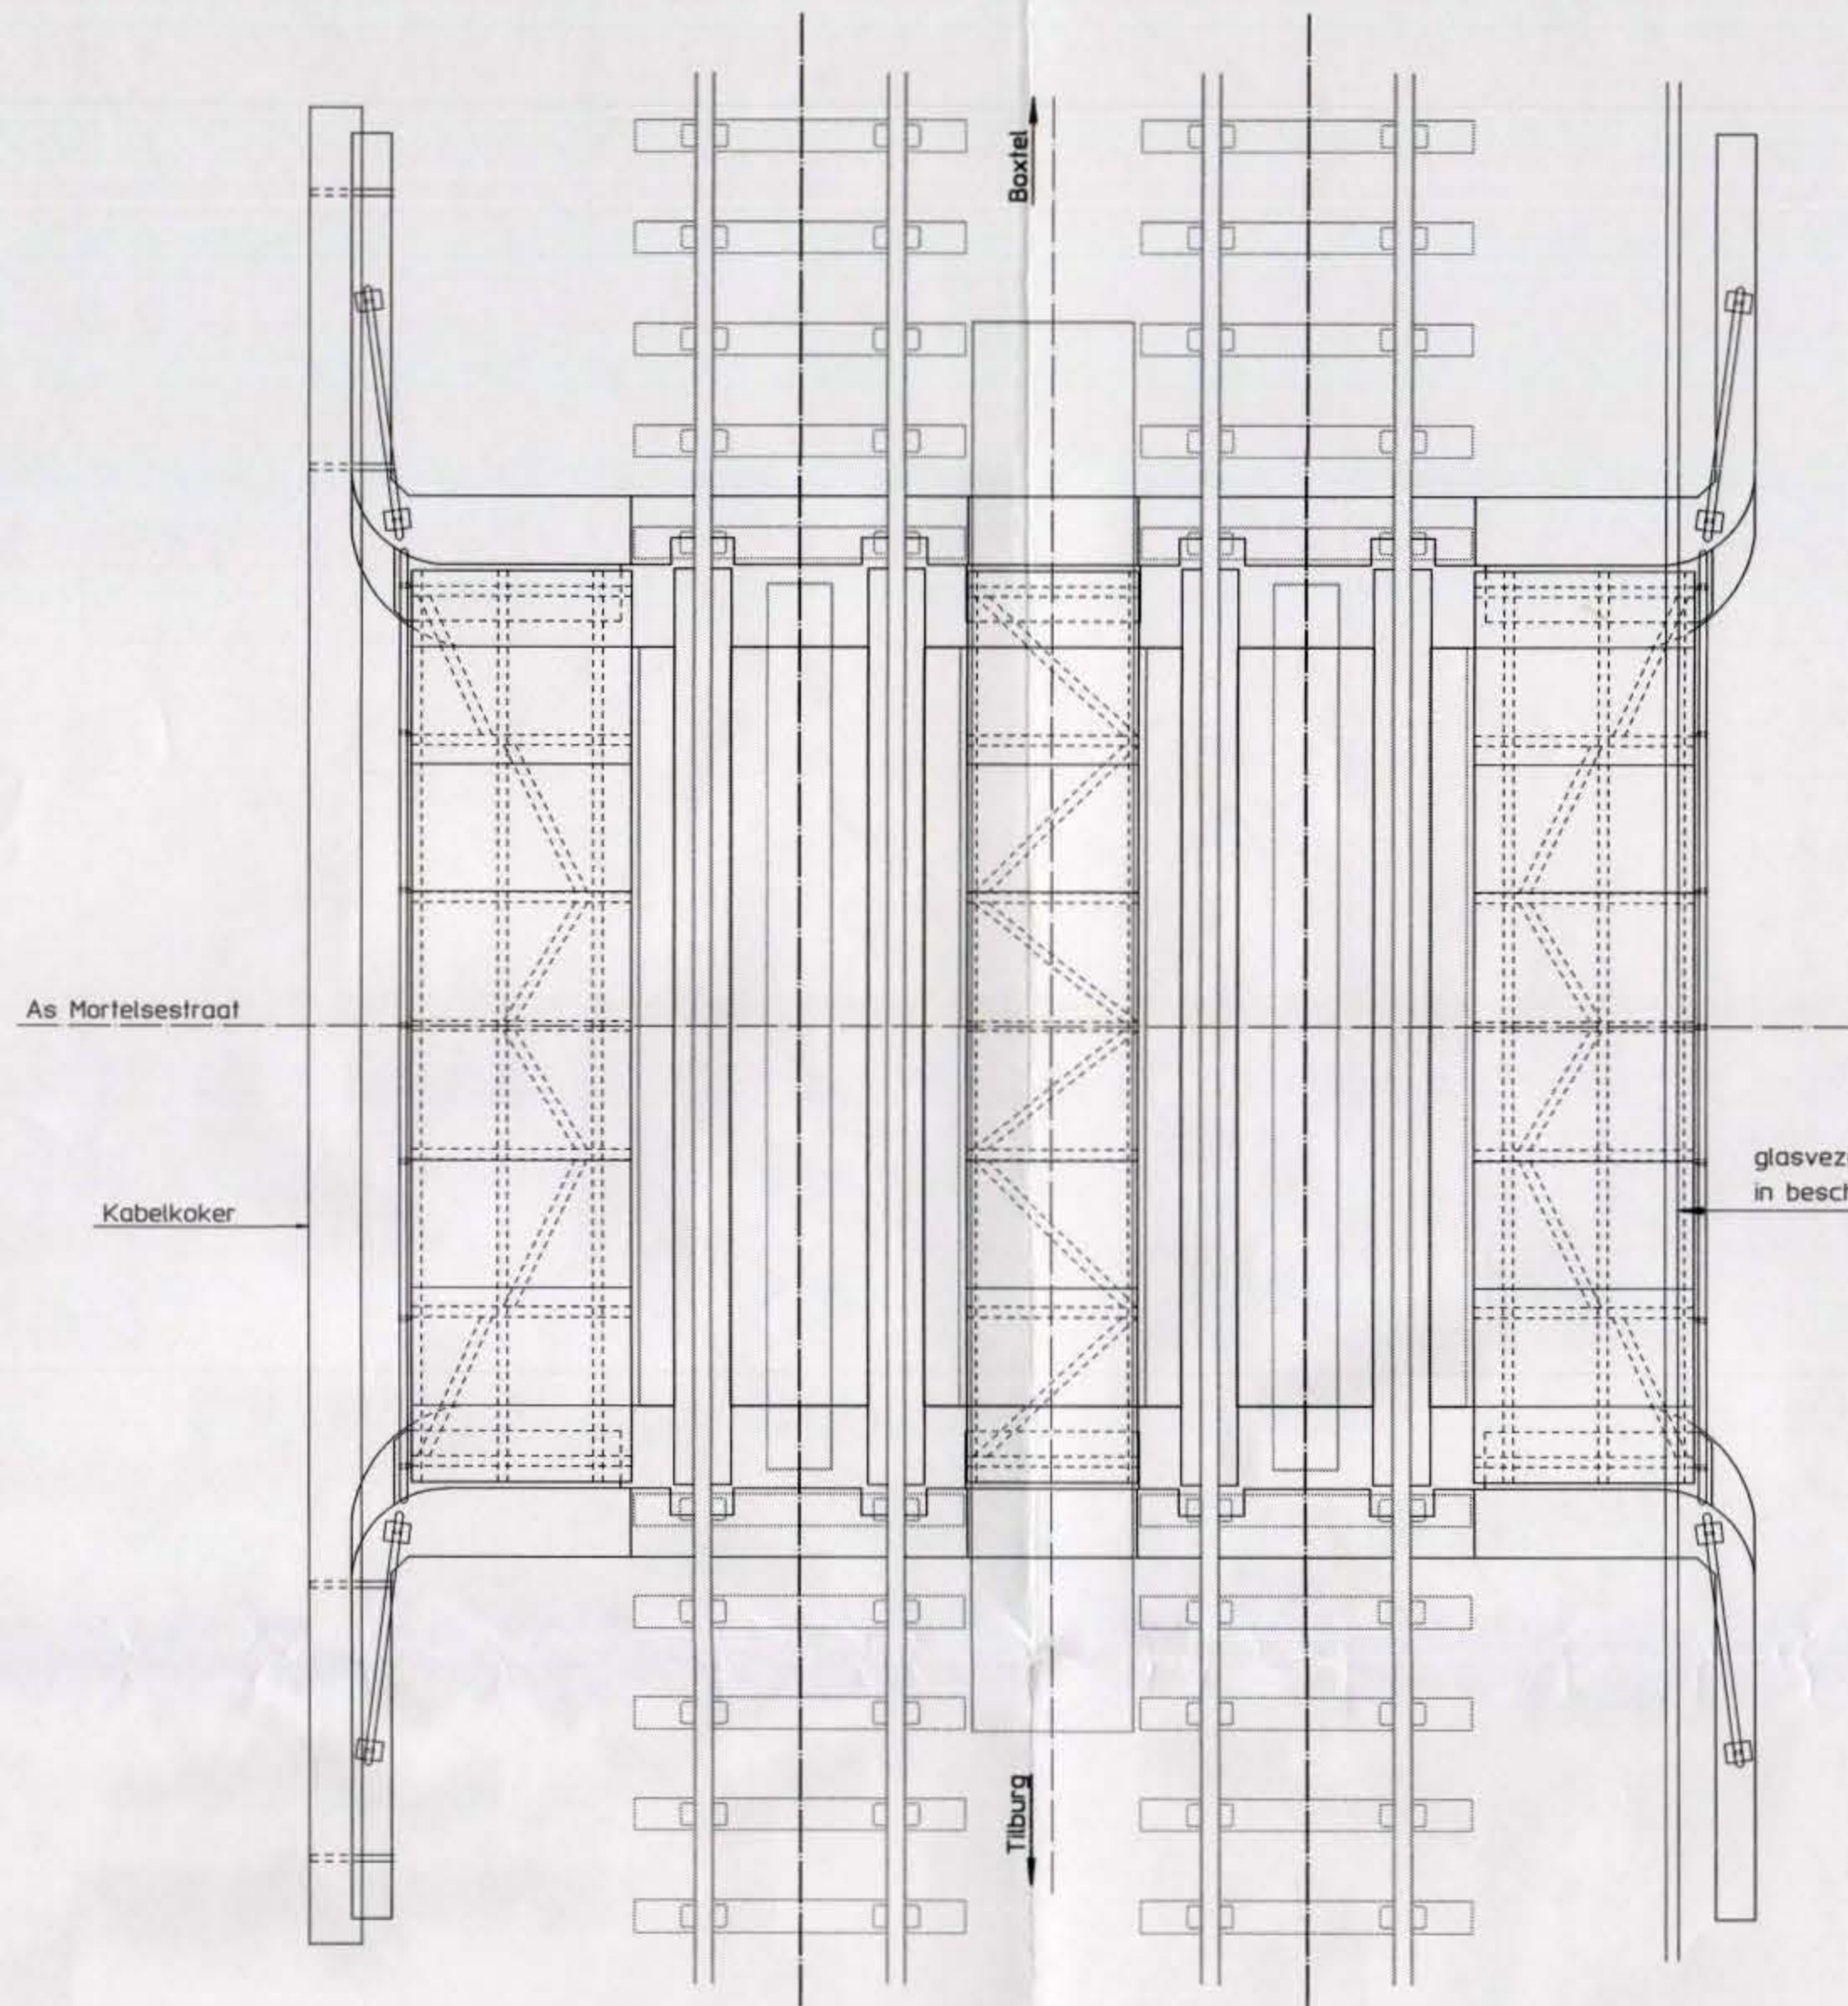


Bovenaanzicht, bestaande situatie 150

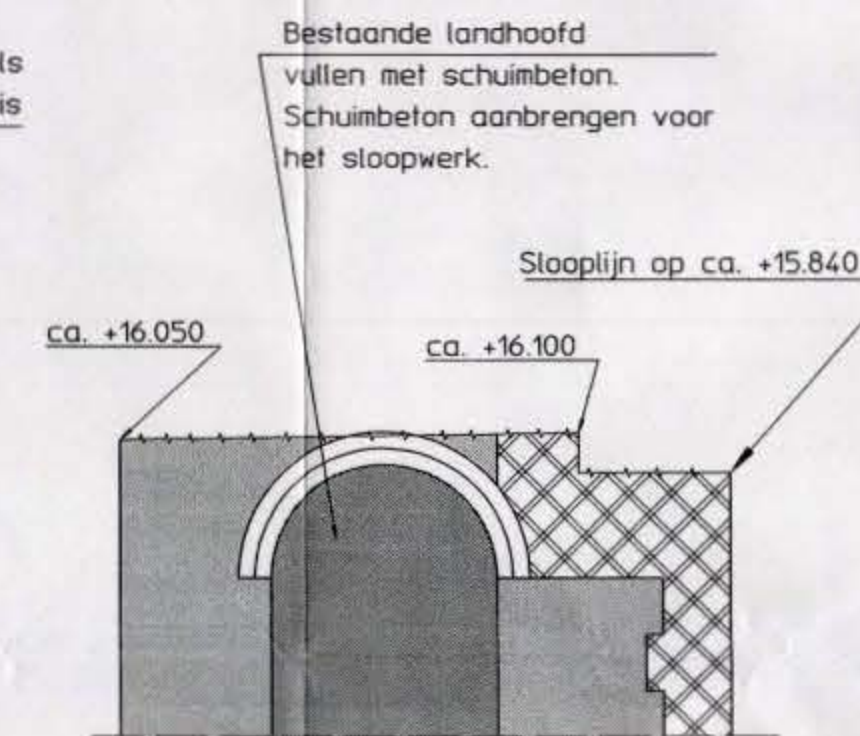


Doorsnede over landhoofd sloopvlak 150

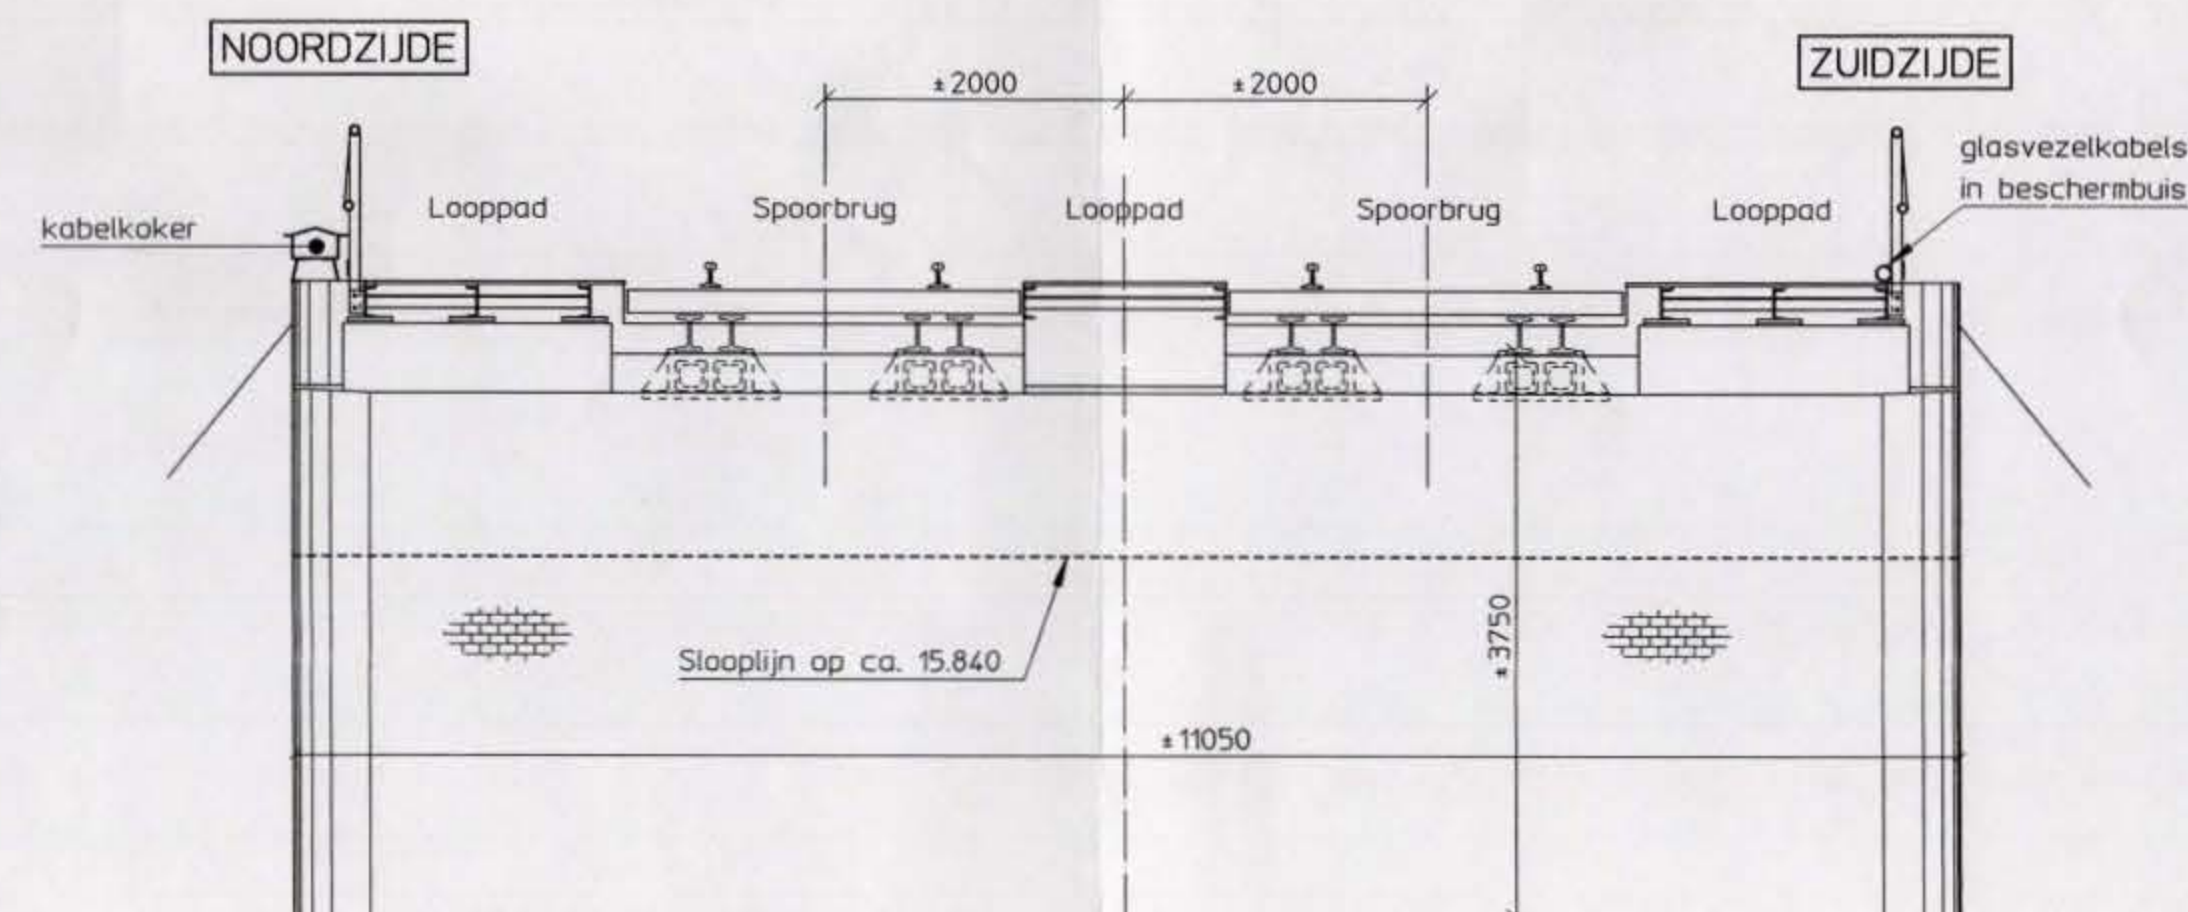


Doorsnede over as Mortelsestraat, bestaande situatie 150

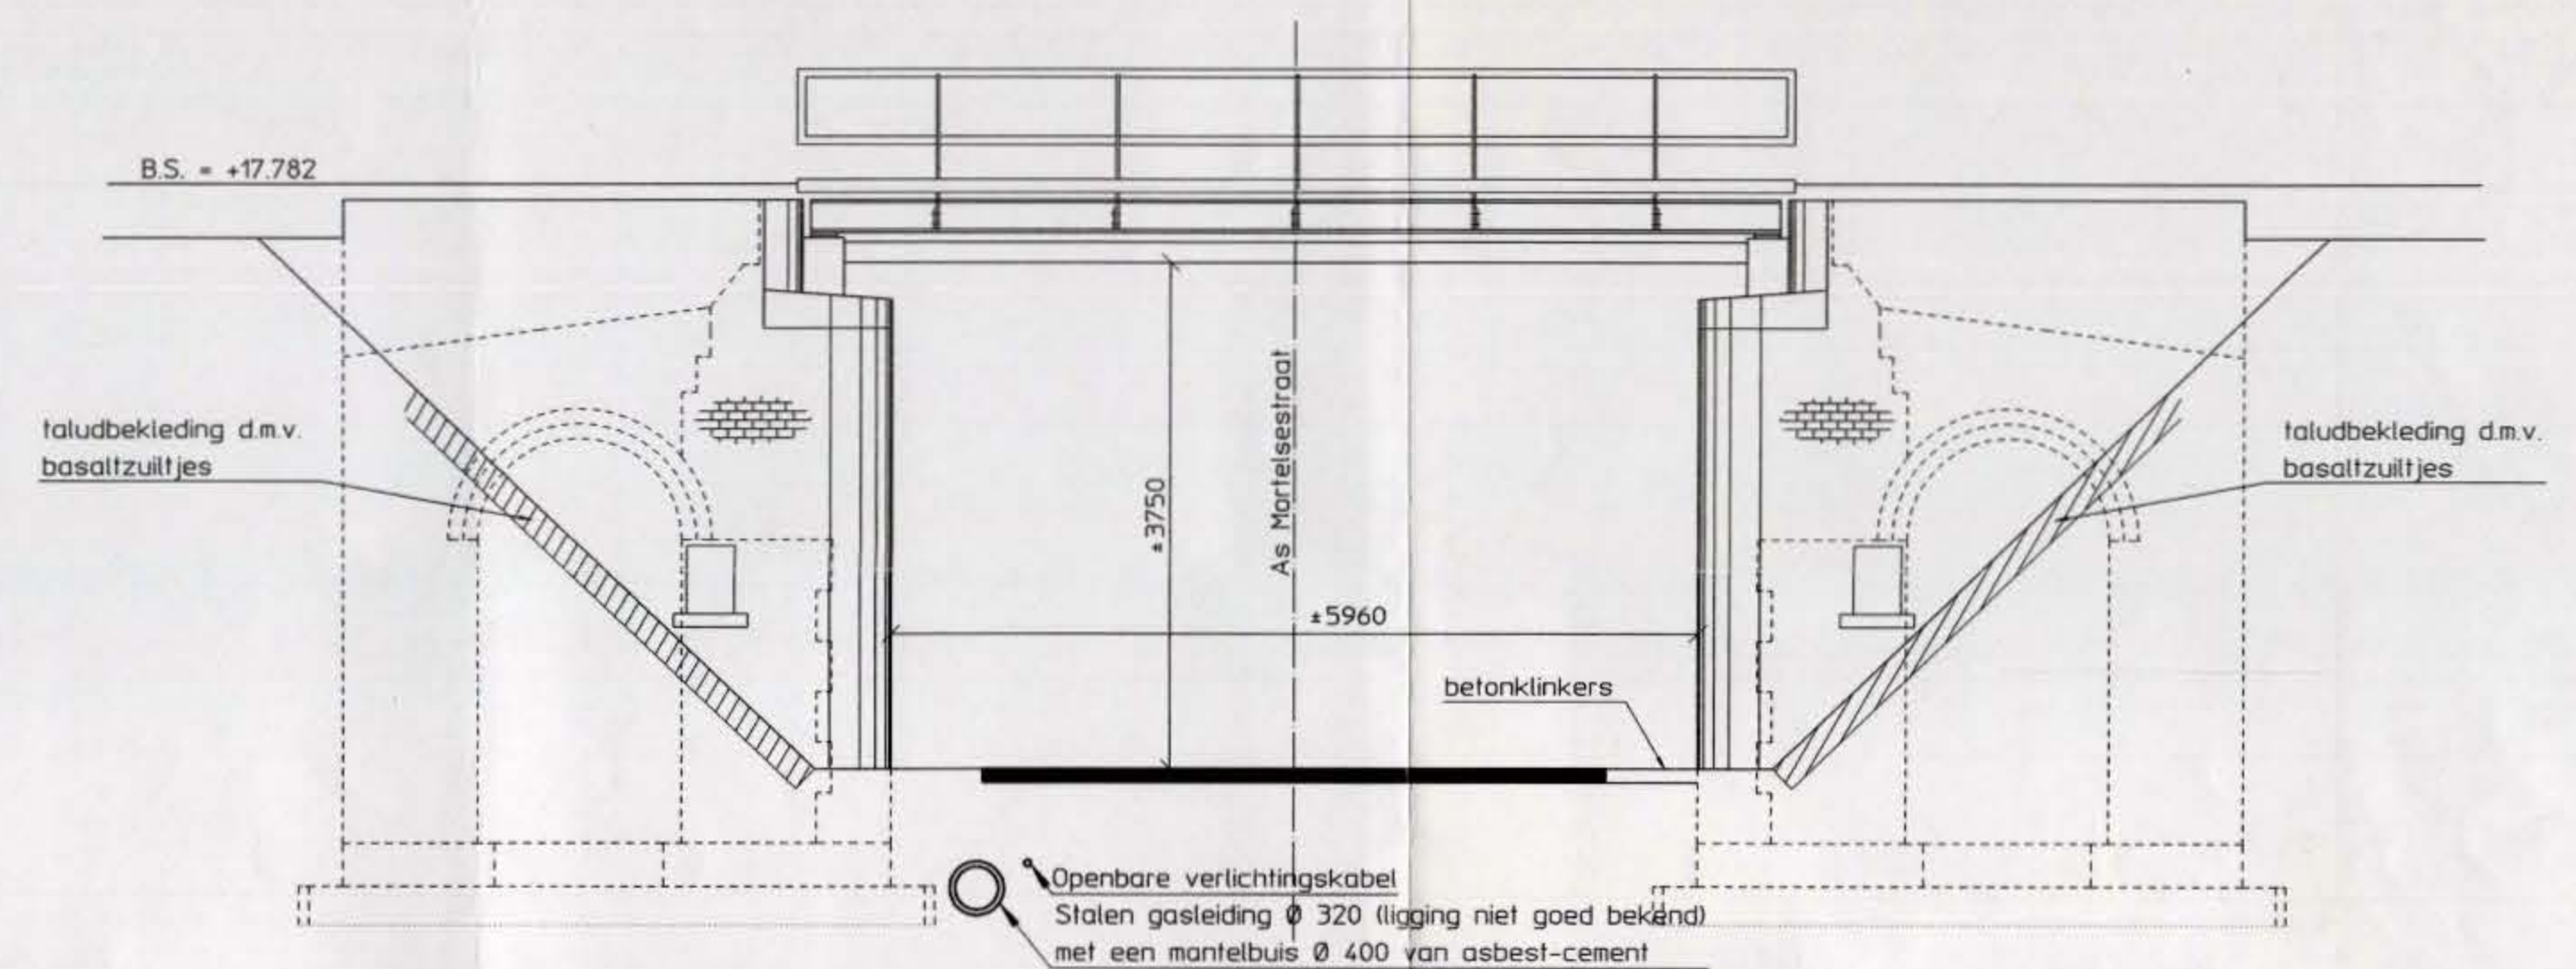

Vooraanzicht, bestaande situatie 150

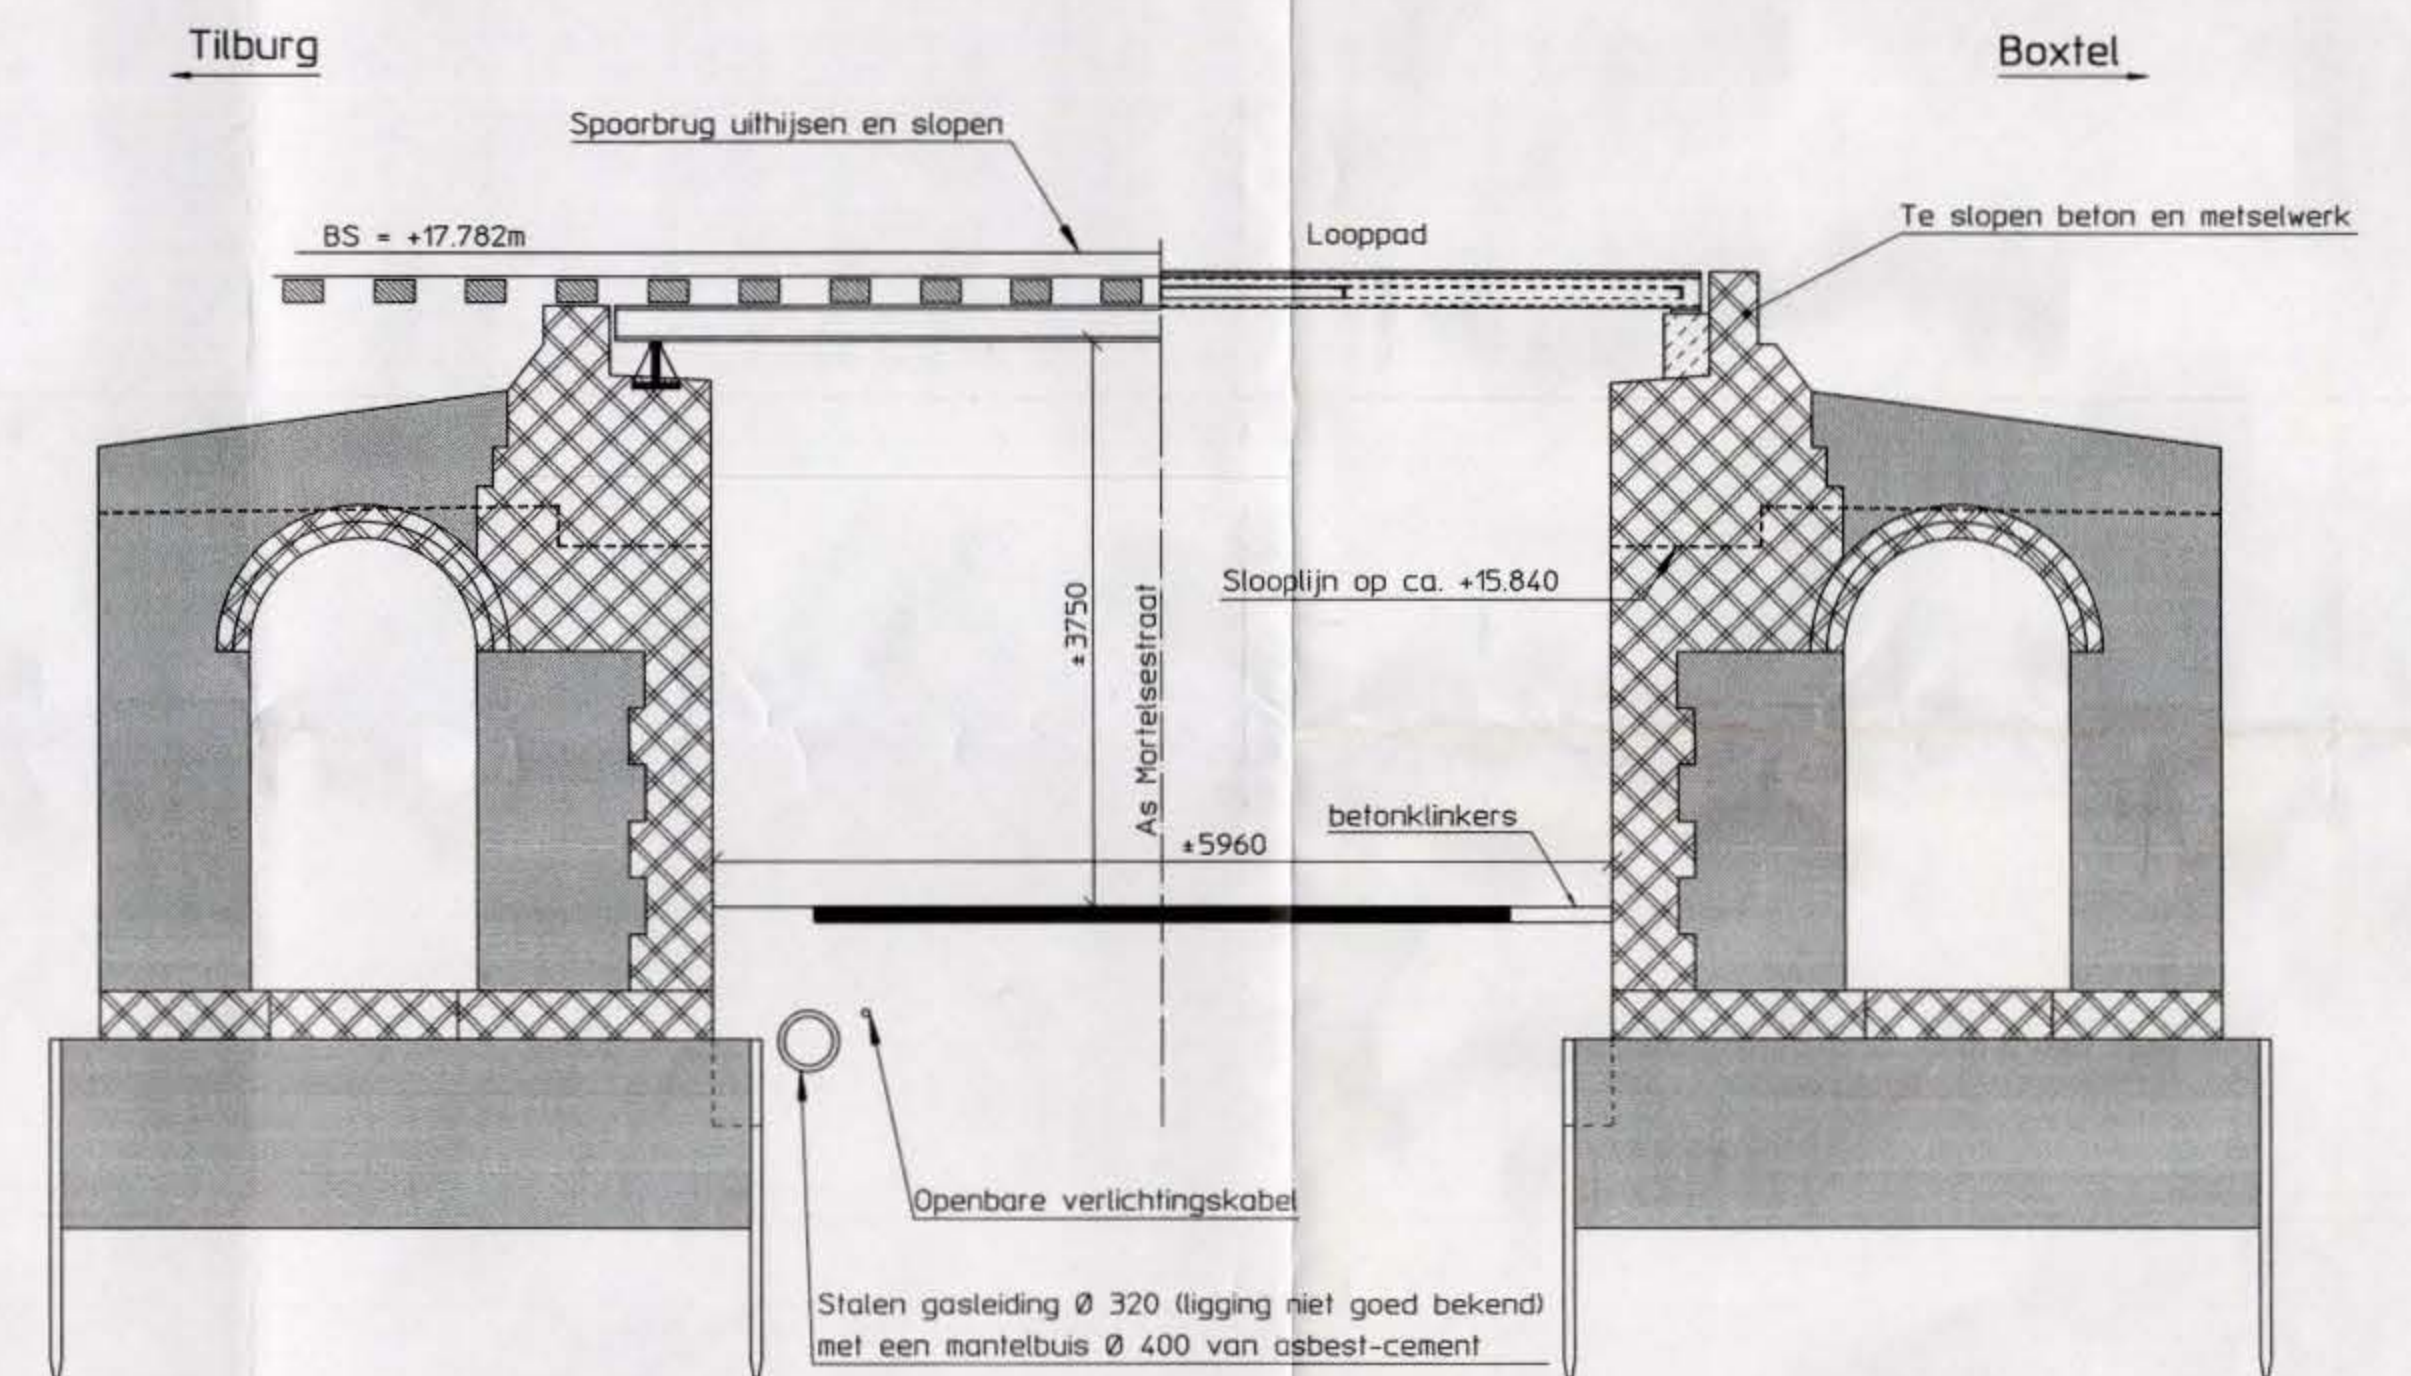

Doorsnede over as spoorbaan, bestaande situatie 150

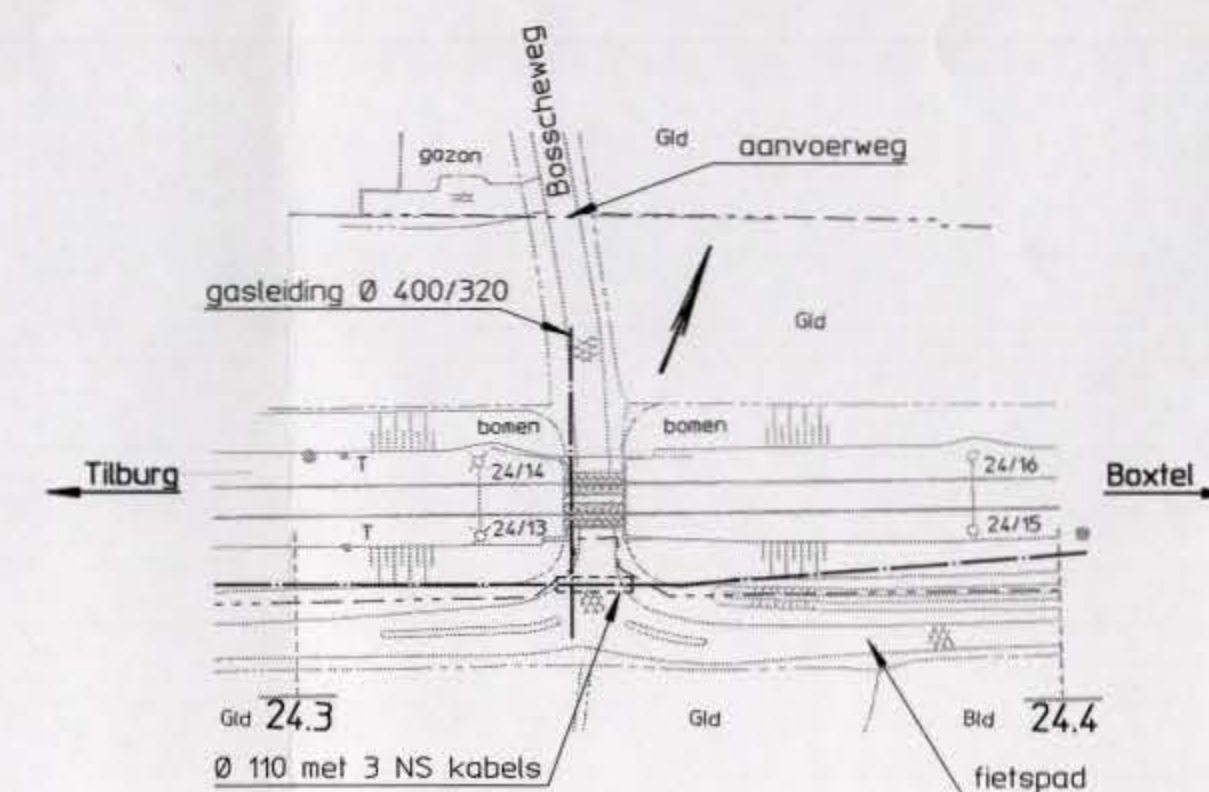

Situatie 1:1000

LEGENDA

- Maten in mm.
- Hoogtematen in m. t.o.v. N.A.P.
- = bestaand metselwerk
- = bestaand betonwerk
- = bestaand natuursteen doorsnede

Status: VRIJGEGEVEN

getekend	B. Timmer	par.	02-05-2000	Bestektekening Bestaande situatie / sloopwerk
projectleider	W.P.T. Vermeulen	08-05-00		
projectnr.	7502004	versie	1.0	Railinfrabeheer Tilburg Verv. spoorbruggen Mortelsestraat
besteknr.	V40BK1566			
formaat	A1			
schaal	150			