

BOVENAANZICHT PILLER 2, 3 EN 4 - WUJFHOUT NIET GETEKEND

AANZICHT

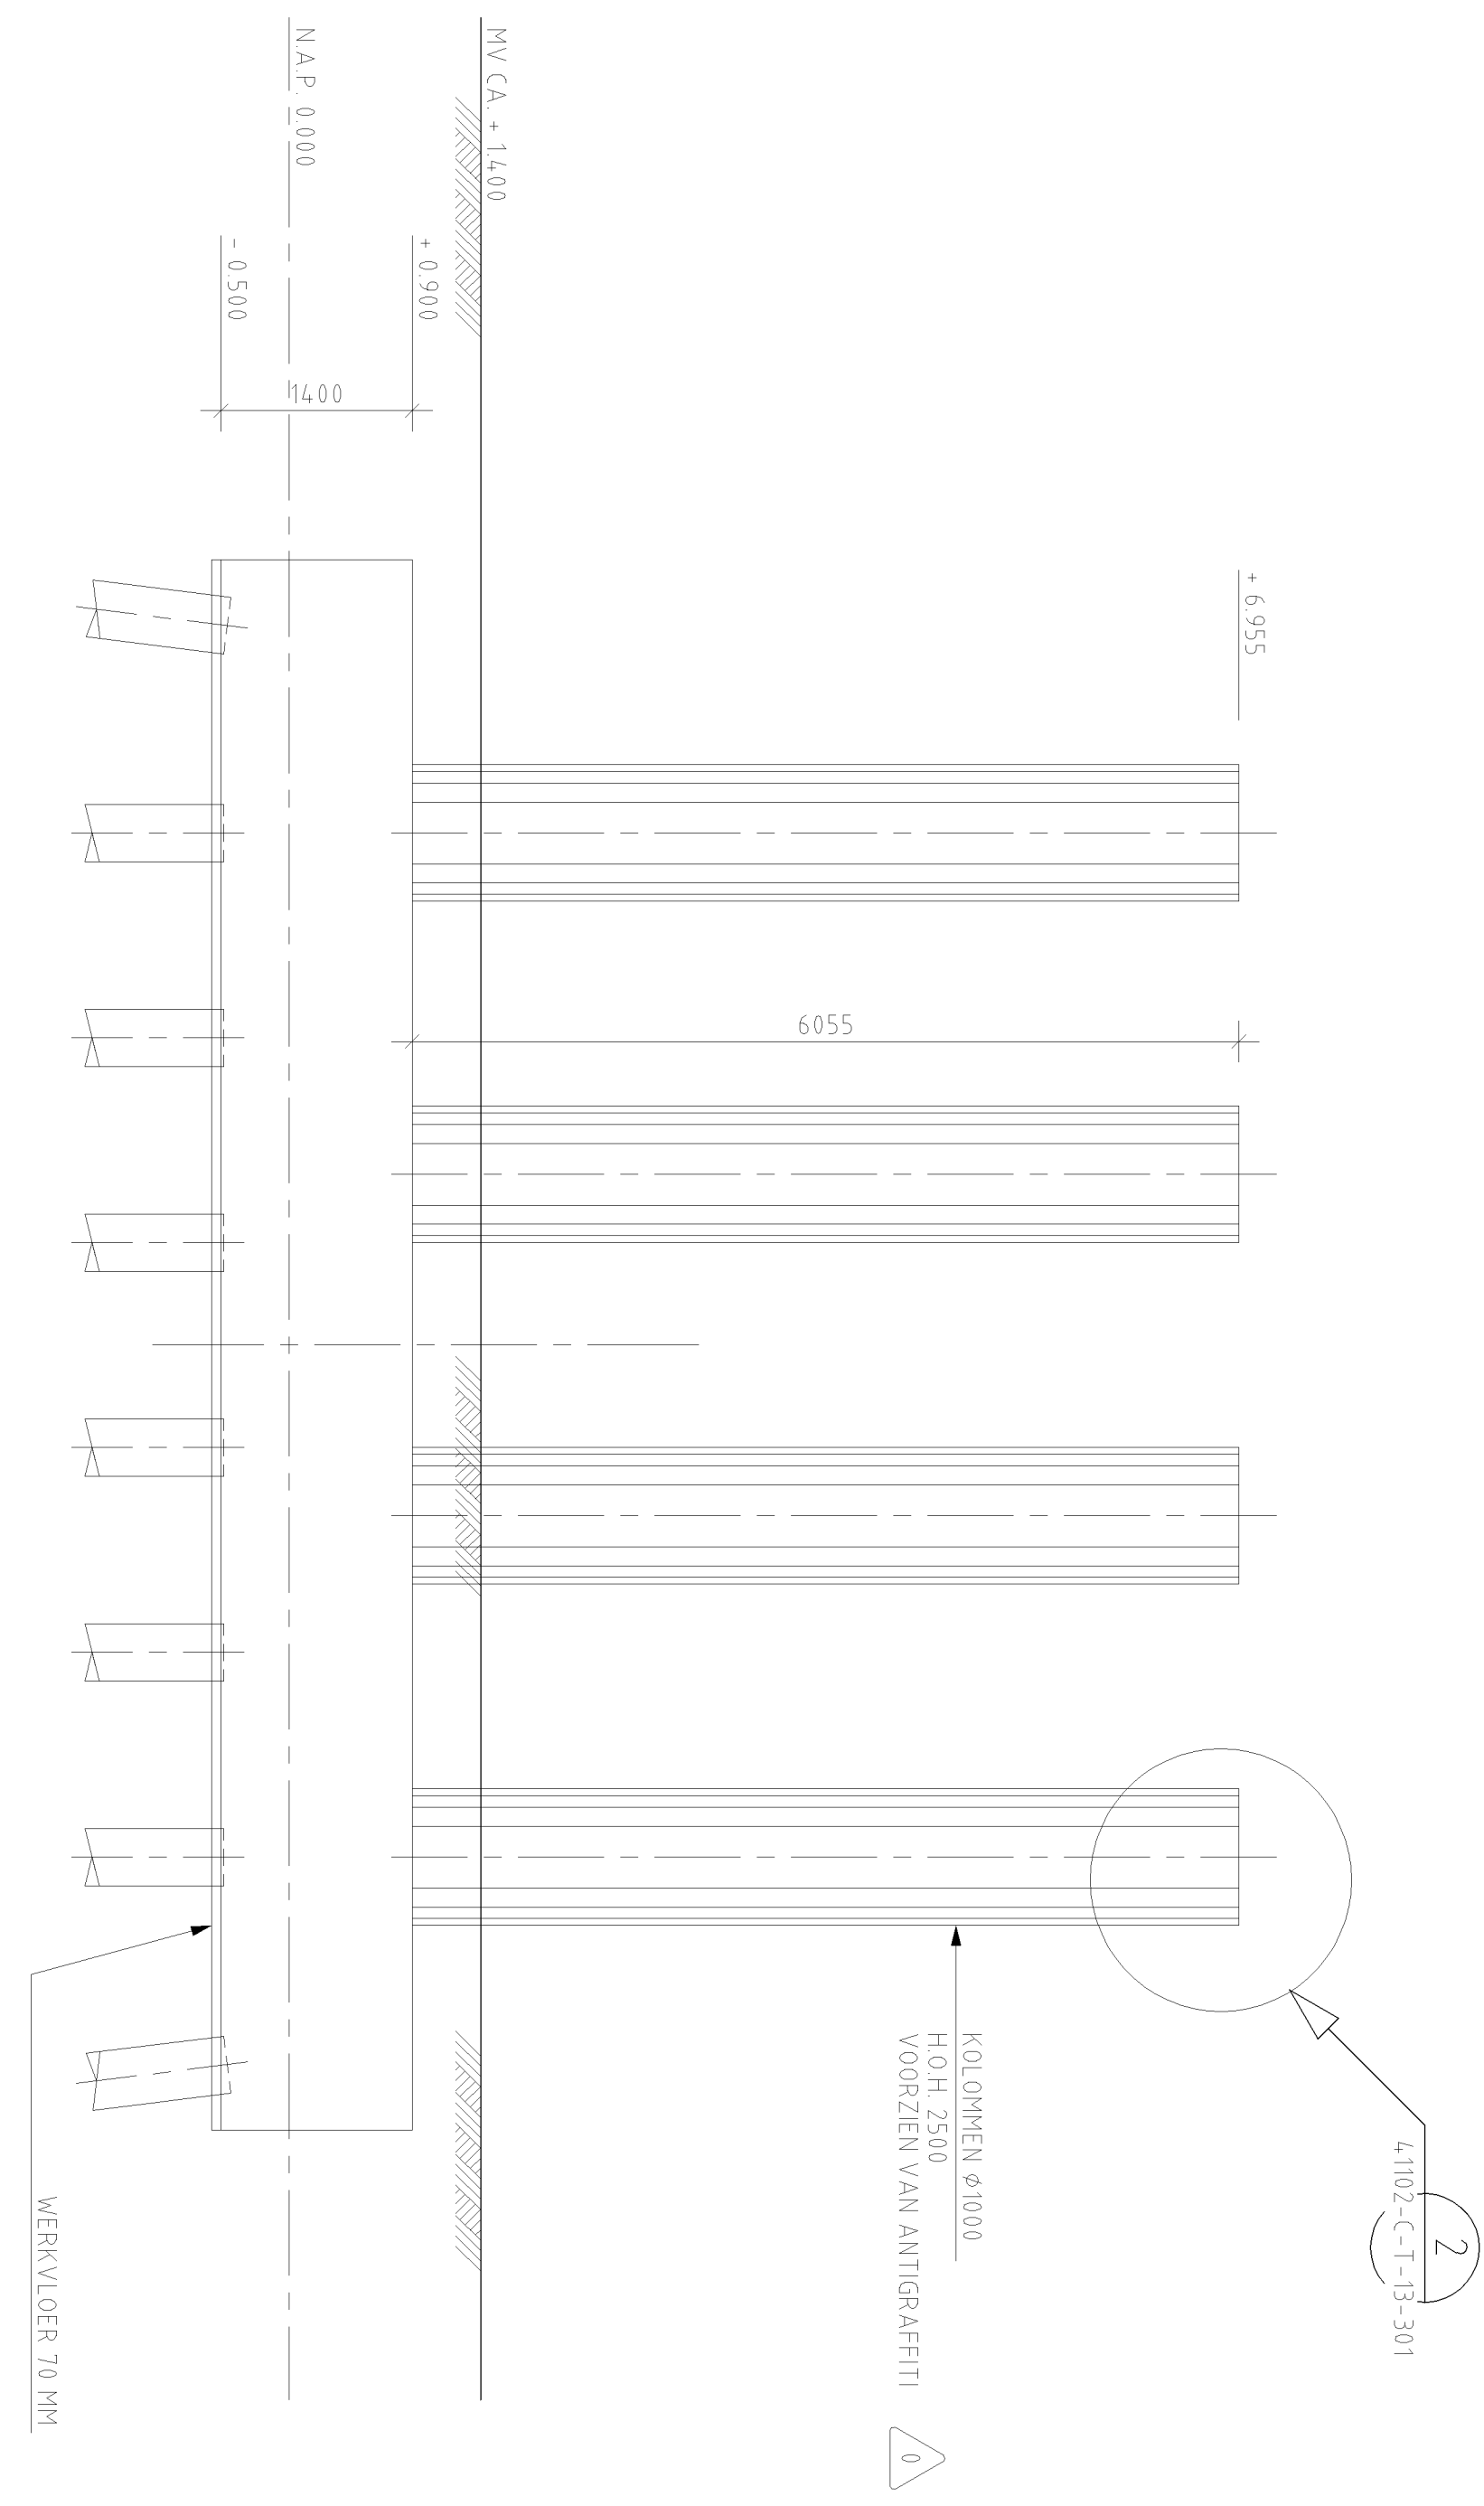
SCHAAL 1 : 50

A

-

DOORSNEDE B
SCHAL 1 : 50

BOVENAANZICHT PILLER 5
SCHAAL 1 : 50

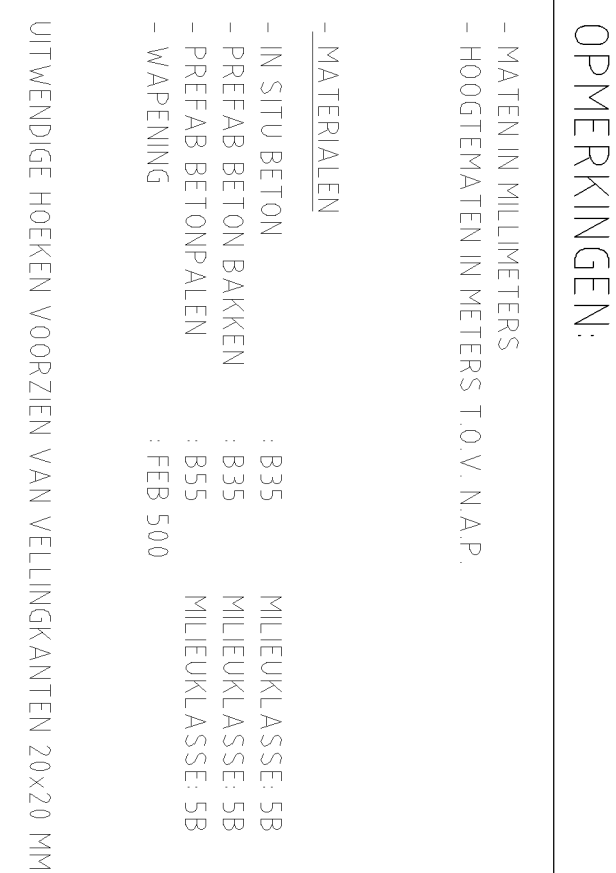
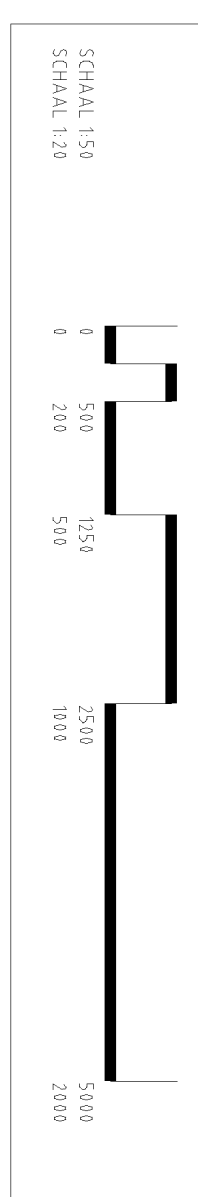


AANZICHT

SCHAAL 1:50

(C)

DOORSNEDE D
SCHAL 1:50

[illegible]