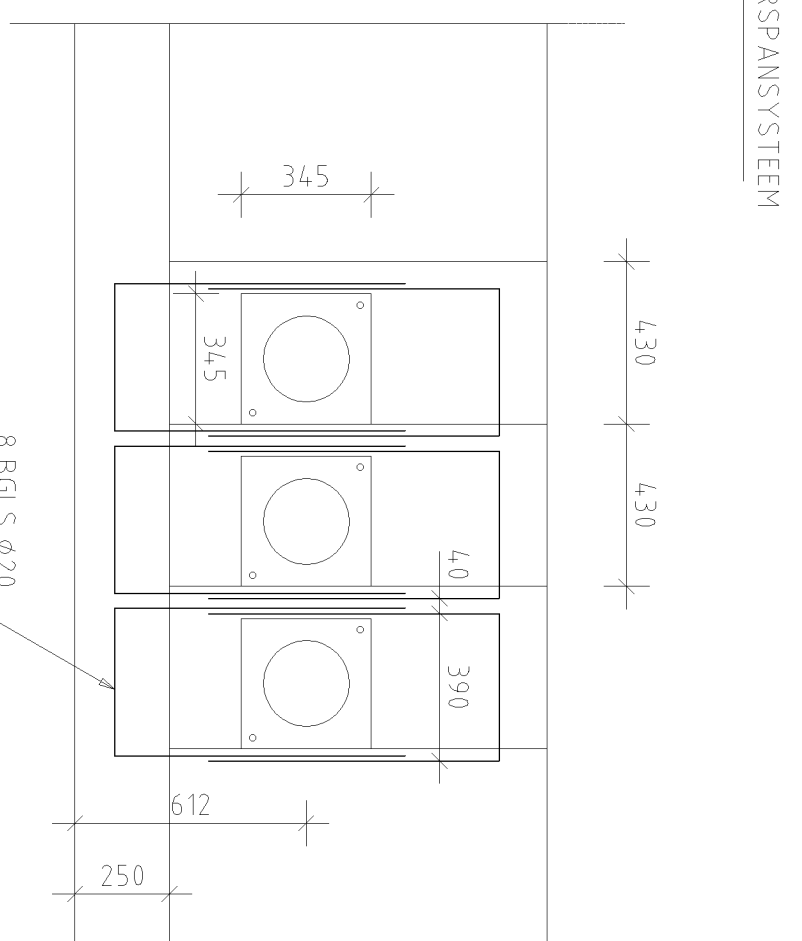
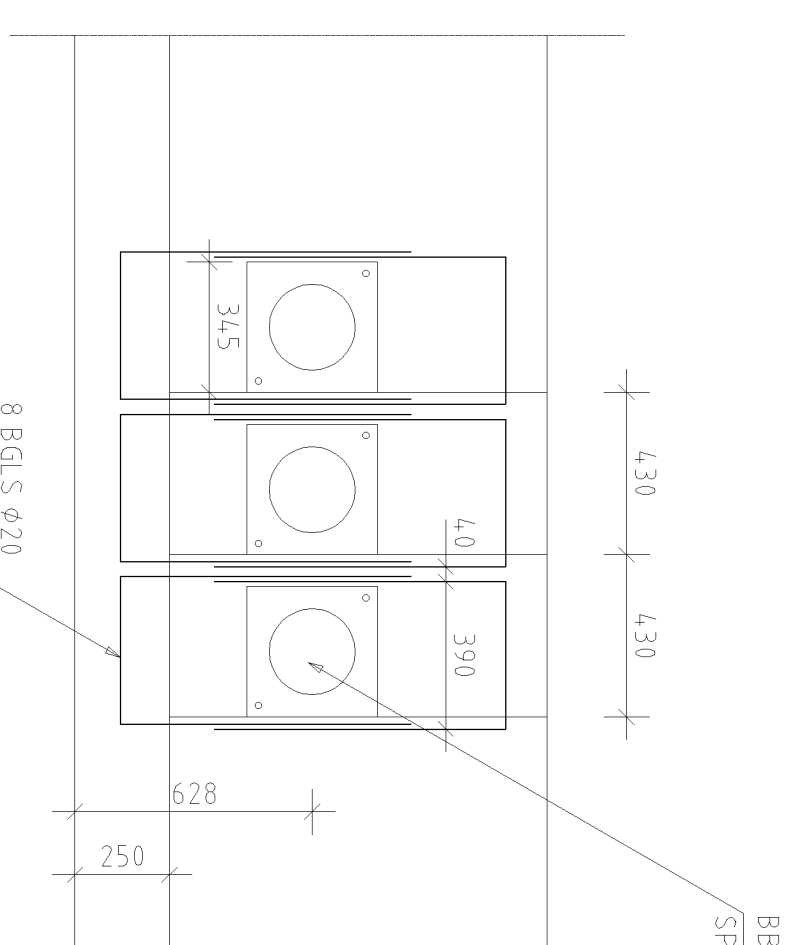
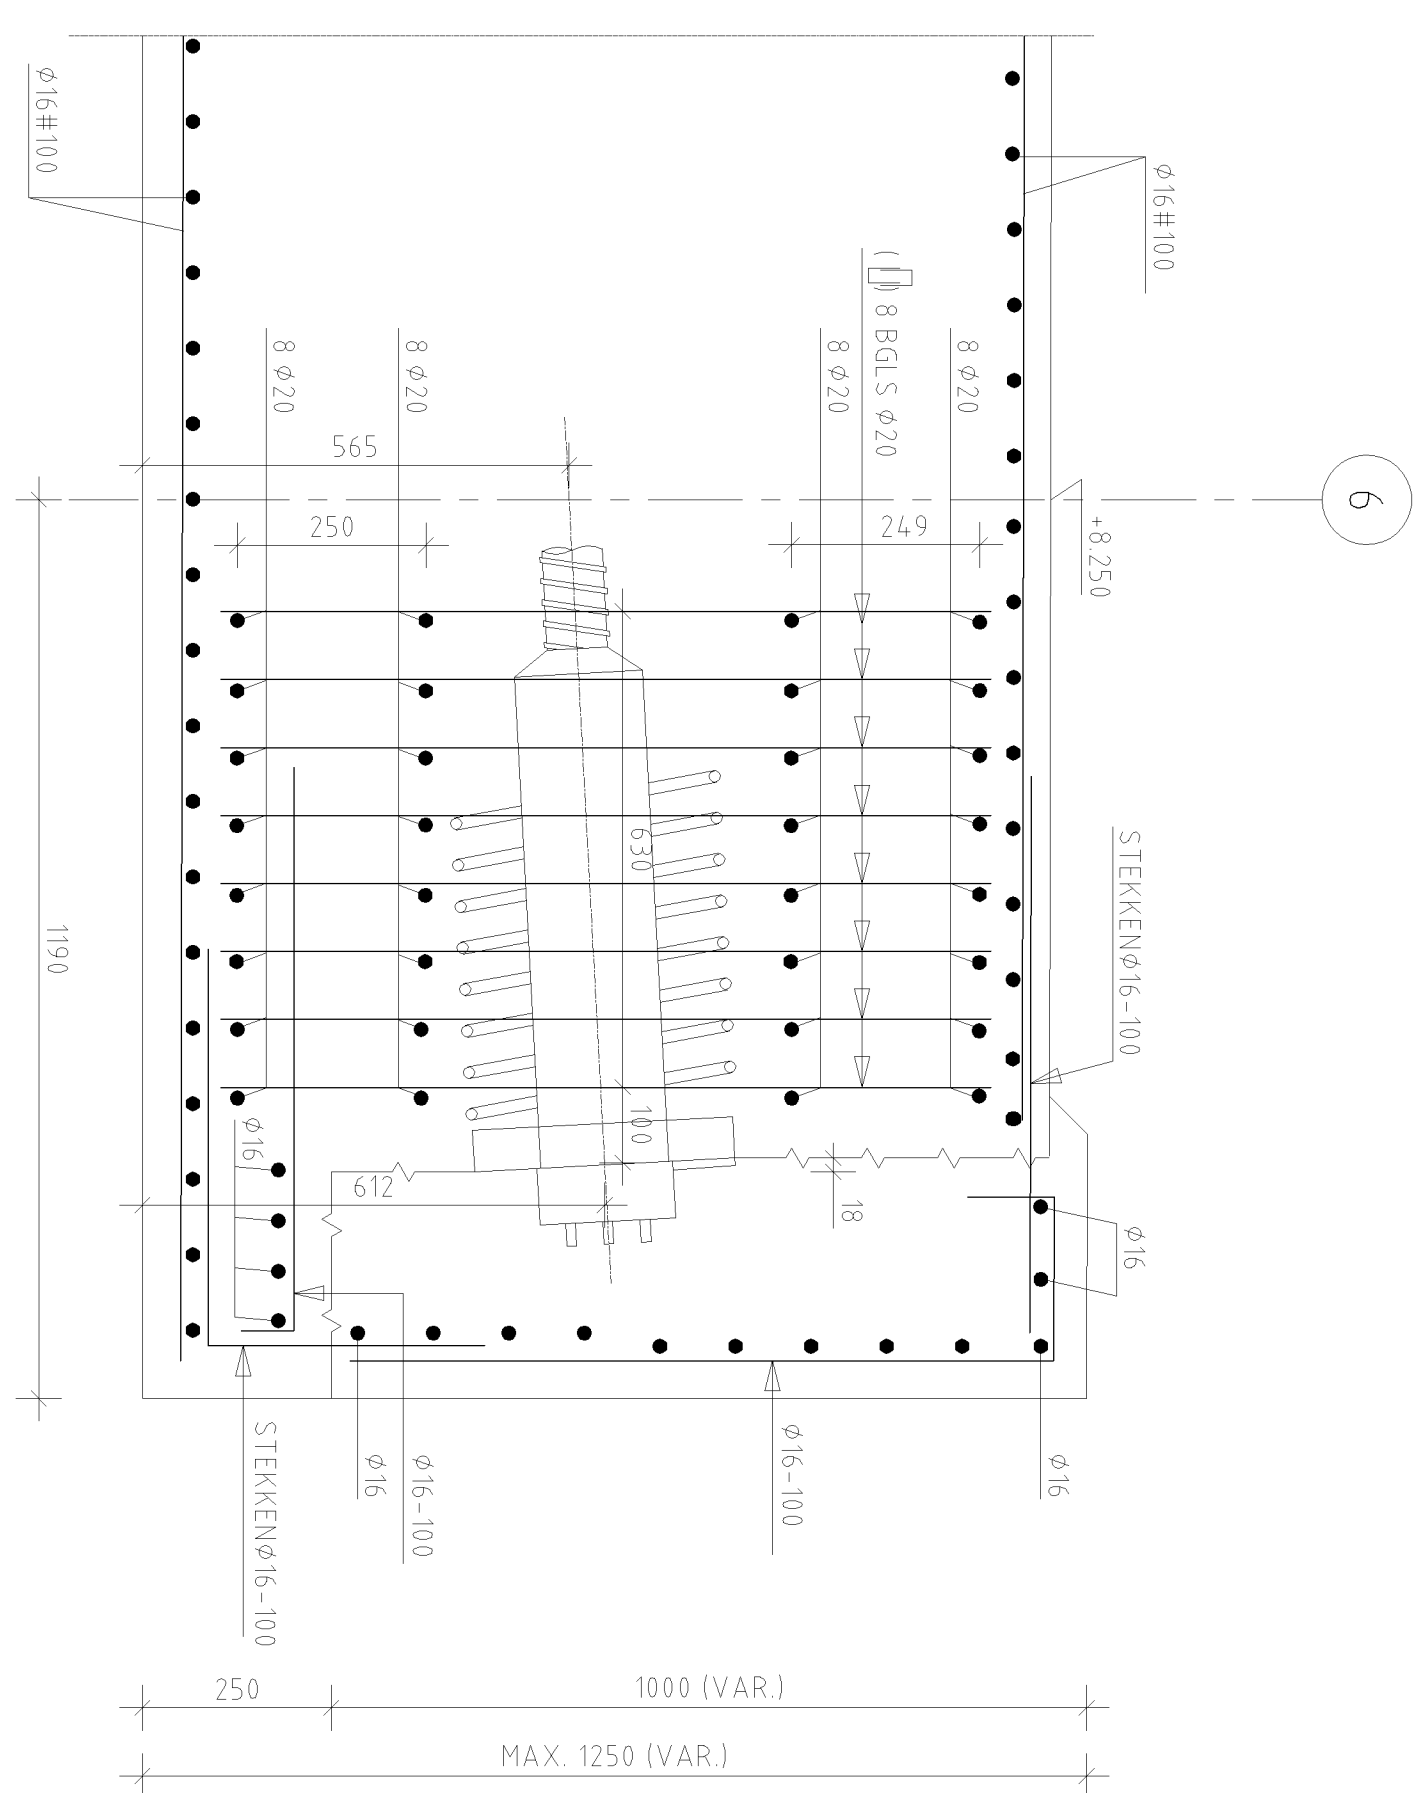
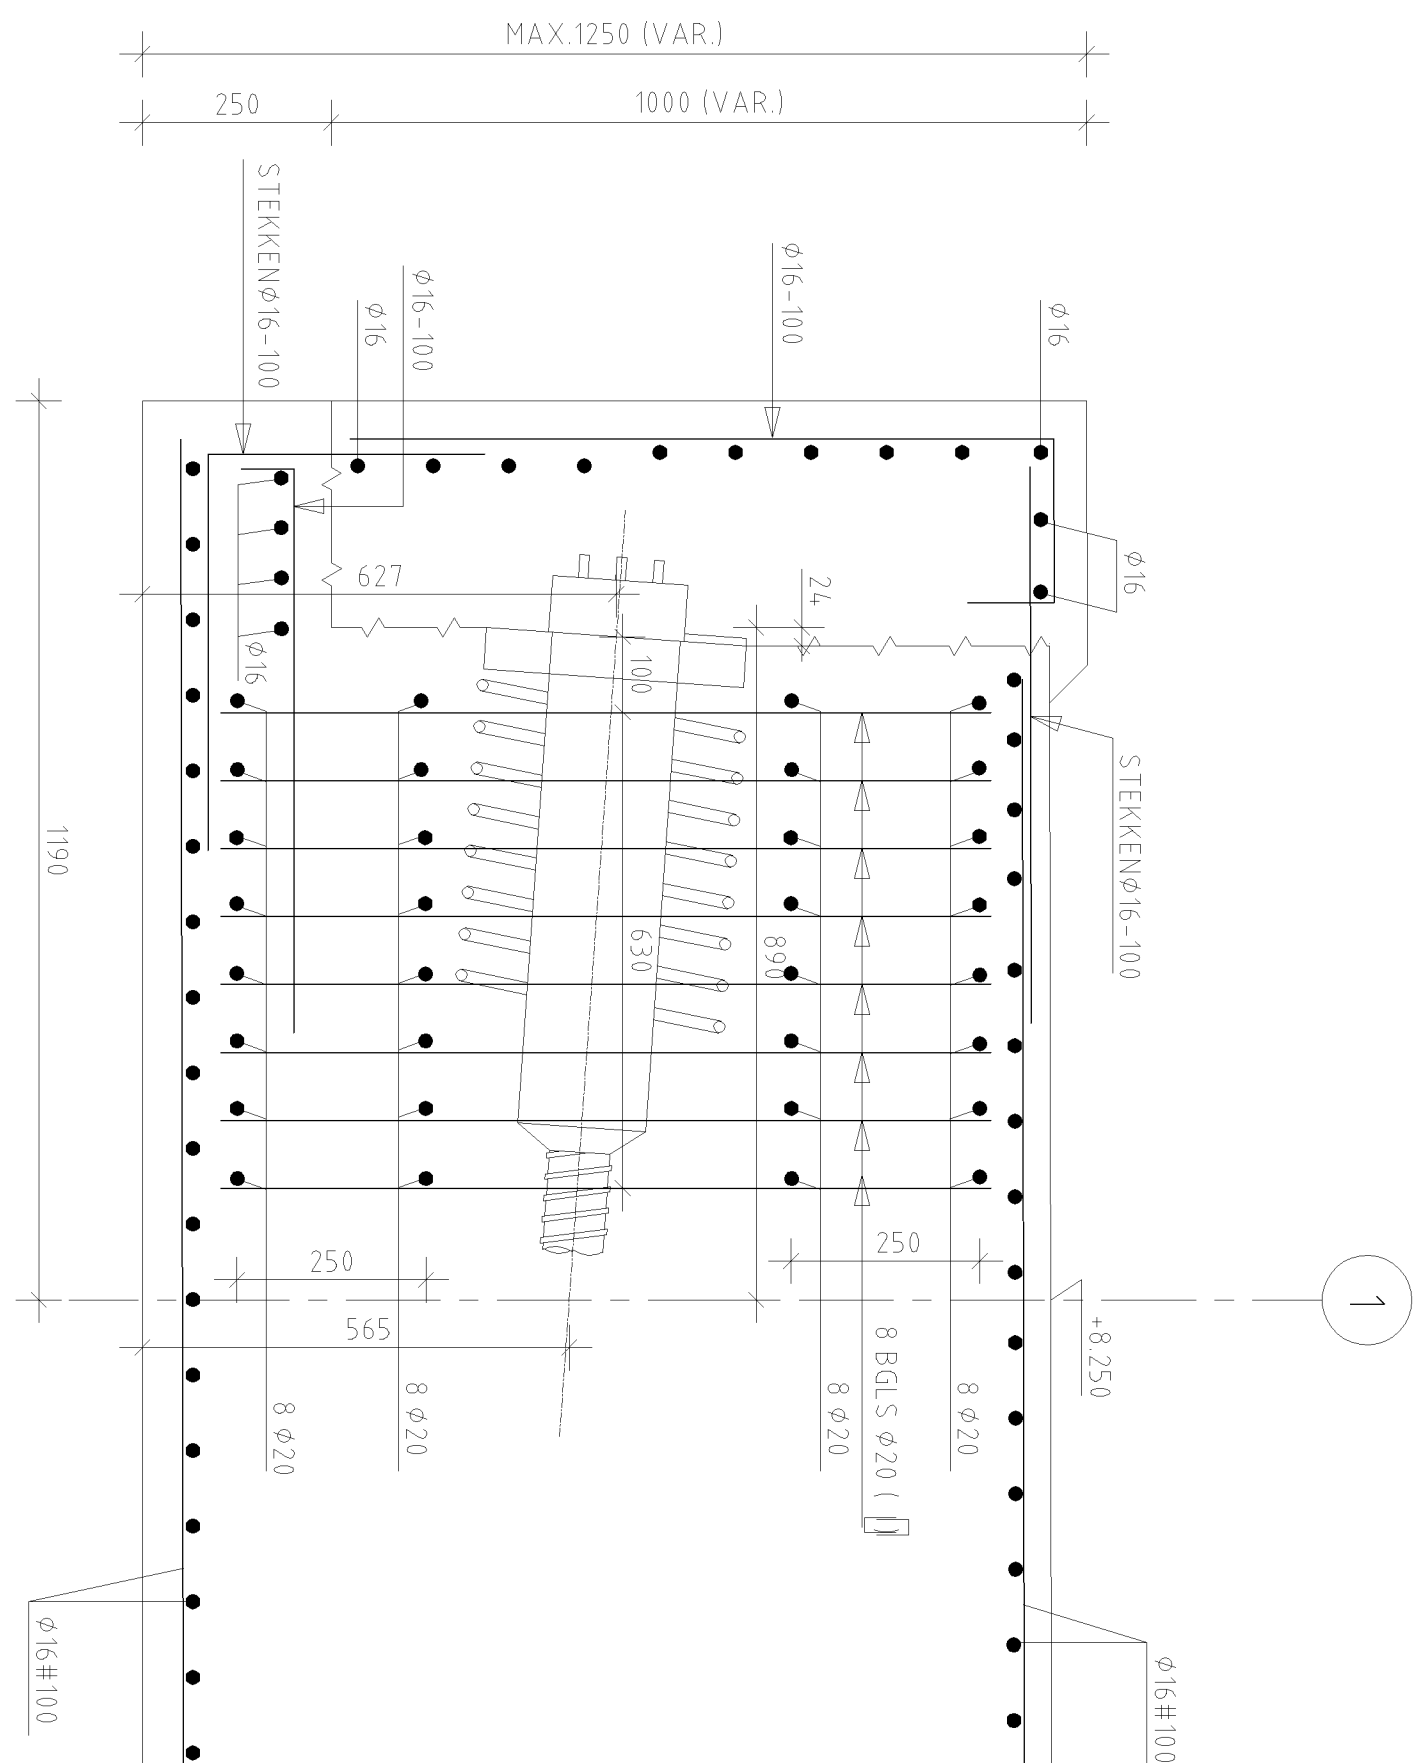
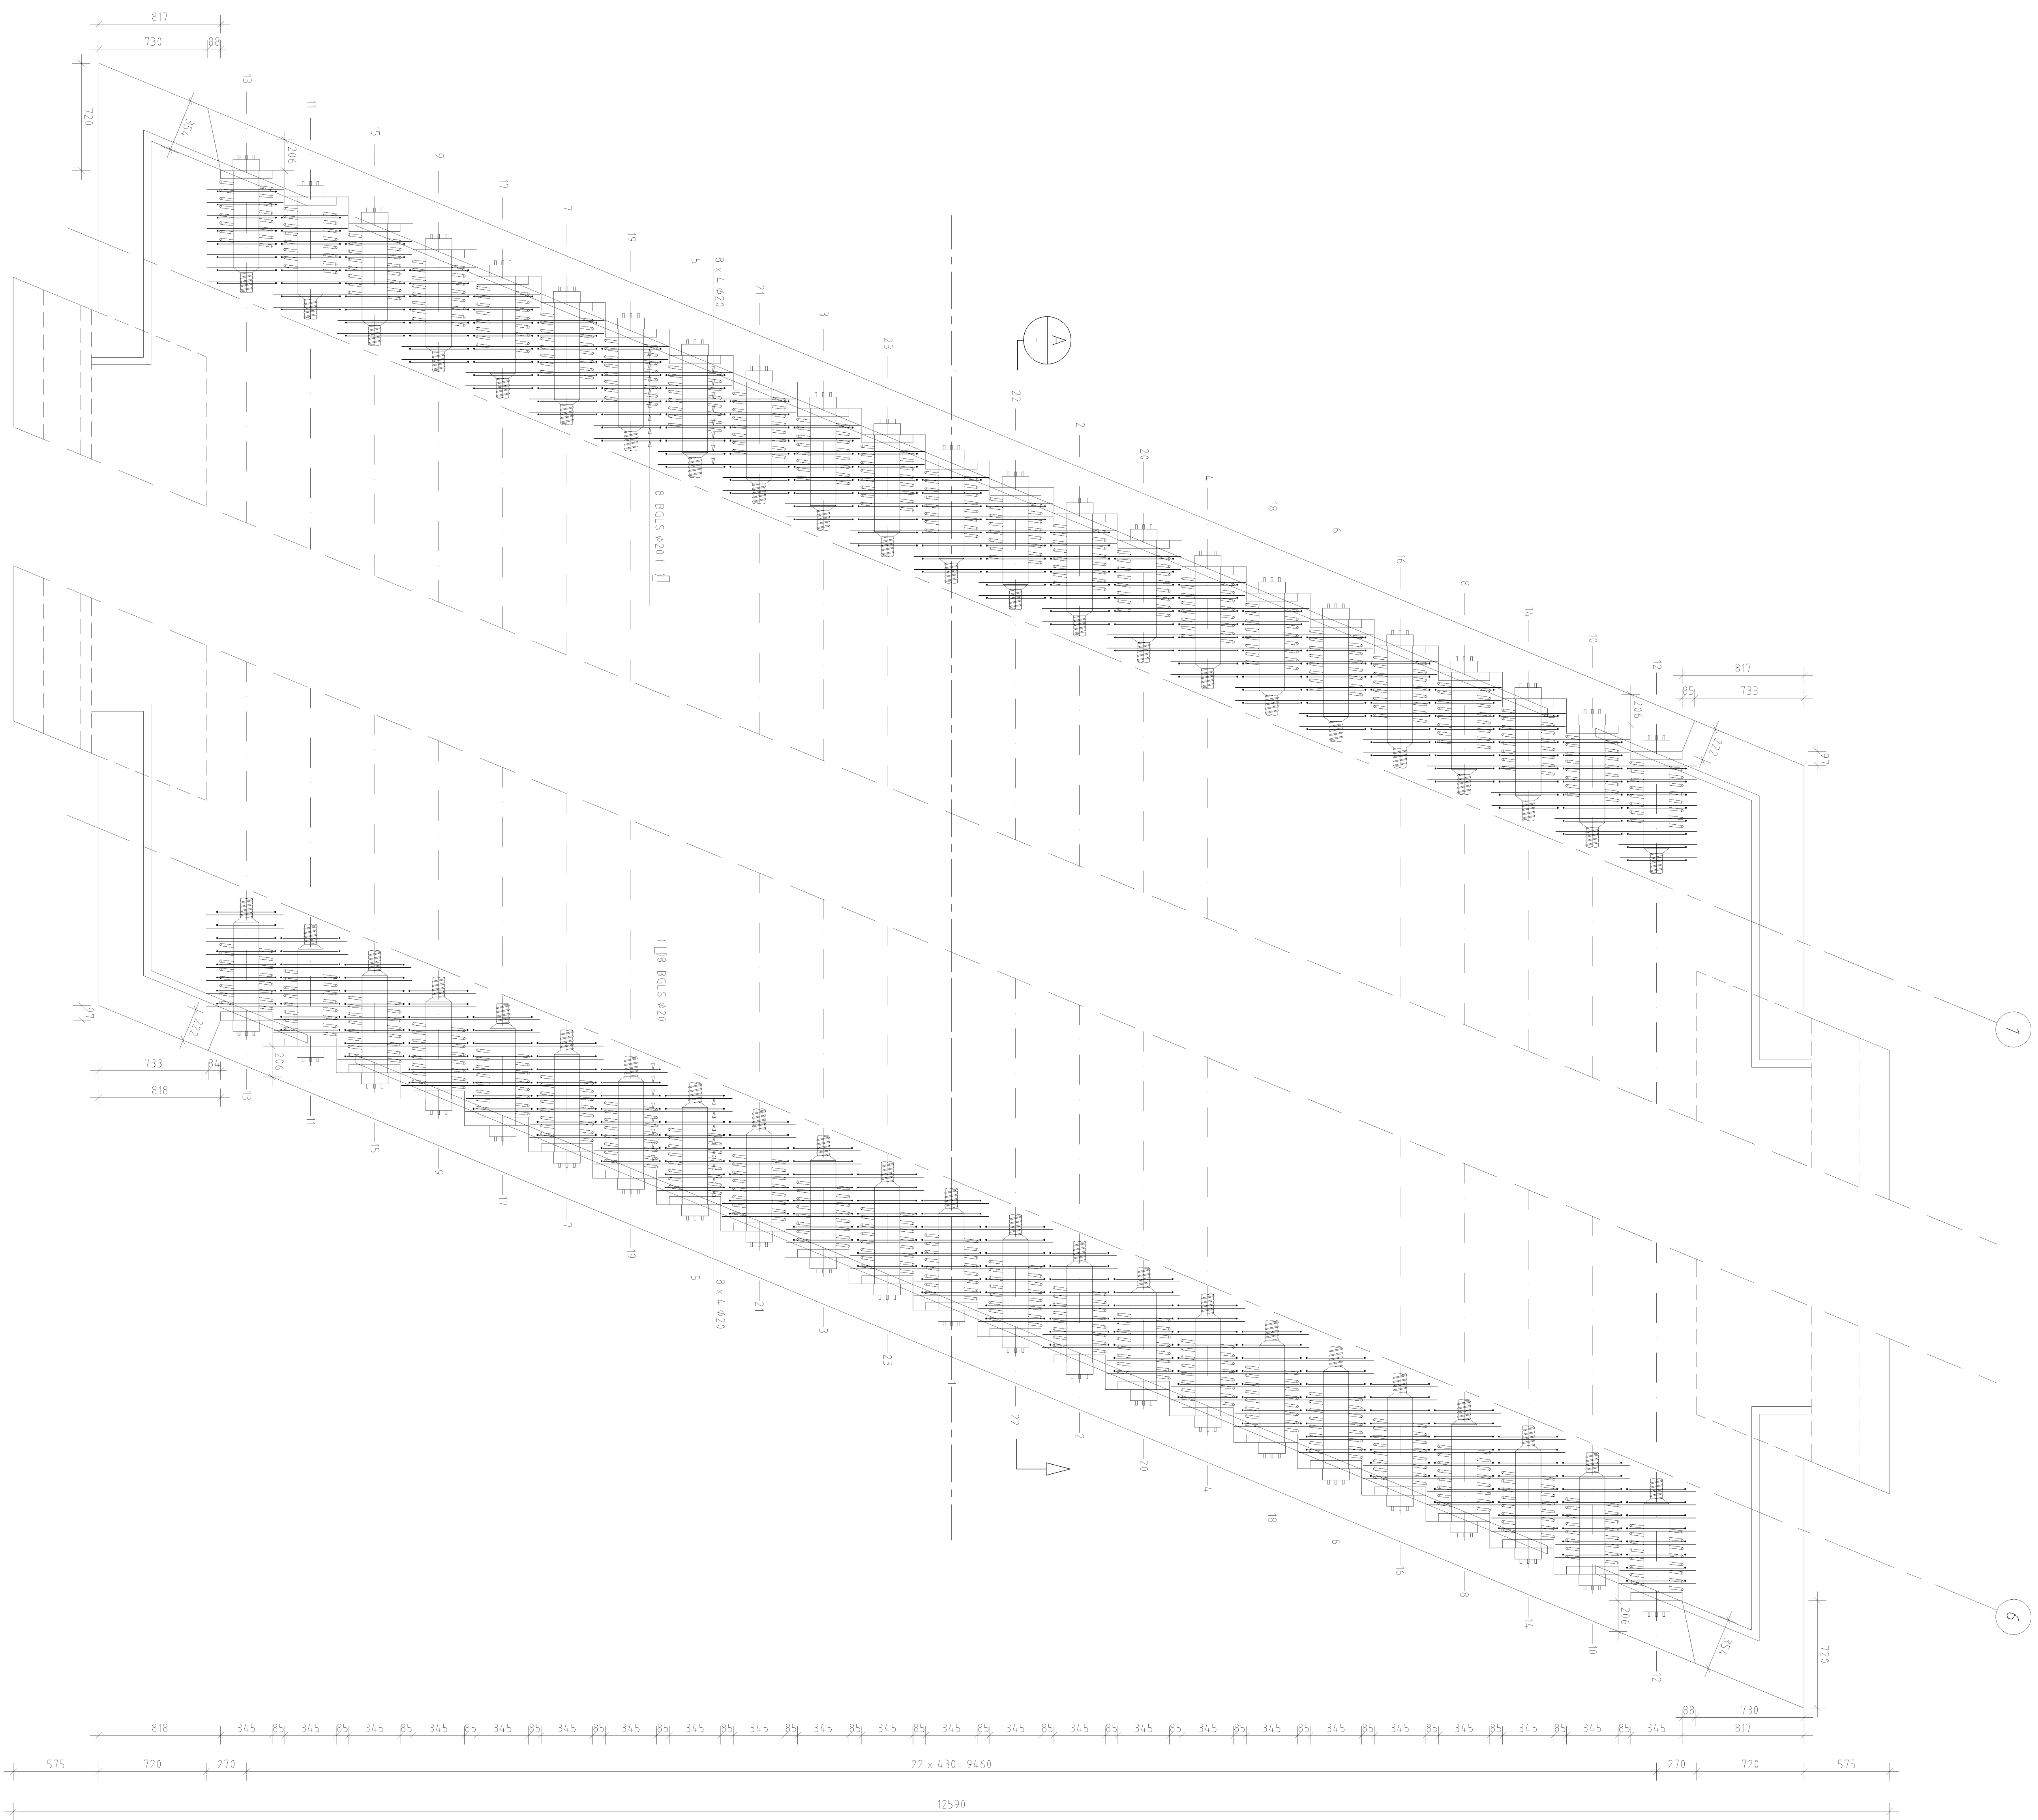


OPMERKINGEN:

- MATEN IN MILIMETERS, TENZIJ ANDERS AANGEGEVEN
- HOOGTEMATEN IN METERS T.O.V N.A.P
- UITEVENDE HOEKEN VOORZIELEN VAN VELLINGSKANTEN 20x20 MM
- VOOR AARDING ZIE TEKENING 14-274

[illegible]

HART BETONCONSTRUCTIE

1e LAAG

2e LAAG