




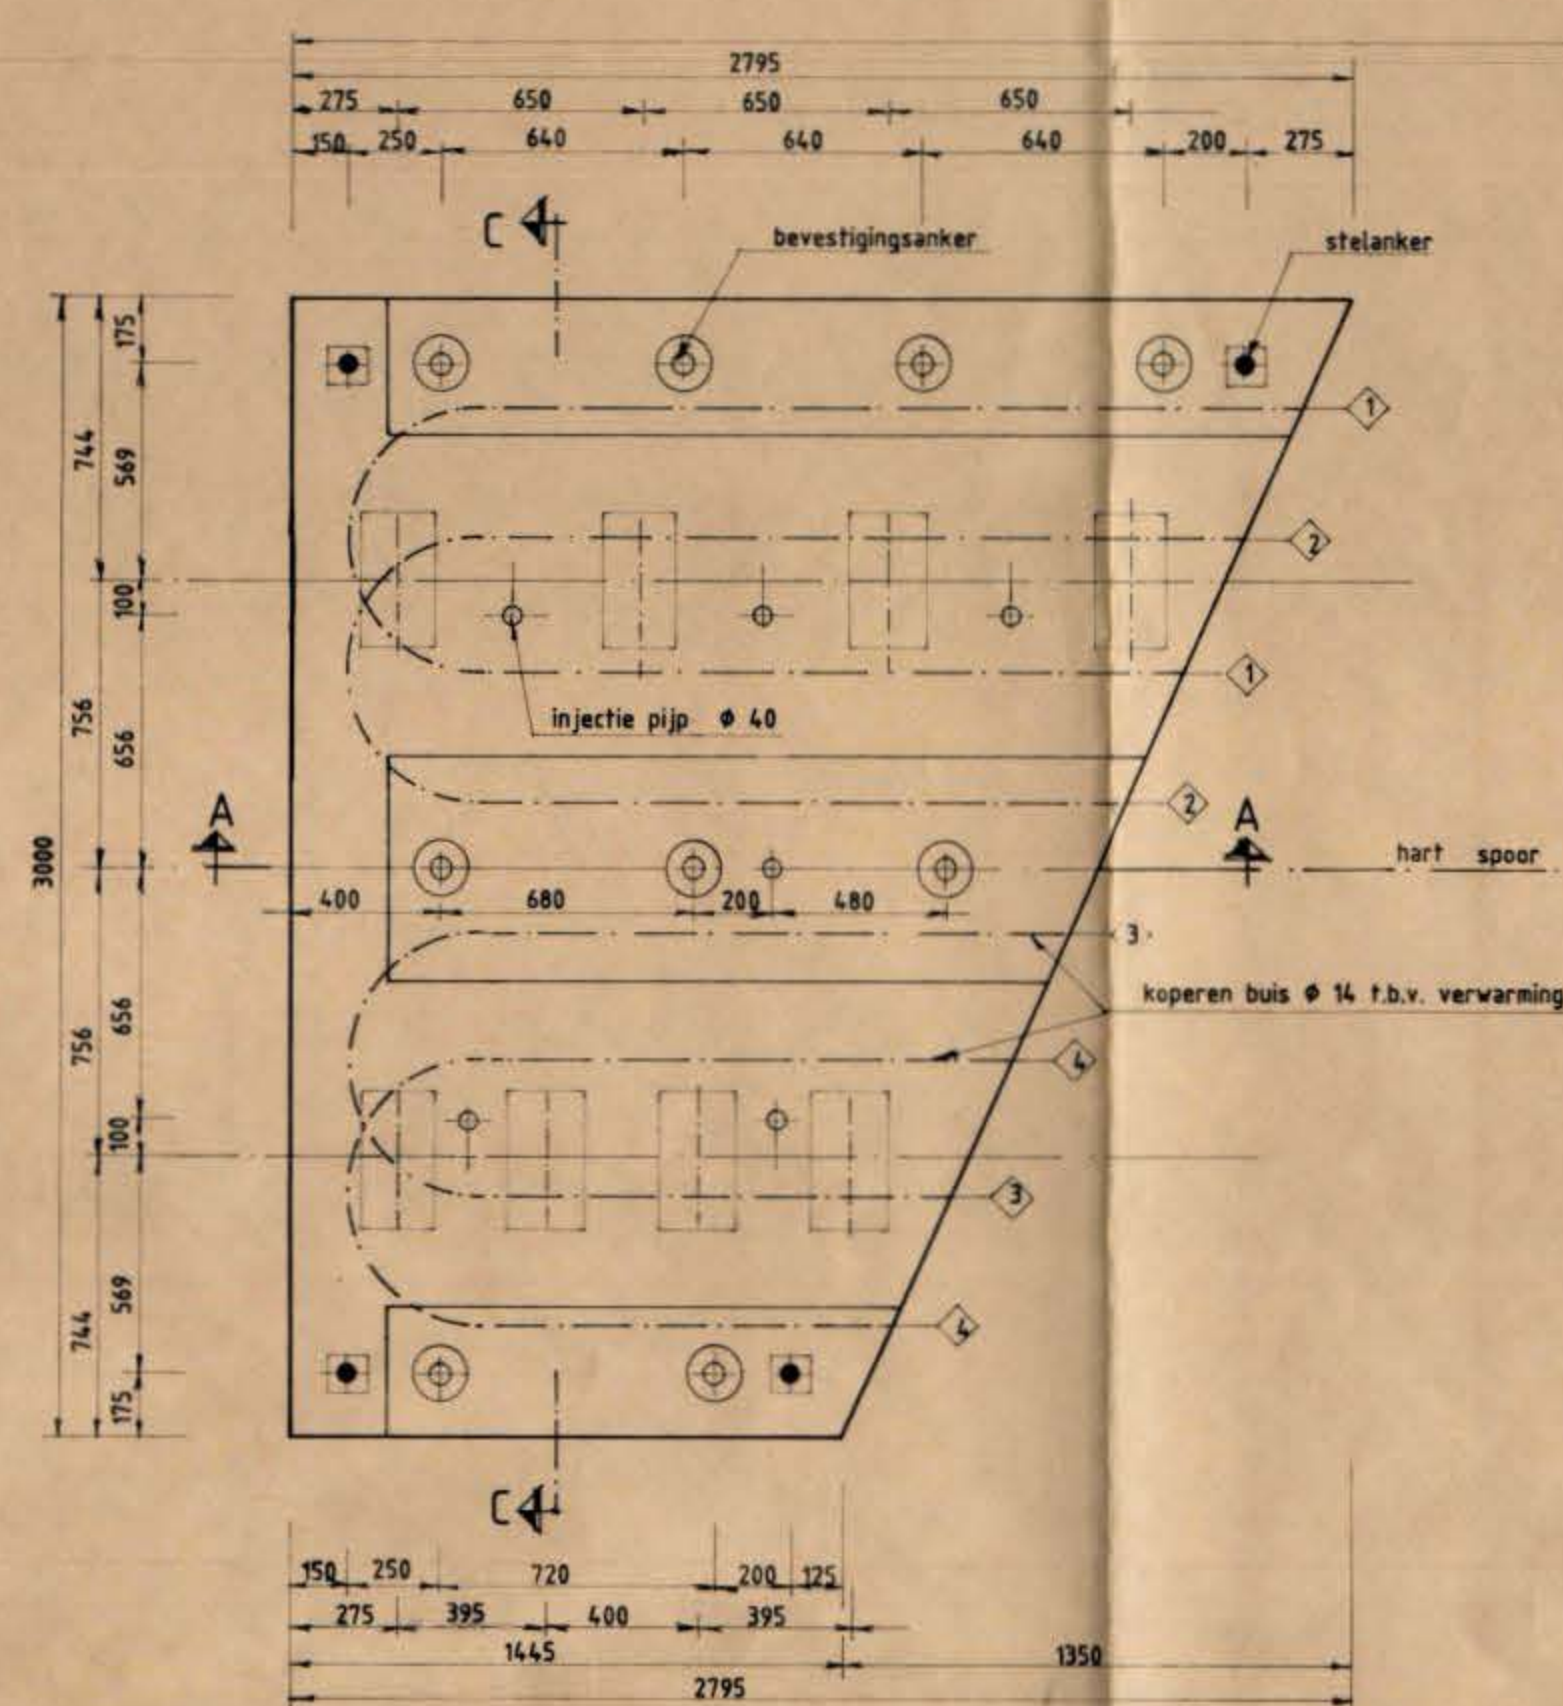


BOVENAANZICHT SPOORPLAATJE TYPE A

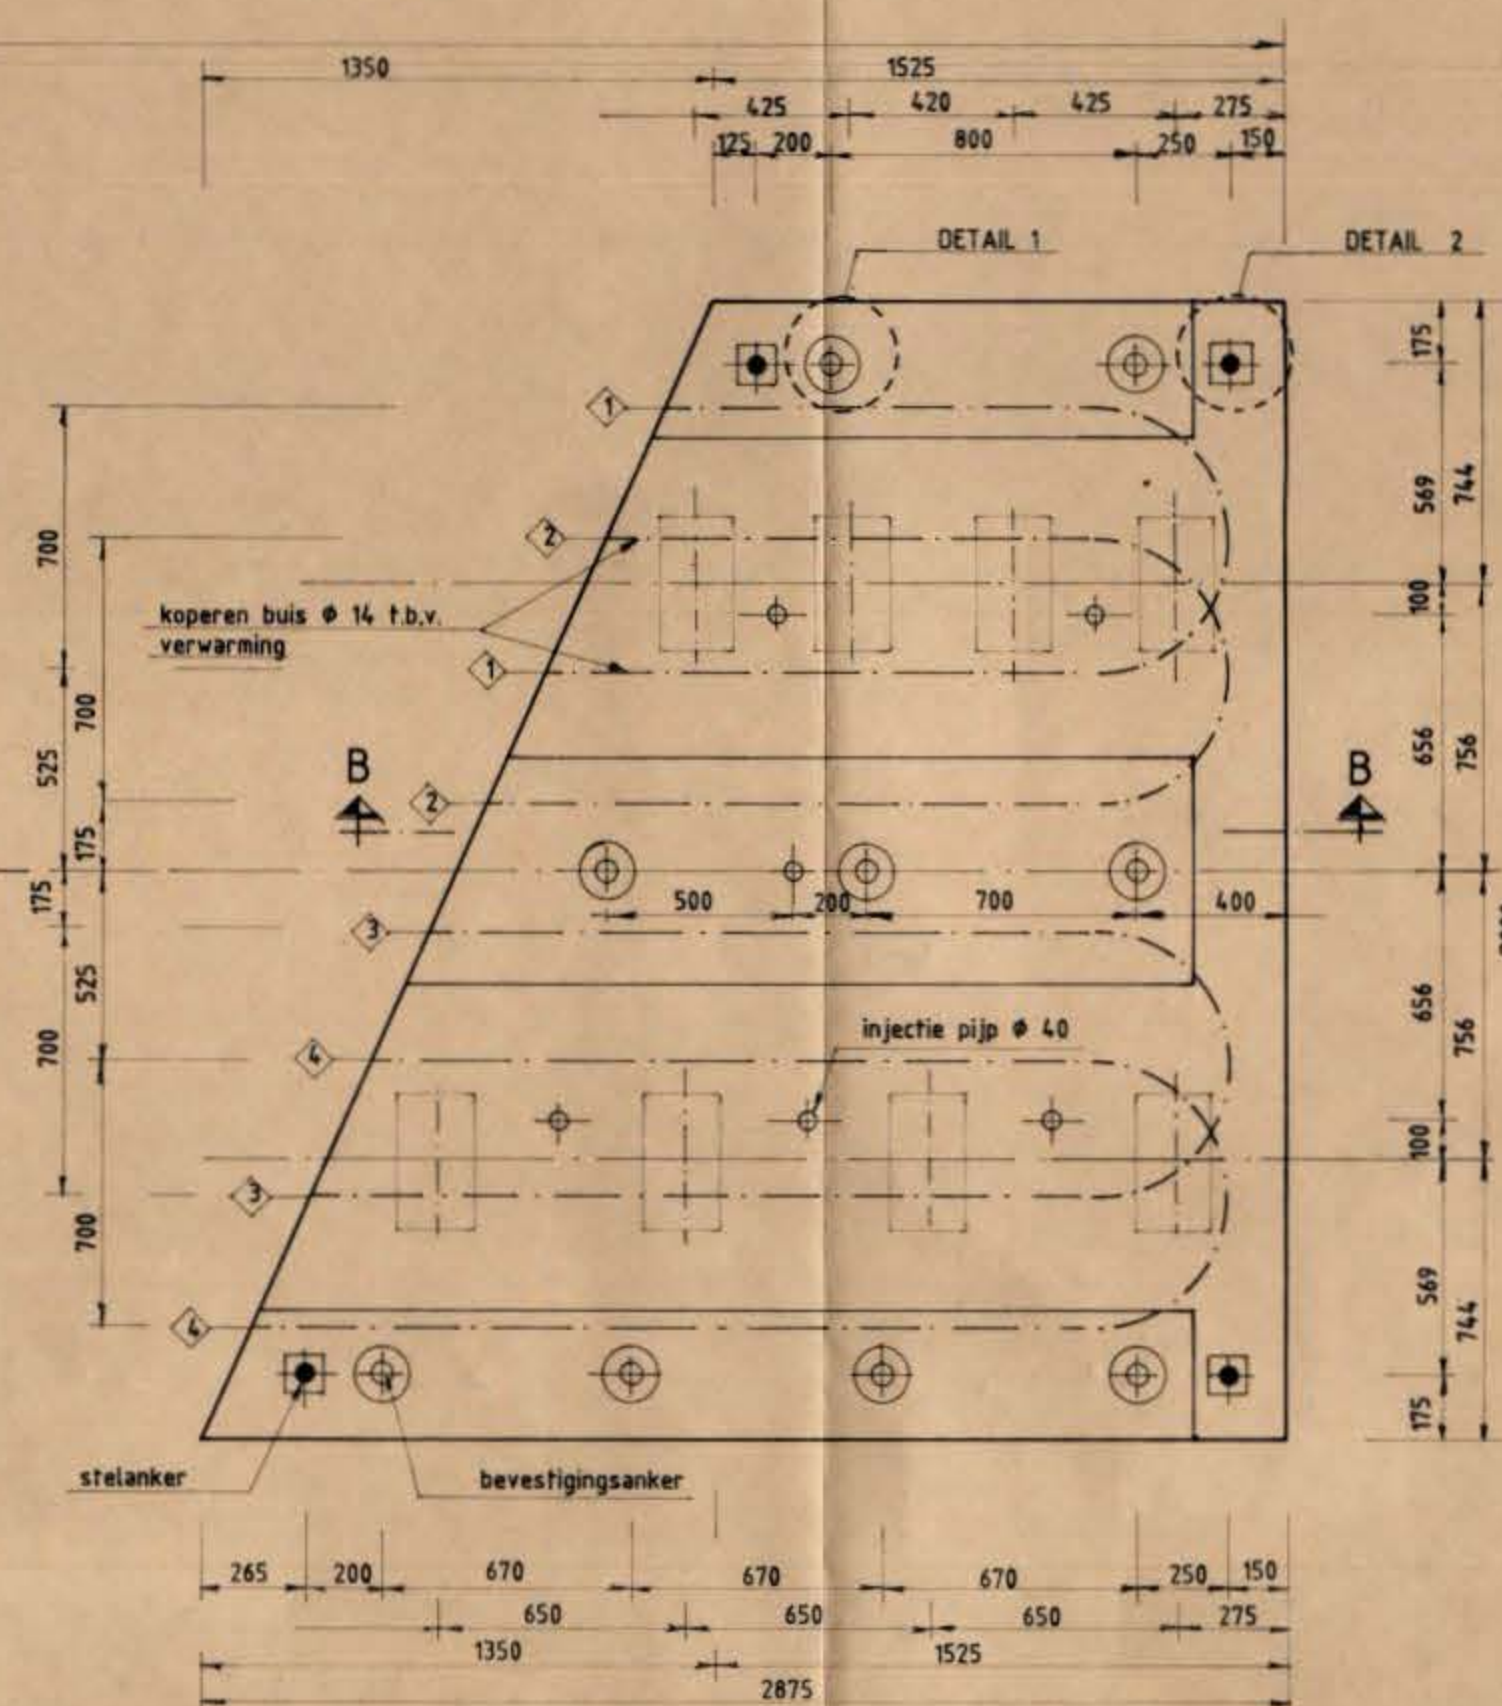


BOVENAANZICHT SPOORPLAATJE TYPE B

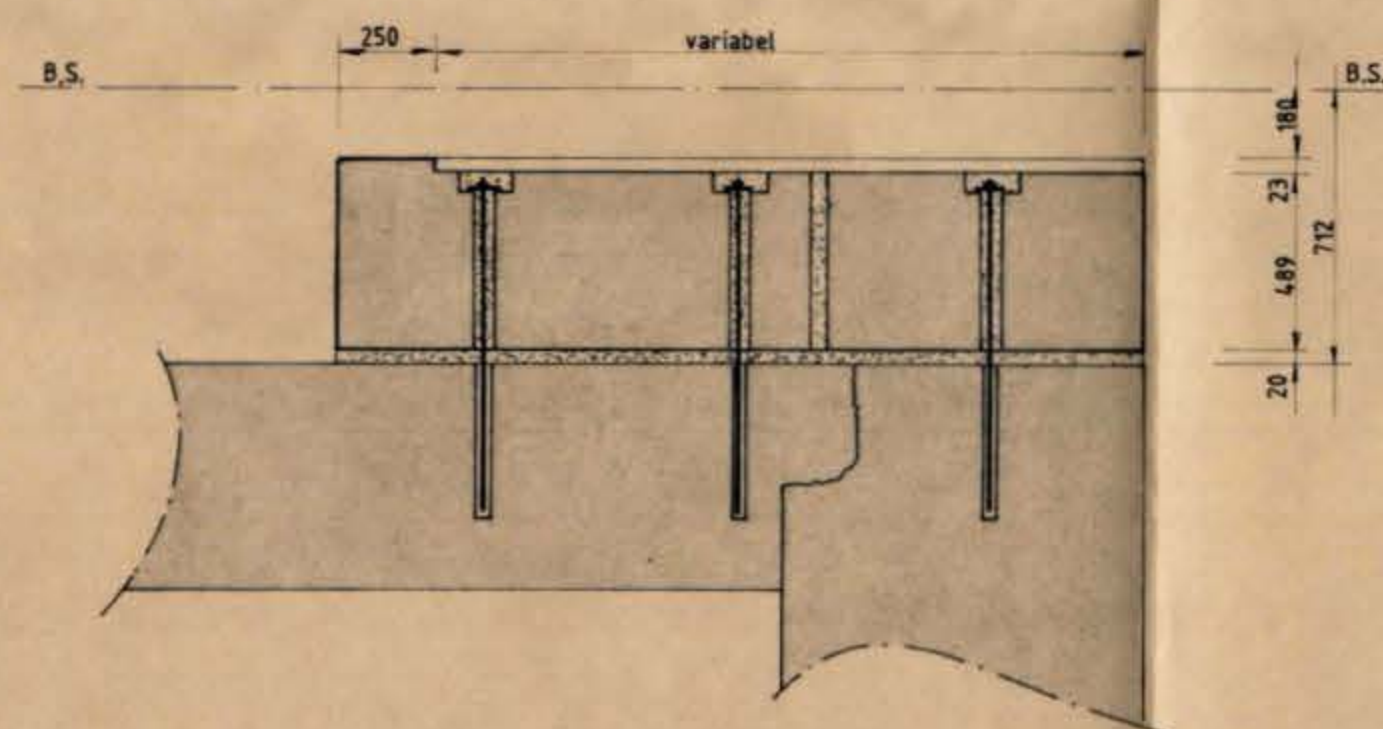


DOORSNEDE A - A

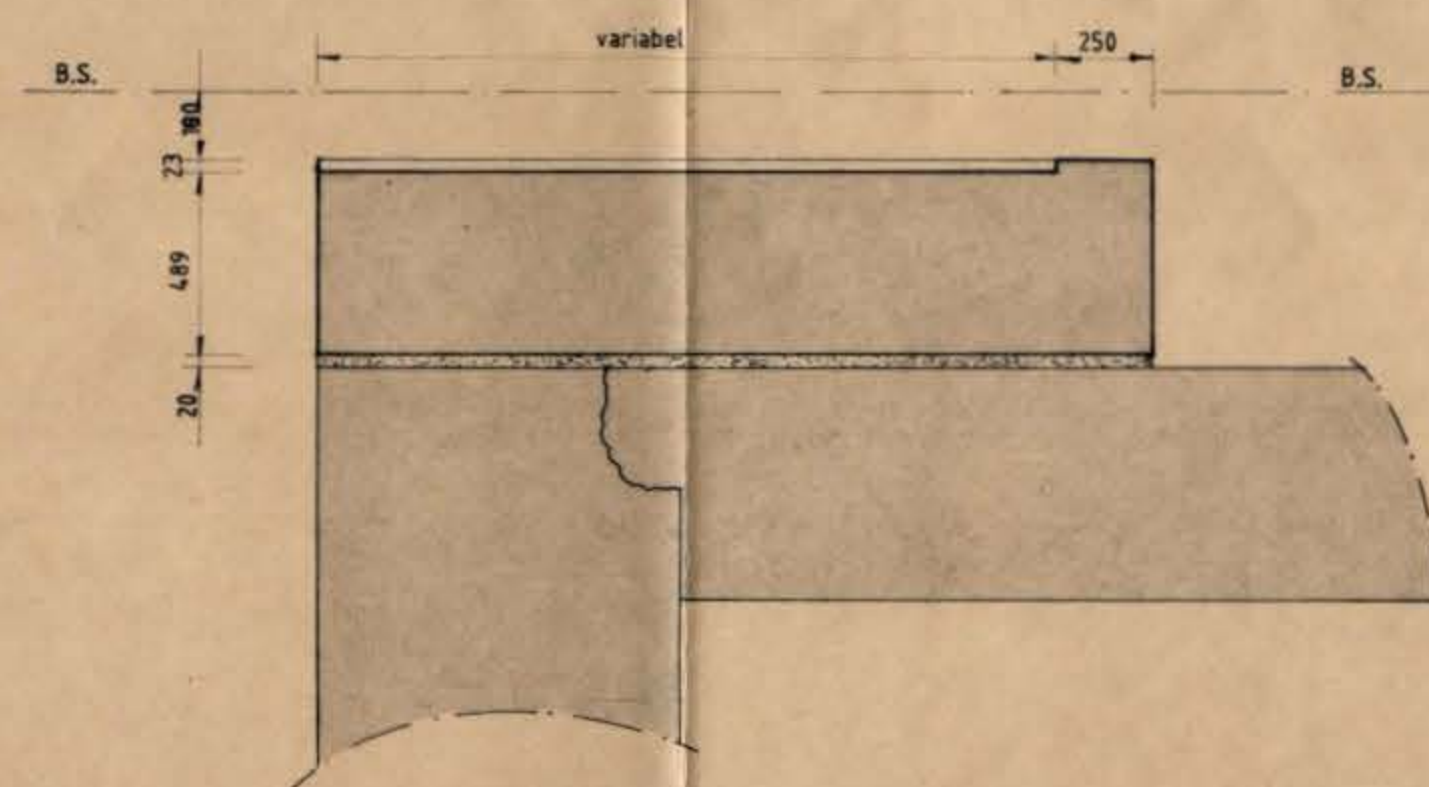

DOORSNEDE B - B

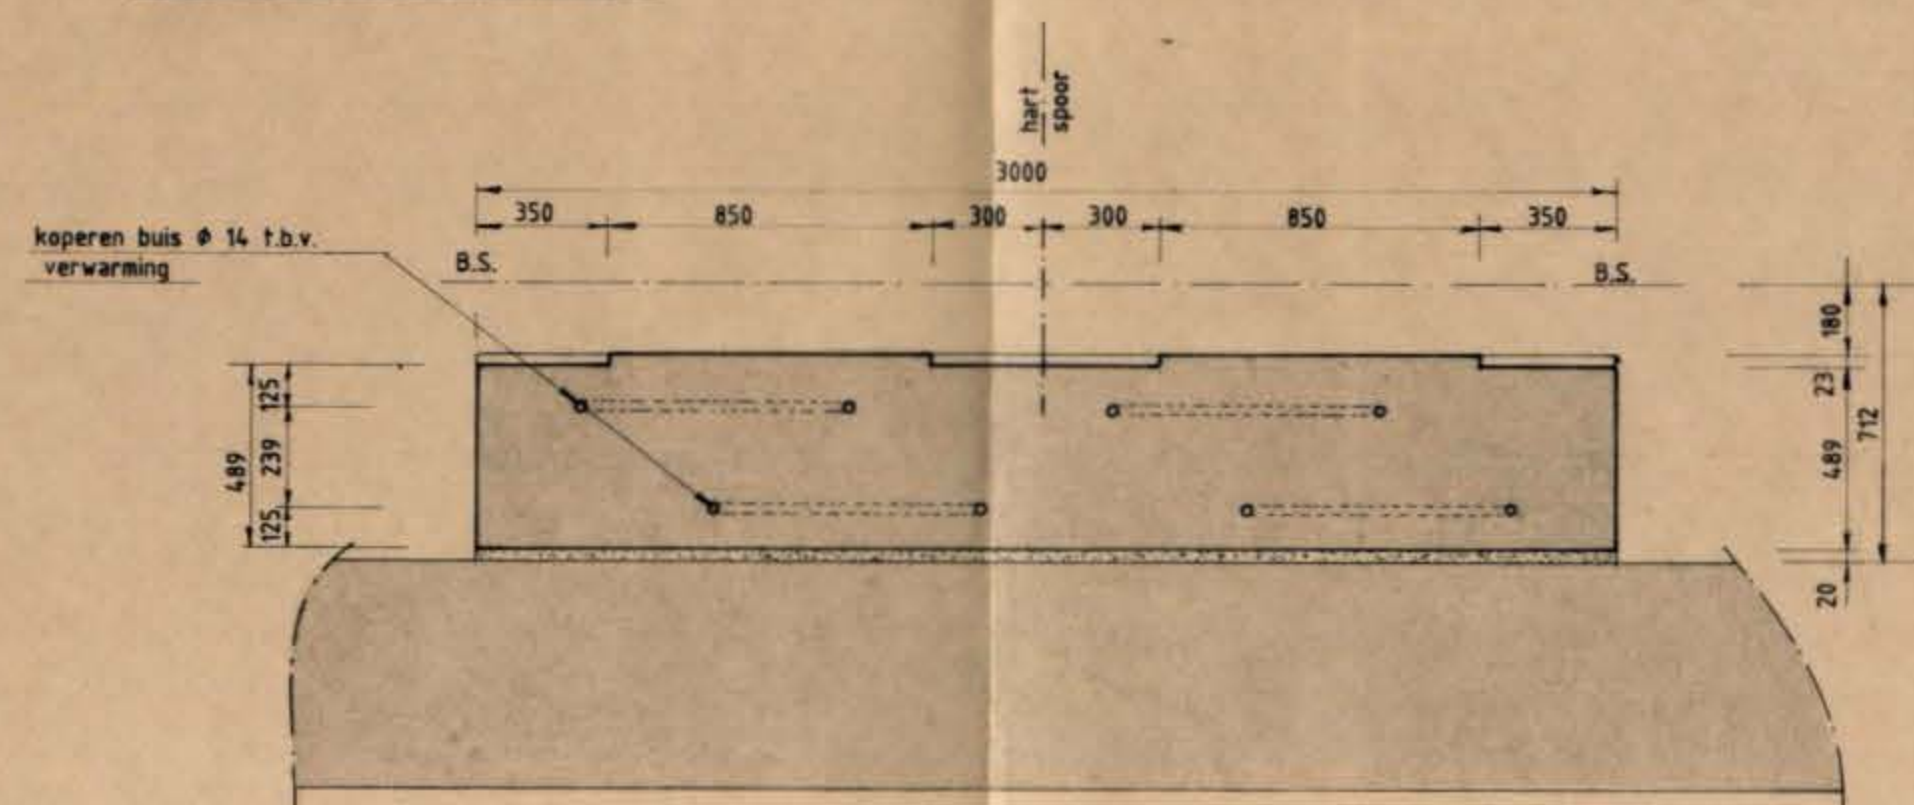


DOORSNEDE C - C

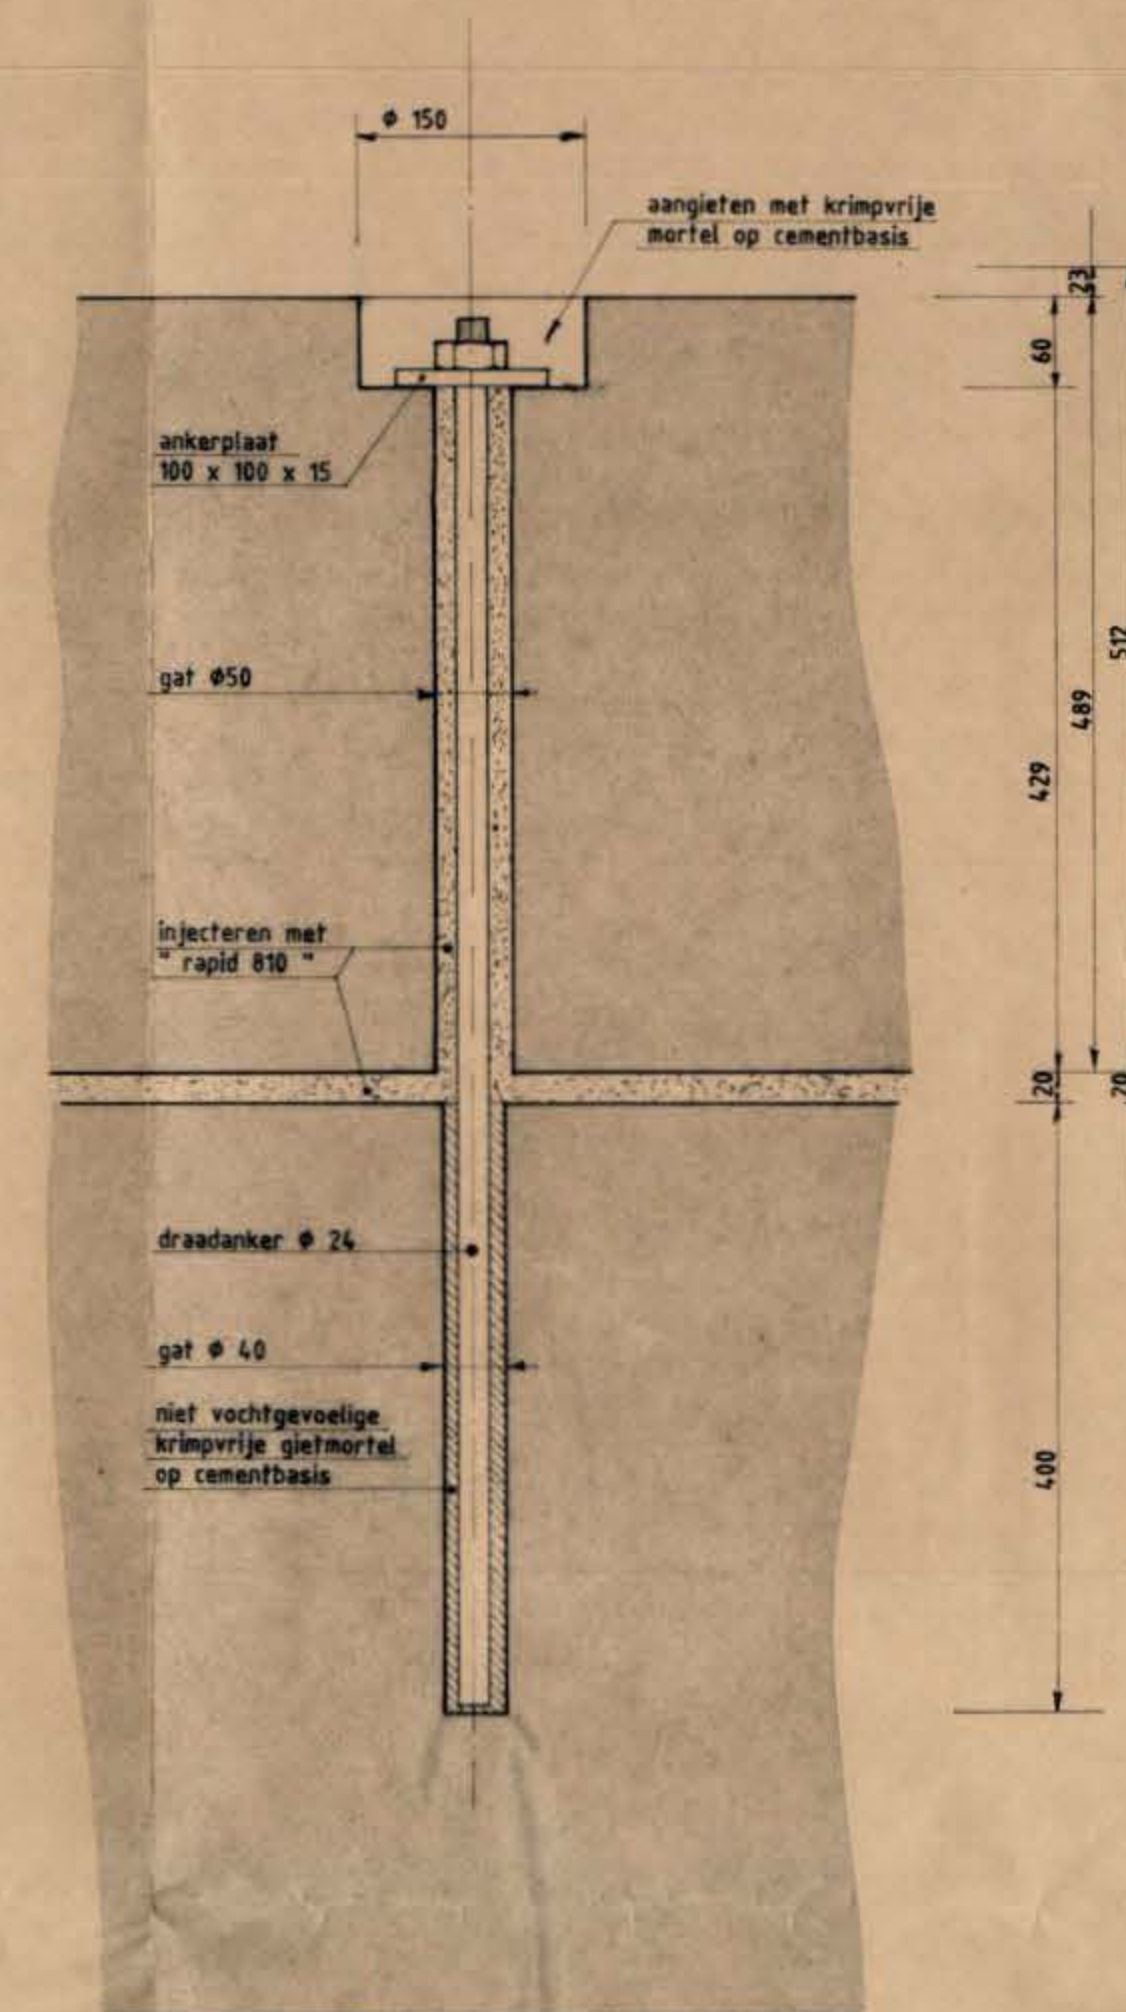

DETAIL 1 BEVESTIGINGS ANKER

36 x uitvoeren

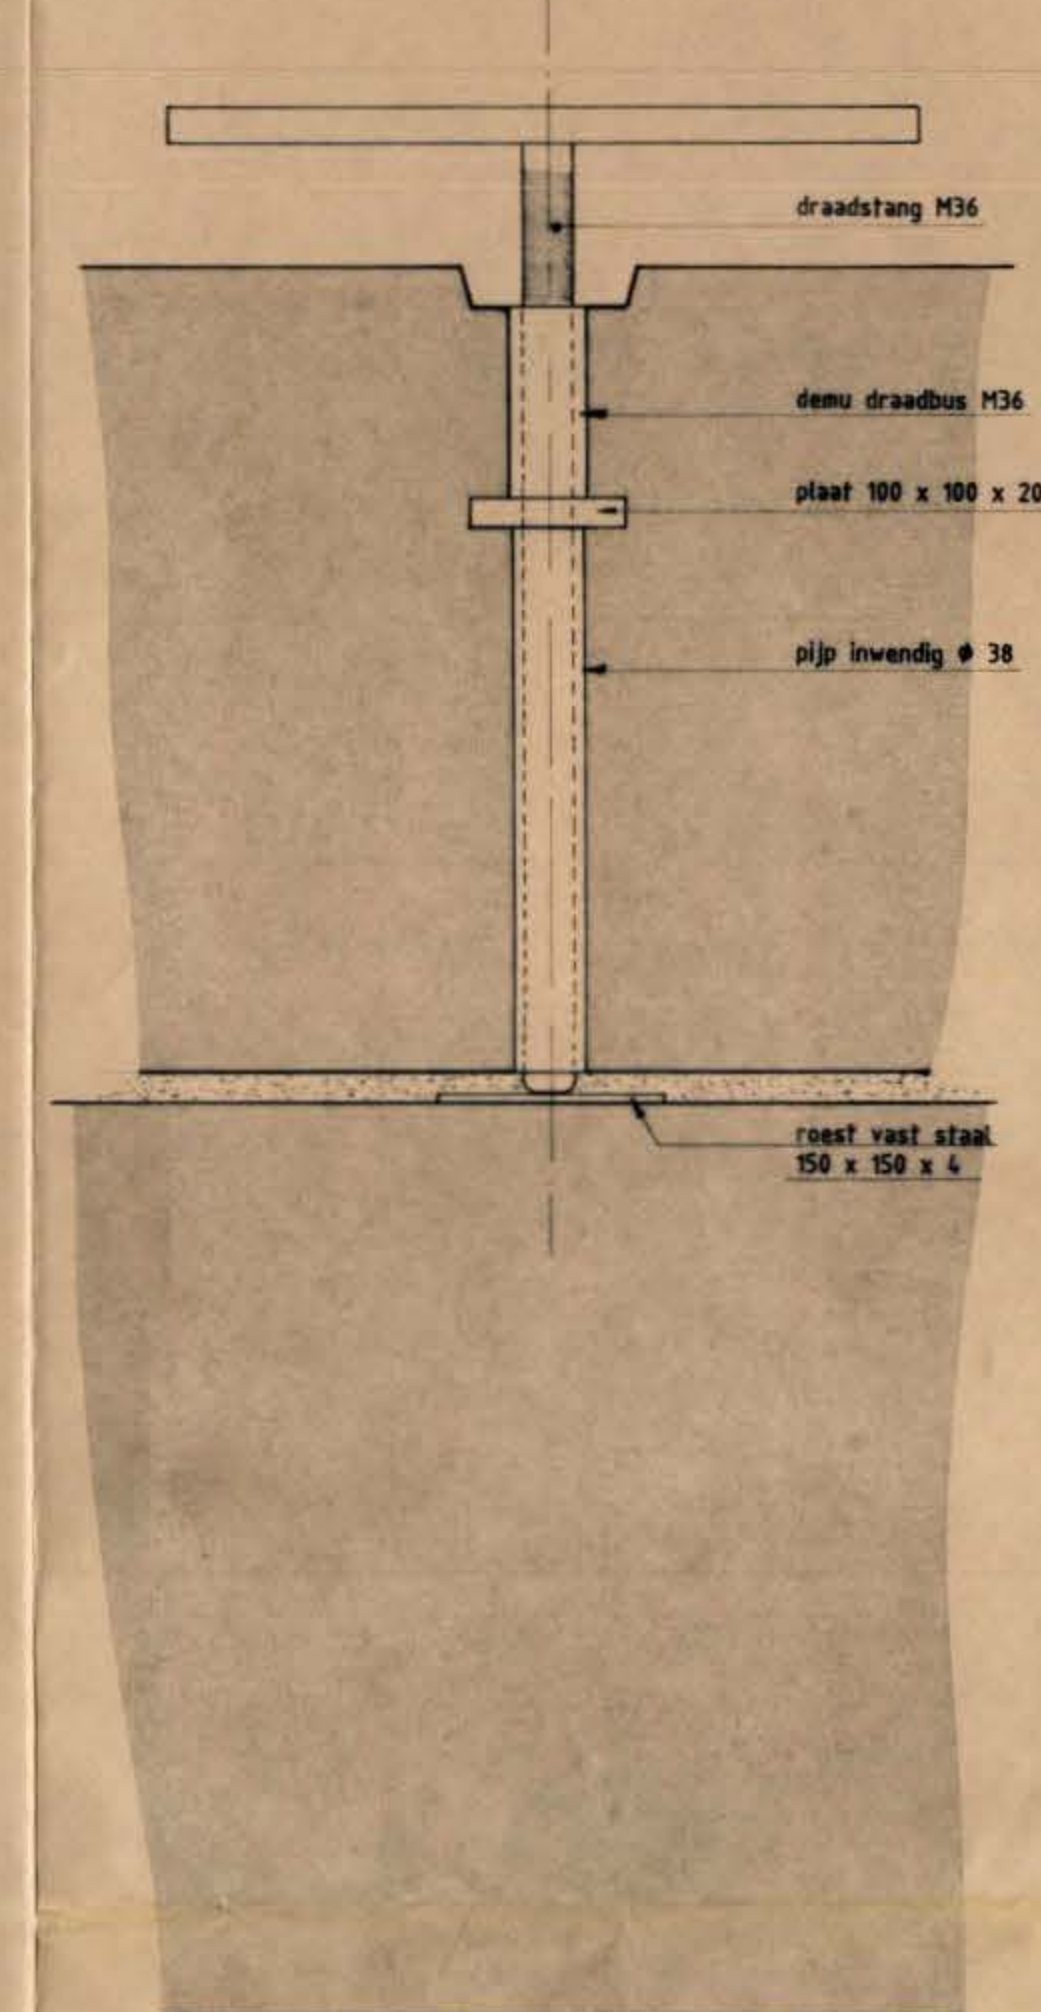

DETAIL 2 STELANKER

16 x uitvoeren

# LEGENDA

Maafvoering in mm.  
Maafvoering f.o.v. B.S. gerekend met NP 46, bij UIC 54 B.S. 13 mm hoger  
B.S. = ± 4370 - N.A.P.  
\* gemerkte maten in het werk exact bepalen  
◇ = aansluitpunt verwarming

|                            |                                    |         |         |      |
|----------------------------|------------------------------------|---------|---------|------|
| deze tekening vervaardigt: | deze tekening is vervaardigt door: | schaal  | Am      | Eu   |
| getekend                   | naam                               | 1:20    | 1:15    | 1:10 |
| gecontroleerd              | gecontroleerd                      | formaat | uitgave |      |
| gecontroleerd              | gecontroleerd                      | A1      |         |      |
| gecontroleerd              | gecontroleerd                      |         |         |      |

NV Nederlandse Spoorwegen/Utrecht

Aanpassen landhoofden draaibrug o/d Mark te langeweg

BESTEKTEKENING

421 / 121 / 8.620 / 591 / B