




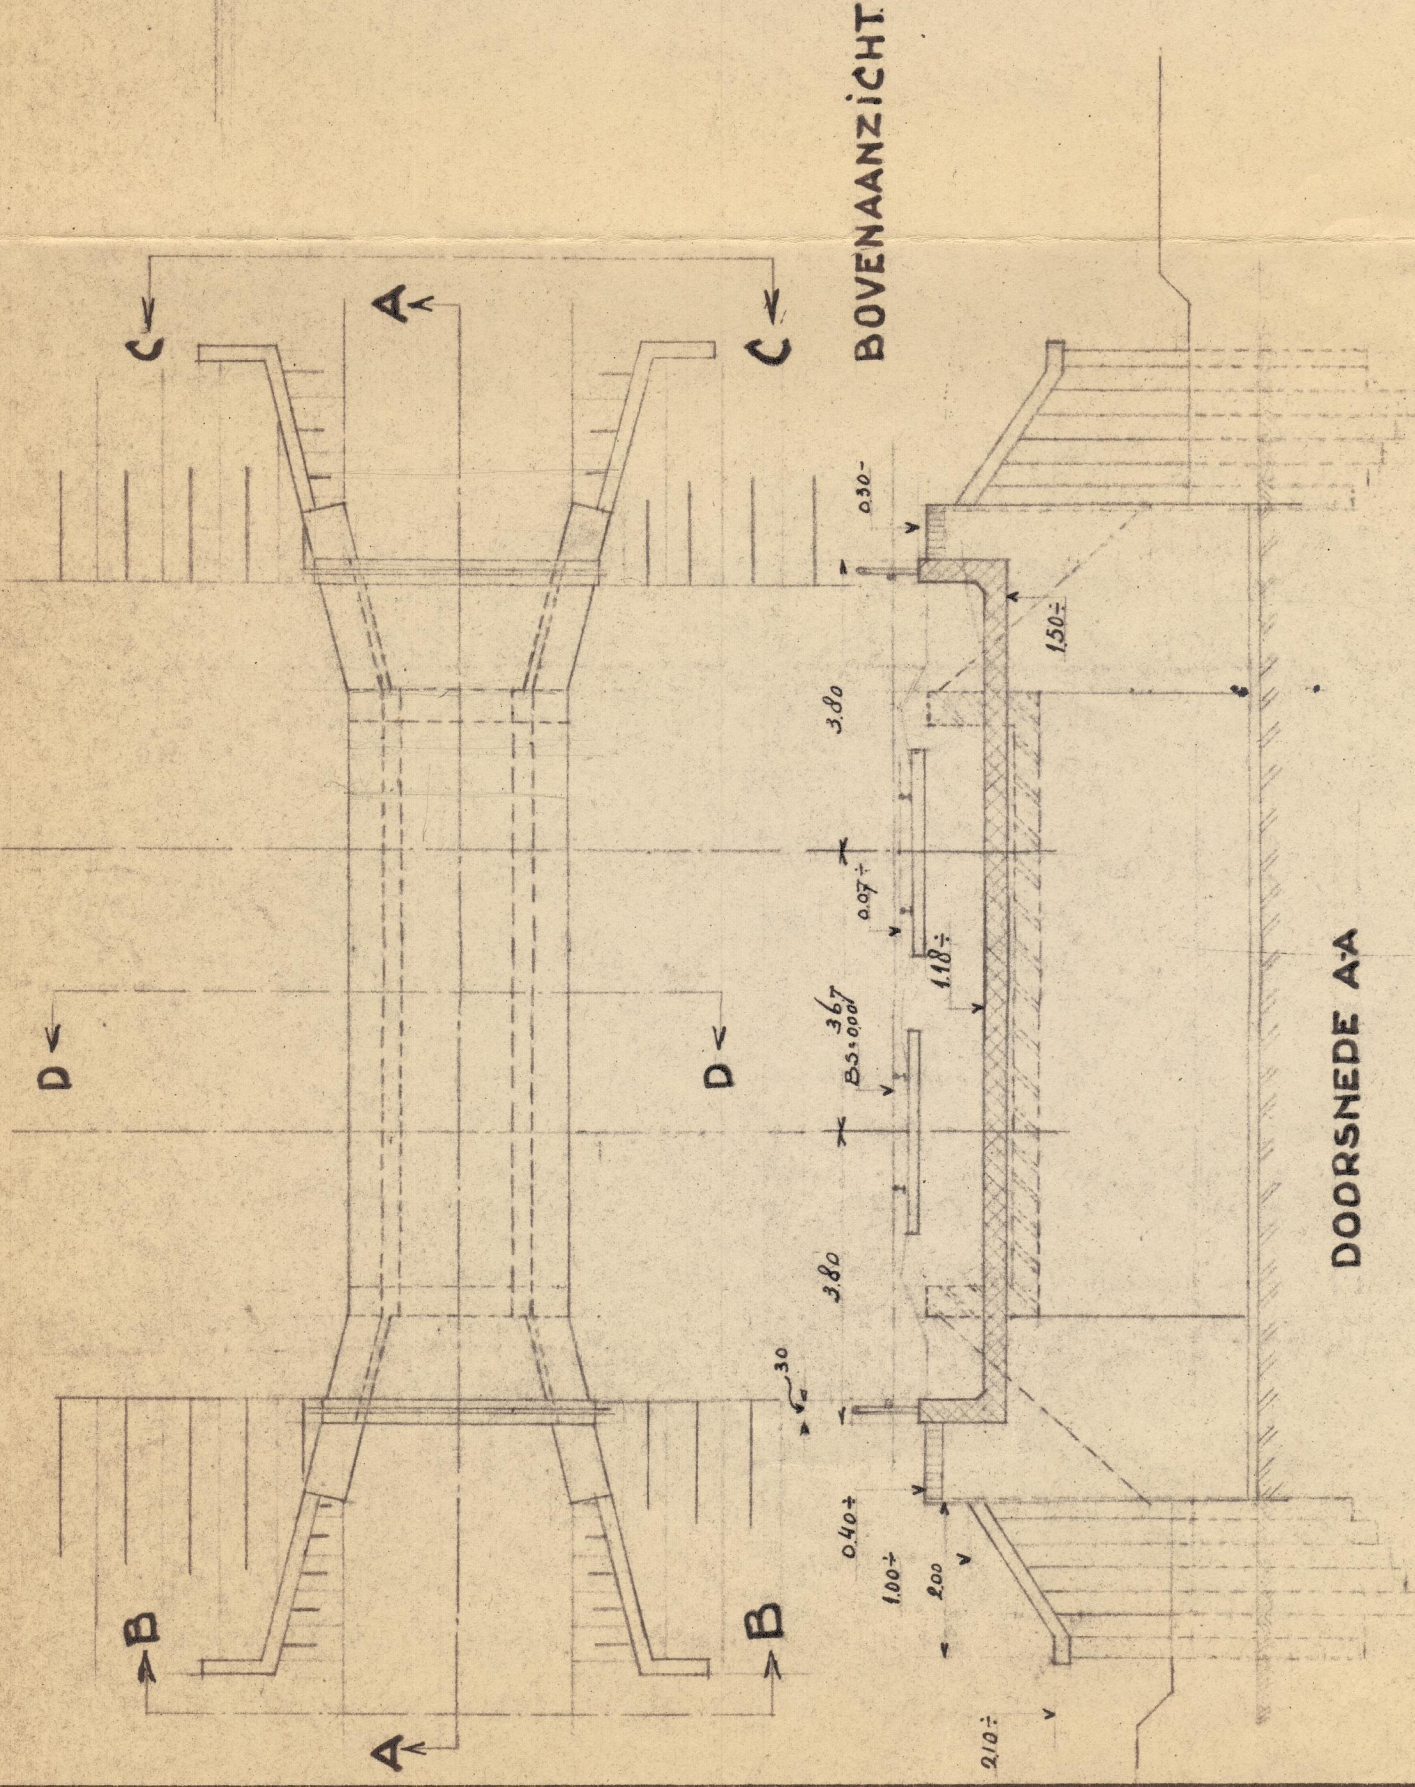


BOVENAANZICHT

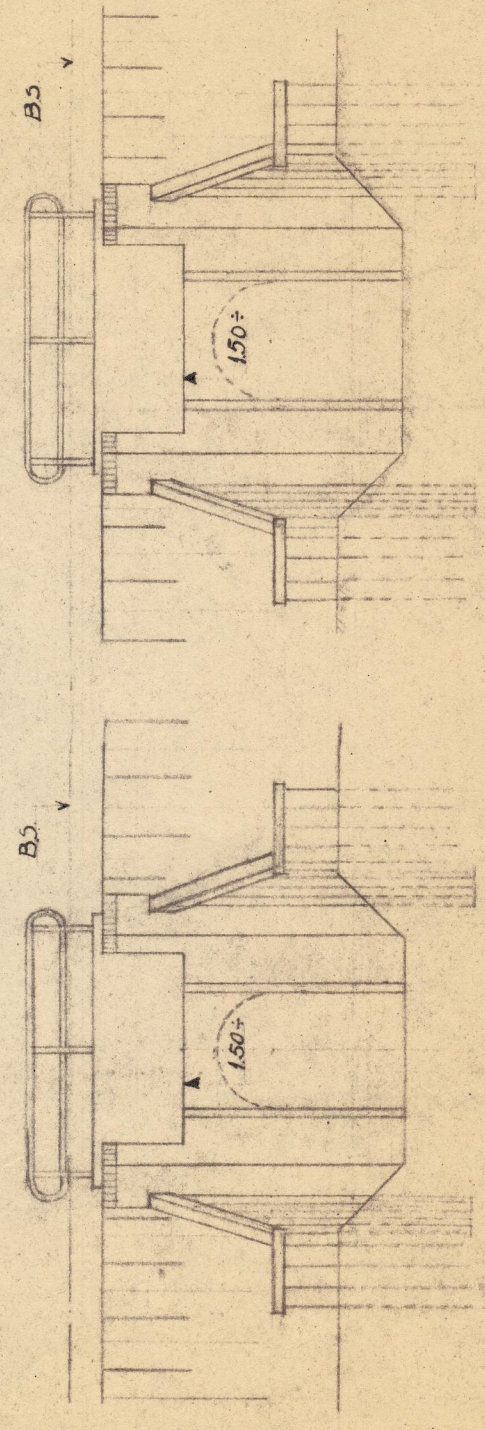

AANZICHT B-B

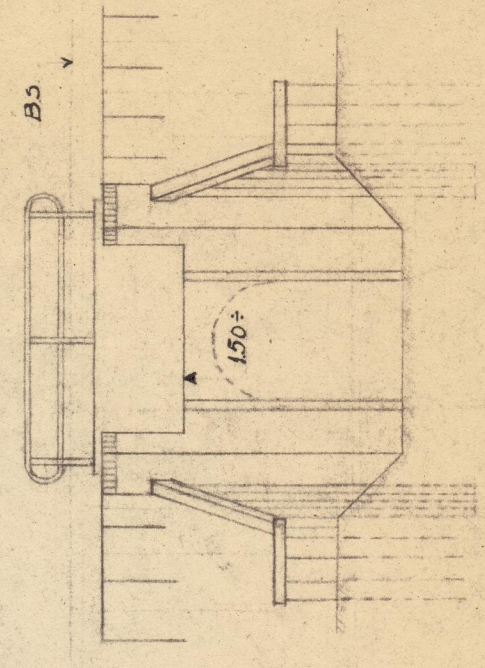


AANZICHT C-C

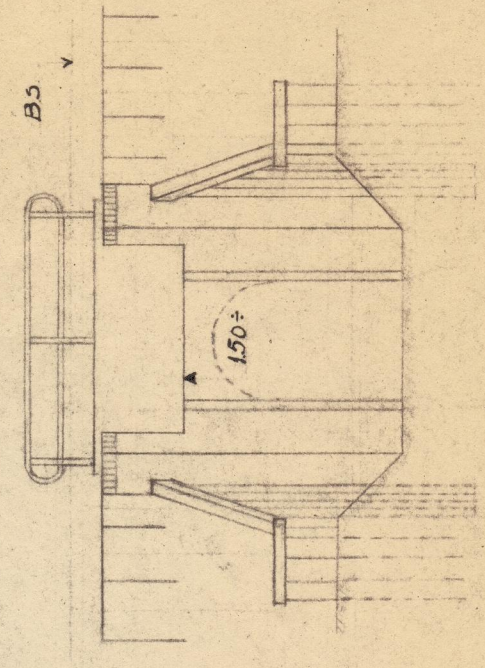


AANZICHT D-D

1275
HULPBRUG L 101/102 EN L 111/112

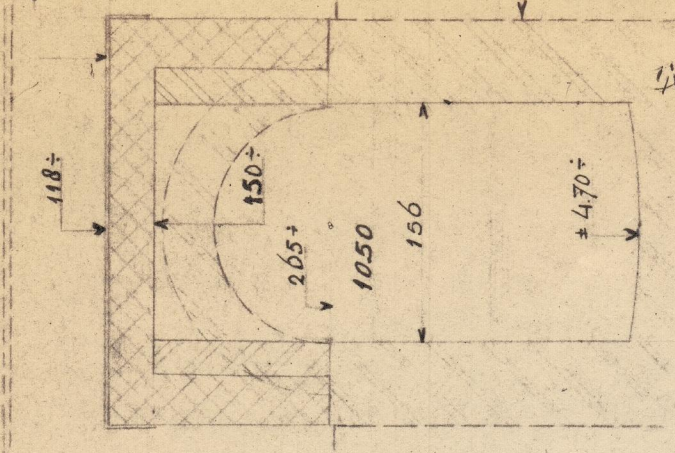

DOORSNEDE D-D

- VERKLARING
- MATEN IN CM.
 - HOOGTEMATEN IN m
 - LOK. B.S.
 - BESTAAND NIEUW
 - GEW. BETON
 - METSELWERK
 - NIEUW
 - BESTAAND
 - SLOPEN

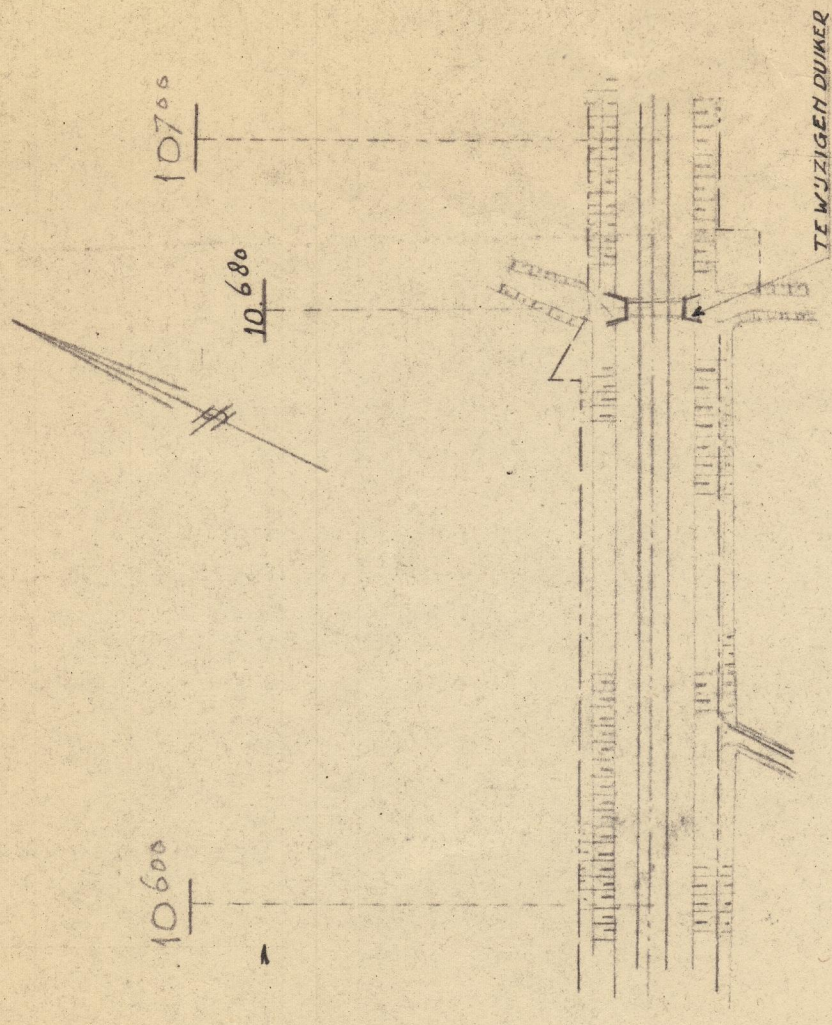

SITUATIE

Km 10.600
R90 - BD

Nº	VAK	OMSCHRIJVING VAN DE WIJZIGING	NAAM	DATUM	GEZ.
N.V. NEDERLANDSCHE SPOORWEGEN					
DIENST VAN DE EXPLOITATIE					
INSPECTIE BREDA					
ROOSENDAAL-BREDA		BESTEK	GET. CREMERS	11-3-59	
WIJZIGEN DUIKER BIJ KM 10.680		Nº	GET. GEC. REV.		
OVERZICHTSTEKENING		AFGEGEVEN V/D UITVOERING	NAAM	DATUM	GEZ.
SCHAAL 1A50 1A100 1A1000		KOKER	LADE		
3A4	CODE: 416/99	Geogr. code	Werk of km.	Object code	Blad
12252		K10680		297	1