

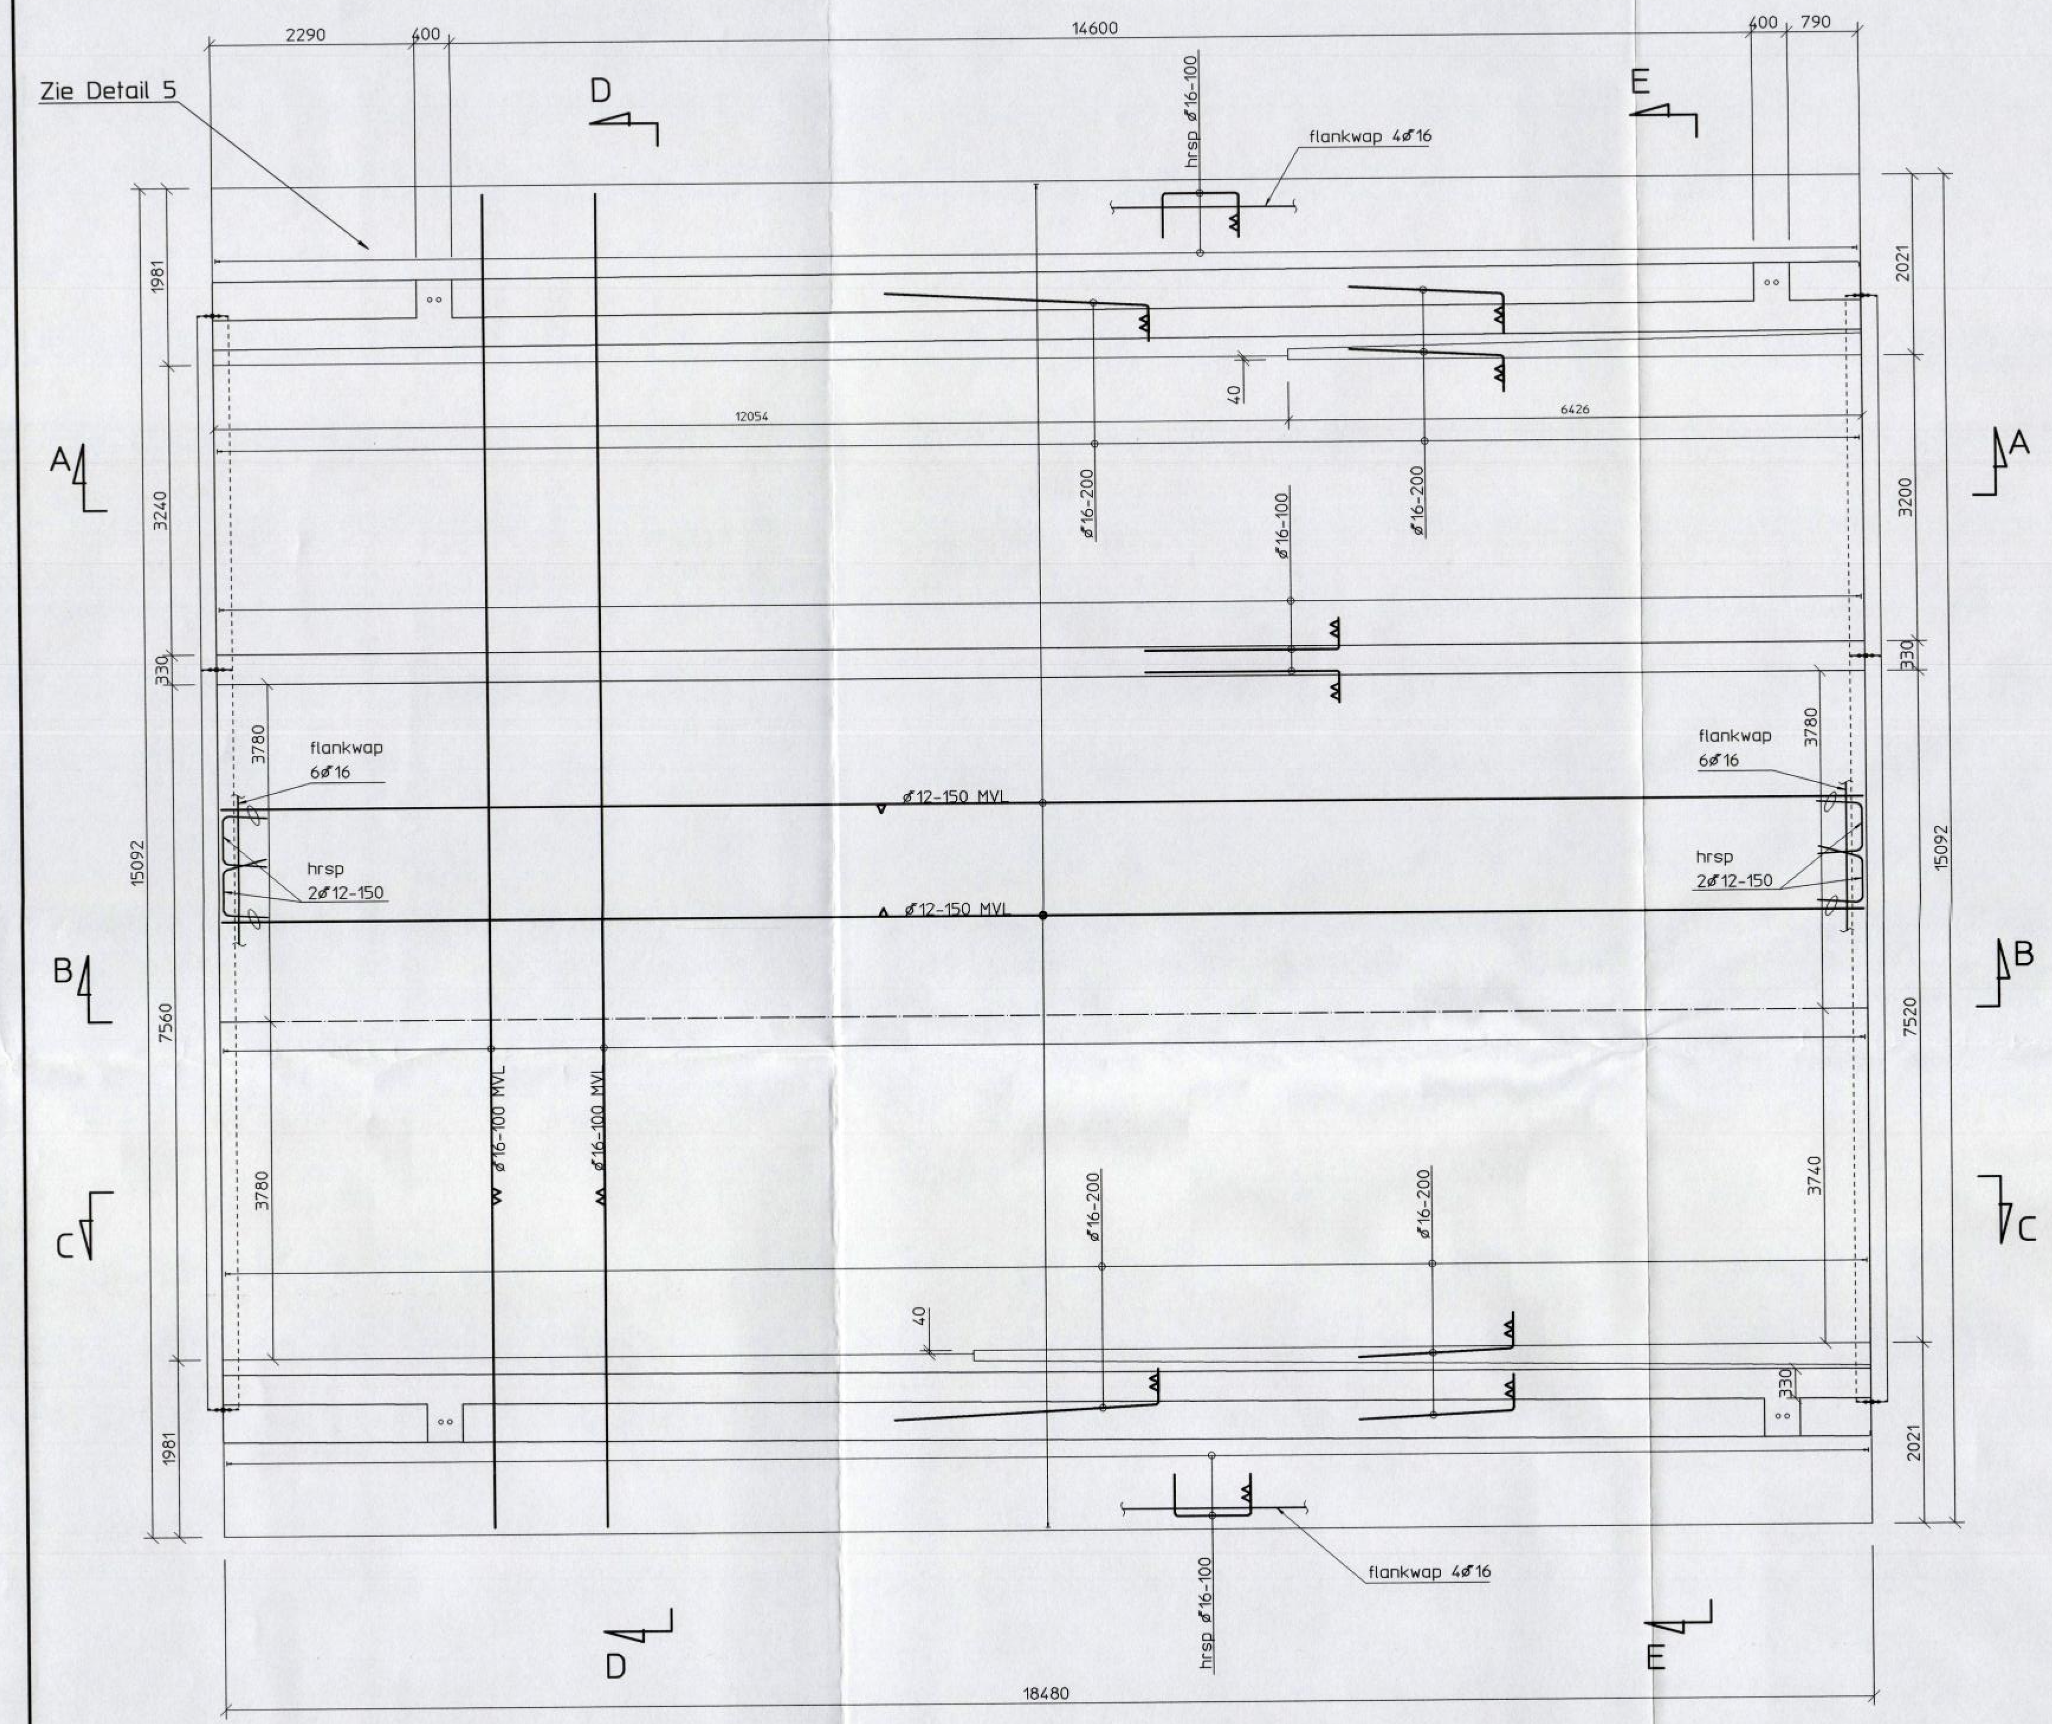



Bovenaanzicht schaal 1:50

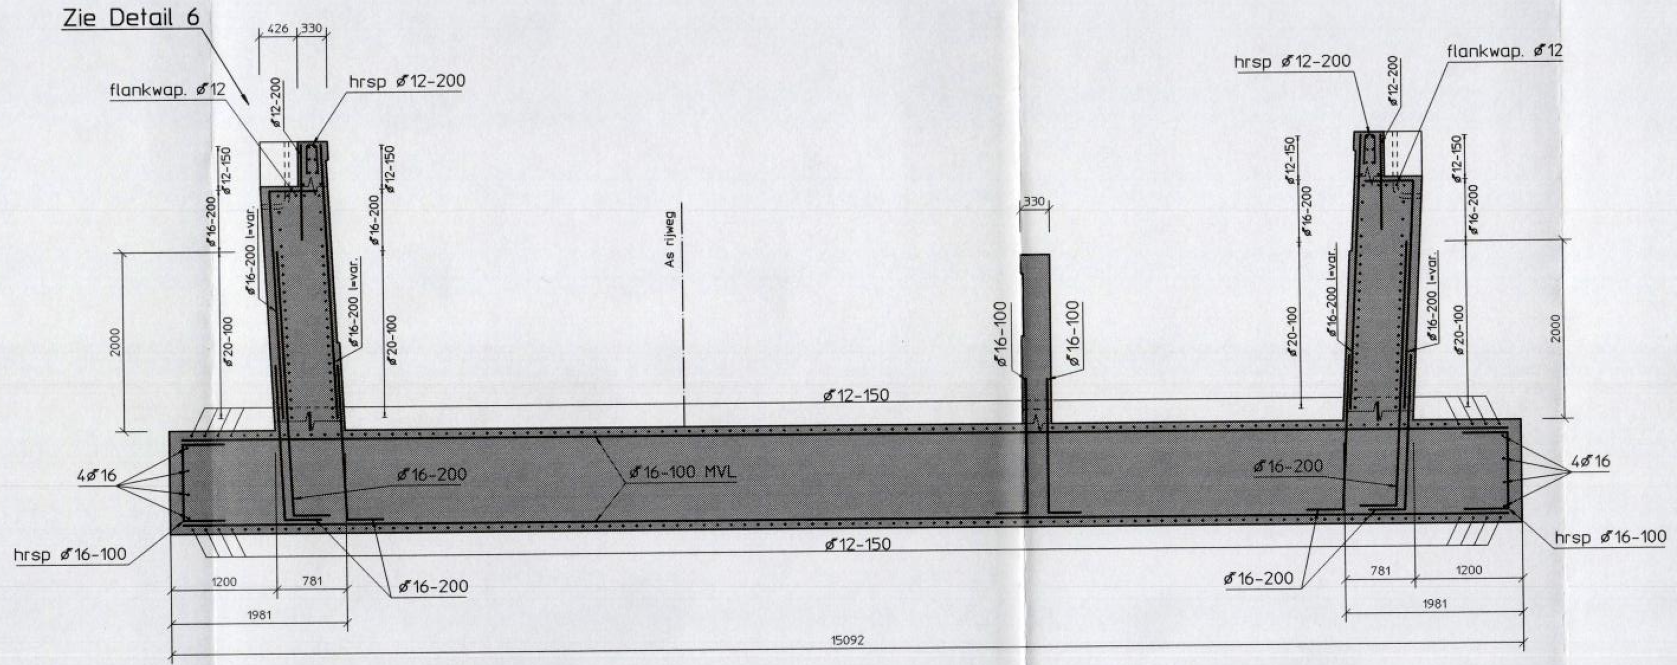

Doorsnede D-D schaal 1:50

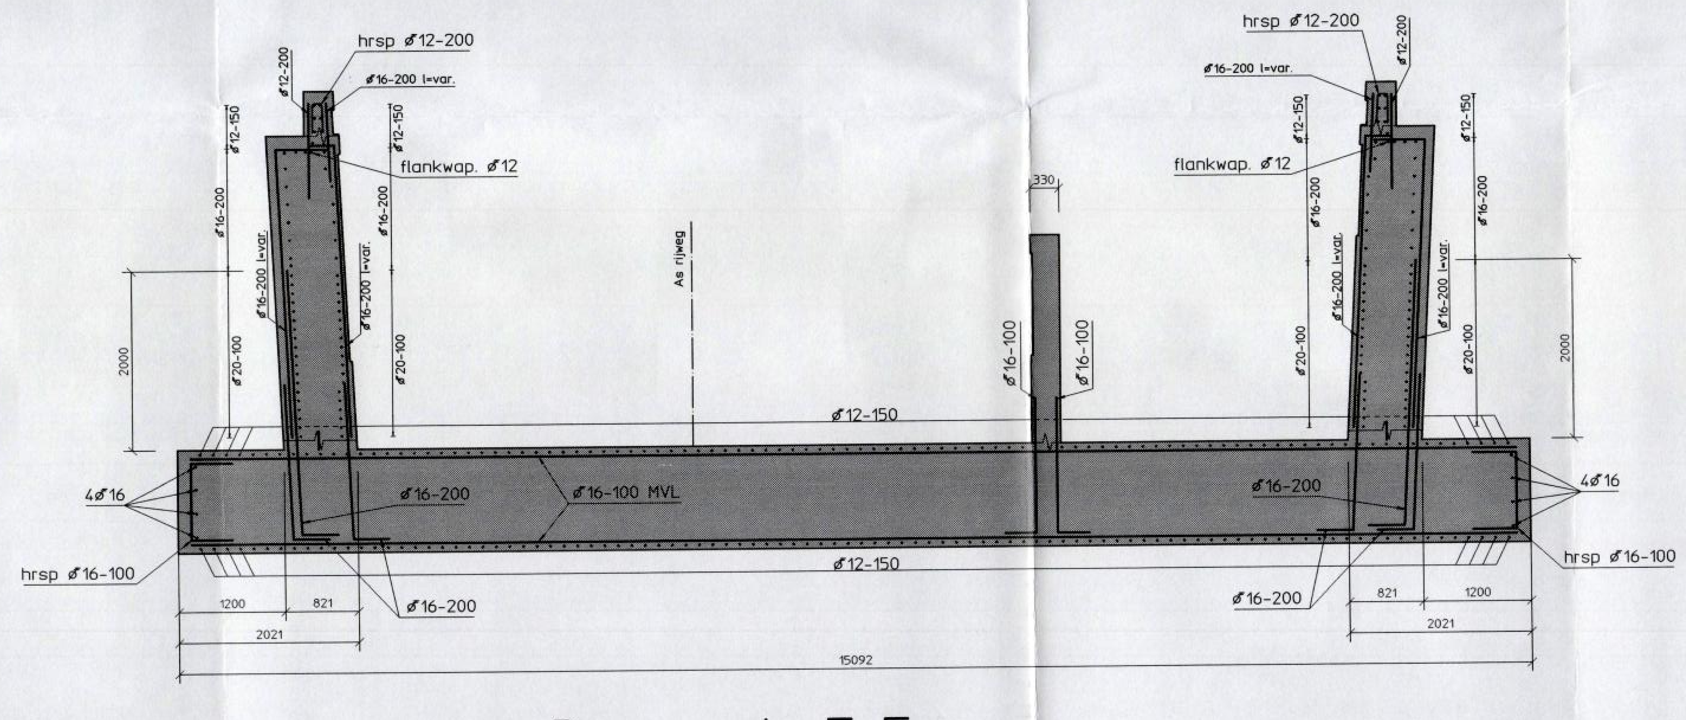


Doorsnede E-E schaal 1:50

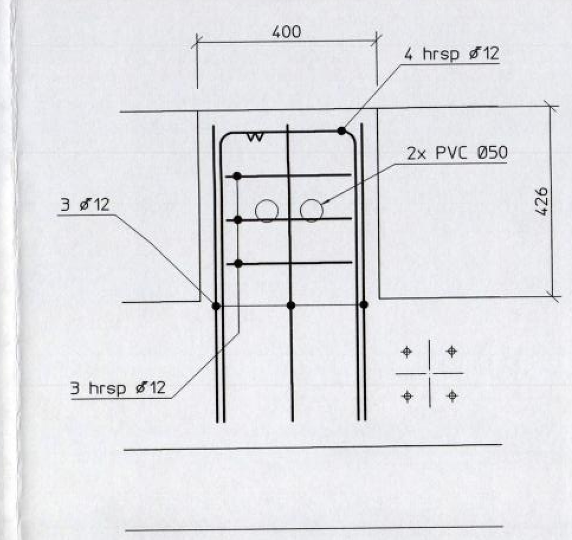


Detail 5 Schaal 1:10

Poer t.b.v. lichtmast

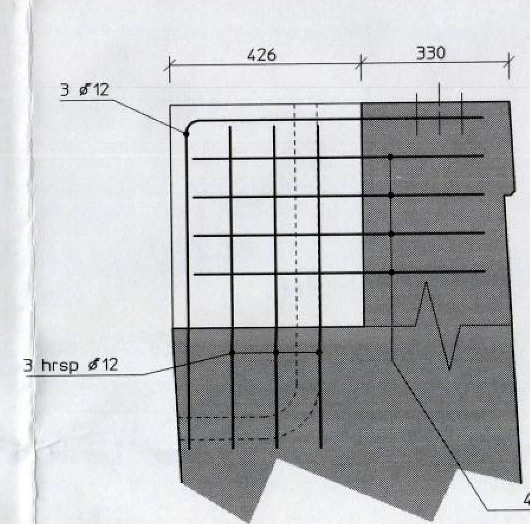


Detail 6 Schaal 1:10


Poer t.b.v. lichtmast

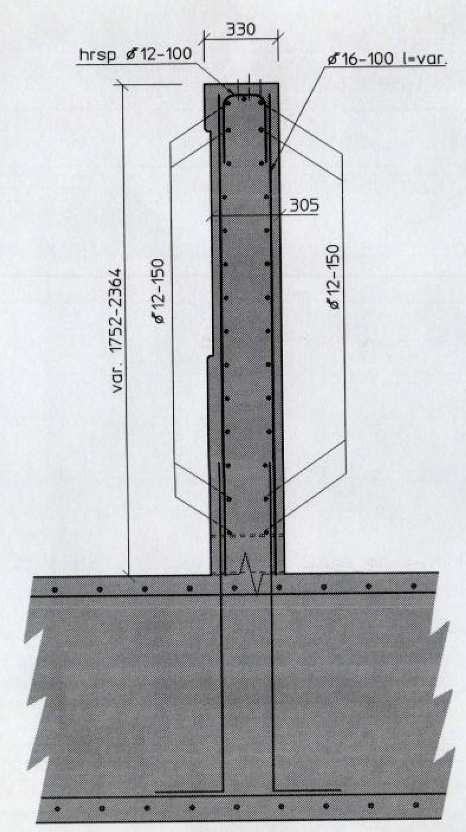


Doorsnede F Schaal 1:20

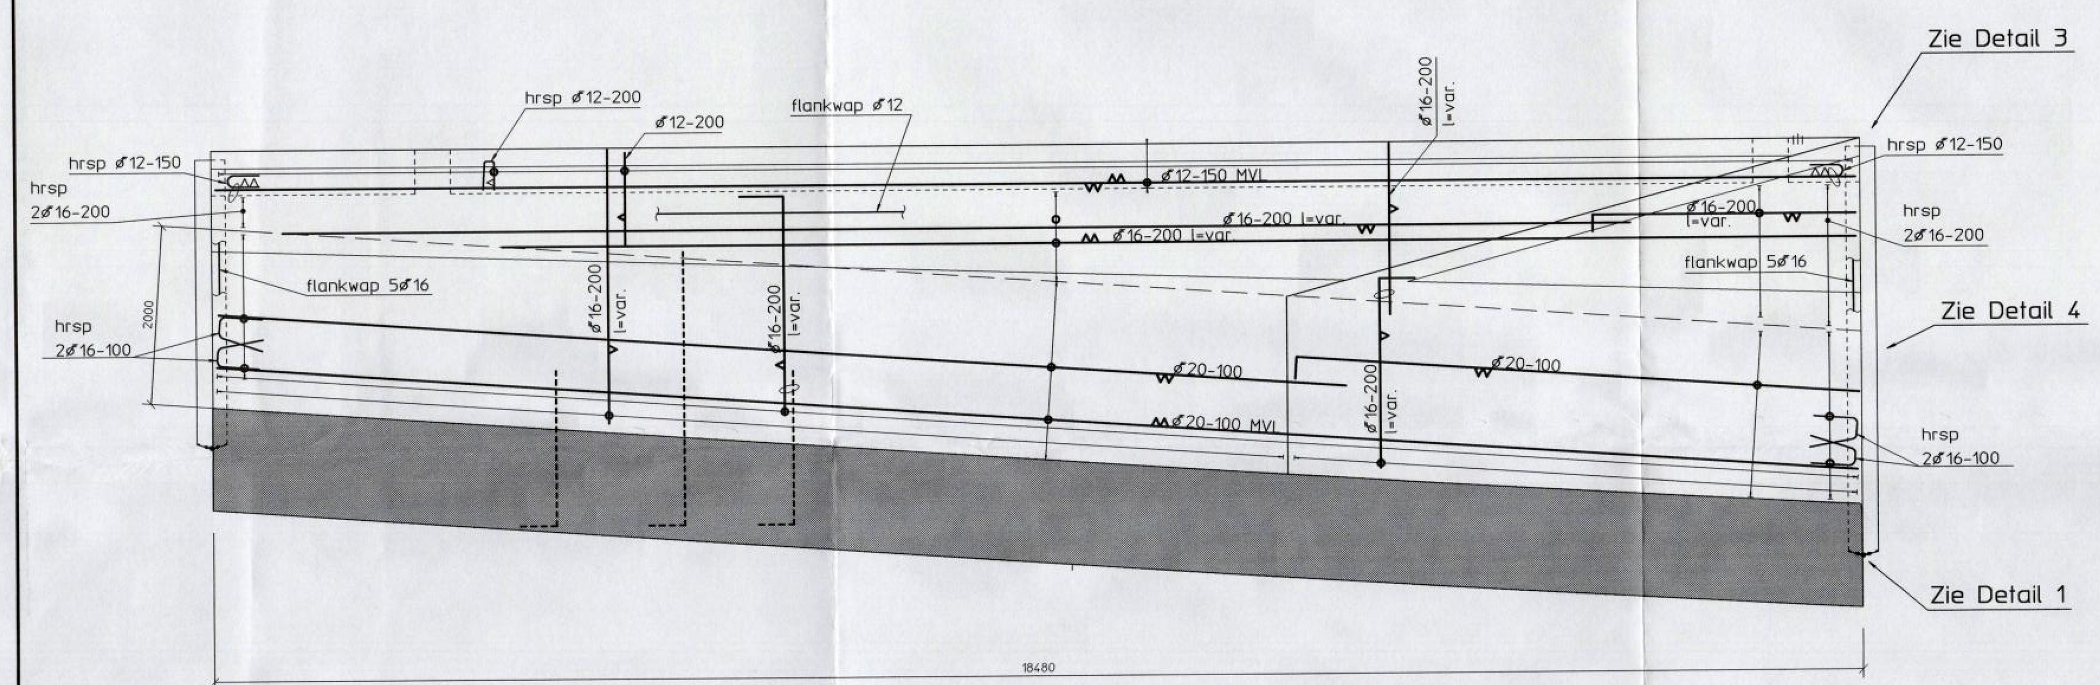


Doorsnede A-A schaal 1:50

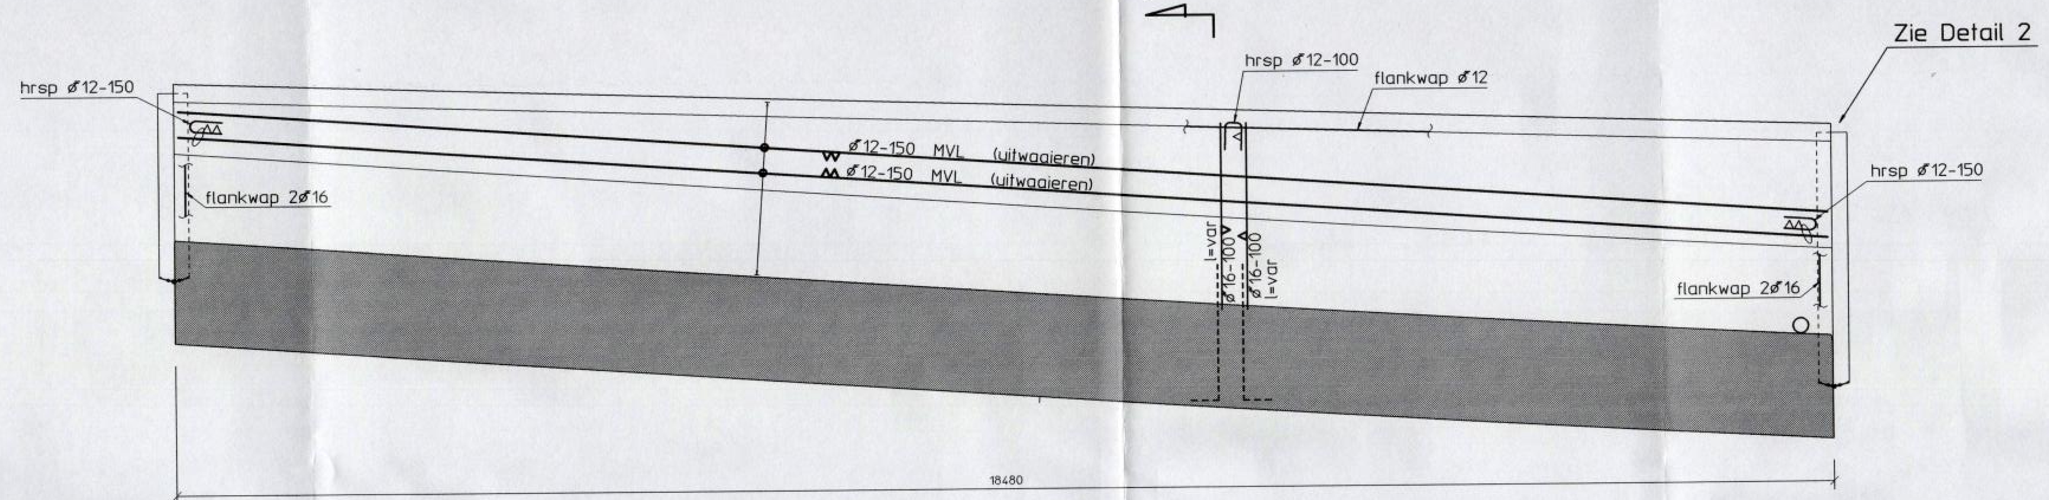


Doorsnede B-B schaal 1:50

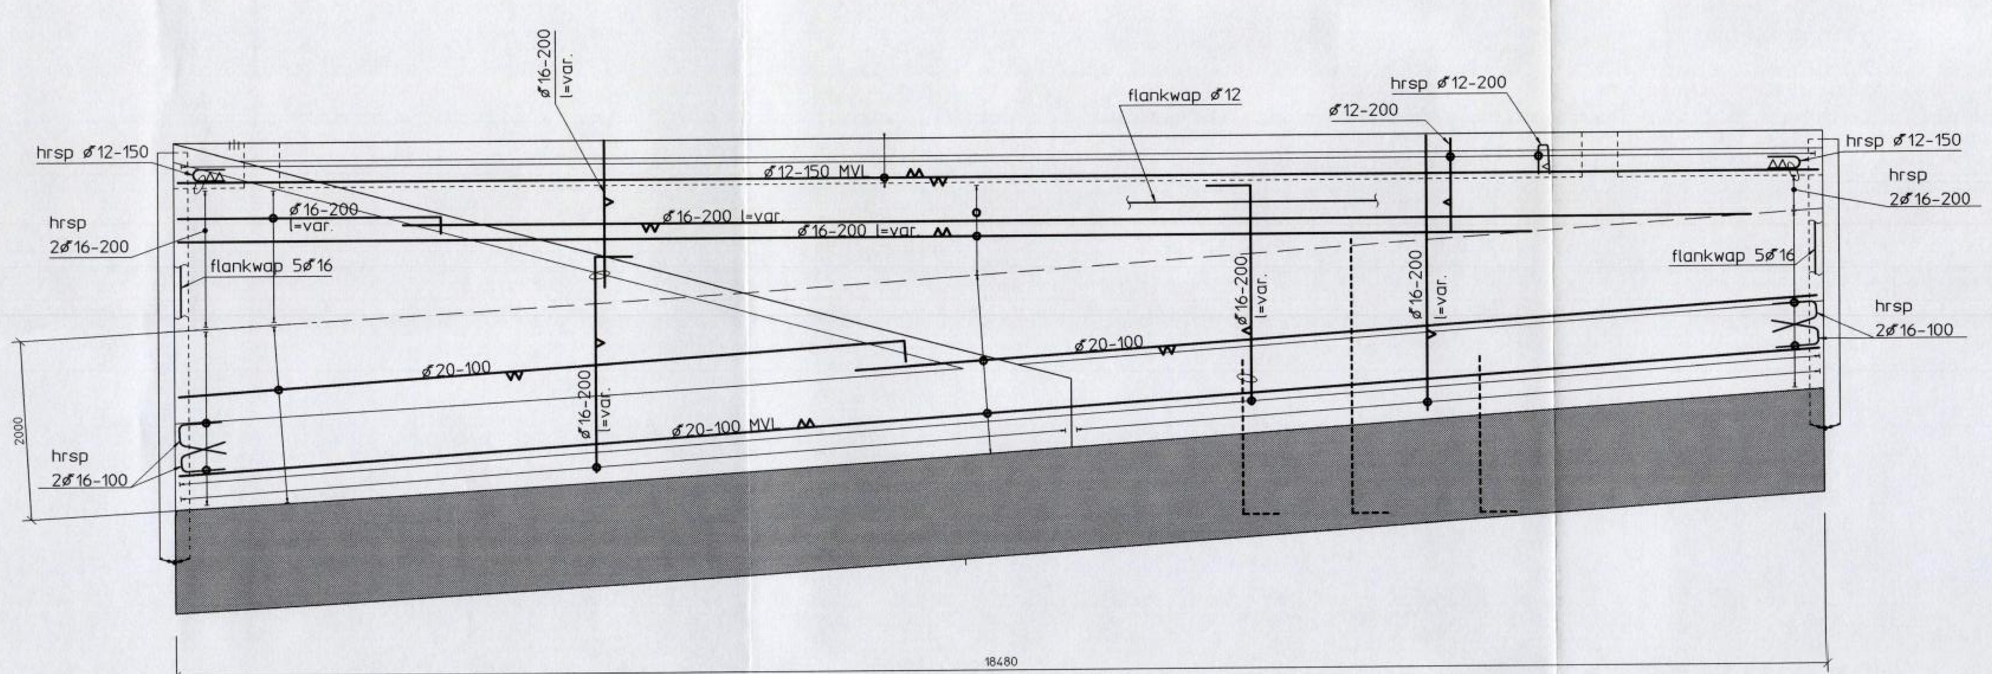


Doorsnede C-C schaal 1:50

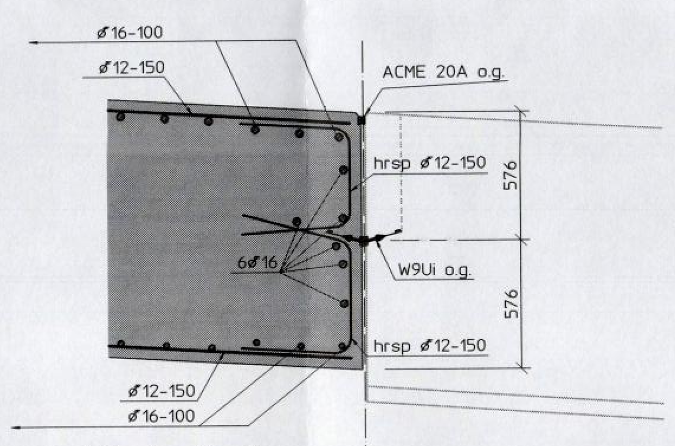


Detail 1 Schaal 1:20

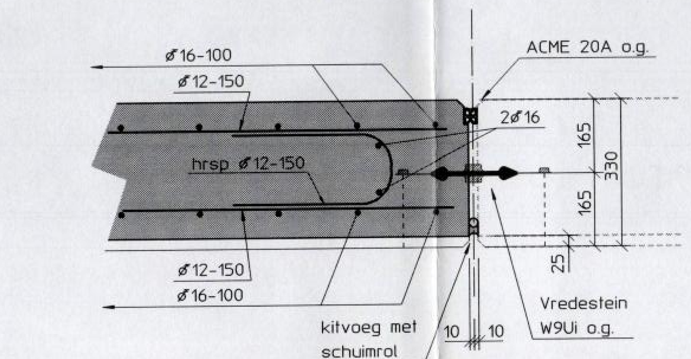


Detail 2 Schaal 1:10

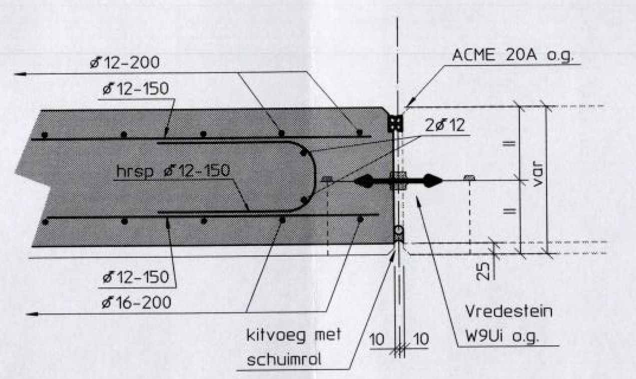

Detail 3 Schaal 1:10

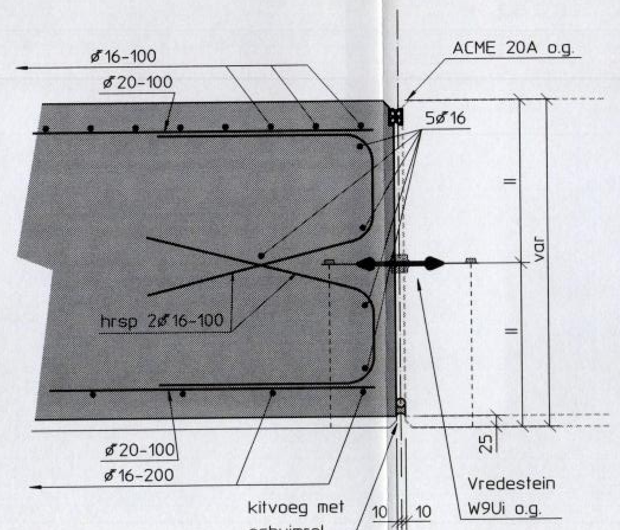

Detail 4 Schaal 1:10

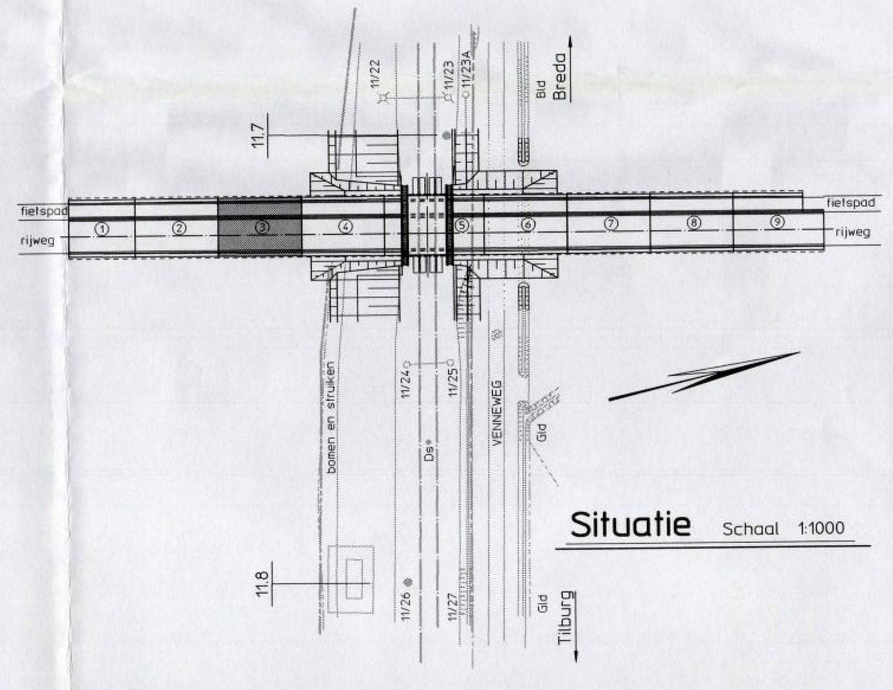

Situatie Schaal 1:1000

Legenda

- maatvoering in mm
- hoogtemaatvoering in m t.o.v. N.A.P.
- voor maatvoering zie tek. 3362706 30 M
- MVL = met verspringende las
- var. = variabel

Status: REVISIE d.d. 17-12-1999 14:10:23

betondekkingstabel

betonstaal : - FeB 500 HWL en/of HK NEN 6008
beton : - sterkteklasse B 35
- milieuklasse 3 (vloer) / 5b (wanden)
- cement CEM III/B LH

constructiedeel	betondekking in mm	
	controleerbaar	oncontroleerbaar
vloer	35	40
wand	35	40
op- en aanstorten	35	40

verankeringslengten	
ø10	*
ø12	270
ø14	*
ø16	420
ø20	570
ø25	760
ø28	*
ø32	1280
ø40	*

	naam	par.	datum	
getekend	T. Brandt /P. de Boeck		17-12-'99	Wapening moot 3
projectleider	C.F. Vink			
projectnr.	3362706	versie	1.0	NS Railinfrabeheer Regio Zuid
besteknr.	V40BK09450			Gilze Rijen
formaat	A0			Onderdoorgang Europalaan
schaal	zie tek.			

420 / 123 / 11.720 / 713 / 3362706 30 W

VA CT PG B2
Postbus 2855
3500 GW Utrecht
Telefoon 030 - 235 89 58
Telefax 030 - 235 72 29

Holland Railconsult

plotinfo: /me10_dwg/ct/lc123/km011.720/pa336270.6/oc714/30_w_revisie boeckp ct_k 20-12-1999 10:57:42