
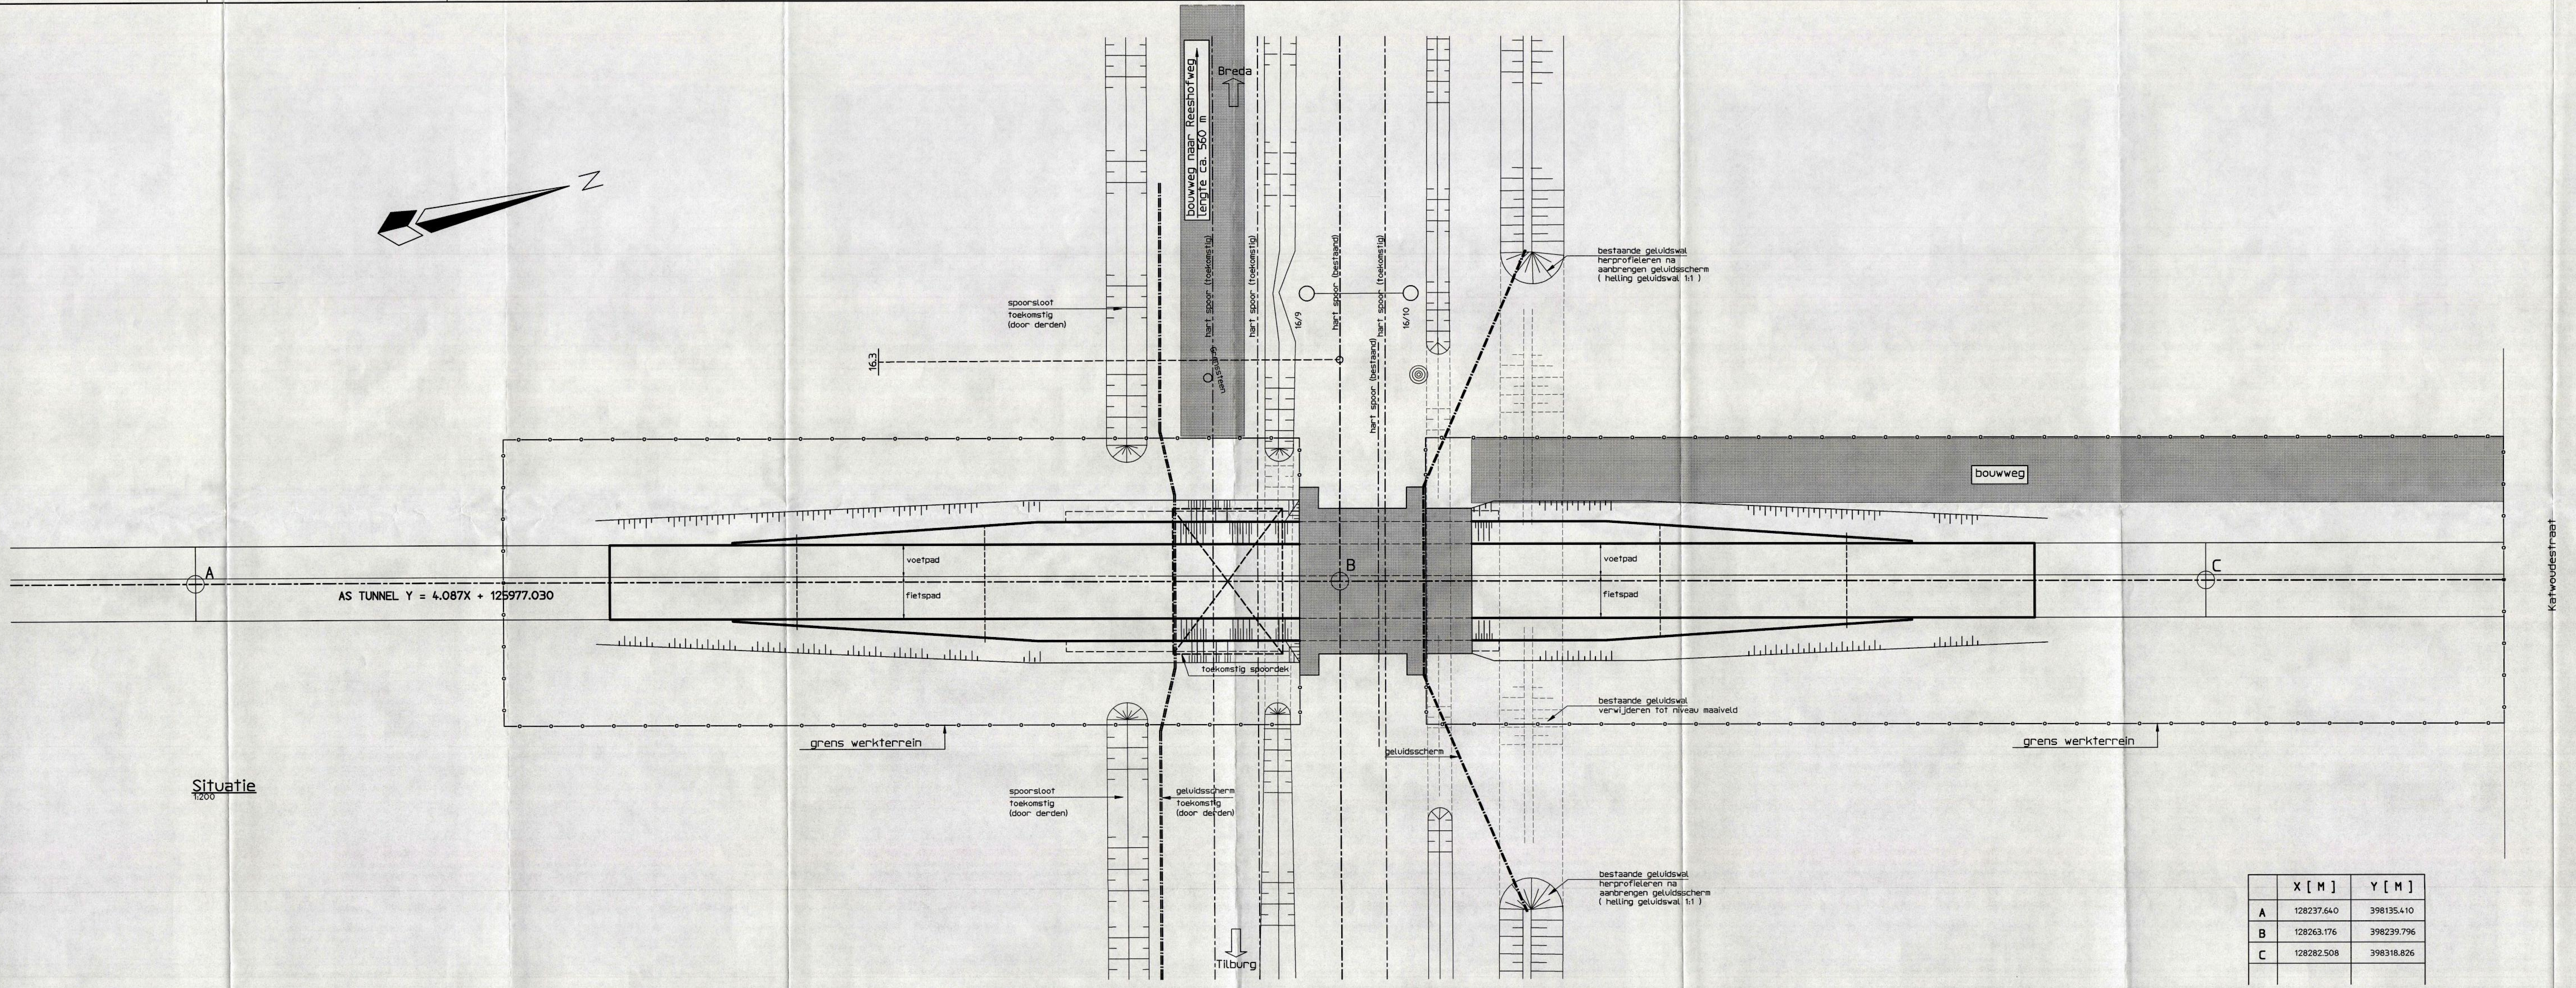


Situatie
1:200

	X [M]	Y [M]
A	128237.640	398135.410
B	128263.176	398239.796
C	128282.508	398318.826


Voor bovenaanzicht en doorsnedes zie blad 301
Voor palenplan zie blad 302
Voor hulpconstructie zie blad 303
Voor details zie blad 304 (Detailboek)

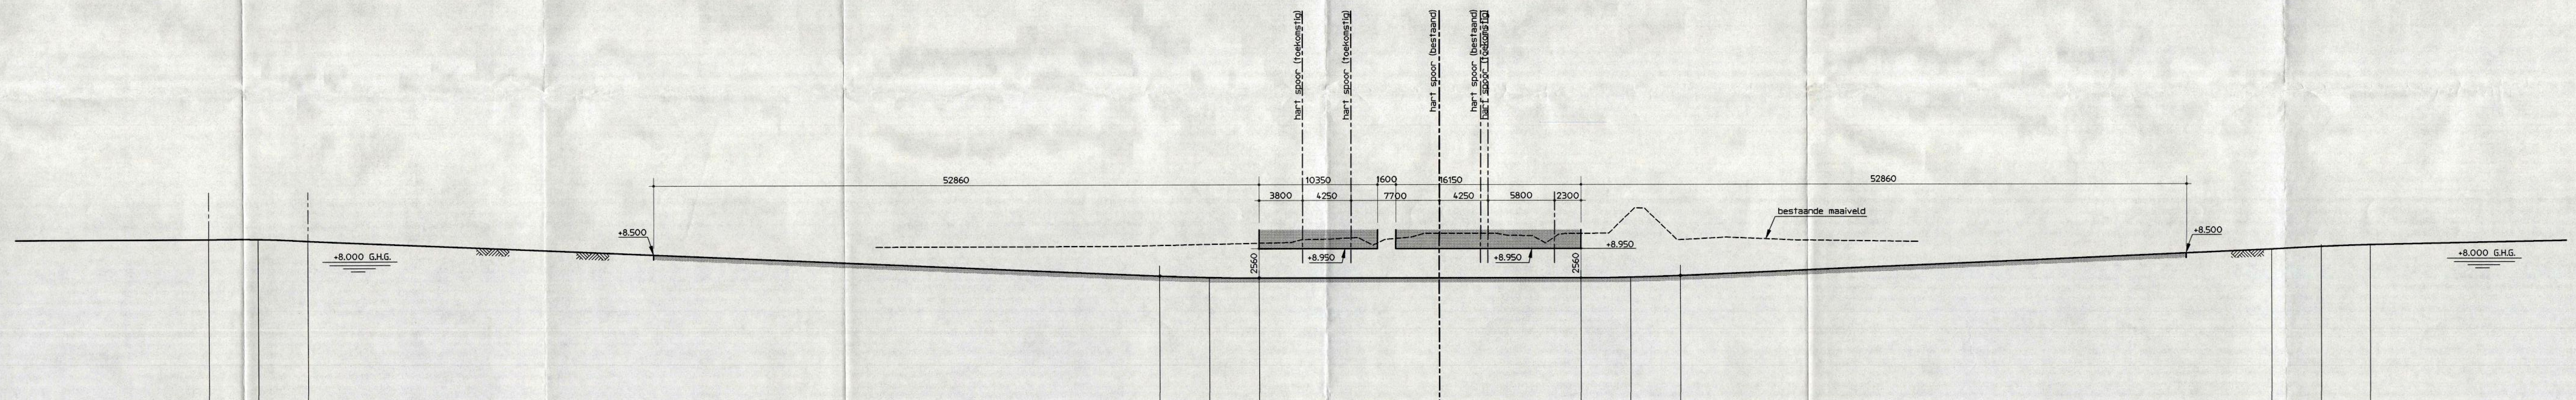

Metrering [m]		-103.12		-20.090		0.000		+16.690		+81.320	
Hoogte as lijn		+10.00		+6.390		+6.390		+6.390		+9.200	
Afstand [mm]			83030		20090		16690		64630		
Helling [%]	0		4.35 (1:23)		0		0		4.35 (1:23)		0

Metrering [m]		-107.46		-98.773		-24.437		-15.750		0.000		+12.350		+21.037		+76.973		+85.660	
Tunnel peil (=b.k. asfalt in tunnel as)		+10.00		+9.811		+6.579		+6.390		+6.390		+6.390		+6.579		+9.011		+9.200	
Afstand [mm]			8687		74336		8687		15750		12350		8687		55936		8687		
Straal [m]	∞		200		∞		200		∞		∞		200		∞		200		

Langsdoorsnede
1:200

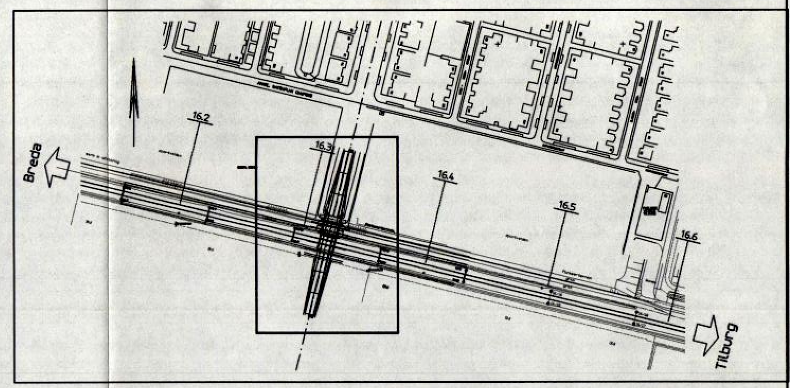

Opmerkingen
- alle maten in mm
- hoogtematen in m t.o.v. N.A.P
- coordinaten t.o.v. Parijs stelsel
- G.H.G. = gemiddelde hoogste grondwater stand

REVISIE TOEGEPAST datum: 28-02-01 paraaf:

ARCADIS BOUW/INFRA

Berkenweg 7
Postbus 220, 3800 AE Amersfoort
Telefoon 033 460 44 00
Telefax 033 460 44 06

Project
Tilburg
o.d.g. Campenhoef-Witbrant

Uitg.	Datum	Getekend	Opmerkingen
R	18-01-01	v.Oostende	revisie
A	07-12-98	Belay A.	

Onderdeel
Bestek
Tunnel alignement

Status : In bewerking / Conceptversie / Goedgekeurd / Vrijgegeven

Goedgekeurd : F.J. Hovinga
Vrijgegeven : J.W.M. Hagen
Schaal : 1:200
Formaat : 2.5xA1

Codering derden :
Tekeningnummer:
Tb 42/3/1 300

0 1 2 3 4 5 6 7 8 9 10

ARCADIS Bouw/Infra BV is ontstaan uit Articon, Grabowsky&Poort, Heidemij Advies Bouw, Bureau Jongen, Starke Diekstra en Van der Mast