
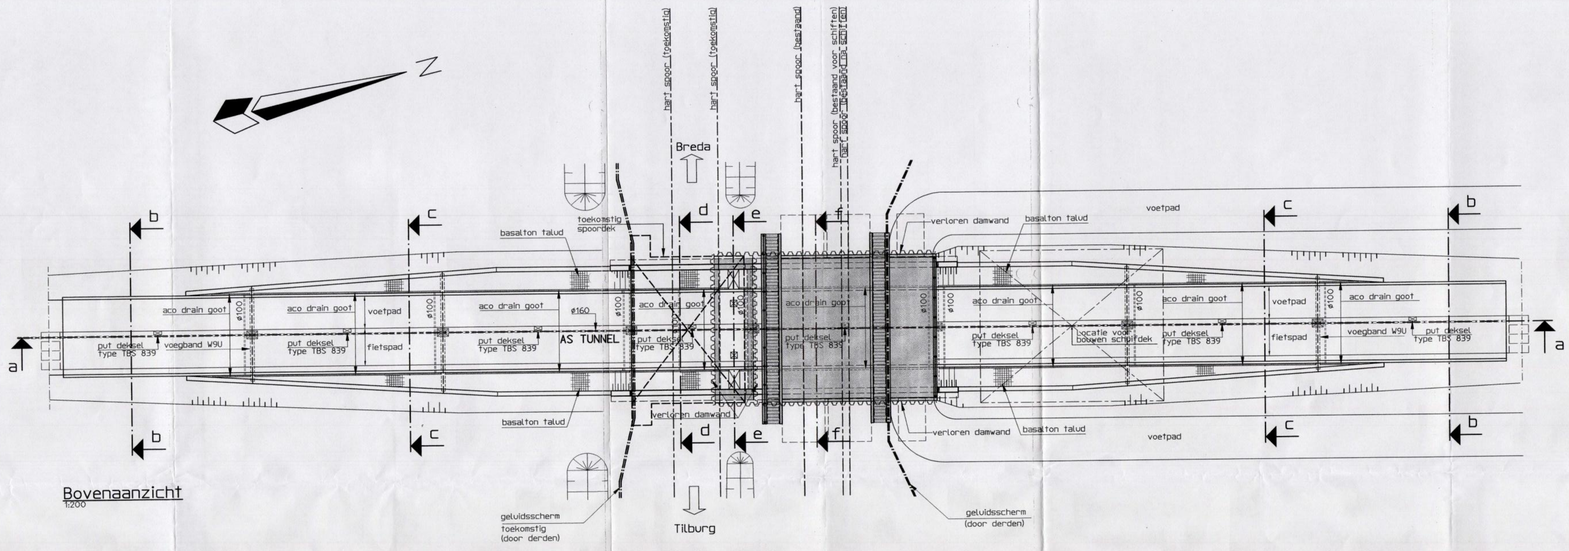


Bovenaanzicht
1:200


Doorsnede a - a
1:200

Palen = Ø 290x290
PPN op NAP = +0.50m
Aantal = 44
Gem. lengte = 6.5m


G.H.G = Gemiddelde hoogste grondwater stand

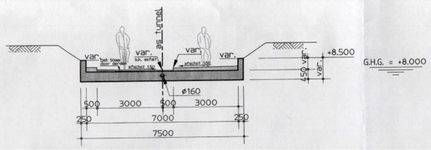


Dsn b - b
1:100

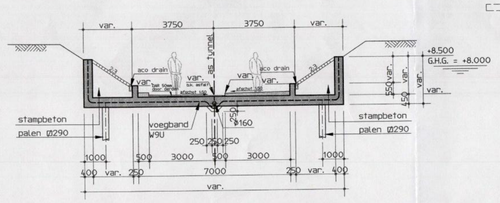


Dsn c - c
1:100

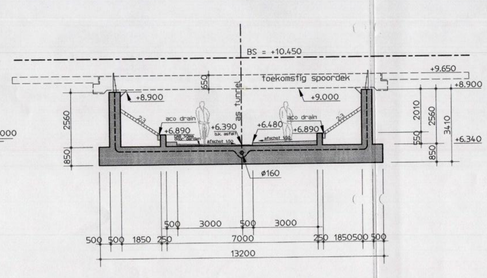


Dsn d - d
1:100

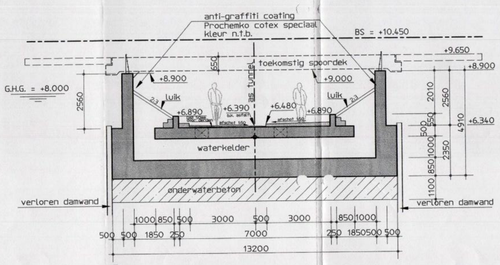

Dsn e - e
1:100

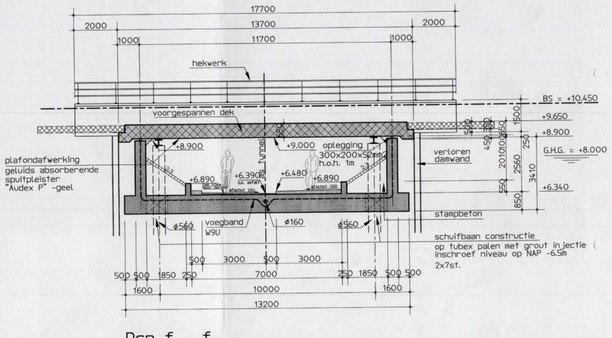

Dsn f - f
1:100

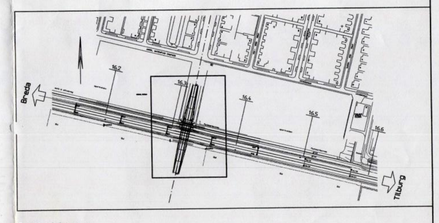

Opmerkingen
- alle maten in mm
- hoogtematen in m t.o.v. N.A.P
- coordinaten t.o.v. Parijs stelsel

ARCADIS BOUW/INFRA

Project
Tilburg
o.d.g. Campenhoef-Witbrant

Uitg.	Datum	Getekend	Opmerkingen
A	09-04-98	Belay A.	

Onderdeel
Definitief ontwerp
Bovenaanzicht en doorsnedes

Status :
- in bewerking
- Concepversie
- voorlopig ontwerp
- definitief

Goedgekeurd : Charles v.d. Sanden
Vrijgegeven : J.M.H. Hagen
Schaal : 1:200, 1:100
Formaat : A0

Codering derden :
Tekeningnummer : Tb 42/3/1 IB 201

Berkenweg 7
Postbus 220, 3800 AE Amersfoort
Telefoon 033 460 44 00
Telefax 033 460 44 06
BV Articon